



kezlo group

PO Box 1086 844.495.3956
Brookhaven, PA 19015 www.kezlo.com

THE INFORMATION CONTAINED HEREIN MAY NOT
BE USED OR REPRODUCED WITHOUT THE
WRITTEN PERMISSION OF KEZLO GROUP, LLC.

SEAL

CONSULTANTS:

ISSUE	DATE	NUMBER

CLIENT:

MARY-ANNE SCHOEB
RICHARD SCHOEB

DATE: 02.28.2025

KEZLO GROUP PROJECT NUMBER: 24-083

PROJECT TITLE:


**STAGHILL
COTTAGE -
ADDITION**

SHEET TITLE:

**FIRST FLOOR &
ROOF FRAMING
PLAN, NOTES &
DETAILS**



SHEET NUMBER:

A6

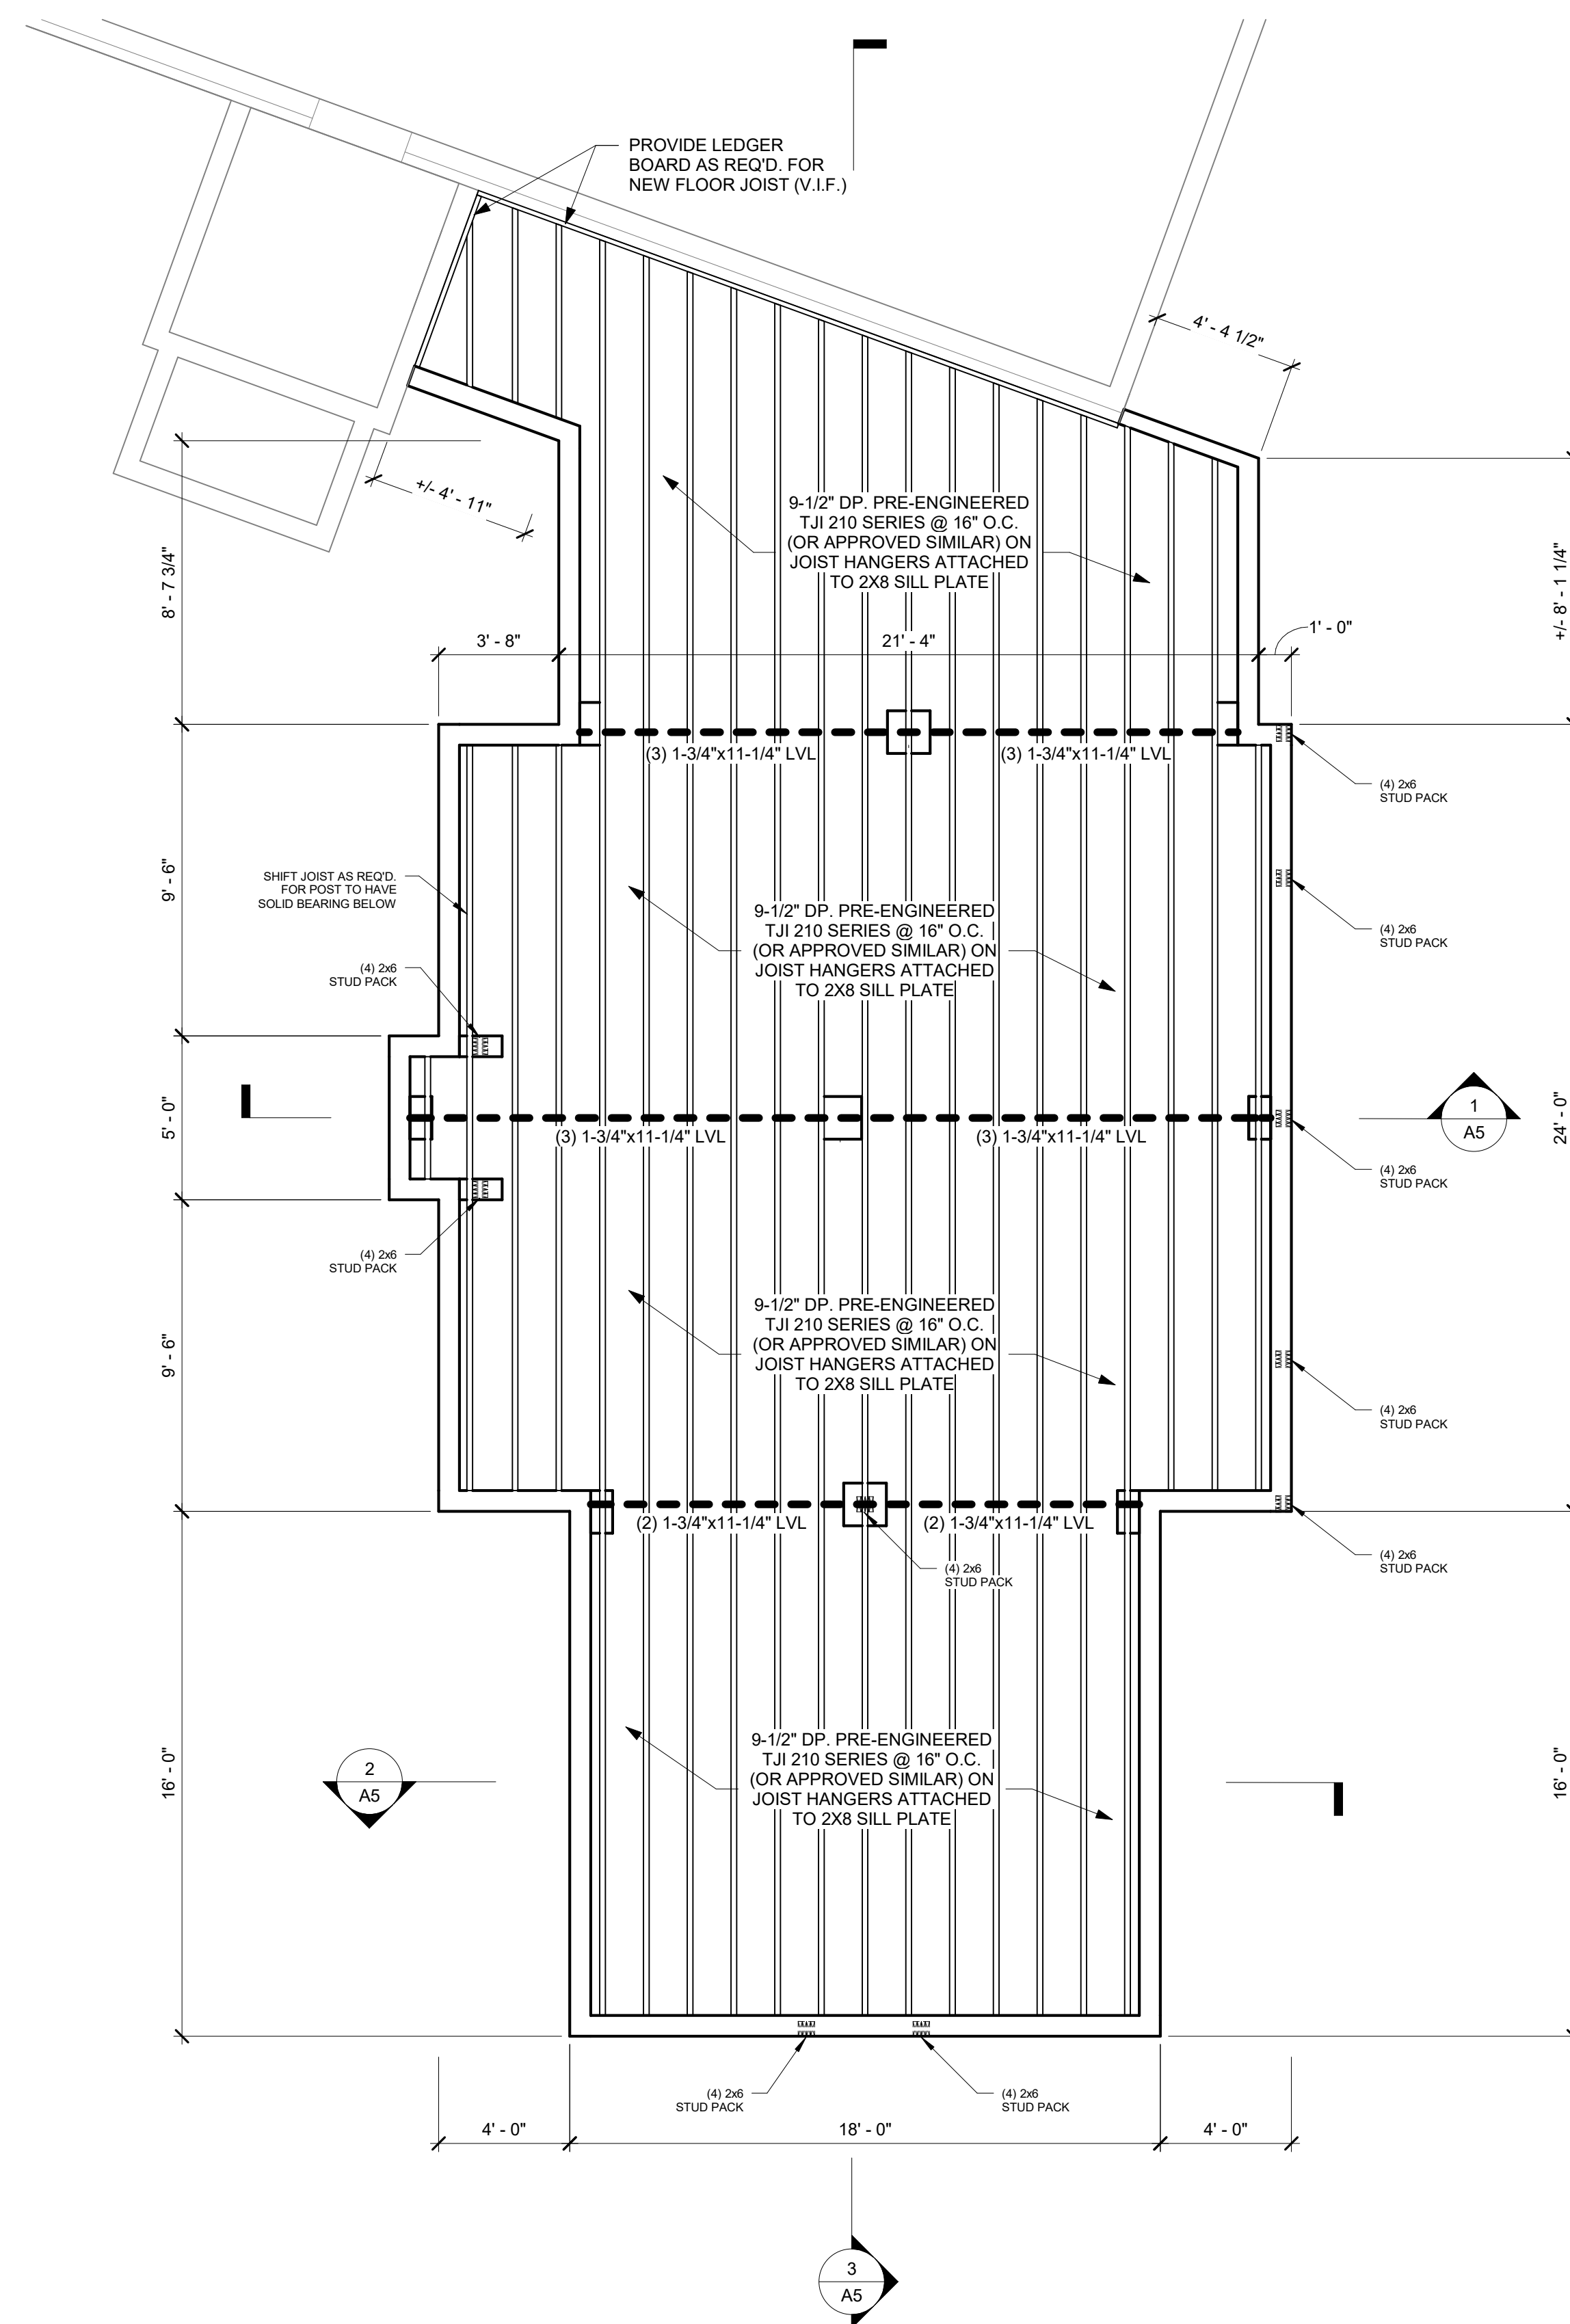

*NOTE: ONLY CRITICAL BEARING POST HAVE
BEEN SHOWN. TYPICAL FRAMING BEST
PRACTICES SHALL APPLY TO ALL WINDOW AND
DOOR HEADERS NOT LABELED

1 ADDITION - FIRST FLOOR FRAMING PLAN
SCALE: 1/4" = 1'-0"

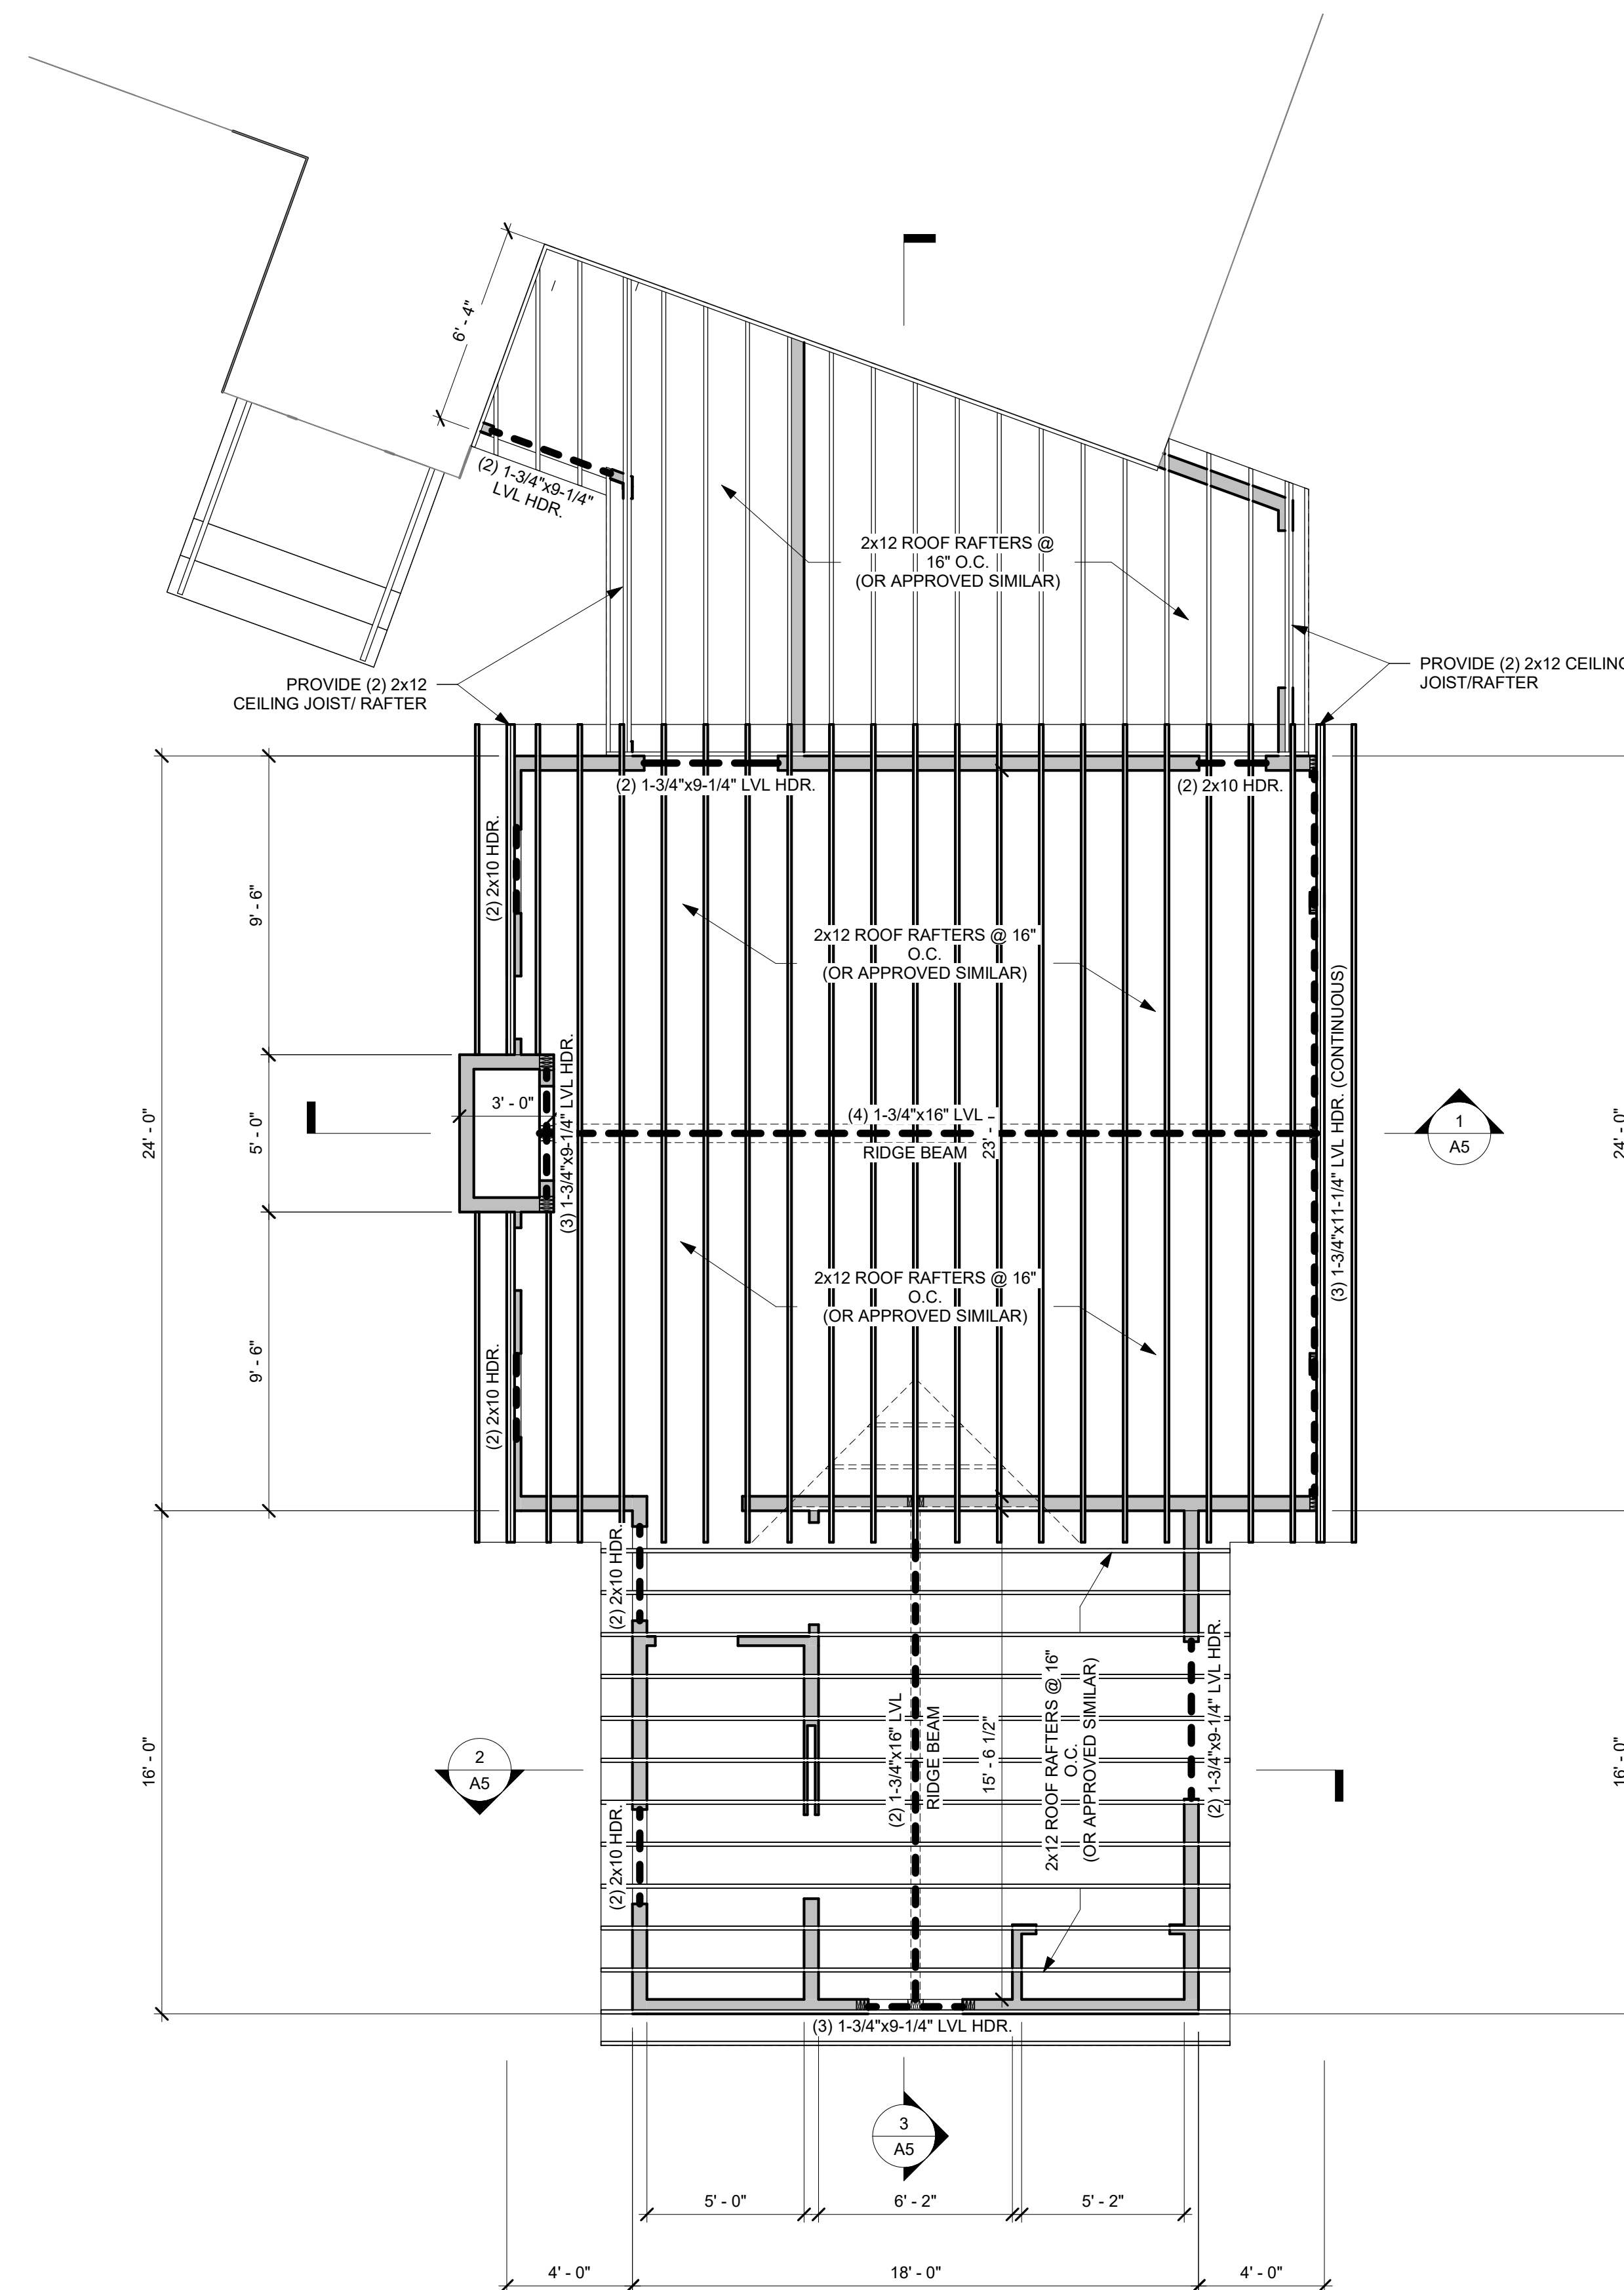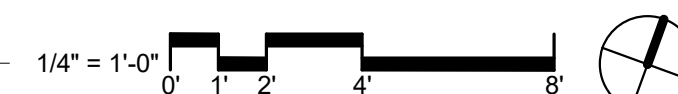

*NOTE: ONLY CRITICAL BEARING POST HAVE
BEEN SHOWN. TYPICAL FRAMING BEST
PRACTICES SHALL APPLY TO ALL WINDOW AND
DOOR HEADERS NOT LABELED

2 ADDITION - ROOF FRAMING PLAN
SCALE: 1/4" = 1'-0"

