


Drawings and Specifications as Instruments of service are and shall remain the property of the Architect. They are not to be used on extensions of the project or other projects, except by agreement in writing and appropriate compensation to the Architect. The General Contractor is responsible for confirming and correlating dimensions at the job site. The Architect will not be responsible for construction means, methods, techniques, sequences, or procedures, or for safety precautions and programs in connection with the project.

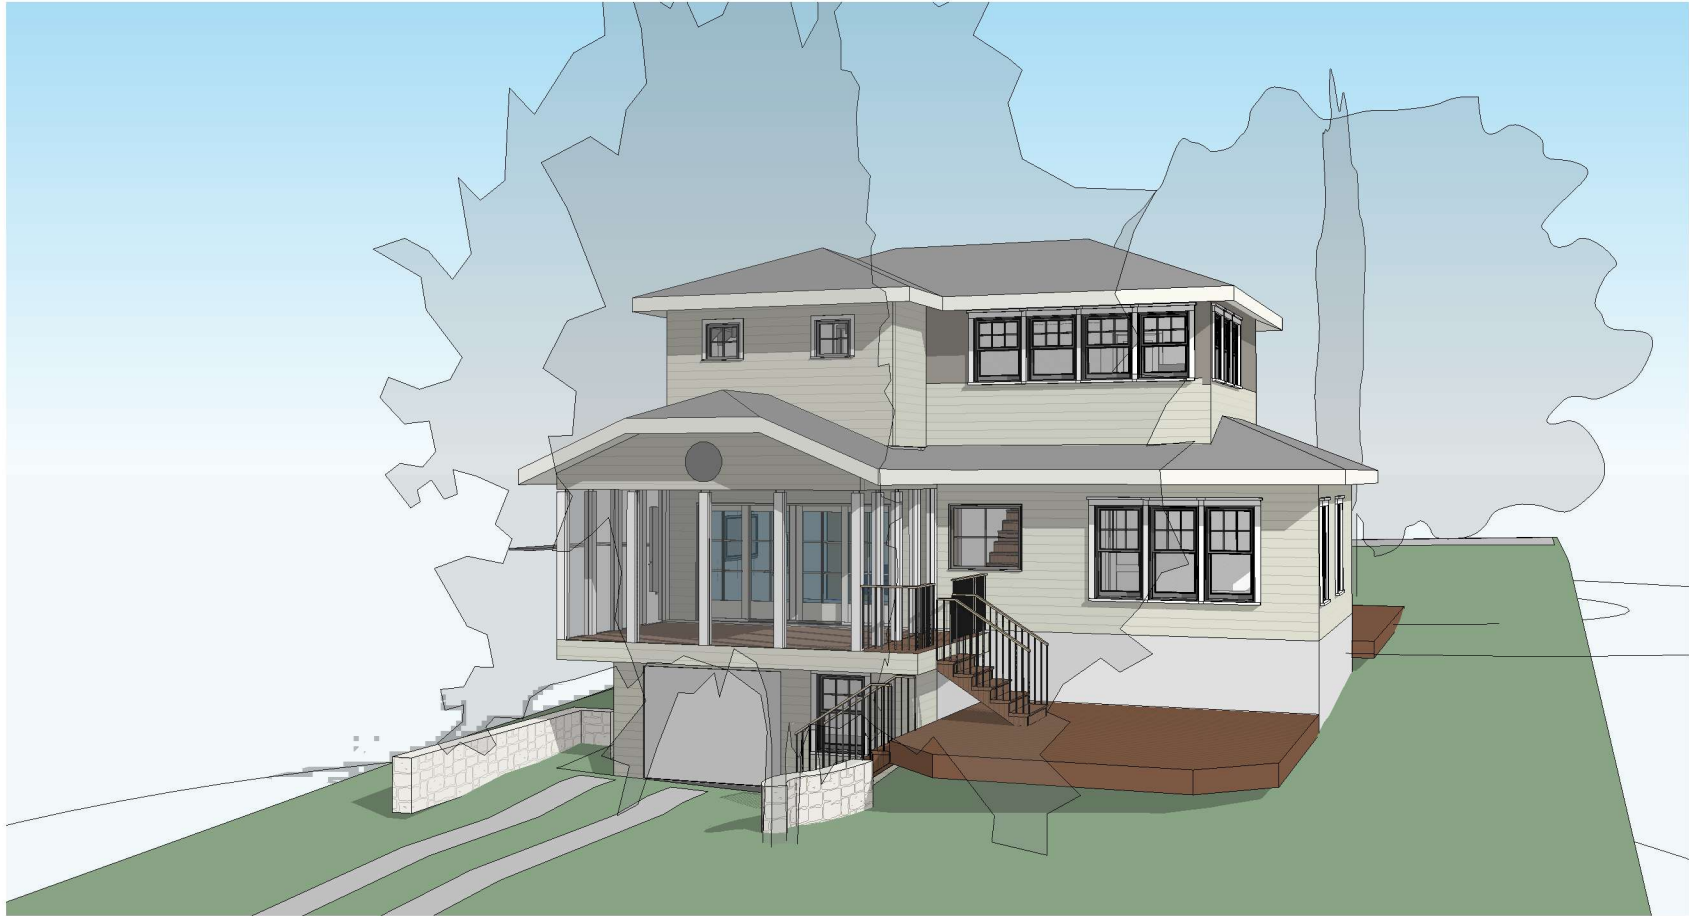

PROJECT INFORMATION

PROJECT DESCRIPTION


REMODEL AND ADDITION TO A SPLIT-LEVEL RESIDENCE IN THE CITY OF AUSTIN

LEGAL DESCRIPTION

LOT 5, BLOCK 4 OF TRAVIS HEIGHTS, A SUBDIVISION IN AUSTIN, TEXAS, ACCORDING TO THE MAP OR PLAT THEREOF RECORDED IN VOLUME 3 PAGE 15 OF THE PLAT RECORD OF TRAVIS COUNTY, TEXAS. (TCAD PARCEL #282923)

ZONING

SF-3-NP - SINGLE-FAMILY RESIDENTIAL
RESIDENTIAL DESIGN STANDARDS (MCMANSION)
SOUTH RIVER CITY NEIGHBORHOOD PLANNING AREA

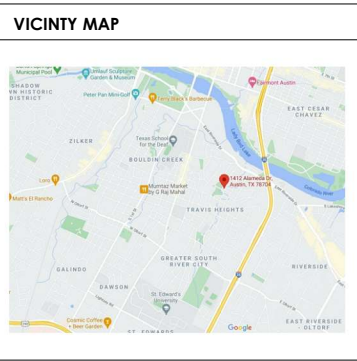

GENERAL PROJECT NOTES

PERFORM ALL WORK IN ACCORDANCE WITH THE CITY OF AUSTIN CODES, REGULATIONS & ORDINANCES

DO NOT SCALE DRAWING, CONTACT ARCHITECT UPON DISCOVERY OF MISSING INFORMATION OR CONFLICTS IN DRAWINGS

STRUCTURAL ENGINEERING FOR ALL PARTS OF THIS PROJECT TO BE DESIGNED BY OTHERS

MECH, ELEC, PLUMB & FIRE ENGINEERING TO BE PROVIDED BY OTHERS, MAY REQUIRE COORDINATION WITH ARCHITECT

VERIFY EXISTING CONDITIONS AND DIMENSIONS PRIOR TO CONSTRUCTION START

FIRE PROTECTION

THIS PROJECT DOES NOT EXCEED 3,600 SF AND THEREFORE IS NOT REQUIRED TO BE REVIEWED BY THE FIRE DEPARTMENT

CONTACTS

CLIENT

BEN & ANNA HALLMARK

ARCHITECT

CVMA
CONTACT: CAROLYN VAN METER
E-MAIL: CAROLYN@CVMARCHITECTURE.COM
PHONE: 512.740.8595

CONTRACTOR:

-NAME:
CONTACT:
E-MAIL:
PHONE:

STRUCTURAL ENGINEER:

STEINMAN LUEVANO STRUCTURES
CONTACT: DREW CAVE
E-MAIL: DREW@SLSTRUCTURES.COM
PHONE: 512.891.6766

INTERIOR DESIGNER:

-NAME:
CONTACT:
E-MAIL:
PHONE:

SYMBOLS LEGEND

1 View Name
1/8" = 1'-0"

DRAWING TITLE
DRAWING NUMBER

Room name
??? CLG.
??? FLOOR

ROOM NAME
- CEILING HEIGHT
- FLOOR MATERIAL

ELEVATION MARKER

BUILDING SECTION MARKER

WALL SECT./DETAIL MARKER

LEVEL MARKER

KEY NOTE

DOOR NUMBER

WINDOW KEY

CENTERLINE

REVISION NUMBER

FLOOR DROP

NORTH ARROW

DRAWING INDEX

ARCHITECTURAL

A0.0 COVER SHEET
A1.1 SITE PLAN AND AREA CALCULATIONS
A1.2 DEMOLITION PLAN
A1.3 DEMOLITION ELEVATIONS
A2.1 LEVEL 1 PLAN
A2.2 LEVEL 2 PLAN
A2.3 ROOF PLAN
A4.1 EXTERIOR ELEVATIONS
A4.2 EXTERIOR ELEVATIONS

STRUCTURAL

S1 FOUNDATION PLAN
S2 FIRST FLOOR CEILING FRAMING AND SECOND FLOOR FRAMING PLAN
S3 ROOF FRAMING PLAN AND SECOND FLOOR CEILING PLAN
S4 DETAILS
S5 BRACE WALL PLANS
S6 NOTES

CVMA

Carolyn Van Meter Architecture

carolyn@cvmarchitecture.com
c. 512.740.8595

REGISTERED ARCHITECT
CAROLYN VAN METER
24997
STATE OF TEXAS

10.13.21

HALLMARK RESIDENCE

1412 ALAMEDA DR.
AUSTIN, TEXAS 78704

ISSUE DATES:		
PERMIT SET	7.20.21	
REV. PERMIT SET	10.13.21	

A0.0
COVER SHEET