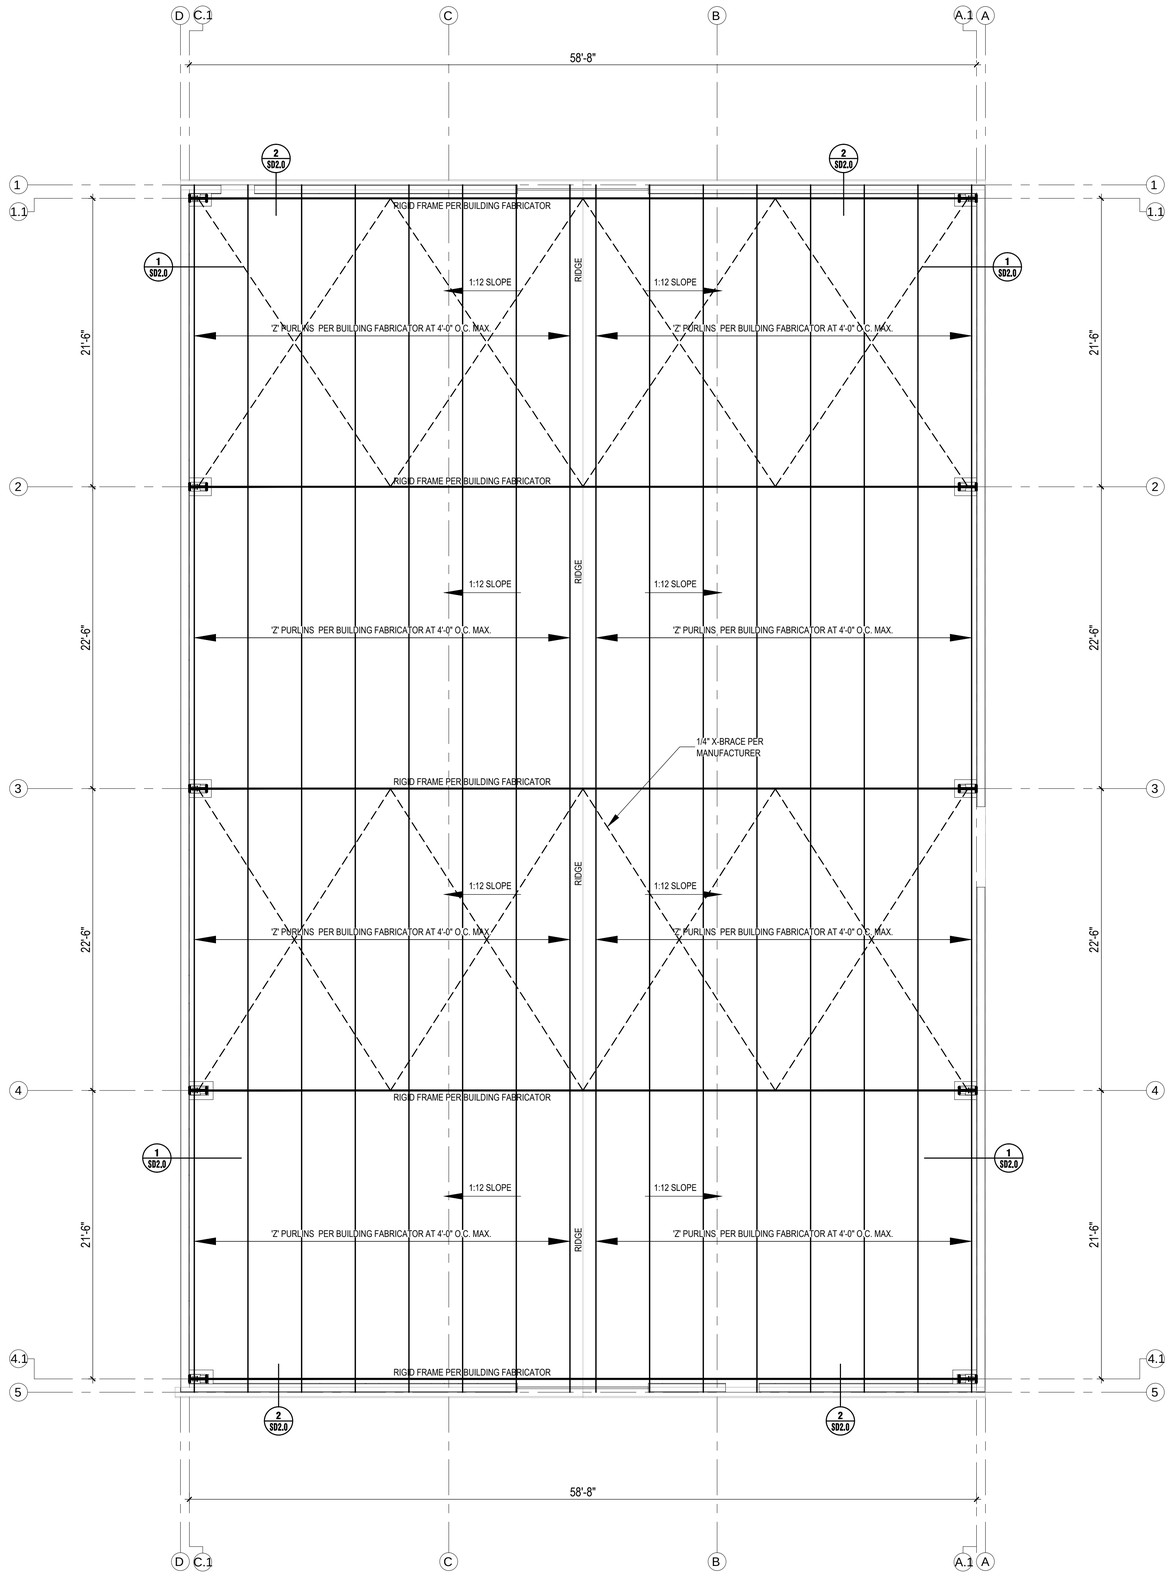


## METAL BUILDING NOTES:

1. THE DESIGN AND CONSTRUCTION OF THE METAL BUILDING IS THE RESPONSIBILITY OF THE SUPPLIER. THE PLAN SHOWN IS SCHEMATIC ONLY.
2. VERIFY SIZE AND LOCATION OF ALL SUPPORTED ITEMS WITH MANUFACTURER AND ARCH'L. DRAWINGS. PRIOR TO FABRICATING STEEL. PROVIDE ALL FRAMING INCLUDING SUB PURLINS AND ROD HANGERS BETWEEN "Z" PURLINS AS REQ'D.
3. THE CONTRACTOR SHALL VERIFY THE SIZE, LOCATION AND NUMBER OF MECH'L. UNITS SUPPORTED BY THE METAL BUILDING STRUCTURE PRIOR TO ORDERING THE METAL BUILDING. SUPPORT FRAMING SHALL BE PROVIDED FOR ALL UNITS WHETHER THEY ARE SHOWN ON THIS DRAWING OR NOT.

1 ROOF FRAMING PLAN
SCALE: 3/16"=1'-0"


CG5 ARCHITECT
TEXAS ARCHITECT
FIRM No: BR4247
WWW.CG5ARCHITECT.COM


SEAL:

**ECISD HIGH SCHOOL ATHLETIC MULTI-USE BUILDING 25-74**

ROBERT VELA HIGH SCHOOL

801 E Canton Rd, Edinburg, TX 78539

CLIENT:
EDINBURG CISD

REVISION:

| No. | Description | Date |
|---|---|---|
| | | |
| | | |
| | | |
| | | |

PROJECT #:
DRAWN BY:
CHECKED BY:
DATE: 4/28/25

ROOF FRAMING PLAN

S3.0

5-16-25
STATE OF TEXAS
C. HINOJOSA, JR.
90636
LICENSED PROFESSIONAL ENGINEER


CHLH
ENGINEERING, LLC
TBPE FIRM No. F-8719
701 S. 15th STREET McALLEN, TX. 78501
(956) 687-5560