


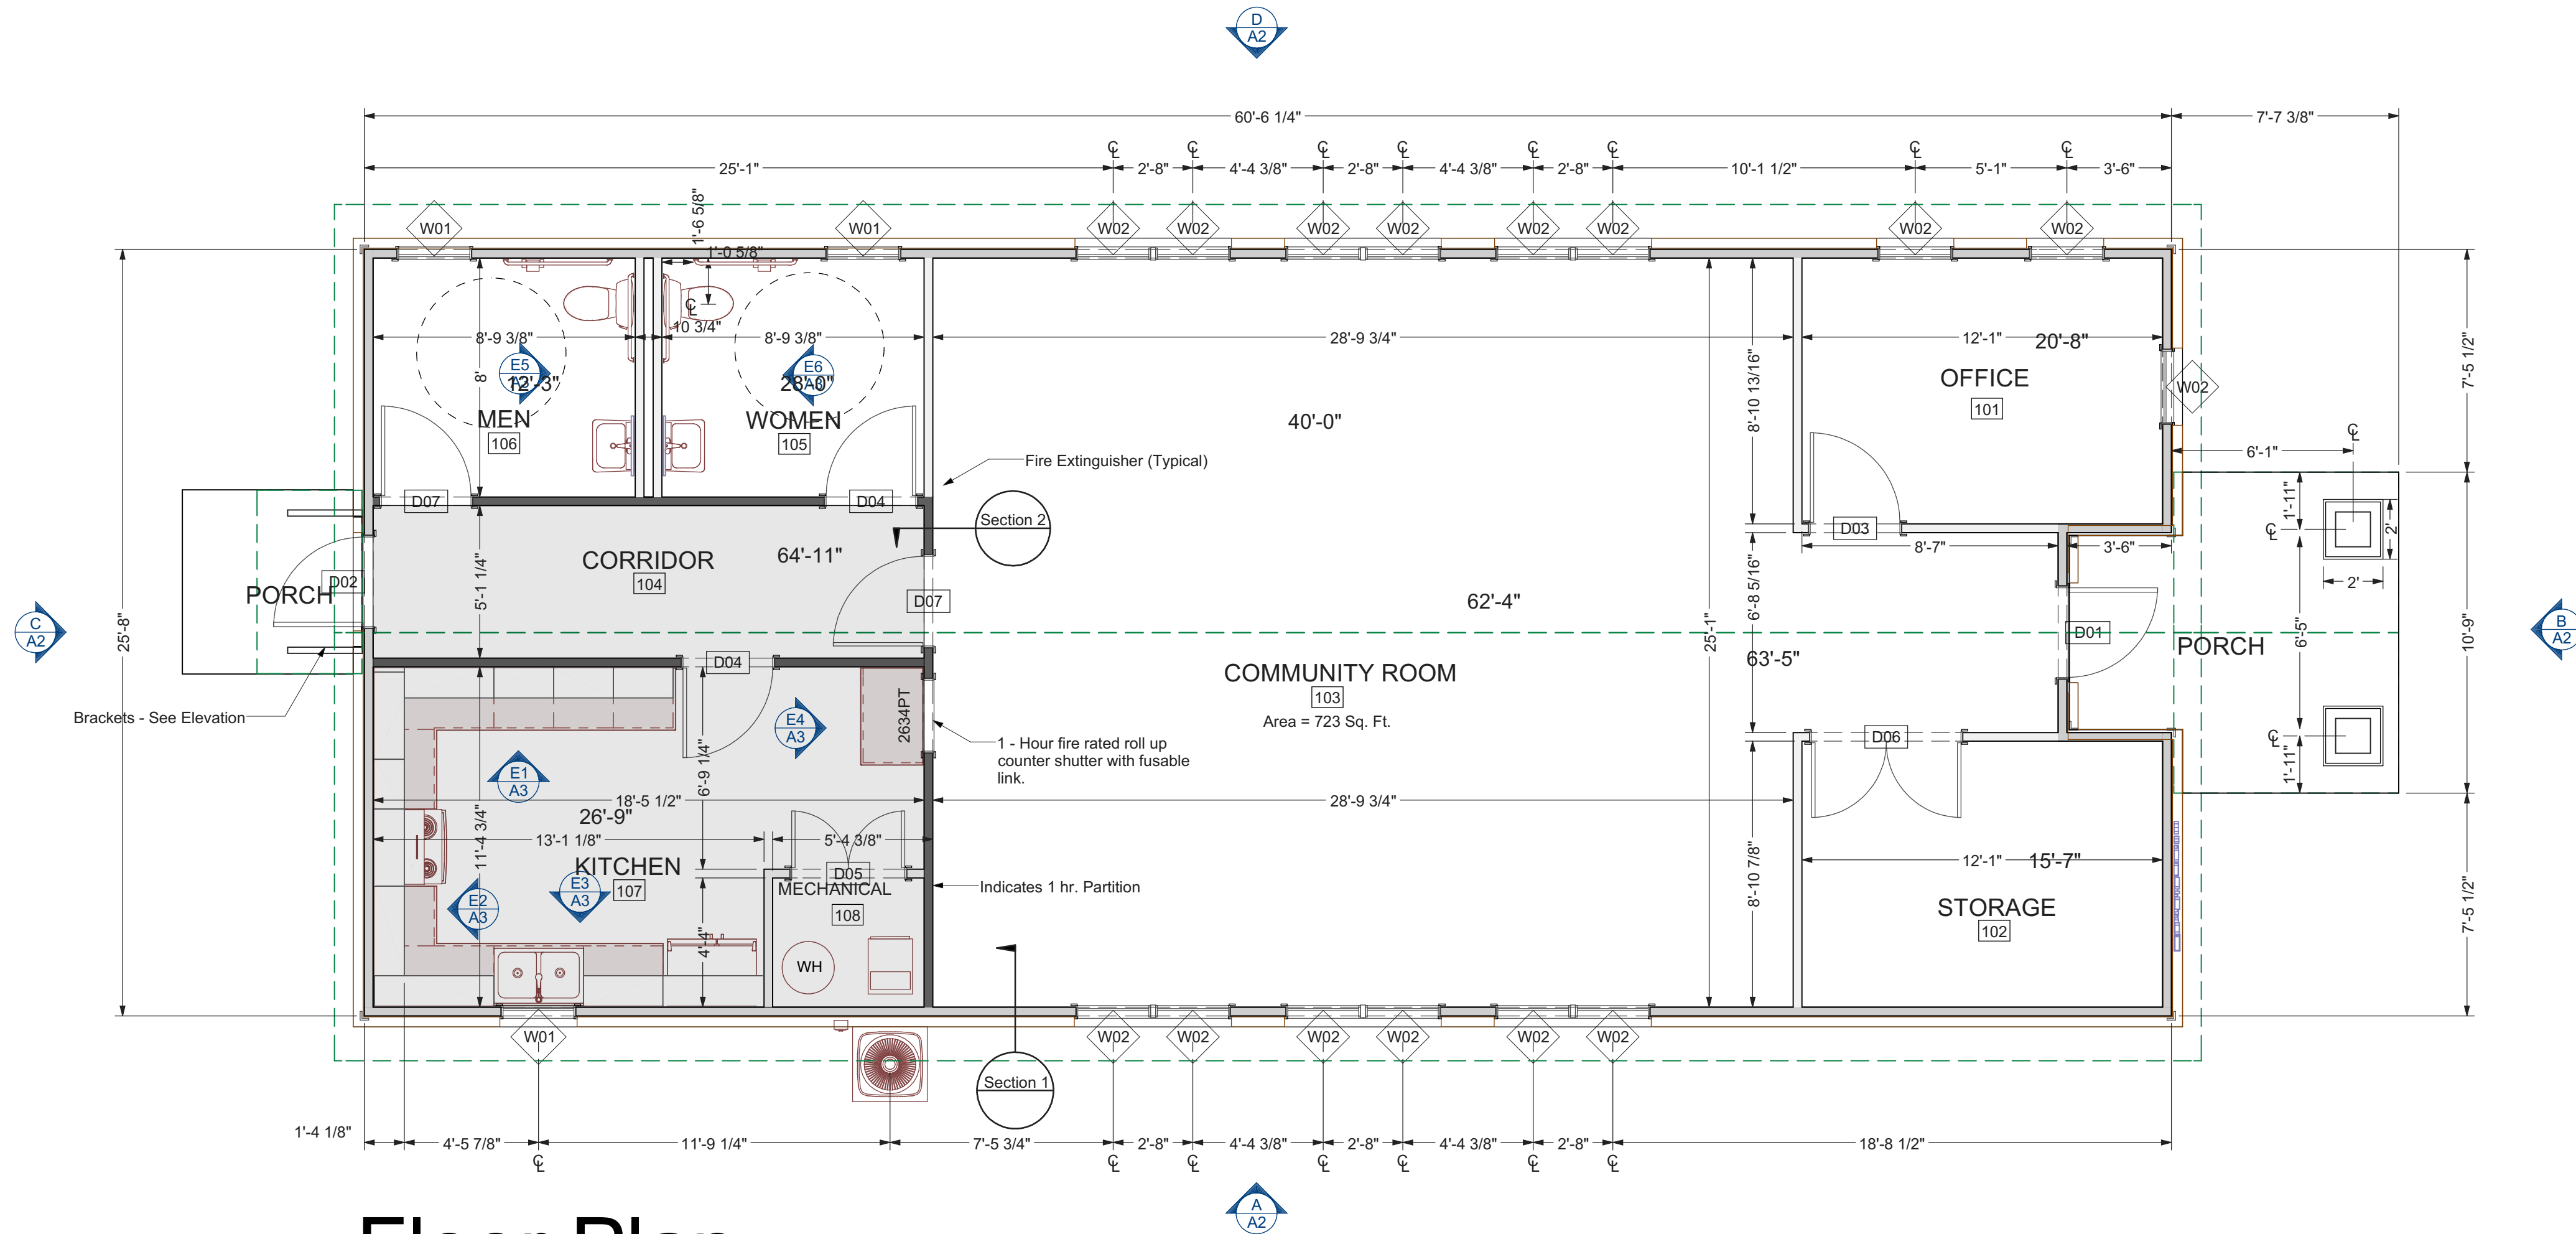

Floor Plan 1/4" = 1' - 0" (when printed on 24x36)

LIVING AREA
1530 SQ FT

Door Schedule											
Number	Label	Qty	Size	Width	Height	R/O	Description	Header	Thickness	Code	Comments
D01	3068	1	3068 L EX	36"	80"	38"X83"	ext. Hinged-Door E06	2"X6"X41" (2)	1 3/4"		
D02	3068	1	3068 L EX	36"	80"	38"X83"	ext. Hinged-Door E21	2"X6"X41" (2)	1 3/4"		
D03	3068	1	3068 L IN	36"	80"	38"X82 1/2"	Hinged-Door P09	2"X6"X41" (2)	1 3/8"		
D04	3068	2	3068 R IN	36"	80"	38"X82 1/2"	Hinged-Door P09	2"X6"X41" (2)	1 3/8"	1 Hr. Rating, C Label	
D05	3968	1	3968 L/R IN	45 7/16"	80"	47 7/16"X82 1/2"	Double Hinged-Door P09	2"X6"X50 7/16" (2)	1 3/8"		
D06	5068	1	5068 L/R IN	60"	80"	62"X82 1/2"	Double Hinged-Door P09	2"X6"X65" (2)	1 3/8"		
D07	3068	2	3068 L IN	36"	80"	38"X82 1/2"	Hinged-Door P09	2"X6"X41" (2)	1 3/8"	1 Hr. Rating, C Label	

Window Schedule									
Number	Label	Qty	Size	Width	Height	R/O	Egress	Description	Header
W01	2630SH	3	2630SH	30"	36"	31"X37"		Single Hung	2"X6"X34" (2)
W02	26410SH	15	26410SH	30"	58"	31"X59"		Single Hung	2"X6"X34" (2)

Revision Table		Revised By		Description	
Number	Date				