

GENERAL NOTES:

GENERAL CONDITIONS
Maintain Utilities During Construction
Temporary Toilet
Dumpsters and Clean-up
Worker's Compensation and Liability Insurance
Permits and Fees
All Work to be Performed in Accordance with all Local Codes/Ordinances

PROJECT PROTECTION & DEMOLITION
See Notes On Existing Conditions / Demolition Drawings

SITEWORK & EXCAVATION
Relocate Plantings as Required
Excavation & Backfill for New Foundation
Excavation & Backfill for New Bulkhead
Rough and Final Grading - Landscaping and Irrigation by Others

CONCRETE & MASONRY
Cut Concrete/Stone Foundation Wall for New Bulkhead & Openings into New Basement
Reinforced Concrete Foundation Walls & Footings
Reinforced Concrete Slabs on Grade

ROUGH CARPENTRY
2 x 6 Exterior Wall Framing @ 16" O.C.
2 x 4 Interior Wall Framing @ 16" O.C.
Conventional Wood Joists and Beams - See Framing Plans
Engineered Wood Joists and Beams - See Framing Plans
Conventional and Engineered Roof Framing - See Framing Plans
Roof and Wall Sheathing - Zip System
SubFloor - 3/4" T&G Plywood or OSB
Rafter Tails and Soffit Blocking to Create Overhangs at Existing House
Misc. Blocking, Strapping, Fire Blocking and Fire Stopping
Solid Blocking @ All Towel Bars & Accessories

FINISH CARPENTRY
Paint Grade PFJ Poplar or Pine at All Interior Trim
Siding: Pre-Stained White Cedar Shingles - To Match Existing Exposure
5/4 Boral TruExterior at All New Window/Door/Corner
1x Boral TruExterior at All New Fascia/Frieze/Rake/Soffit Trim
Composite Decking w/ Color Matching Screws
RDI Excalibur Railing System @ Rear Entry
Conceal Fasteners to Greatest Practical Extent by Countersinking and Filling
Use Full Length Boards Where Possible, Otherwise Scarf Joints

THERMAL AND MOISTURE PROTECTION
Min. R-30 Spray Foam Insul. at All Above Grade New Exterior Walls
Min. R-60 Combination Spray Foam (Closed & Open Cell) at Entire New Roof
Sound Attenuating Batt Insulation @ All Bath Walls & Floors
Dampproofing @ All New Foundation Walls
Certainteed 'Landmark' Roof Shingles or Equal at New and Affected Areas - Match Existing
Ice and Water Barrier at All New & Affected Roofs
5" K-Style Alum. Gutters and Round Downspouts to Match Existing
Self-Adhered Flashing and Sill Pan Flashing at New Windows per Window Manufacturer Rec.

DOORS AND WINDOWS
Paint Grade MDF Interior Panel Doors to Match Existing - Provide Allowance
Exterior Doors - Provide Allowance for a (2) New Mudroom Doors.
Andersen 400 Series Windows as Indicated - See Sched.
Door Hardware - Provide Allowance

FINISHES
Gypsum Veneer Plaster on 1/2" Blueboard at All Affected Areas - Smooth Finish Throughout
Benjamin Moore Primer and Two Coats Regal Select Finish Paint at all Interior Surfaces
Benjamin Moore Primer and Two Coats 'Advance' Finish Paint at All Interior Trim
Benjamin Moore Primer and Two Coats Flat Ceiling Paint at all Ceilings
Sherwin Williams Primer and Two Coats 'Emerald' Paint at All Exterior Siding & Trim

FLOORING AND TILE
Hardwood Flooring to Match Existing - Provide Allowance
Sand/Finish New & Affected Hardwood Floors with Sealer and Oil Finish
Porcelain/Ceramic Tile at All New Bathrooms - Provide Material Allowance
Cement Backer Board at all Tiled Areas
Rubber Shower Pan at Tiled Showers
All Floor Material Transitions Shall Occur at Center of Door Slab or Center of Cased Opening

SPECIALITES
3/8" Frameless Temp. Shower Glass & Door - Provide Allowance
Hardware Finish Shall be Approved by Owner.
Wall Mirrors & Bath Accessories - Provide Allowance

KITCHEN/BATH
Kitchen Cabinets - Provide Allowance
Kitchen Counters - Provide Allowance
Bath Cabinets/Counters - Provide Allowance
Appliances - Provide Allowance
Kitchen/Bath Exhaust - Provide Allowance

MECHANICAL & PLUMBING
Remove all Existing Air Handling Equipment and Ductwork
Heating & Cooling to be Design/Build
Kitchen/Bath Exhaust Ducting for New and Existing Baths
Kitchen Makeup Air Damper with Pressure Sensor
Dryer Vent Ducting to Exterior
3/4" H&C Supply Lines to New Bath
Hot Water Return from Most Remote Fixture at New Bath with Recirc. Pump
Stainless Steel Drain at Tiled Showers
Plumbing Fixtures as Indicated - Provide Allowance
All Water Supply Lines Shall be Copper or PEX

ELECTRICAL
Recessed Lighting at New Areas
Surface Mounted Lighting - Provide Allowance
Exterior Building Lighting - Provide Allowance
Appliance Wiring & Installation
Bath Fan Supply/Install
Makeup Air Switch Connection
Provide Dimmer Quantity Allowance

PROJECT INFORMATION

PROJECT DESCRIPTION: ALTERATIONS TO SINGLE FAMILY RESIDENCE
BUILDING TYPE: DETACHED SINGLE-FAMILY DWELLING
BUILDING CODE REFERENCES: MASS. ONE & TWO FAMILY DWELLING CODE - 9TH ED.
IECC 2021 ENERGY CODE WITH MASS. AMENDMENTS

SHEET INDEX			
DWG #:	DRAWING TITLE	ISSUE DATES	ISSUE DATES
		PRICING SET 2022.02.09	PERMIT SET 2023.03.16
T1.0	TITLE SHEET	X	X
EC1.1	EXISTING BASEMENT & FIRST FLOOR PLANS W/ DEMO	X	X
EC2.1	EXISTING EXTERIOR ELEVATIONS W/ DEMO	X	X
EC2.2	EXISTING EXTERIOR ELEVATIONS W/ DEMO	X	X
A1.0	PROPOSED BASEMENT PLAN	X	X
A1.1	PROPOSED FIRST FLOOR PLAN	X	X
A2.1	EXTERIOR ELEVATIONS	X	X
A2.2	EXTERIOR ELEVATIONS	X	X
A3.0	STRUCTURAL NOTES & SHEAR WALL DETAIL	X	X
A3.1	FOUNDATION PLAN	X	X
A3.2	FIRST FLOOR FRAMING PLAN	X	X
A3.3	ROOF FRAMING PLAN	X	X
A4.0	DOOR & WINDOW SCHEDULE	X	X
A4.1	BASEMENT REFLECTED CEILING PLAN	X	X
A4.2	FIRST FLOOR REFLECTED CEILING PLAN	X	X

ALTERATIONS TO THE PIGNATELLI RESIDENCE

11 SILVER HILL RD WESTON, MA



KRAUS ASSOCIATES

66 CENTRAL STREET STE. 2
WELLESLEY, MA 02482
(781) 431-7400
WWW.KRAUSAB.COM

ALL RIGHTS RESERVED. NO USE OR REPRODUCTION OF THIS MATERIAL IS PERMITTED WITHOUT WRITTEN CONSENT.

DO NOT SCALE THE DRAWINGS. USE ALL DIMENSIONS SHOWN. VERIFY ALL DIMENSIONS ON SITE & NOTIFY ARCHITECT OF ANY DISCREPANCIES.

No.	Date	Description

PROJECT NAME:
PIGNATELLI
RESIDENCE

11 SILVER HILL RD
WESTON, MA



DRAWING NAME:
TITLE SHEET

DATE:	03.16.2023
PROJECT NO:	21031
SCALE:	
DRAWN & CHECKED BY:	JJ/CK

DRAWING NO:
T1.1

2023.03.16 - PROGRESS SET




ALL RIGHTS RESERVED. NO USE OR
REPRODUCTION OF THIS MATERIAL IS PERMITTED
WITHOUT WRITTEN CONSENT.

PROJECT NAME:
**PIGNATELLI
RESIDENCE**

A circular professional seal for a registered architect. The outer ring contains the text "REGISTERED ARCHITECT" at the top and "COMMONWEALTH OF MASSACHUSETTS" at the bottom. The center of the seal contains the name "CHARLES E. FUGATE", the number "No. 10560", and the location "BOSTON MASS.". A blue ink signature is written across the seal.

EC1.1

2023.03.16 - PROGRESS SET

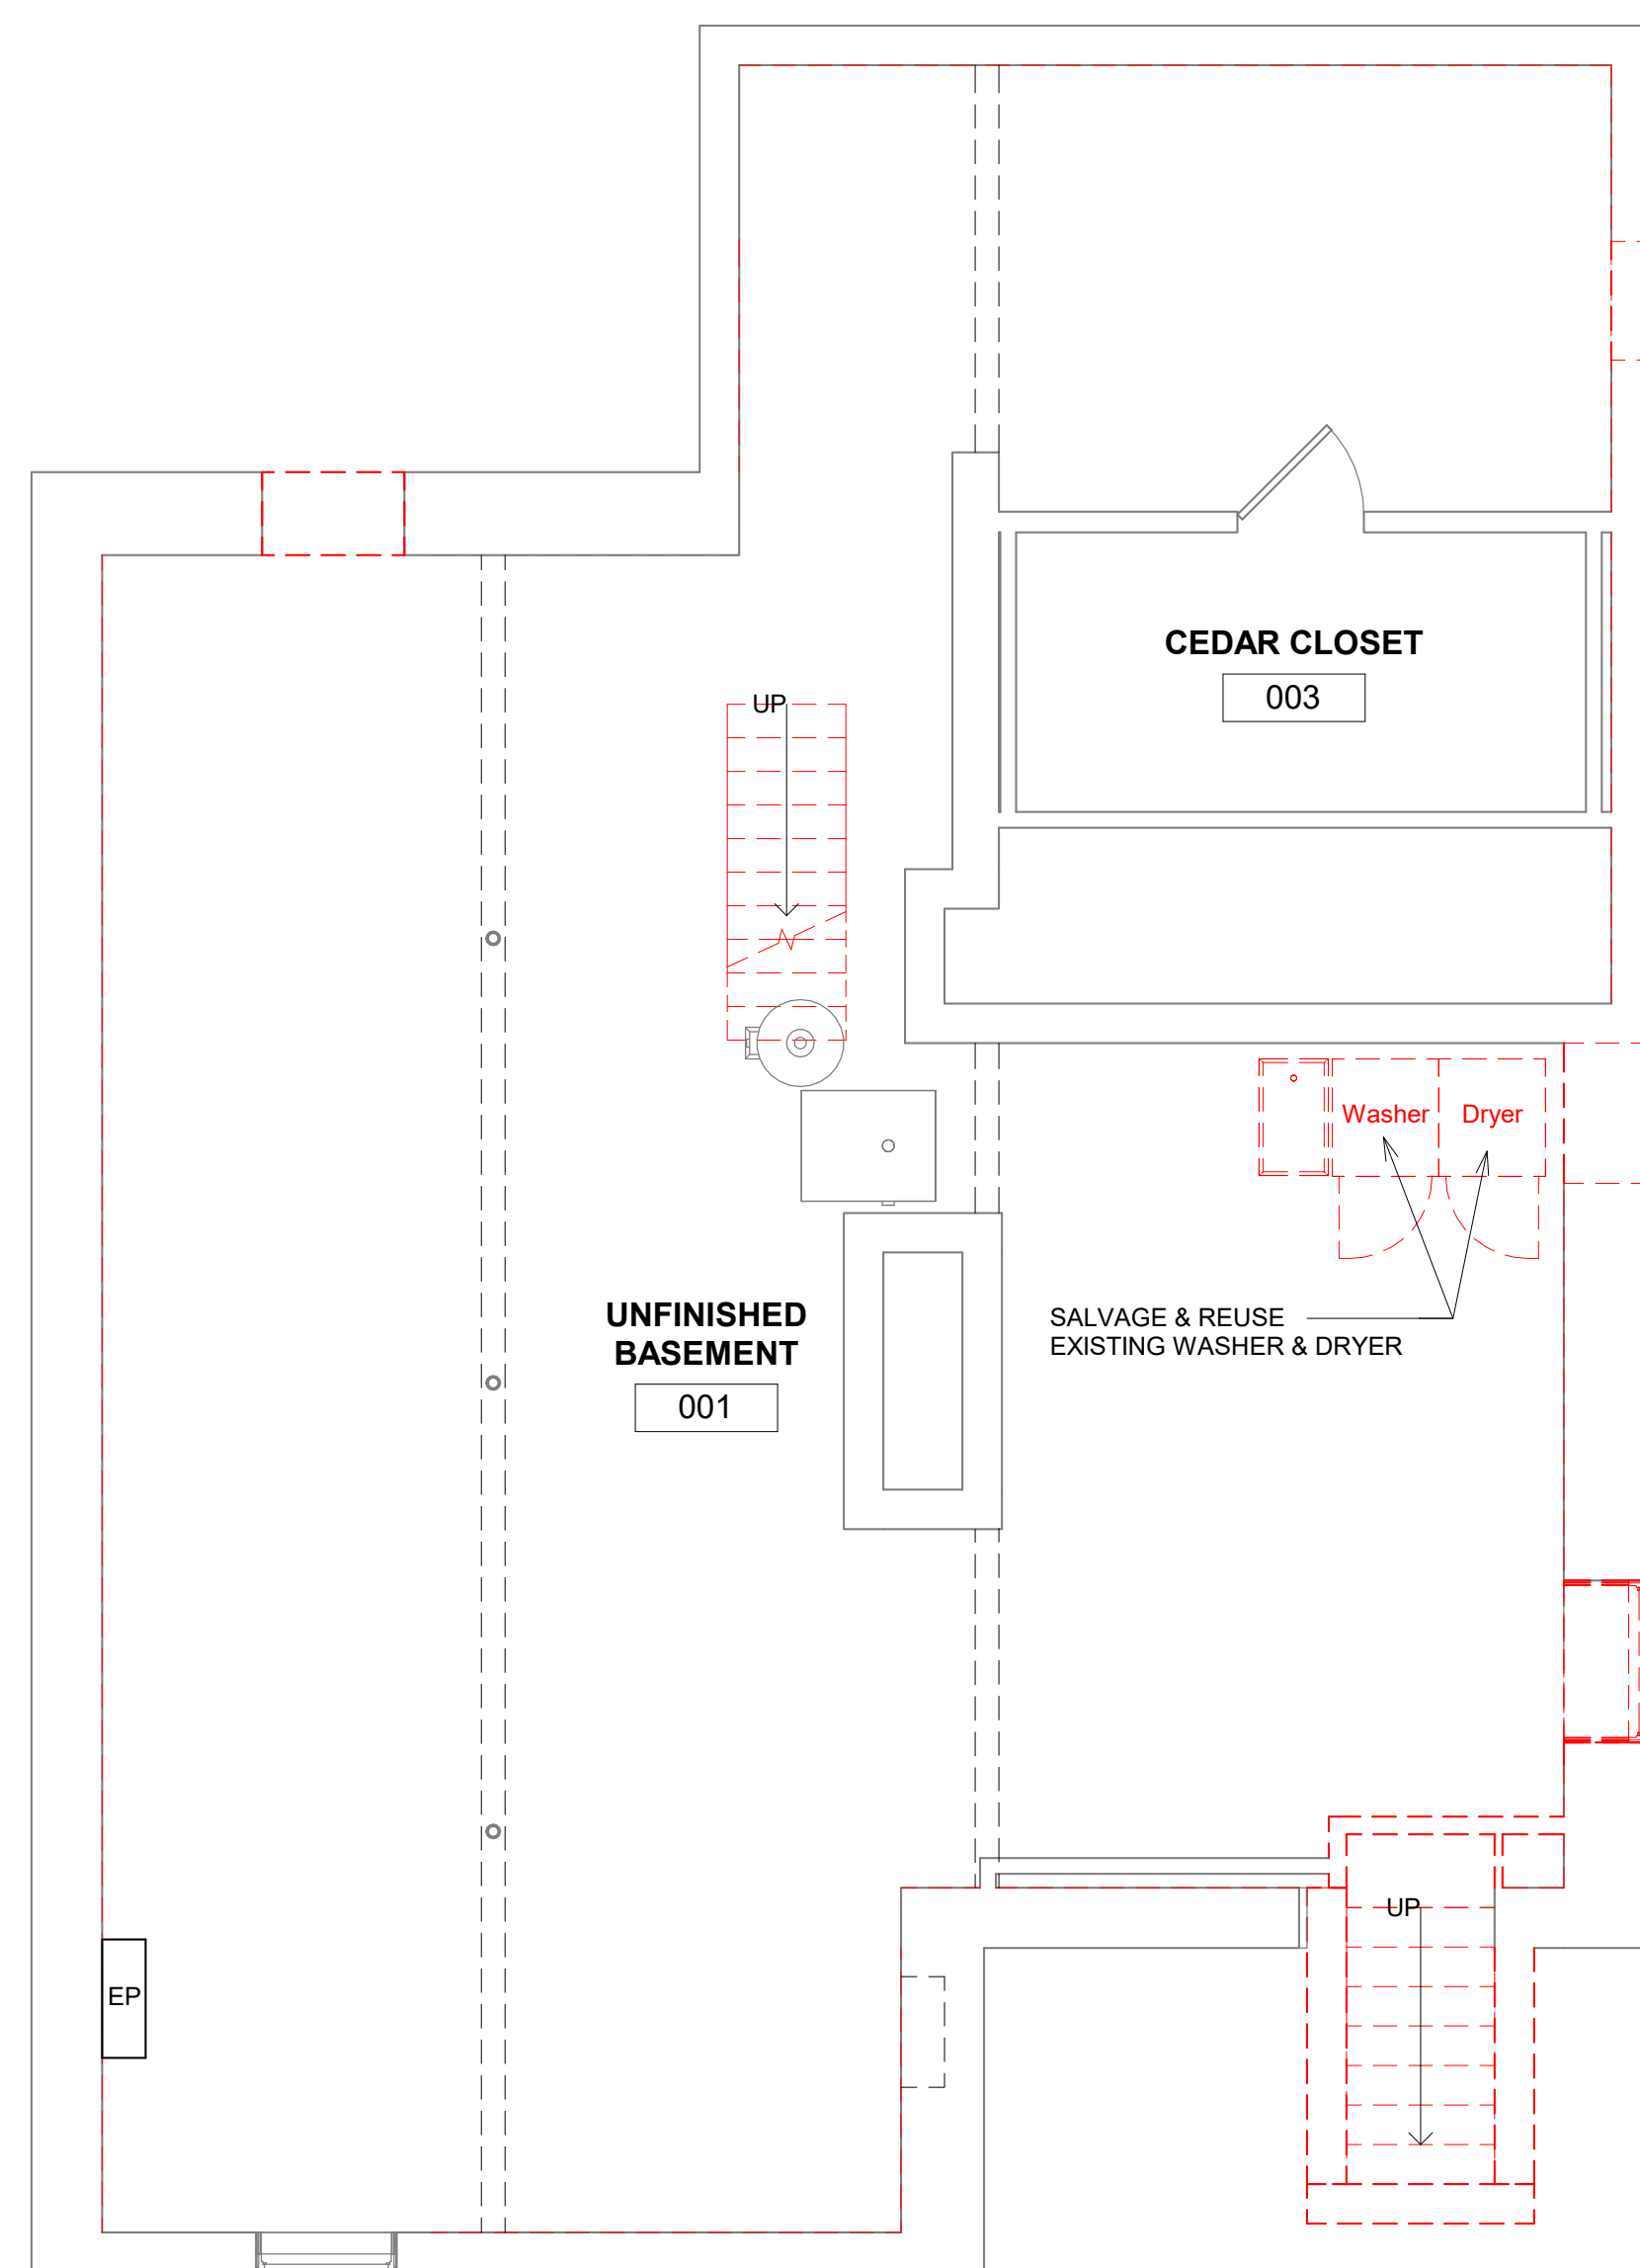


Architectural floor plan of the first floor of a building. The plan shows a large rectangular room on the left, a central corridor, and several smaller rooms on the right. A staircase is located in the bottom left corner, labeled "DN" and "11' - 7\" V.I.F.". A north arrow is located in the bottom right corner. The plan is titled "FIRST FLOOR - ECIDEMO" at the bottom left.



TRUE NORTH


EXISTING

DEMO

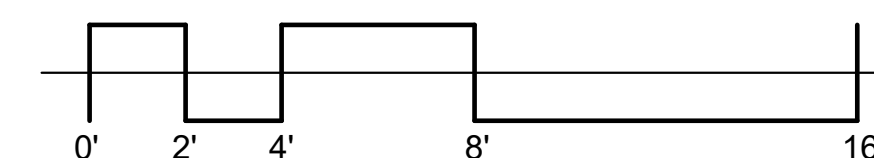




① WEST ELEVATION - EC/DEMO
1/4" = 1'-0"

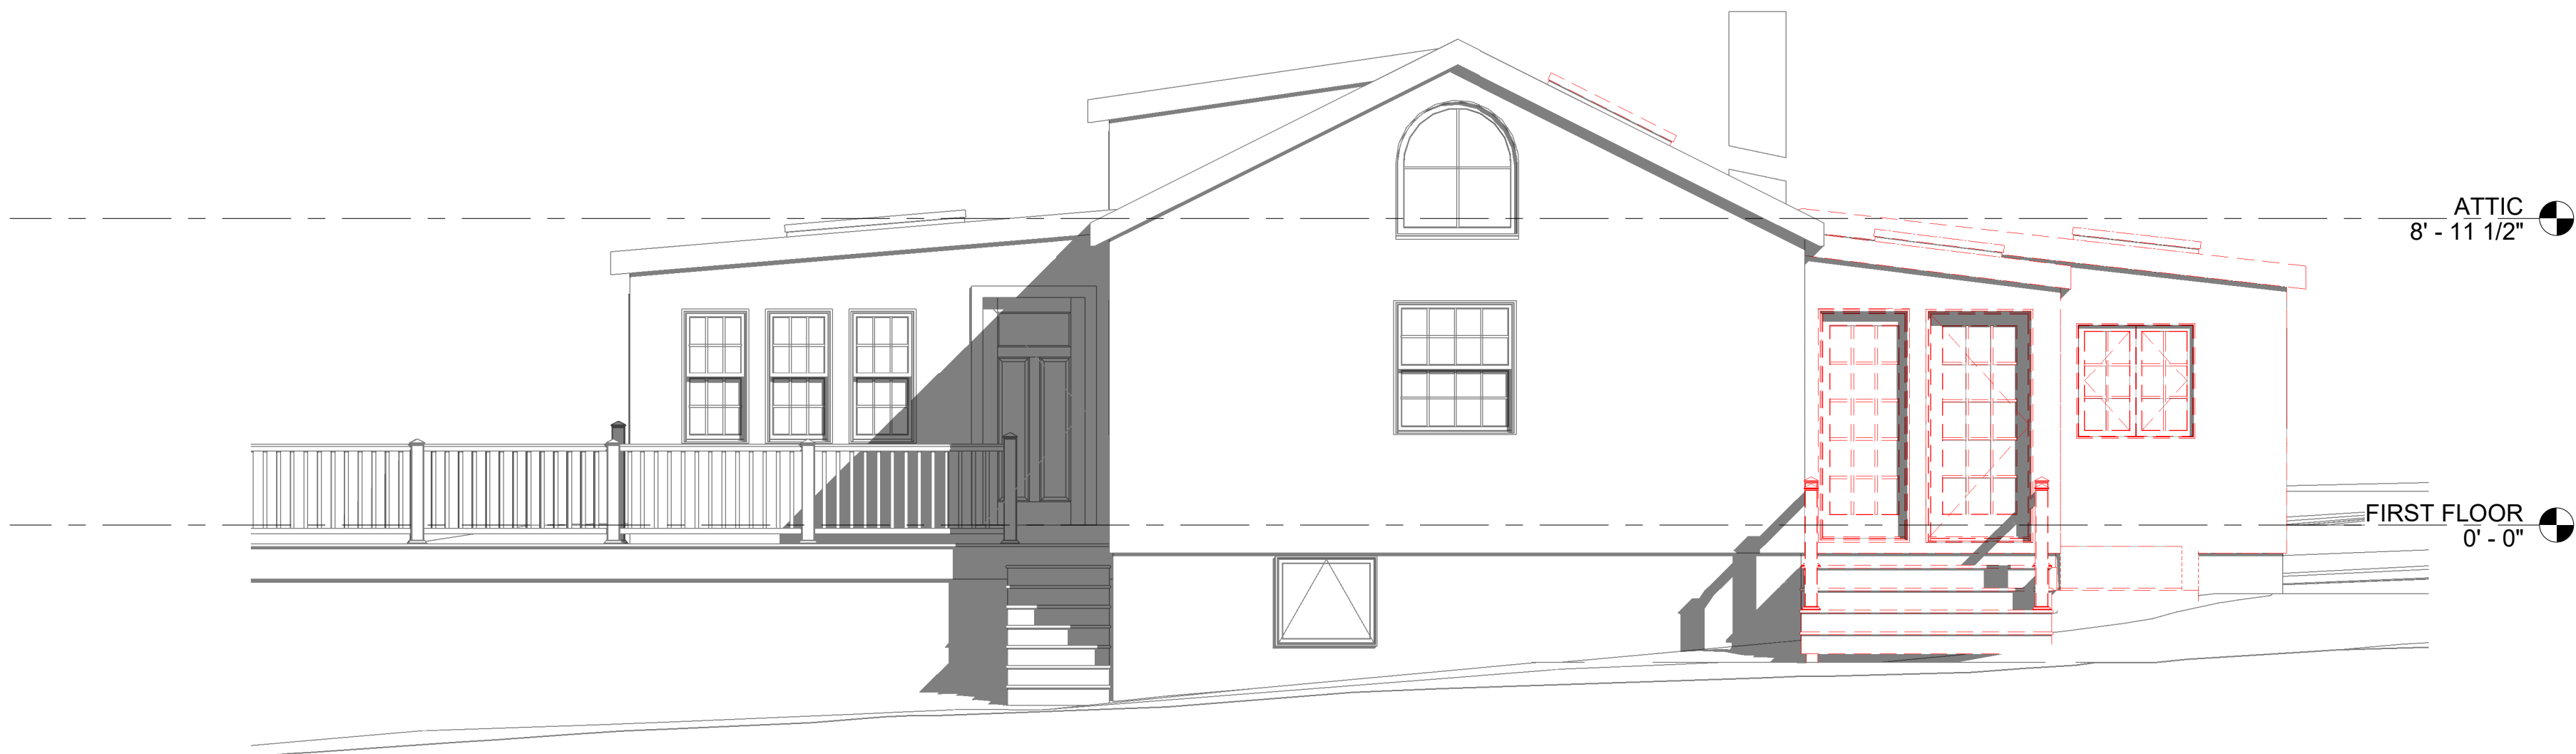

② SOUTH ELEVATION - EC/DEMO
1/4" = 1'-0"

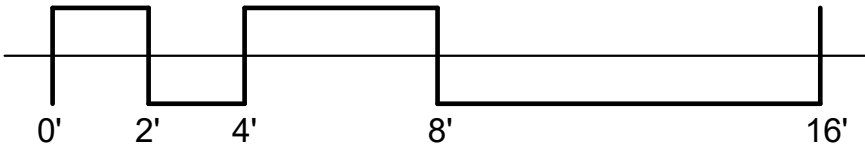

KRAUS ASSOCIATES

66 CENTRAL STREET STE. 2
WELLESLEY, MA 02482
(781) 431-7400
WWW.KRAUSAB.COM

ALL RIGHTS RESERVED. NO USE OR
REPRODUCTION OF THIS MATERIAL IS PERMITTED
WITHOUT WRITTEN CONSENT.

DO NOT SCALE THE DRAWINGS. USE ALL
DIMENSIONS SHOWN. VERIFY ALL DIMENSIONS ON
SITE & NOTIFY ARCHITECT OF ANY
DISCREPANCIES.

No.	Date	Description

PROJECT NAME:
**PIGNATELLI
RESIDENCE**


**11 SILVER HILL RD
WESTON, MA**




DRAWING NAME:
**EXISTING
EXTERIOR
ELEVATIONS W/
DEMO**

DATE:	03.16.2023
PROJECT NO:	21031
SCALE:	1/4" = 1'-0"
DRAWN & CHECKED BY:	JJ/CK


DRAWING NO:
EC2.1

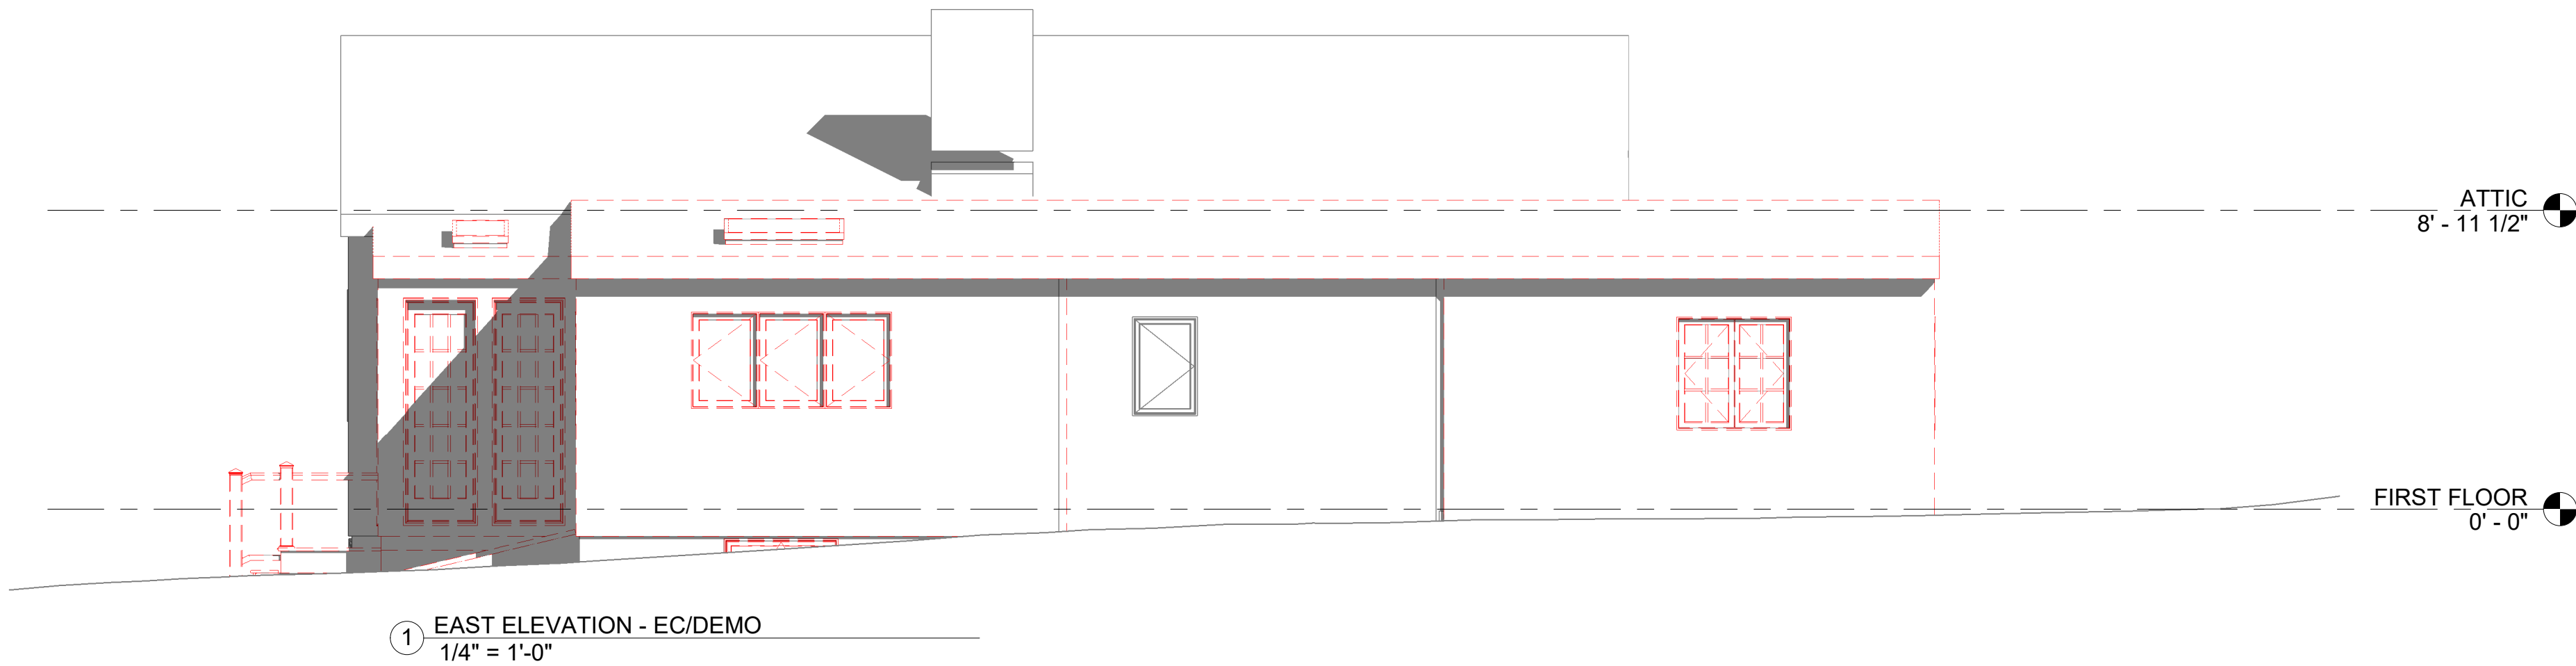

① EAST ELEVATION - EC/DEMO
1/4" = 1'-0"

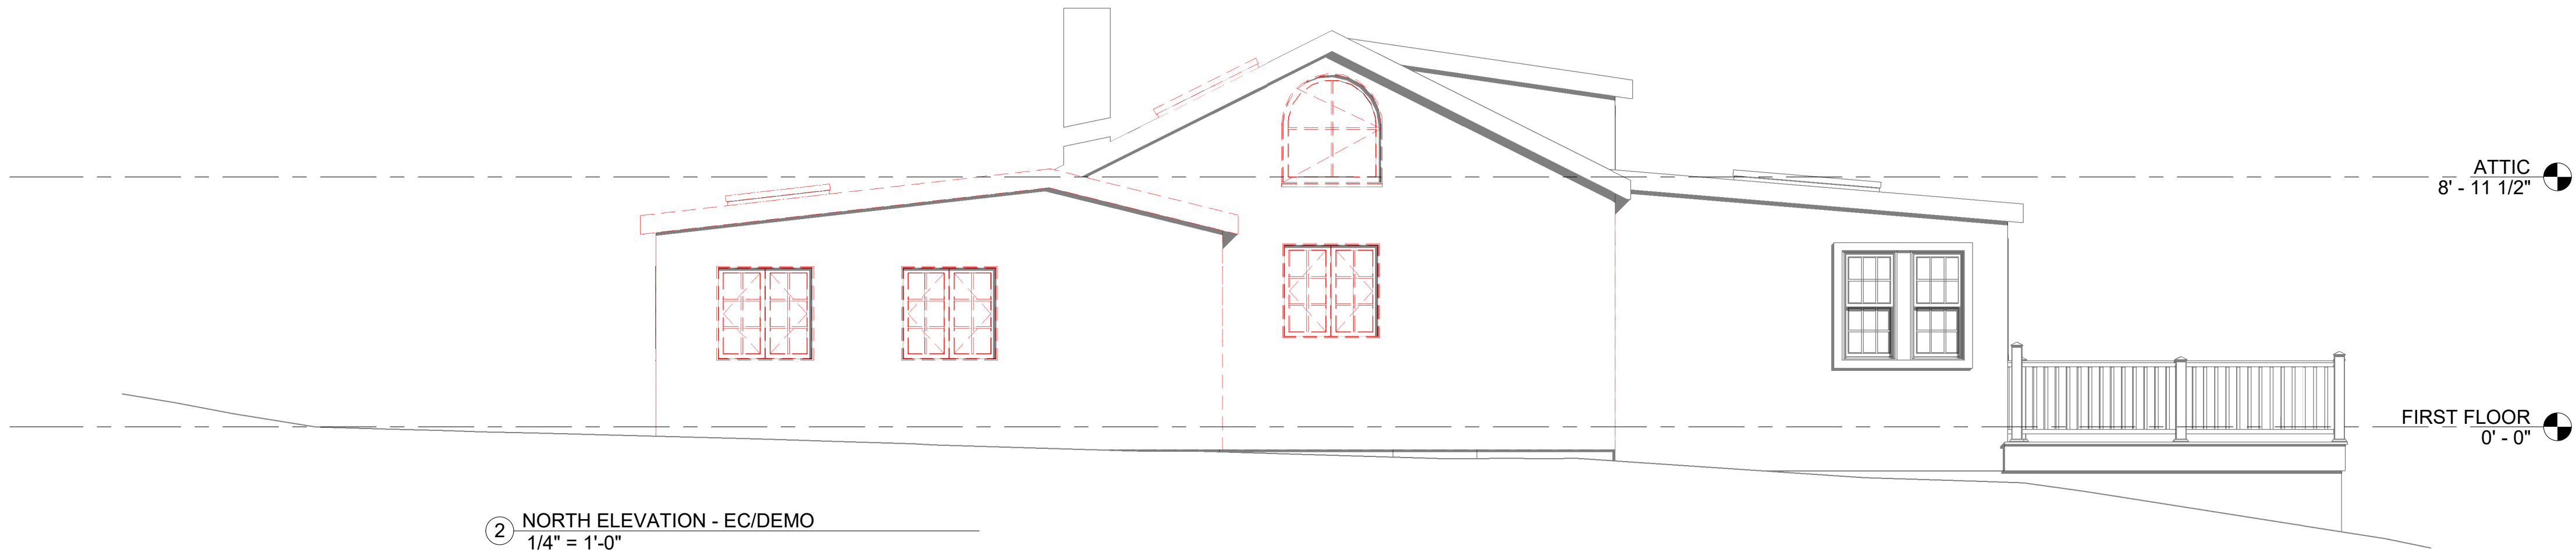

② NORTH ELEVATION - EC/DEMO
1/4" = 1'-0"

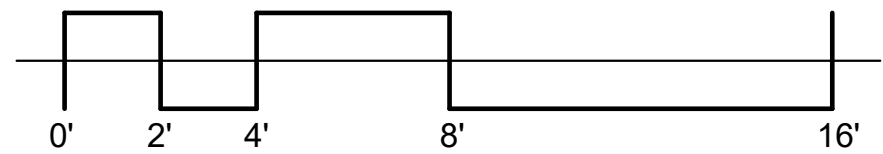

KRAUS ASSOCIATES

66 CENTRAL STREET STE. 2
WELLESLEY, MA 02482
(781) 431-7400
WWW.KRAUSAB.COM

ALL RIGHTS RESERVED. NO USE OR REPRODUCTION OF THIS MATERIAL IS PERMITTED WITHOUT WRITTEN CONSENT.

DO NOT SCALE THE DRAWINGS. USE ALL DIMENSIONS SHOWN. VERIFY ALL DIMENSIONS ON SITE & NOTIFY ARCHITECT OF ANY DISCREPANCIES.

No.	Date	Description

PROJECT NAME:
**PIGNATELLI
RESIDENCE**

**11 SILVER HILL RD
WESTON, MA**



DRAWING NAME:

**EXISTING
EXTERIOR
ELEVATIONS W/
DEMO**

DATE:	03.16.2023
PROJECT NO:	21031
SCALE:	1/4" = 1'-0"
DRAWN & CHECKED BY:	JJ/CK

DRAWING NO:

EC2.2




ALL RIGHTS RESERVED. NO USE OR
REPRODUCTION OF THIS MATERIAL IS PERMITTED
WITHOUT WRITTEN CONSENT.

DO NOT SCALE THE DRAWINGS. USE ALL DIMENSIONS SHOWN. VERIFY ALL DIMENSIONS ON SITE & NOTIFY ARCHITECT OF ANY DISCREPANCIES.

[illegible]

PROJECT NAME:

11 SILVER HILL RD
WESTON, MA

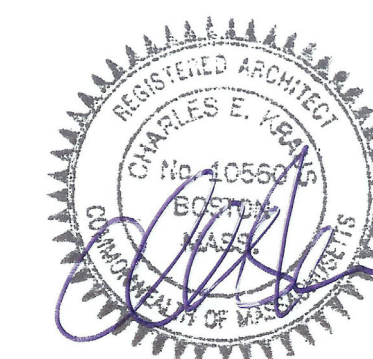

DRAWING NAME:

DATE:	03.16.2023
-------	------------

PROJECT NO:	21031
-------------	-------



SCALE: $1/4" = 1'-0"$

DRAWN & CHECKED BY:	JJ/CK
---------------------	-------

DRAWING NO:


A1.0

2023.03.16 - PROGRESS SET

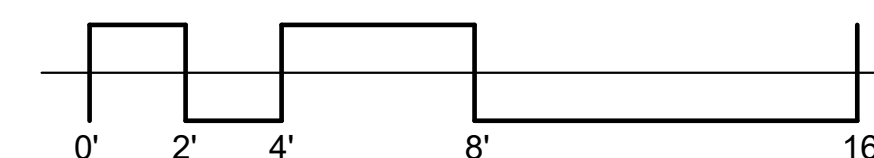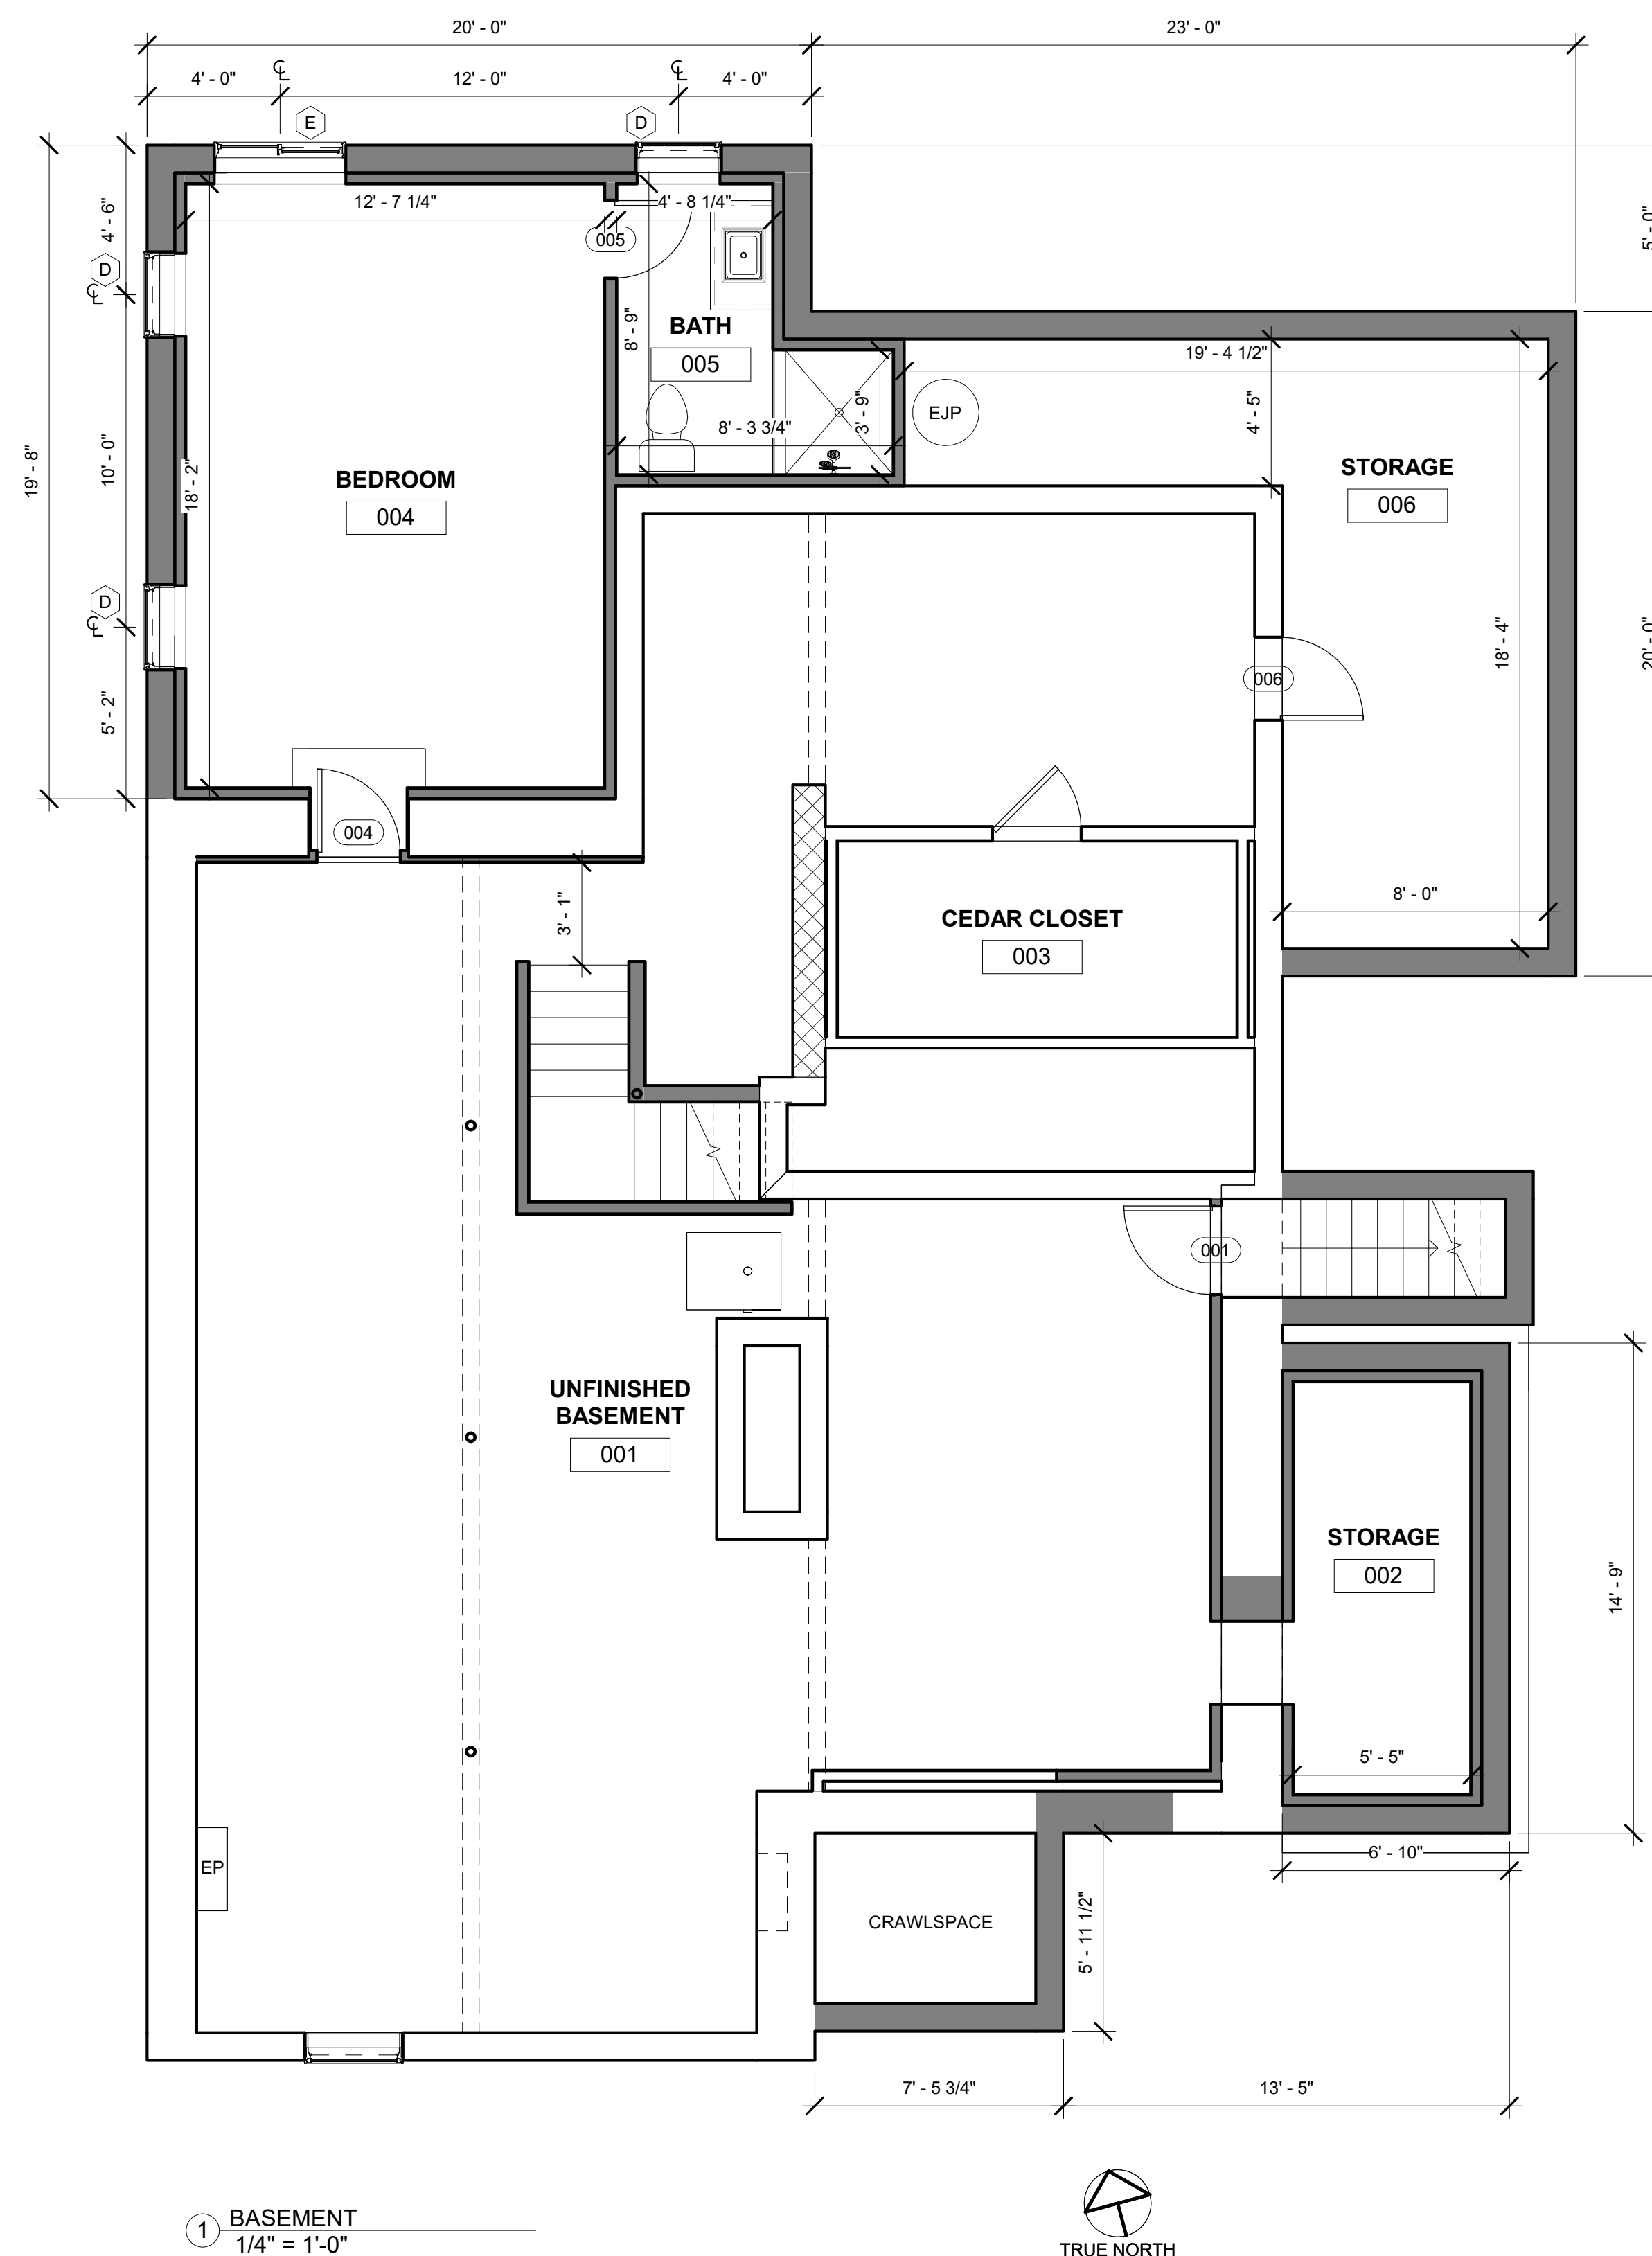



2 FIRST FLOOR
1/4" = 1'-0"

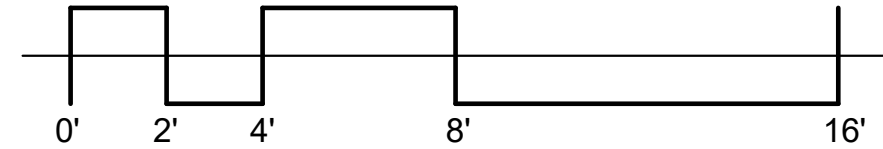

KRAUS ASSOCIATES

66 CENTRAL STREET STE. 2
WELLESLEY, MA 02482
(781) 431-7400
WWW.KRAUSAB.COM


ALL RIGHTS RESERVED. NO USE OR REPRODUCTION OF THIS MATERIAL IS PERMITTED WITHOUT WRITTEN CONSENT.

DO NOT SCALE THE DRAWINGS. USE ALL DIMENSIONS SHOWN. VERIFY ALL DIMENSIONS ON SITE & NOTIFY ARCHITECT OF ANY DISCREPANCIES.

No.	Date	Description

PROJECT NAME:
PIGNATELLI RESIDENCE


**11 SILVER HILL RD
WESTON, MA**

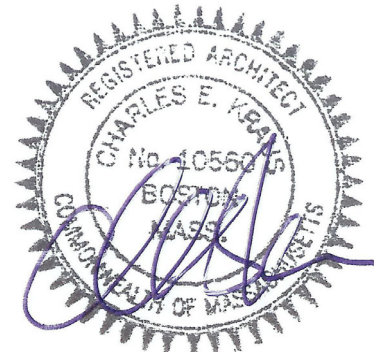


DRAWING NAME:
**FIRST FLOOR
PLAN**

DATE:	03.16.2023
PROJECT NO:	21031
SCALE:	1/4" = 1'-0"
DRAWN & CHECKED BY:	JJ/CK
DRAWING NO:	


A1.1

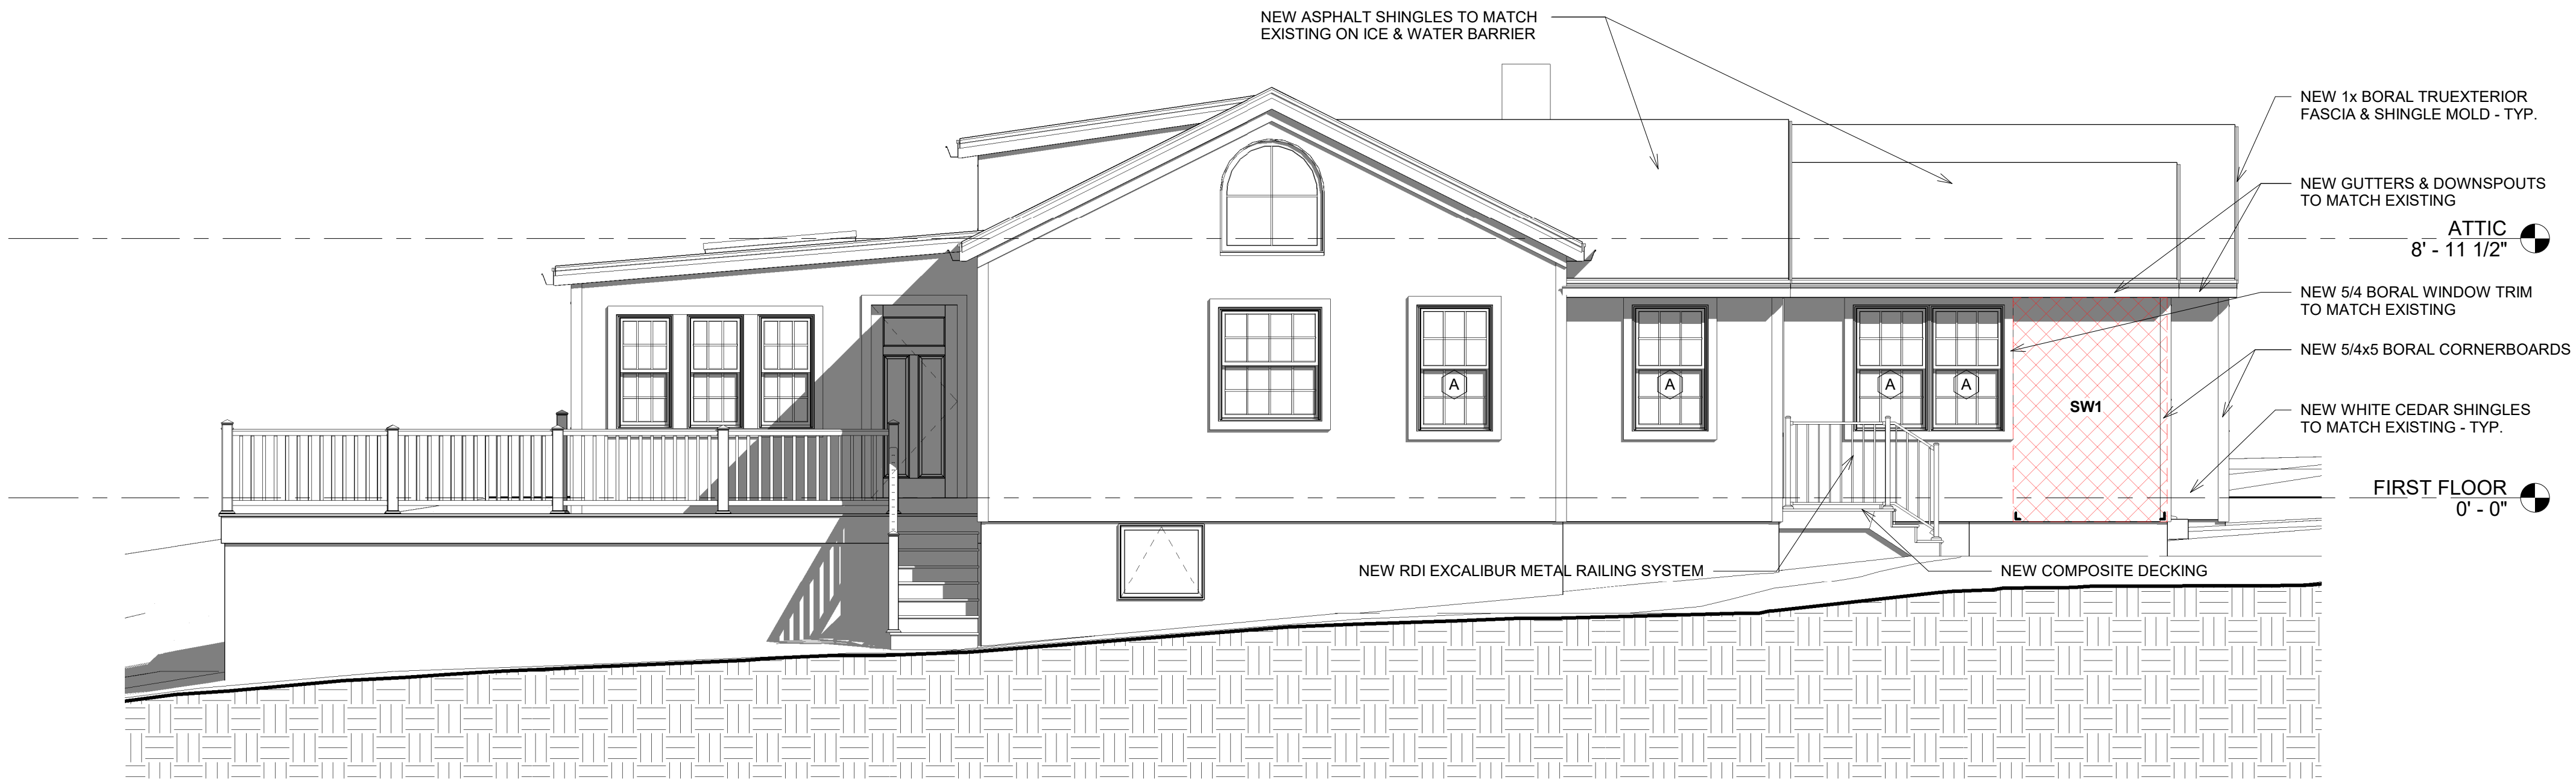

① SOUTH ELEVATION
1/4" = 1'-0"

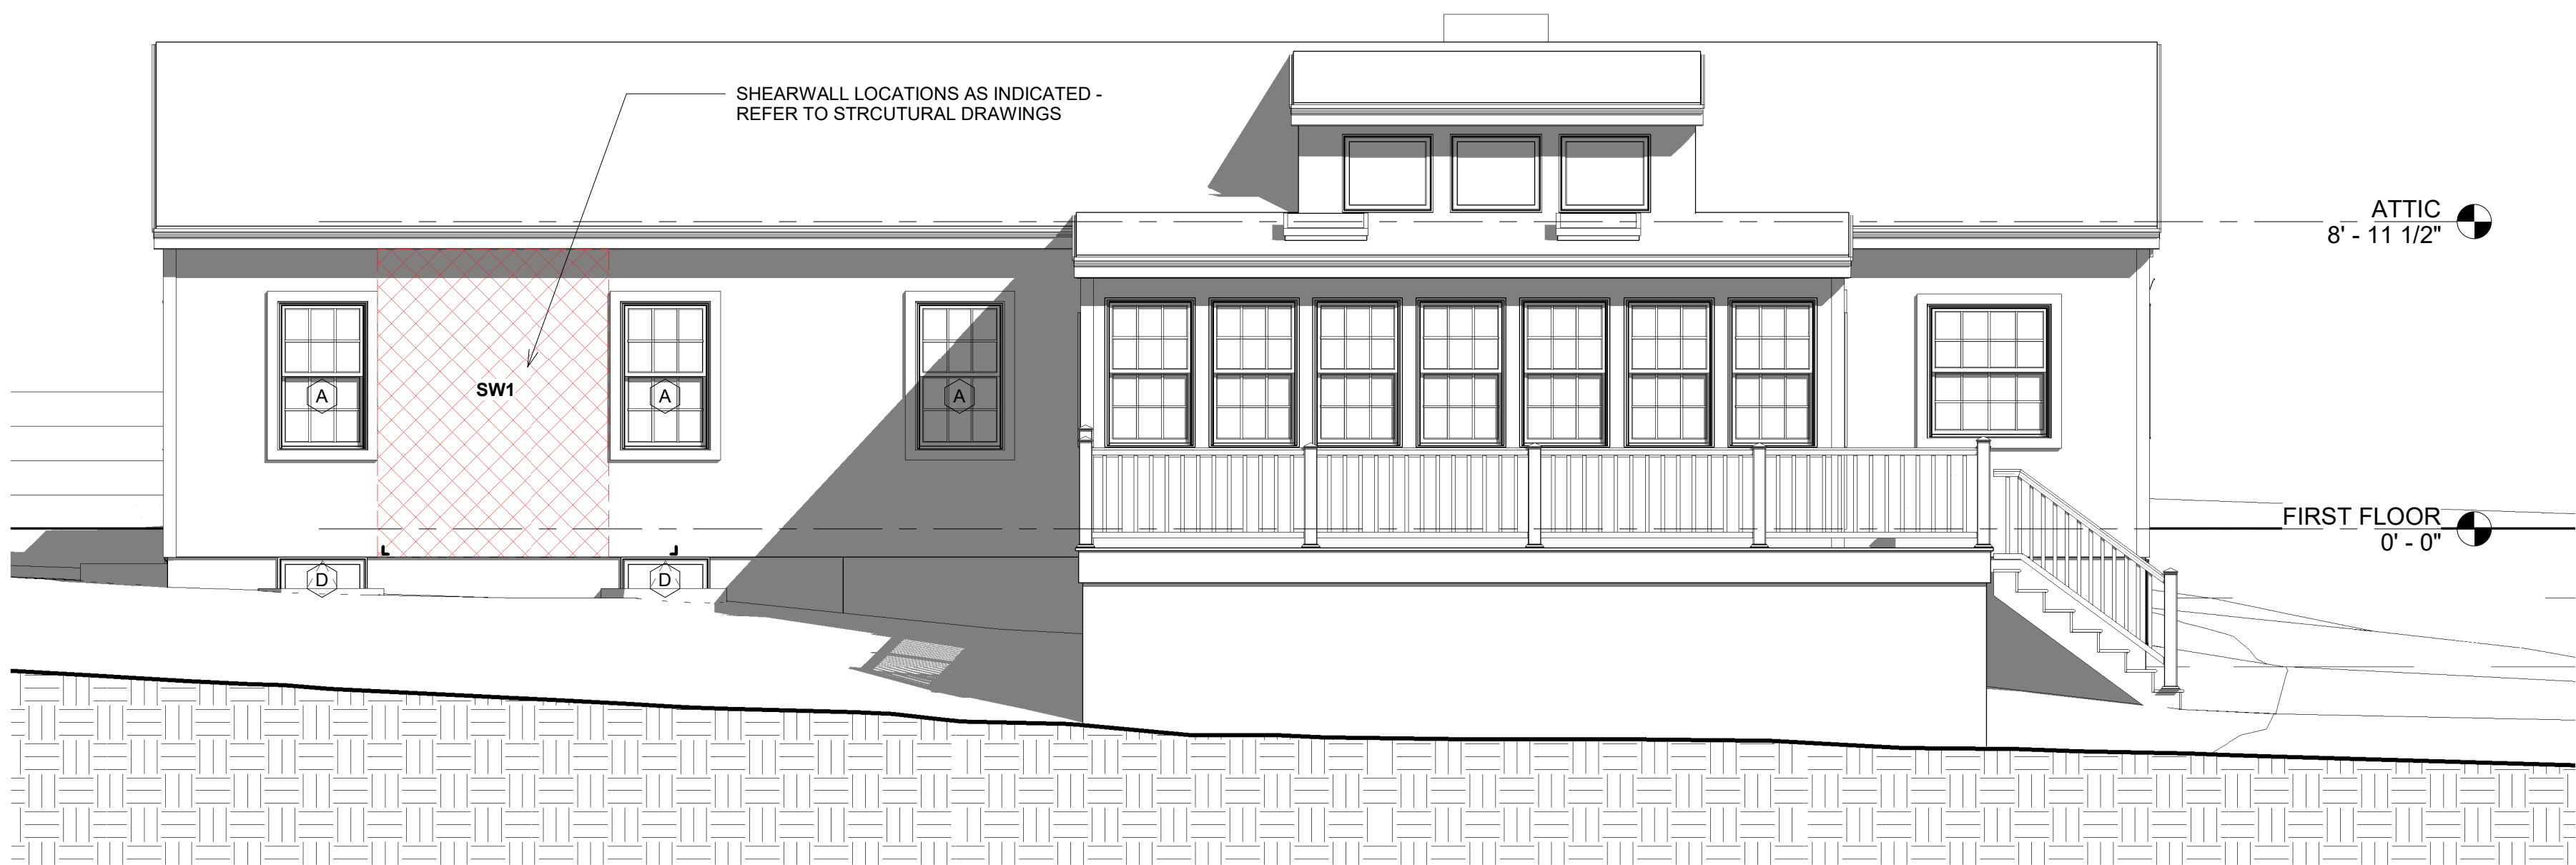

② WEST ELEVATION
1/4" = 1'-0"

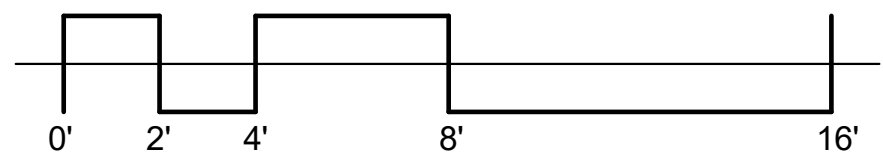

KRAUS ASSOCIATES

66 CENTRAL STREET STE. 2
WELLESLEY, MA 02482
(781) 431-7400
WWW.KRAUSAB.COM

ALL RIGHTS RESERVED. NO USE OR REPRODUCTION OF THIS MATERIAL IS PERMITTED WITHOUT WRITTEN CONSENT.

DO NOT SCALE THE DRAWINGS. USE ALL DIMENSIONS SHOWN. VERIFY ALL DIMENSIONS ON SITE & NOTIFY ARCHITECT OF ANY DISCREPANCIES.

No.	Date	Description

PROJECT NAME:
PIGNATELLI
RESIDENCE

11 SILVER HILL RD
WESTON, MA



DRAWING NAME:
EXTERIOR
ELEVATIONS

DATE:	03.16.2023
PROJECT NO:	21031
SCALE:	1/4" = 1'-0"
DRAWN & CHECKED BY:	JJ/CK

DRAWING NO:

A2.1



66 CENTRAL STREET STE. 2
WELLESLEY, MA 02482
(781) 431-7400
WWW.KRAUSAB.COM

ALL RIGHTS RESERVED. NO USE OR
REPRODUCTION OF THIS MATERIAL IS PERMITTED
WITHOUT WRITTEN CONSENT.


DO NOT SCALE THE DRAWINGS. USE ALL DIMENSIONS SHOWN. VERIFY ALL DIMENSIONS ON SITE & NOTIFY ARCHITECT OF ANY DISCREPANCIES.

[illegible]

PROJECT NAME:

PIGNATELLI RESIDENCE

11 SILVER HILL RD
WESTON, MA

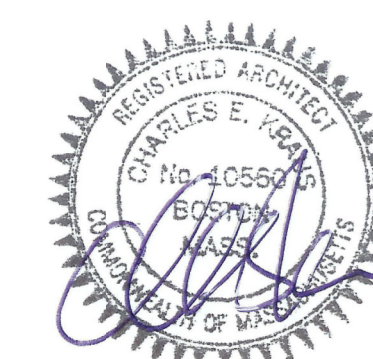

DRAWING NAME:


EXTERIOR ELEVATIONS

DATE:	03.16.2023
PROJECT NO:	21031
SCALE:	1/4" = 1'-0"
DRAWN & CHECKED BY:	JJ/CK


DRAWING NO:

A2.2


2023.03.16 - PROGRESS SET

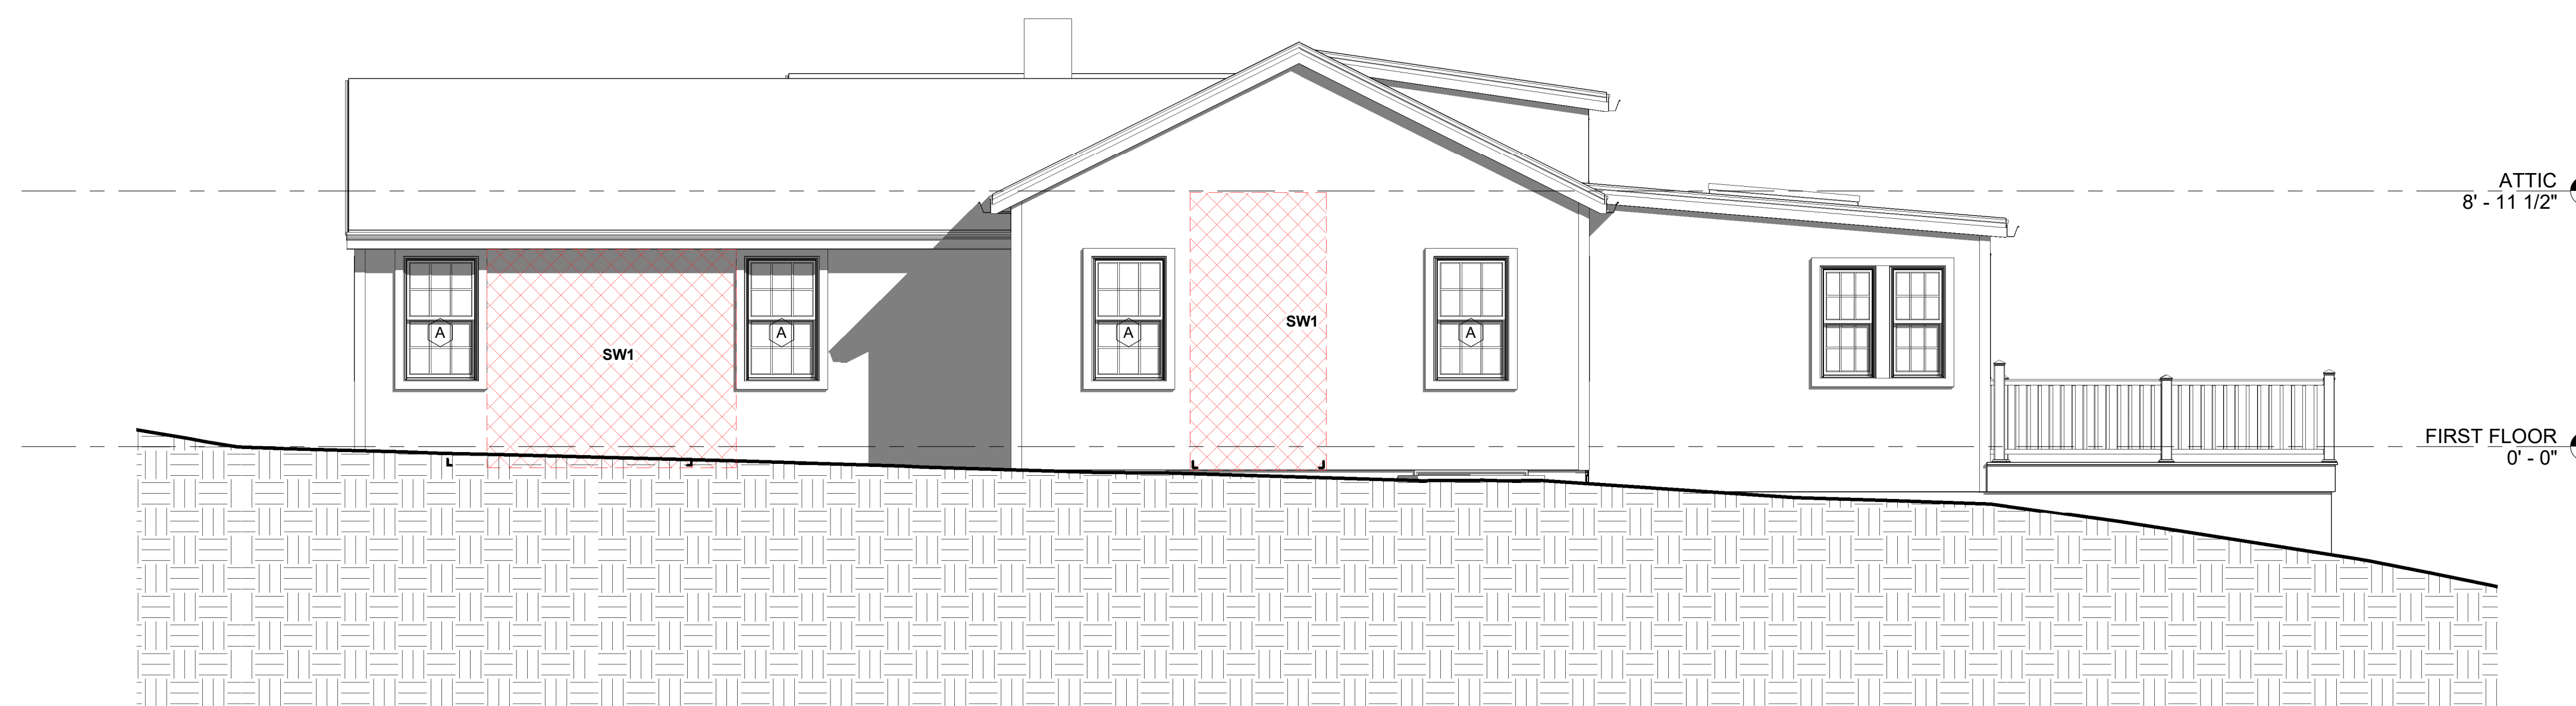

1 NORTH ELEVATION
1/4" = 1'-0"

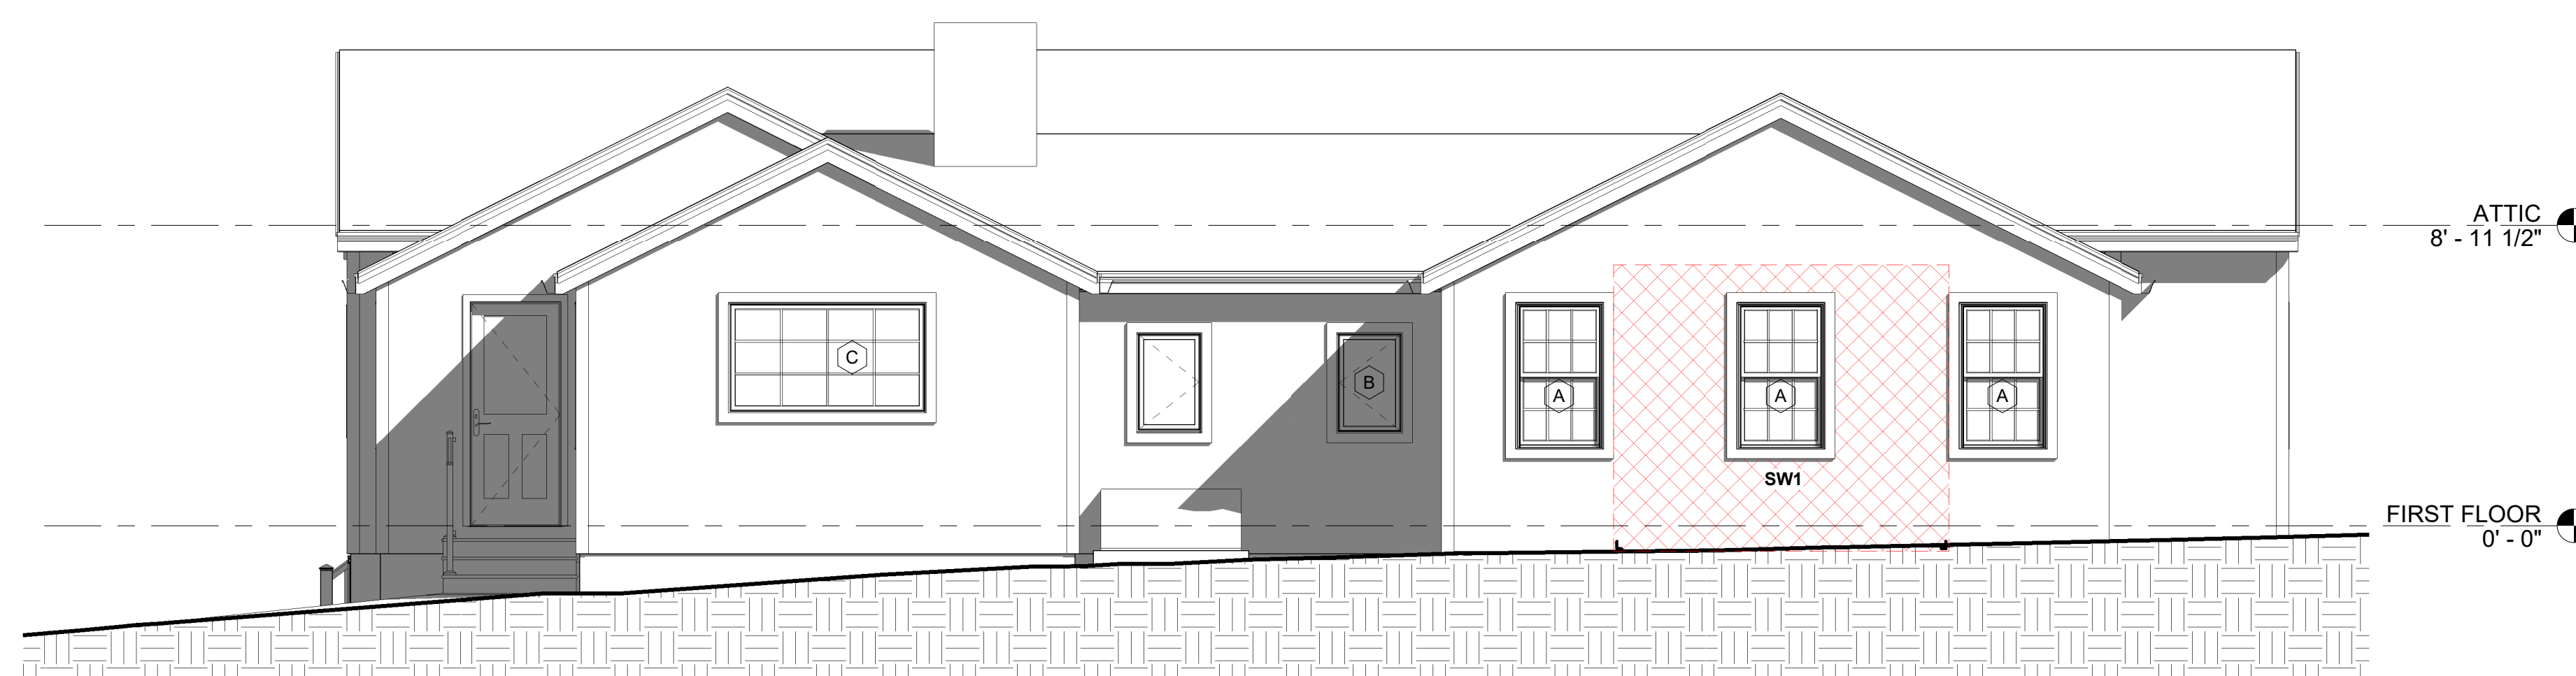

② EAST ELEVATION
1/4" = 1'-0"

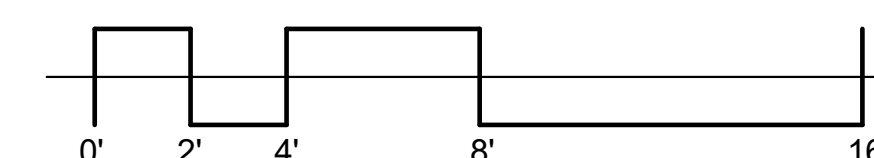



ALL RIGHTS RESERVED. NO USE OR
REPRODUCTION OF THIS MATERIAL IS PERMITTED
WITHOUT WRITTEN CONSENT.

DO NOT SCALE THE DRAWINGS. USE ALL
DIMENSIONS SHOWN. VERIFY ALL DIMENSIONS ON
SITE & NOTIFY ARCHITECT OF ANY
DISCREPANCIES.

[illegible]


PIGNATELLI
RESIDENCE

FIRST FLOOR FRAMING PLAN


DATE:	03.16.2023
PROJECT NO:	21031
SCALE:	1/4" = 1'-0"
DRAWN & CHECKED BY:	JJ/CK


A3.2

2023.03.16 - PROGRESS SET

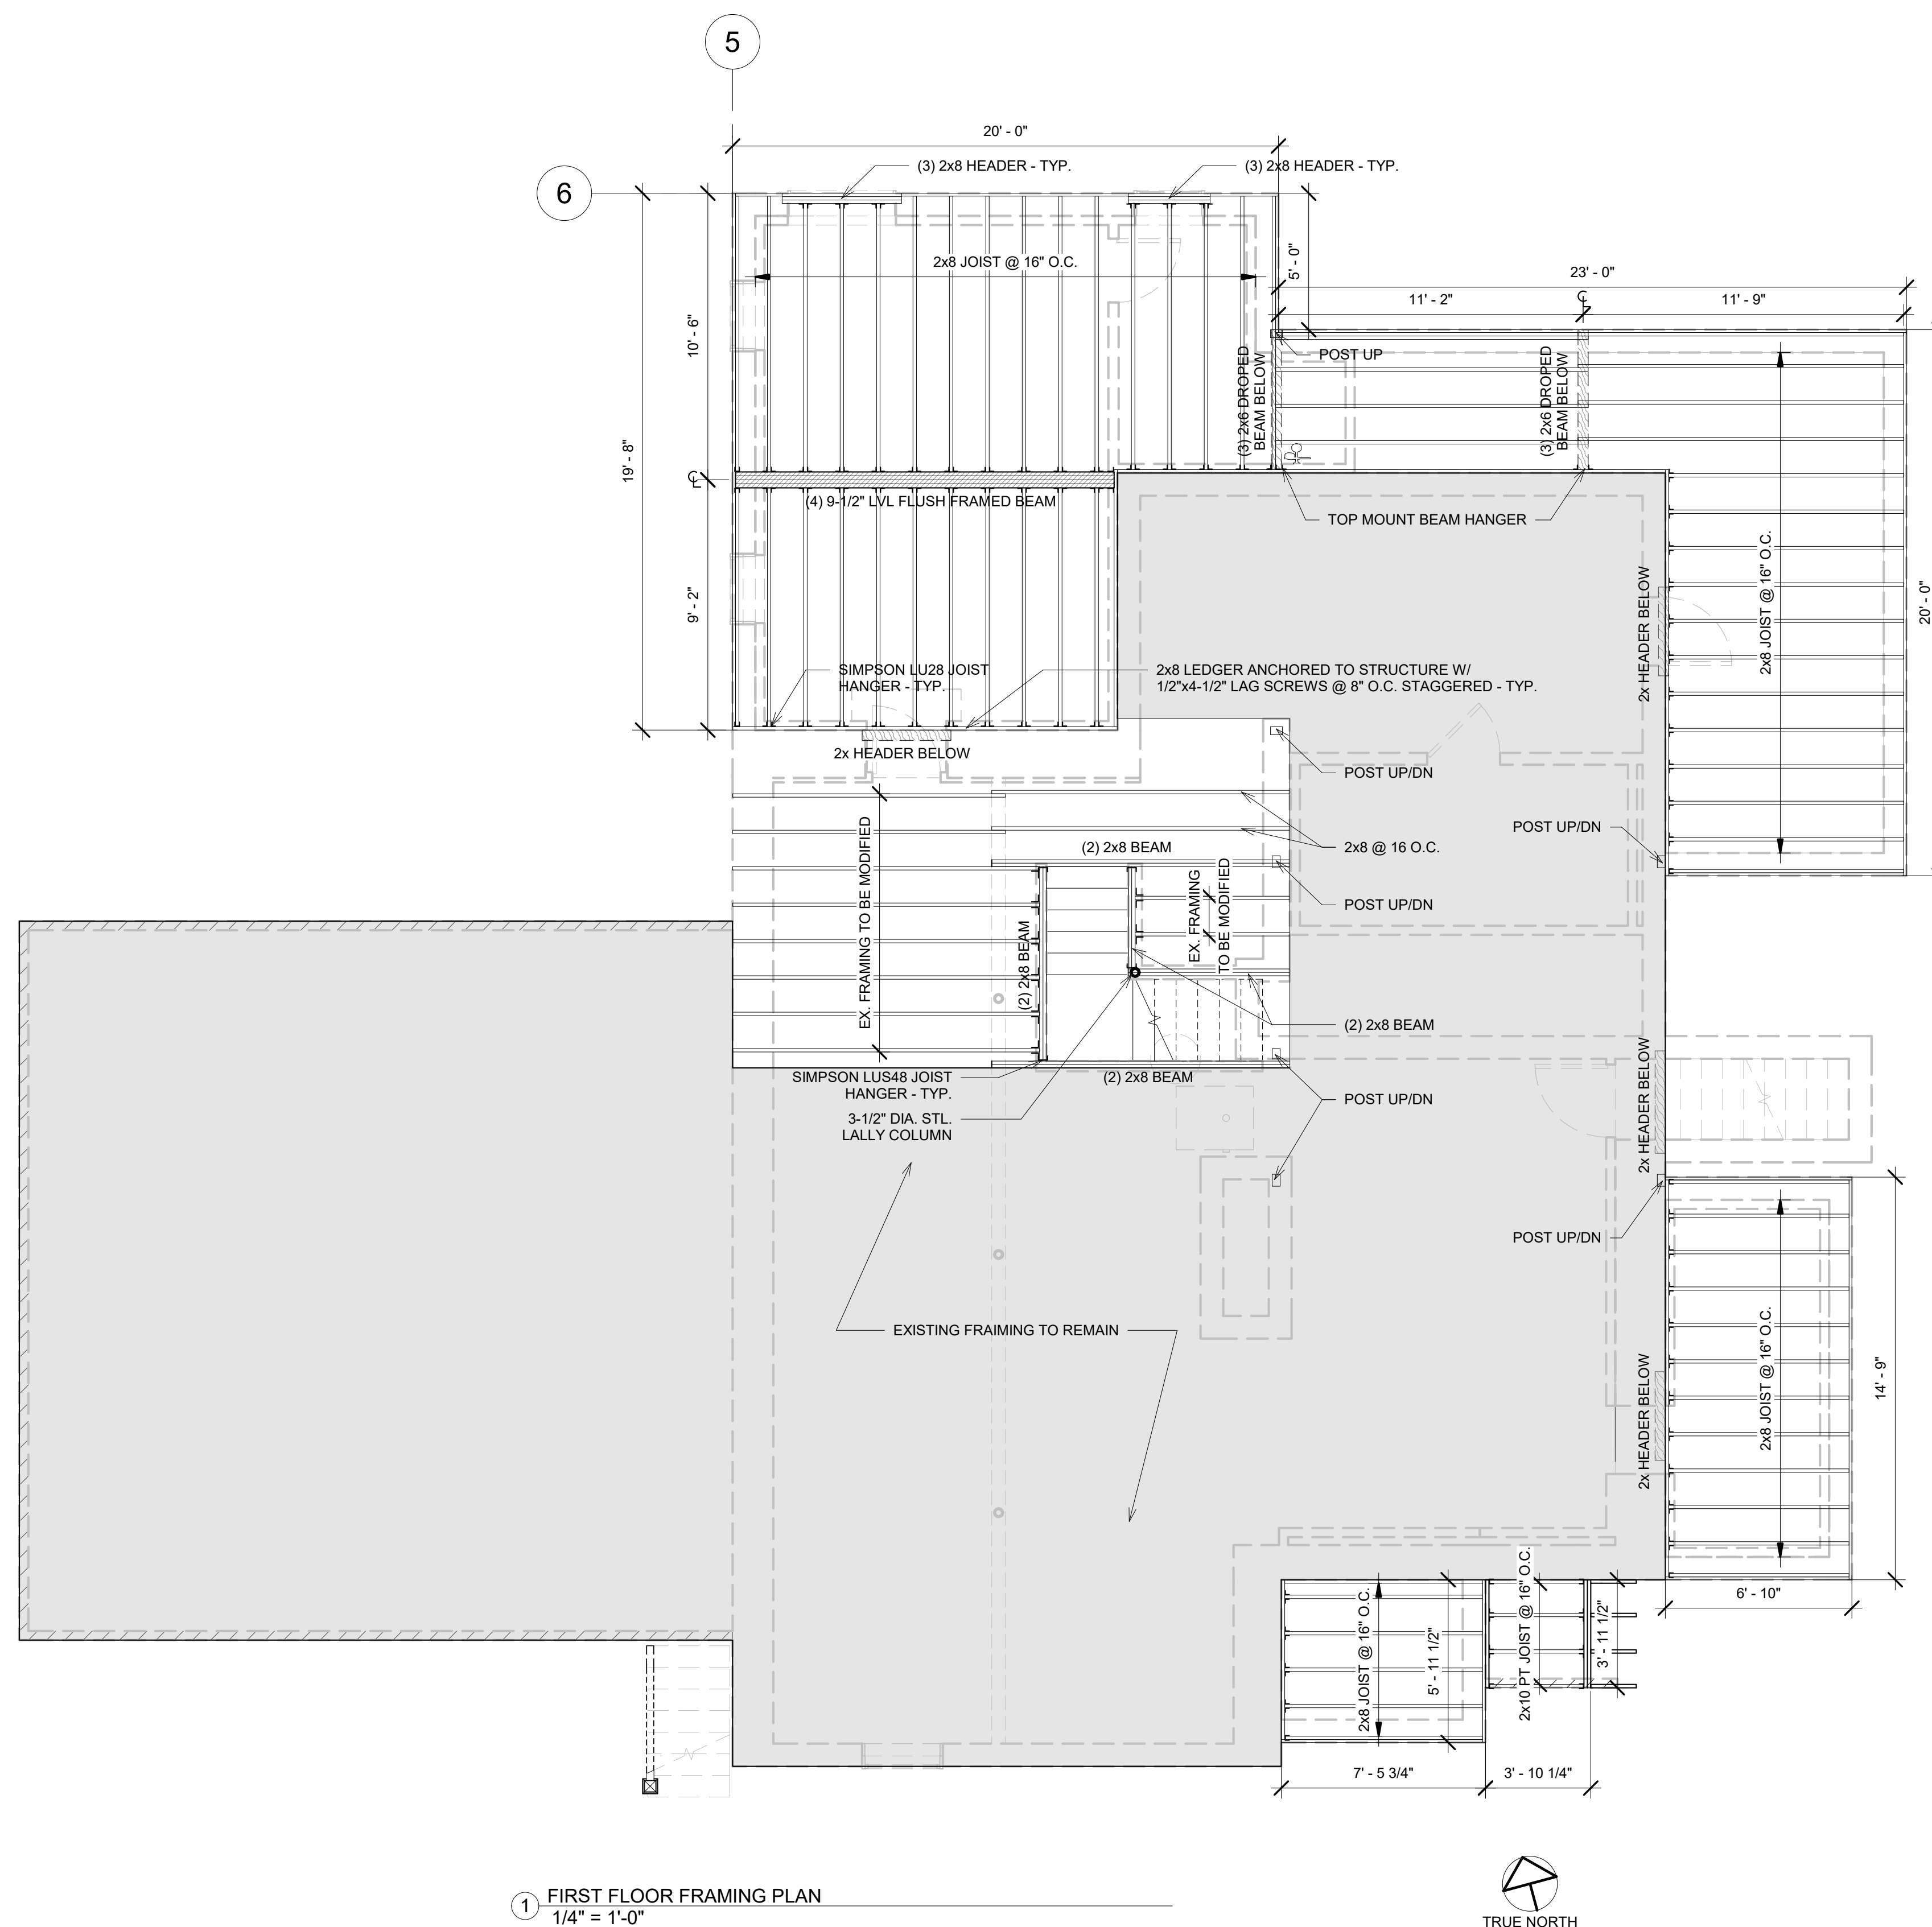


① FIRST FLOOR FRAMING PLAN
1/4" = 1'-0"

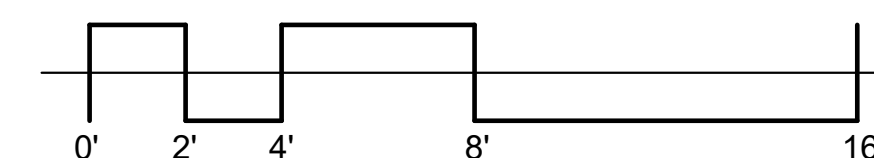

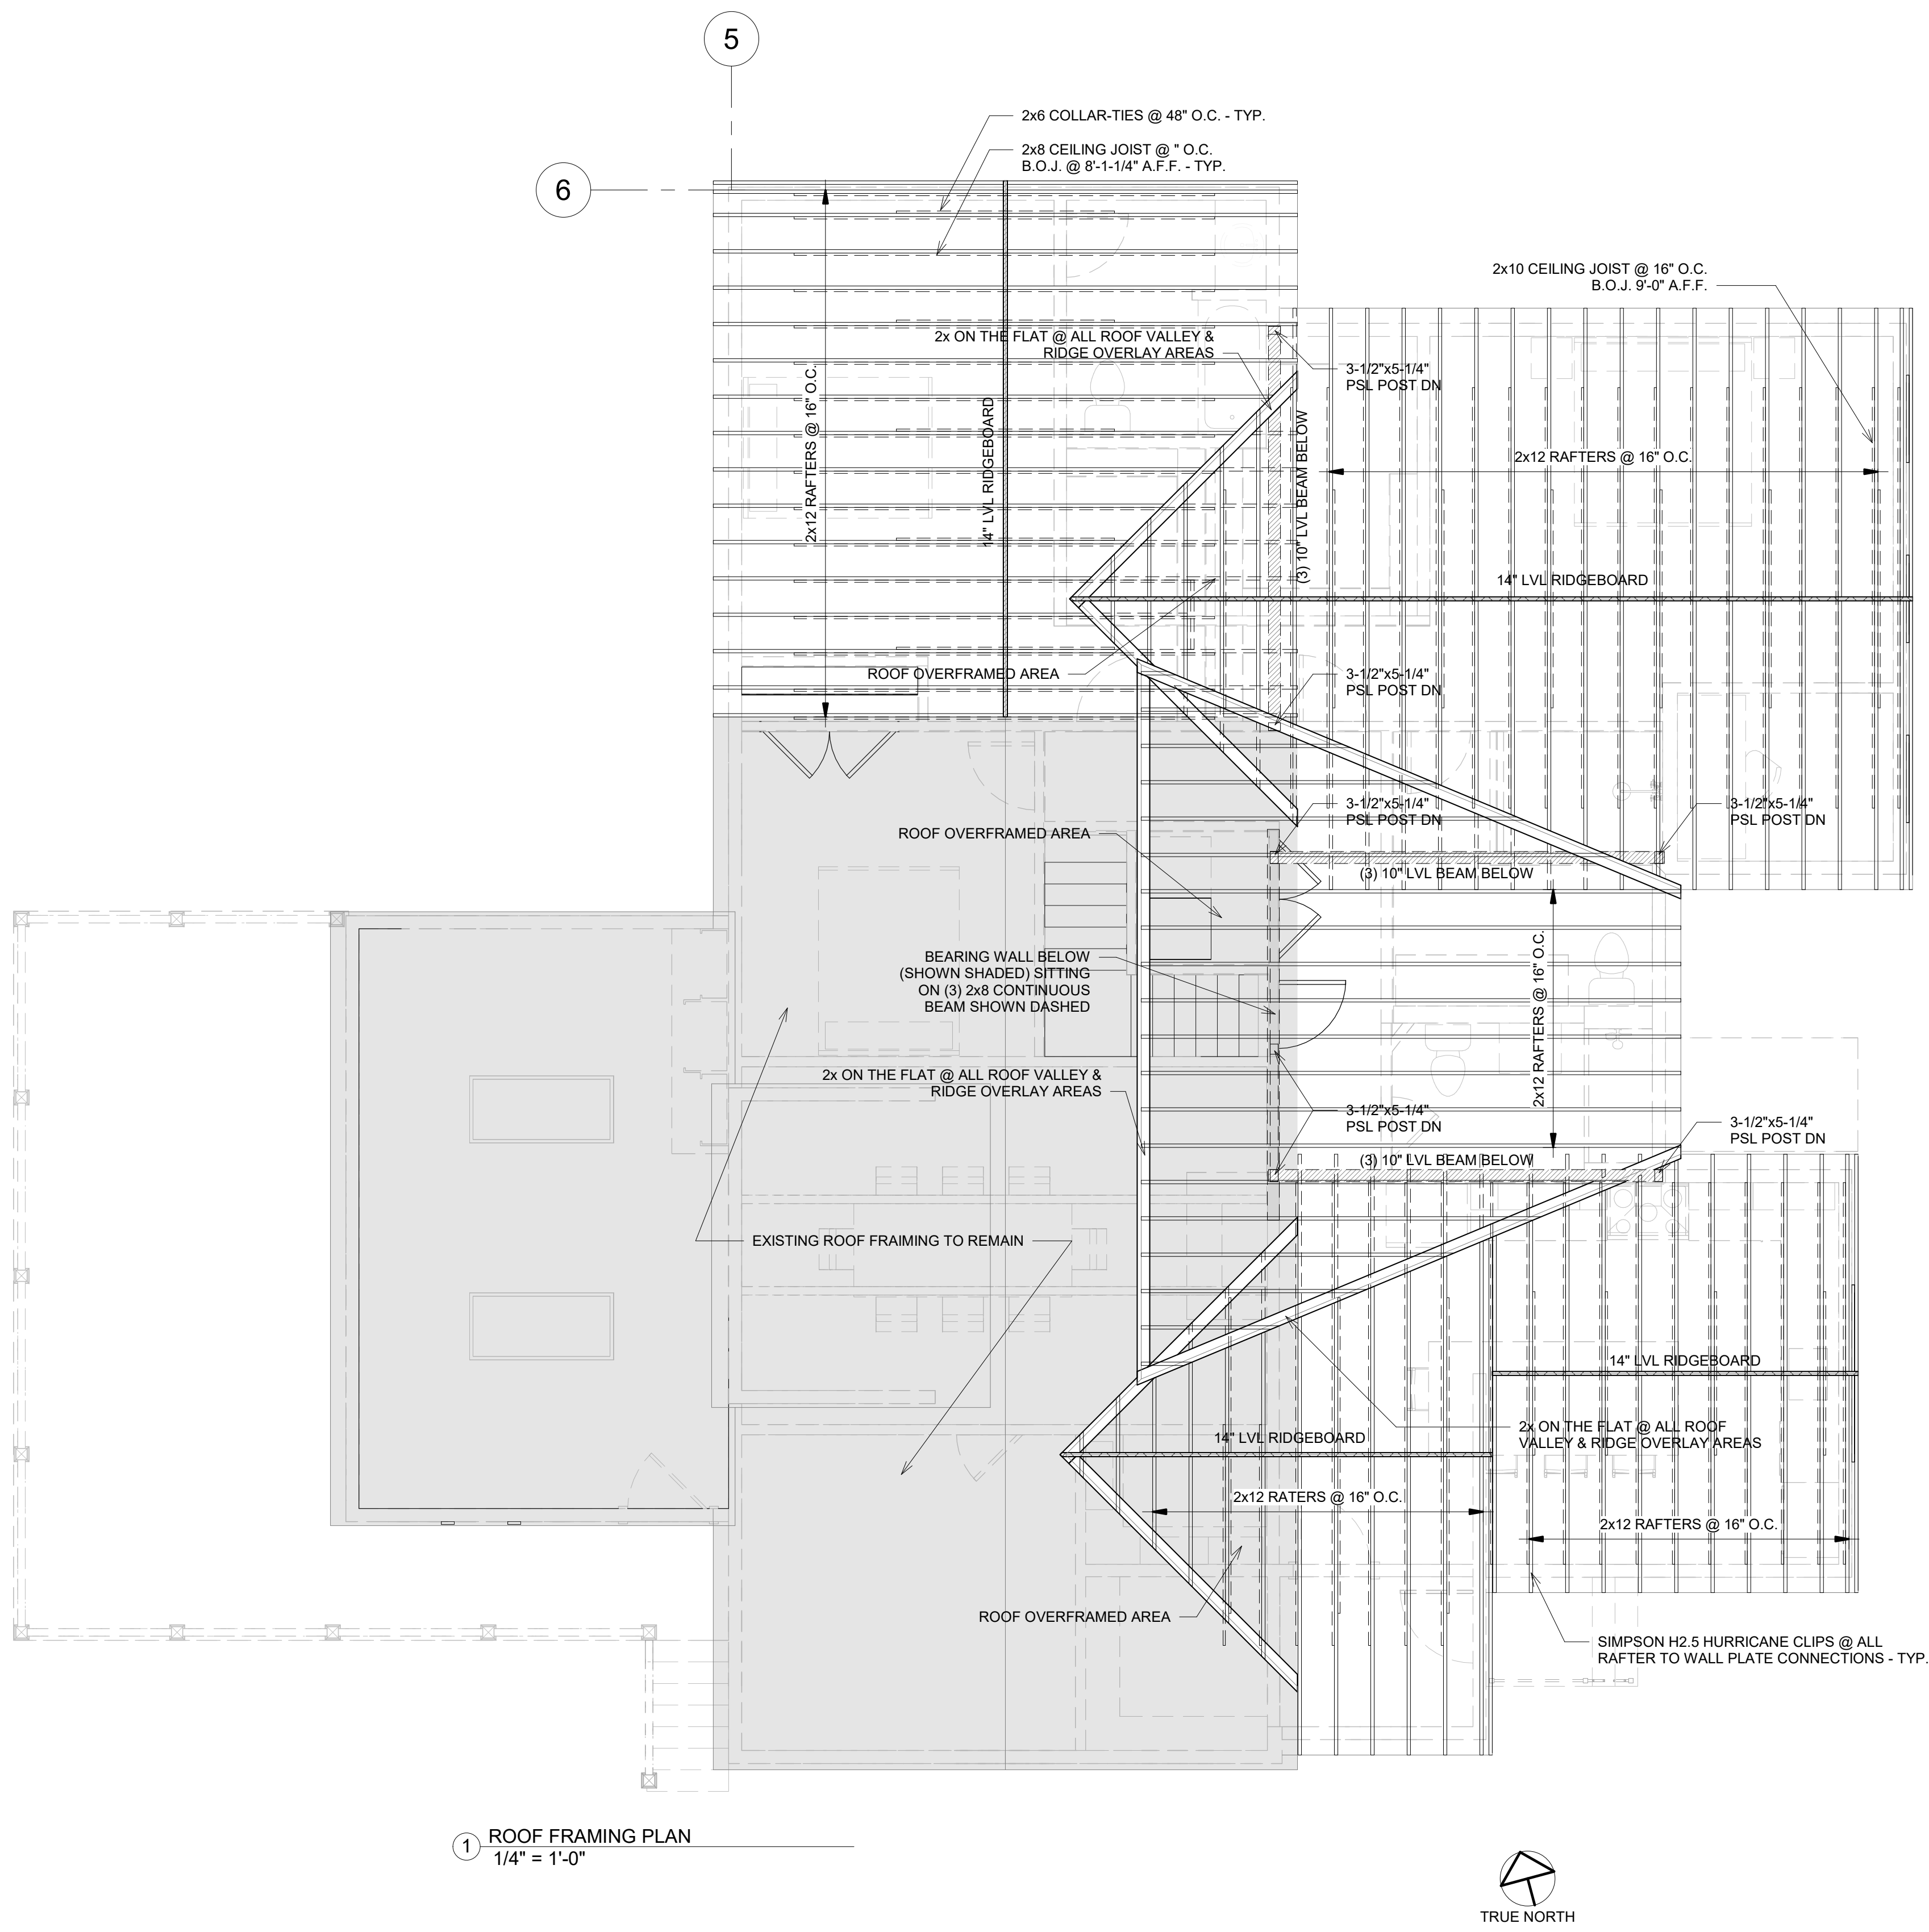

1 ROOF FRAMING PLAN
1/4" = 1'-0"

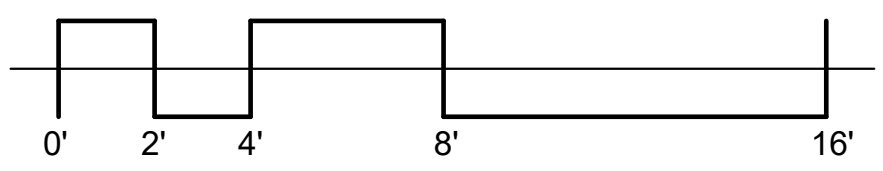

KRAUS ASSOCIATES

66 CENTRAL STREET STE. 2
WELLESLEY, MA 02482
(781) 431-7400
WWW.KRAUSAB.COM


ALL RIGHTS RESERVED. NO USE OR REPRODUCTION OF THIS MATERIAL IS PERMITTED WITHOUT WRITTEN CONSENT.

DO NOT SCALE THE DRAWINGS. USE ALL DIMENSIONS SHOWN. VERIFY ALL DIMENSIONS ON SITE & NOTIFY ARCHITECT OF ANY DISCREPANCIES.

No.	Date	Description

PROJECT NAME:
PIGNATELLI RESIDENCE

**11 SILVER HILL RD
WESTON, MA**

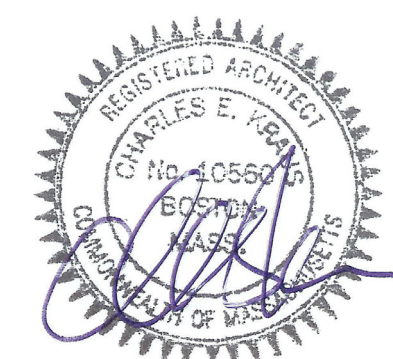


DRAWING NAME:
ROOF FRAMING PLAN

DATE:	03.16.2023
PROJECT NO:	21031
SCALE:	1/4" = 1'-0"
DRAWN & CHECKED BY:	JJ/CK
DRAWING NO:	


A3.3

2023.03.16 - PROGRESS SET

	6" RECESSED LED CAN LIGHT - PROVIDE ALLOWANCE
	4" RECESSED LED CAN LIGHT - PROVIDE ALLOWANCE
	WALL MOUNTED FIXTURE - PROVIDE ALLOWANCE
	WALL MOUNTED LIGHT FIXTURE - PROVIDE ALLOWANCE
	EXTERIOR WALL MOUNTED FIXTURE - PROVIDE ALLOWANCE
	LED STRIP LIGHT - PROVIDE ALLOWANCE
	SURFACE MOUNTED CEILING FIXTURE - PROVIDE ALLOWANCE
	PENDANT MOUNTED LIGHT FIXTURE - PROVIDE ALLOWANCE
	LINE VOLTAGE LED UNDER-CABINET LIGHT - PROVIDE ALLOWANCE
	CABLE TV & POWER RECEPTACLE HIGH & LOW ON WALL
	SWITCH
	DRYER/RANGE/WALL OVEN OUTLET
	SINGLE DUPLEX OUTLET
	SINGLE SWITCHED DUPLEX OUTLET
	BATHROOM EXHAUST FAN - PROVIDE ALLOWANCE
	SMOKE DETECTOR
	COMBINATION SMOKE/CARBON DIOXIDE DETECTOR

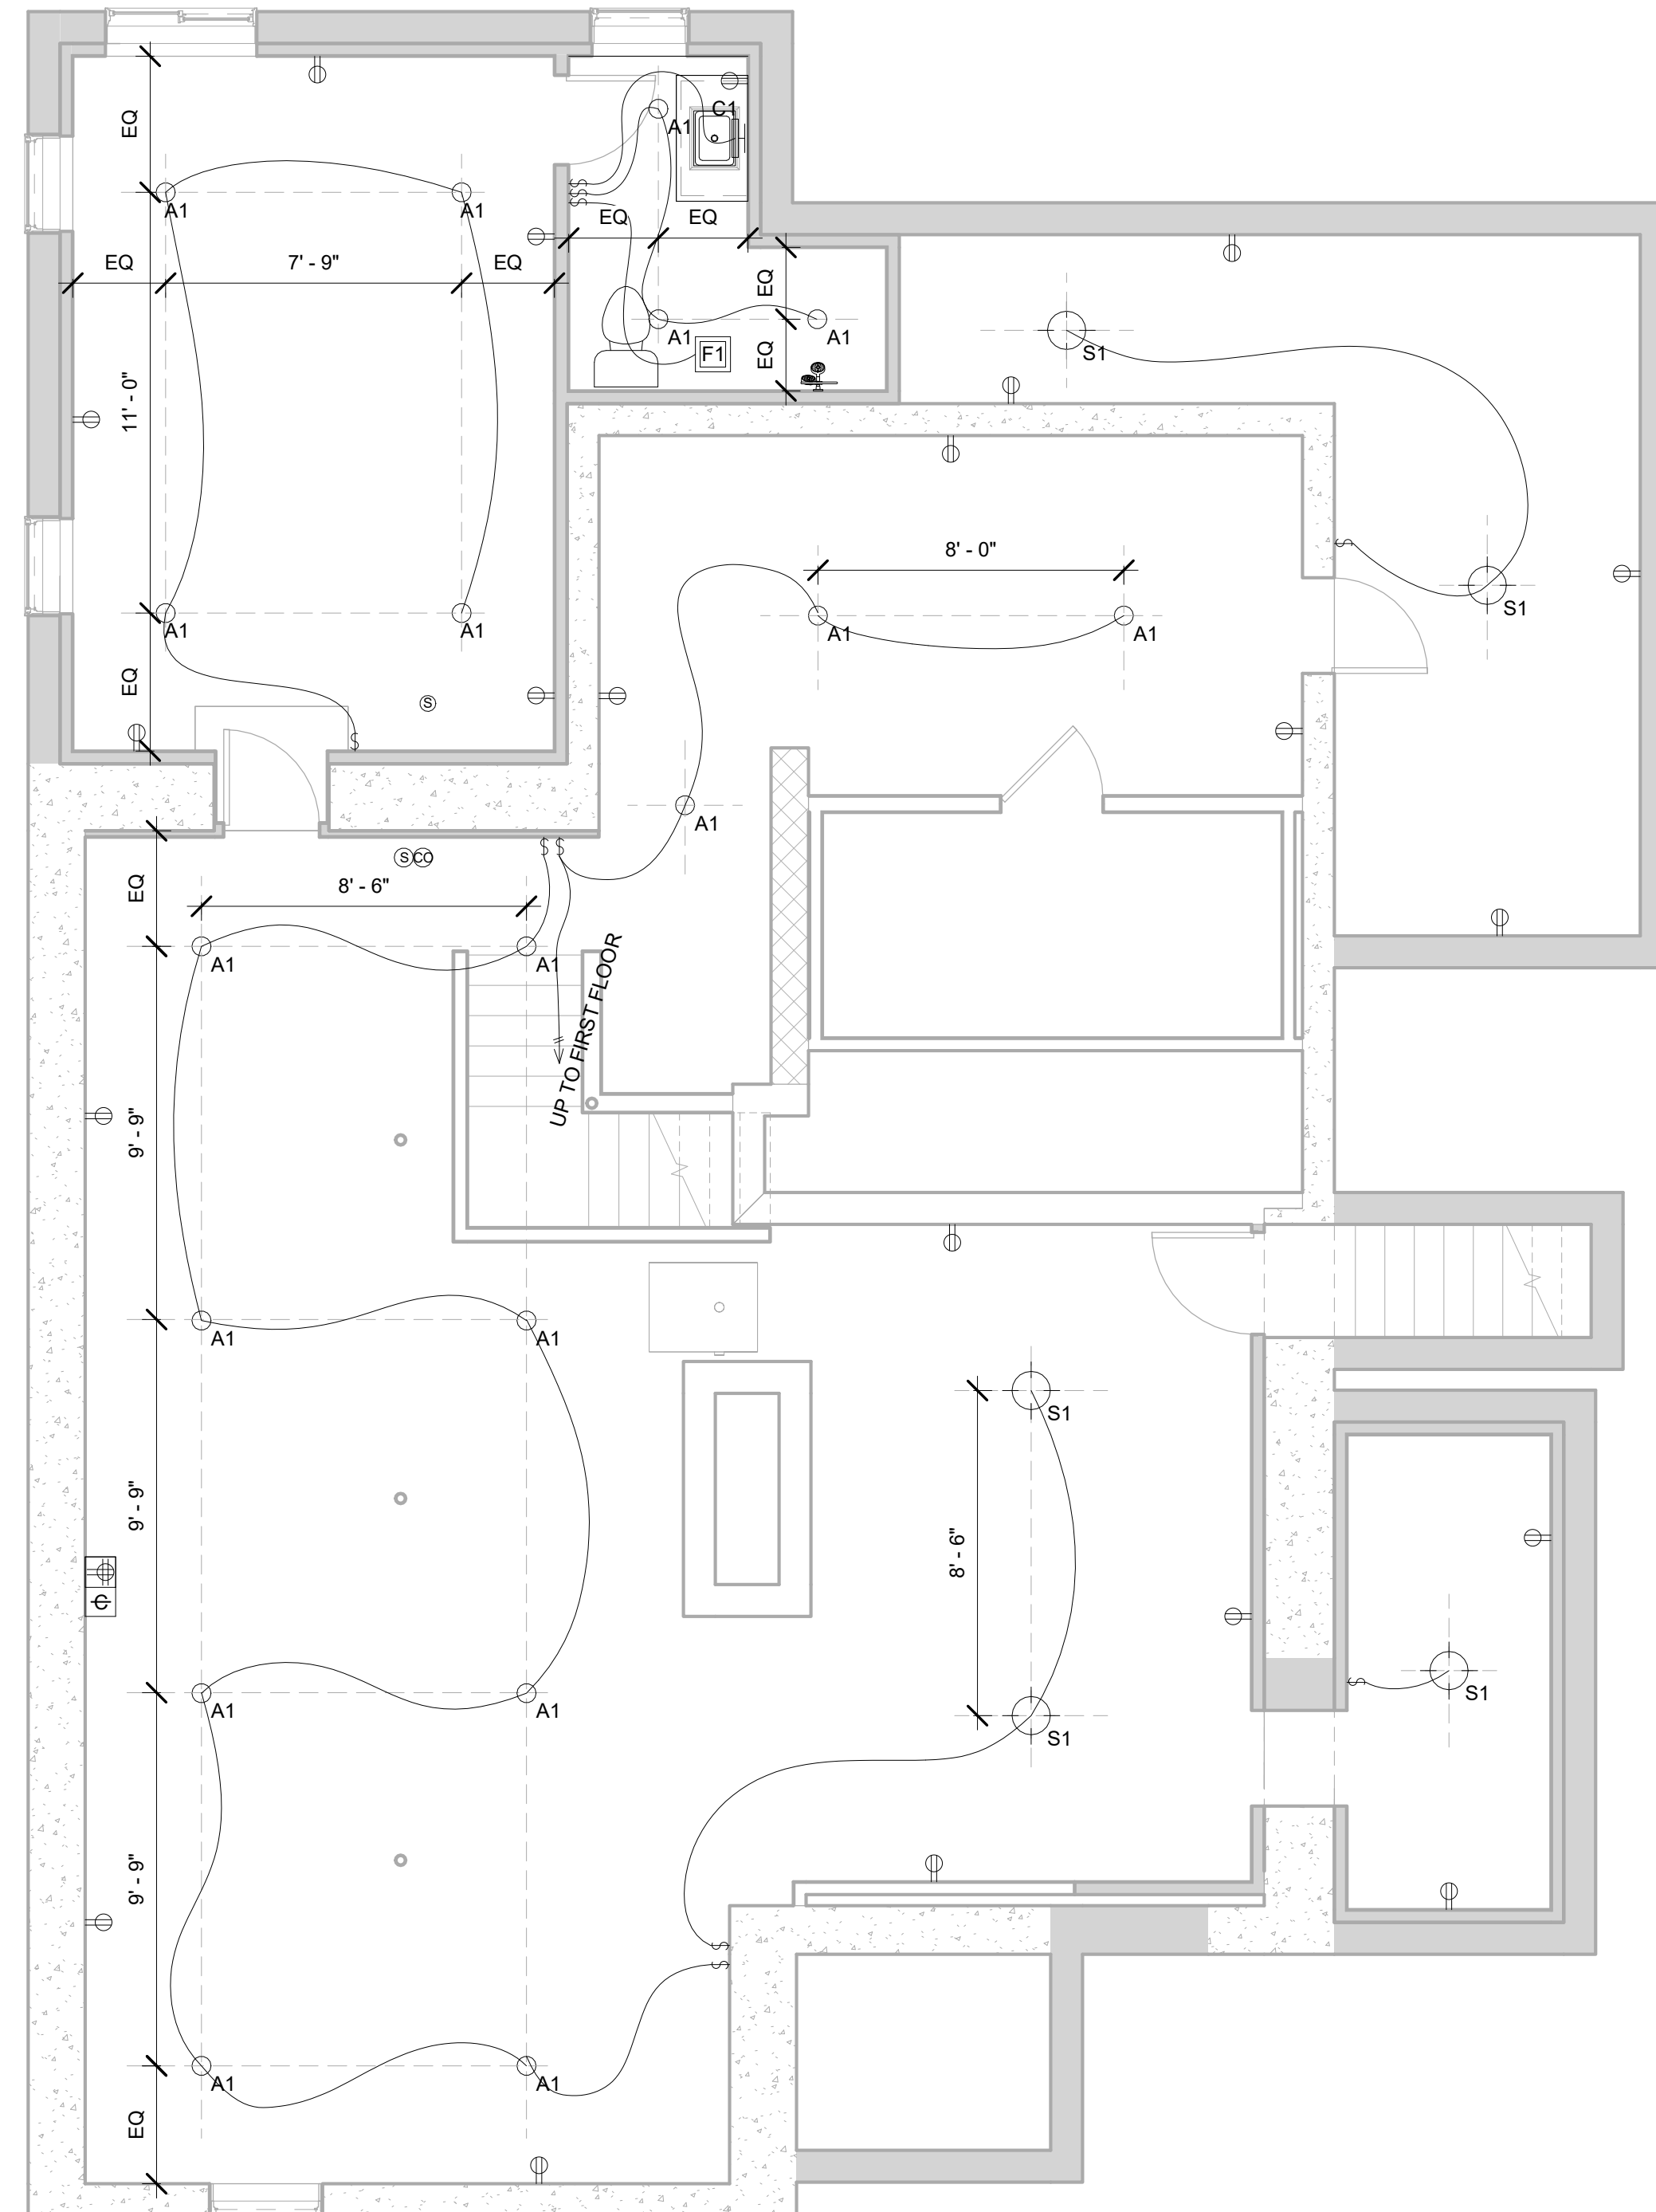

1 BASEMENT REFLECTED CEILING PLAN
1/4" = 1'-0"

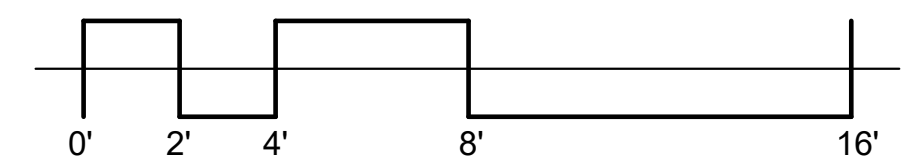

66 CENTRAL STREET STE. 2
WELLESLEY, MA 02482
(781) 431-7400
WWW.KRAUSAB.COM

ALL RIGHTS RESERVED. NO USE OR REPRODUCTION OF THIS MATERIAL IS PERMITTED WITHOUT WRITTEN CONSENT.


DO NOT SCALE THE DRAWINGS. USE ALL
DIMENSIONS SHOWN. VERIFY ALL DIMENSIONS ON
SITE & NOTIFY ARCHITECT OF ANY
DISCREPANCIES.

[illegible]

PROJECT NAME:

PIGNATELLI RESIDENCE

11 SILVER HILL RD
WESTON, MA

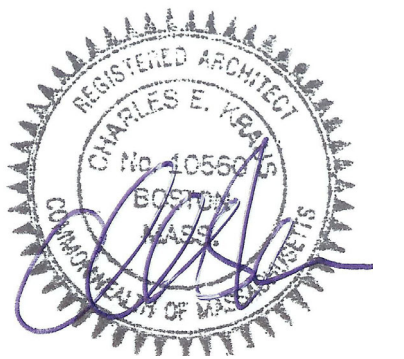

DRAWING NAME:


BASEMENT REFLECTED CEILING PLAN

DATE:	03.16.2023
PROJECT NO:	21031
SCALE:	1/4" = 1'-0"
DRAWN & CHECKED BY:	JJ/CK
DRAWING NO:	


A4.1

2023.03.16 - PROGRESS SET

	6" RECESSED LED CAN LIGHT - PROVIDE ALLOWANCE
	4" RECESSED LED CAN LIGHT - PROVIDE ALLOWANCE
	WALL MOUNTED FIXTURE - PROVIDE ALLOWANCE
	WALL MOUNTED LIGHT FIXTURE - PROVIDE ALLOWANCE
	EXTERIOR WALL MOUNTED FIXTURE - PROVIDE ALLOWANCE
	LED STRIP LIGHT - PROVIDE ALLOWANCE
	SURFACE MOUNTED CEILING FIXTURE - PROVIDE ALLOWANCE
	PENDANT MOUNTED LIGHT FIXTURE - PROVIDE ALLOWANCE
	LINE VOLTAGE LED UNDER-CABINET LIGHT - PROVIDE ALLOWANCE
	CABLE TV & POWER RECEPTACLE HIGH & LOW ON WALL
	SWITCH
	DRYER/RANGE/WALL OVEN OUTLET
	SINGLE DUPLEX OUTLET
	SINGLE SWITCHED DUPLEX OUTLET
	BATHROOM EXHAUST FAN - PROVIDE ALLOWANCE
	SMOKE DETECTOR
	COMBINATION SMOKE/CARBON DIOXIDE DETECTOR

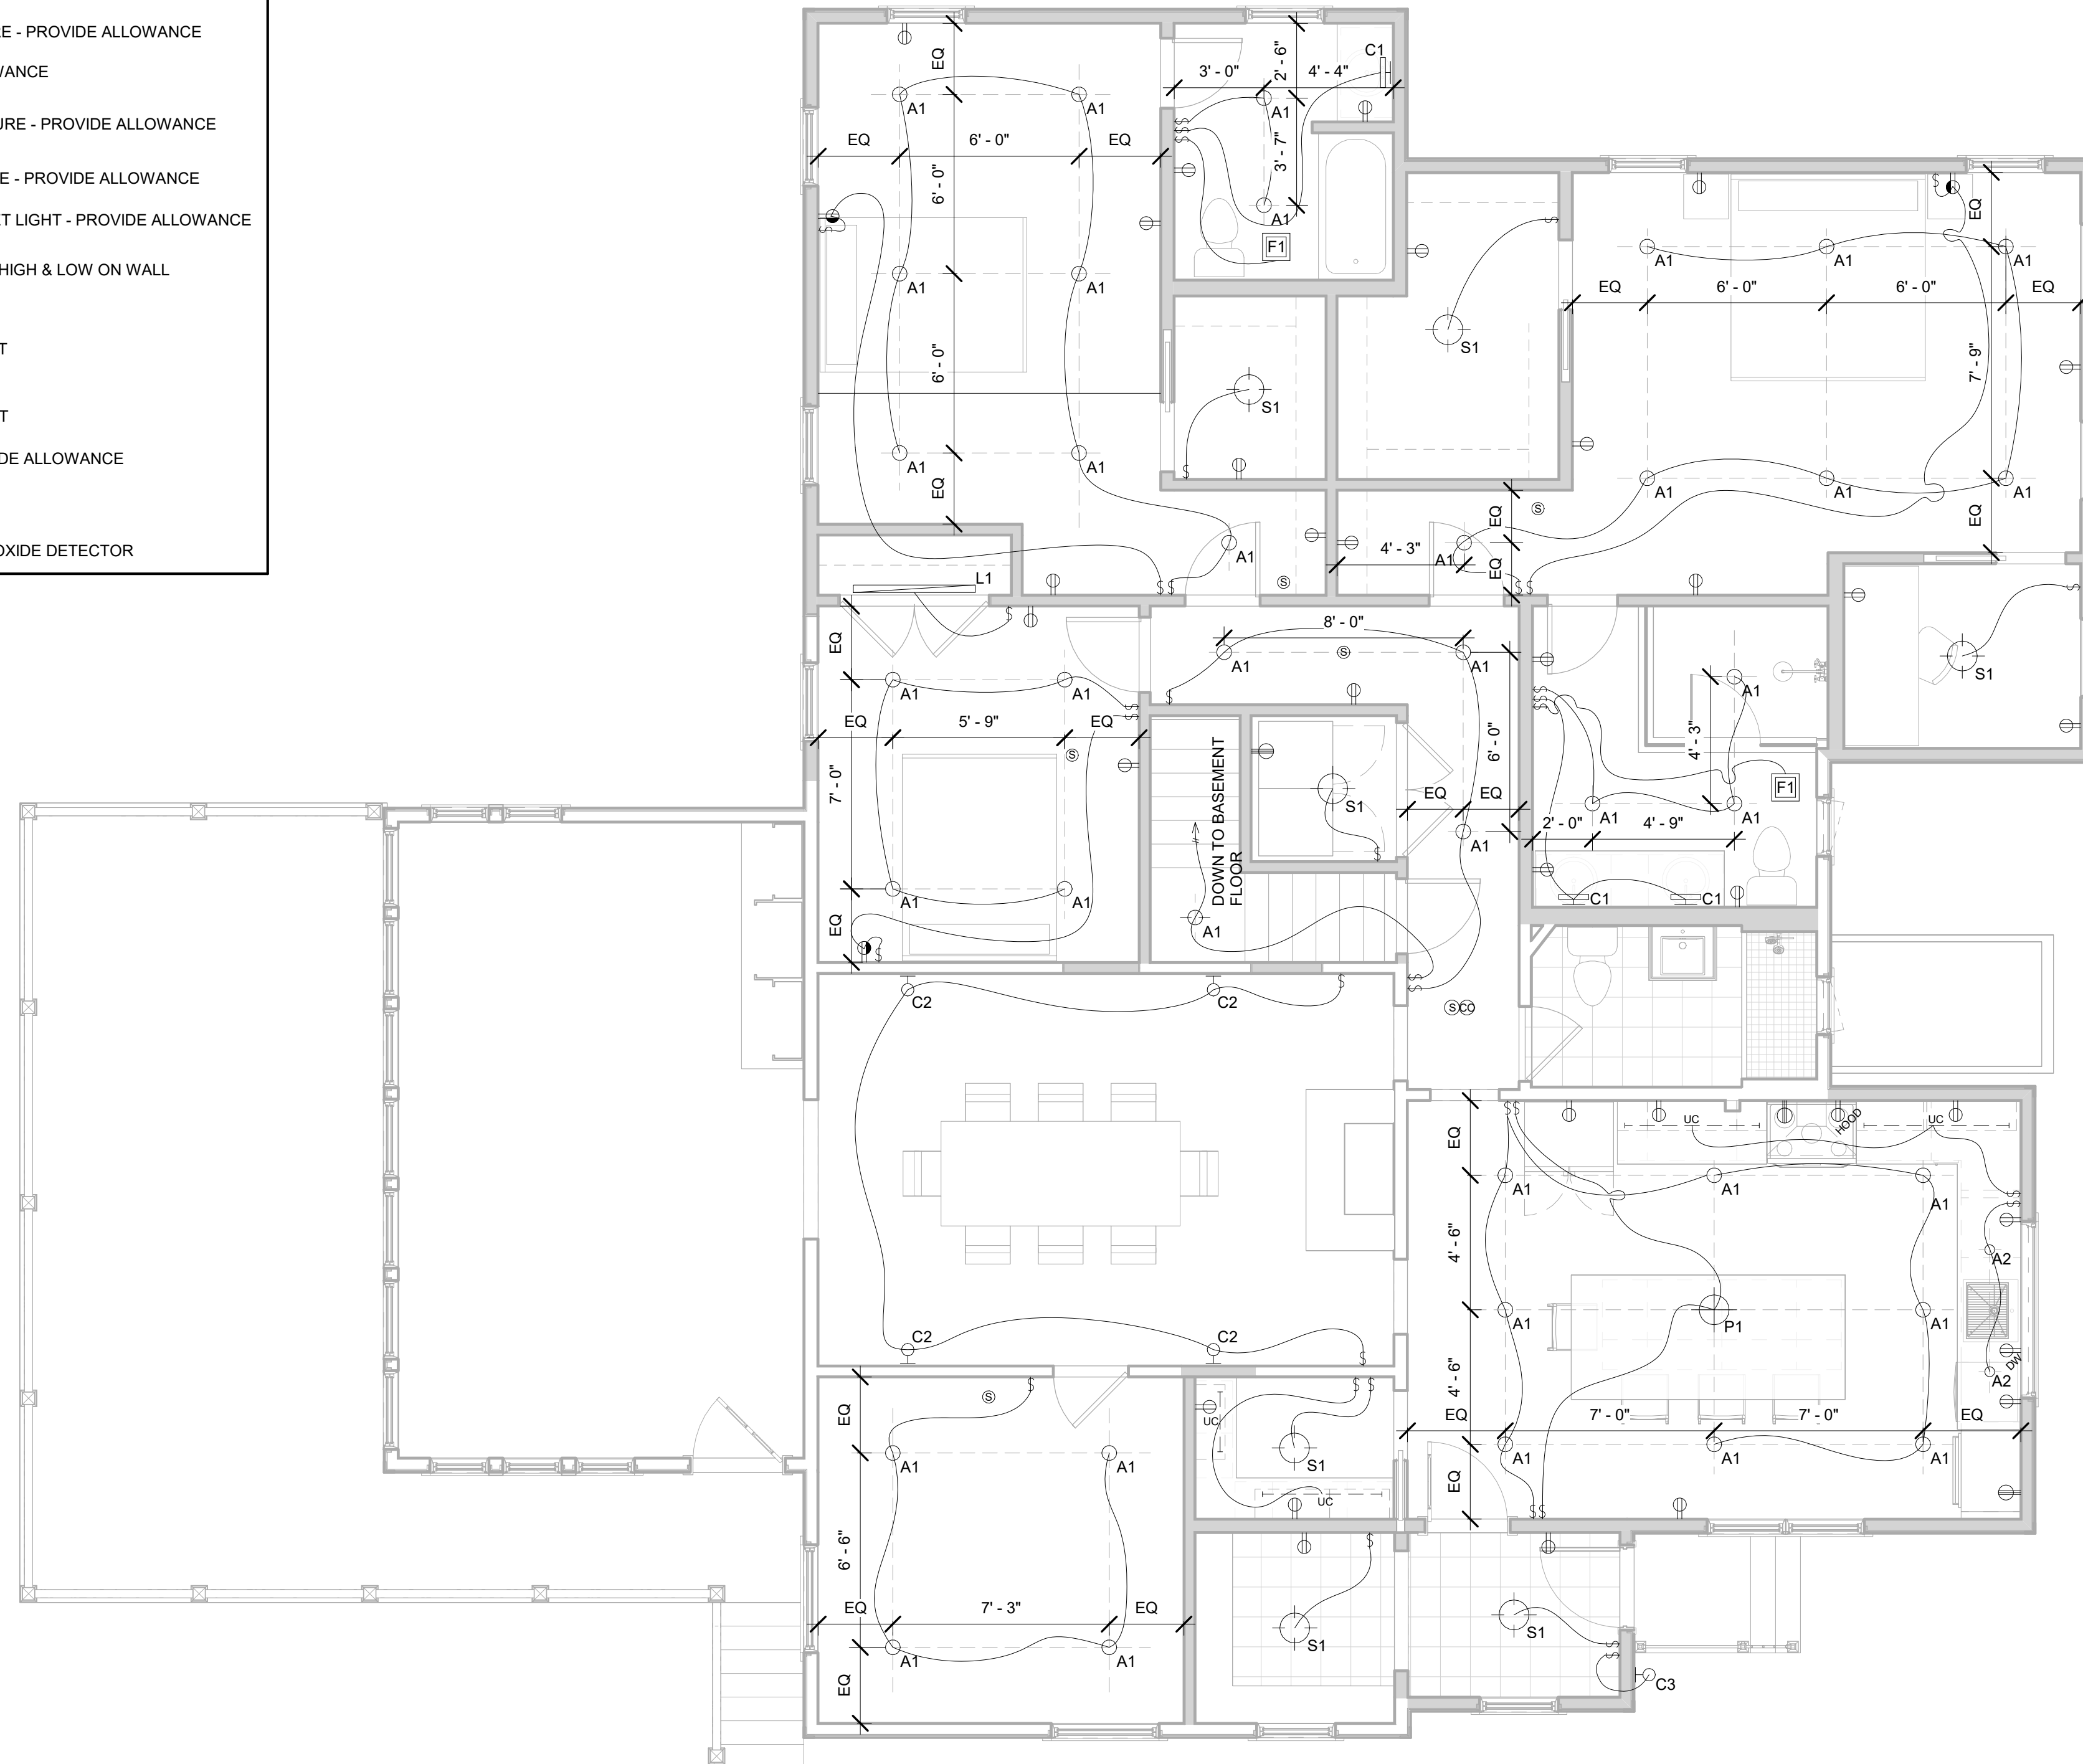

1 FIRST FLOOR REFLECTED CEILING
PLAN
1/4" = 1'-0"

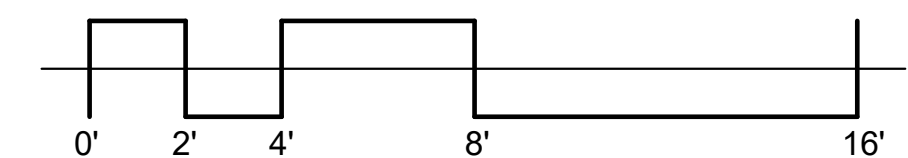

66 CENTRAL STREET STE. 2
WELLESLEY, MA 02482
(781) 431-7400
WWW.KRAUSAB.COM

ALL RIGHTS RESERVED. NO USE OR
REPRODUCTION OF THIS MATERIAL IS PERMITTED
WITHOUT WRITTEN CONSENT.

DO NOT SCALE THE DRAWINGS. USE ALL
DIMENSIONS SHOWN. VERIFY ALL DIMENSIONS ON
SITE & NOTIFY ARCHITECT OF ANY
DISCREPANCIES.

[illegible]

PROJECT NAME:

PIGNATELLI RESIDENCE

11 SILVER HILL RD
WESTON, MA



DRAWING NAME:

FIRST FLOOR REFLECTED CEILING PLAN

DATE:	03.16.2023
PROJECT NO:	21031
SCALE:	1/4" = 1'-0"
DRAWN & CHECKED BY:	JJ/CK
DRAWING NO:	

A4.2

2023.03.16 - PROGRESS SET