

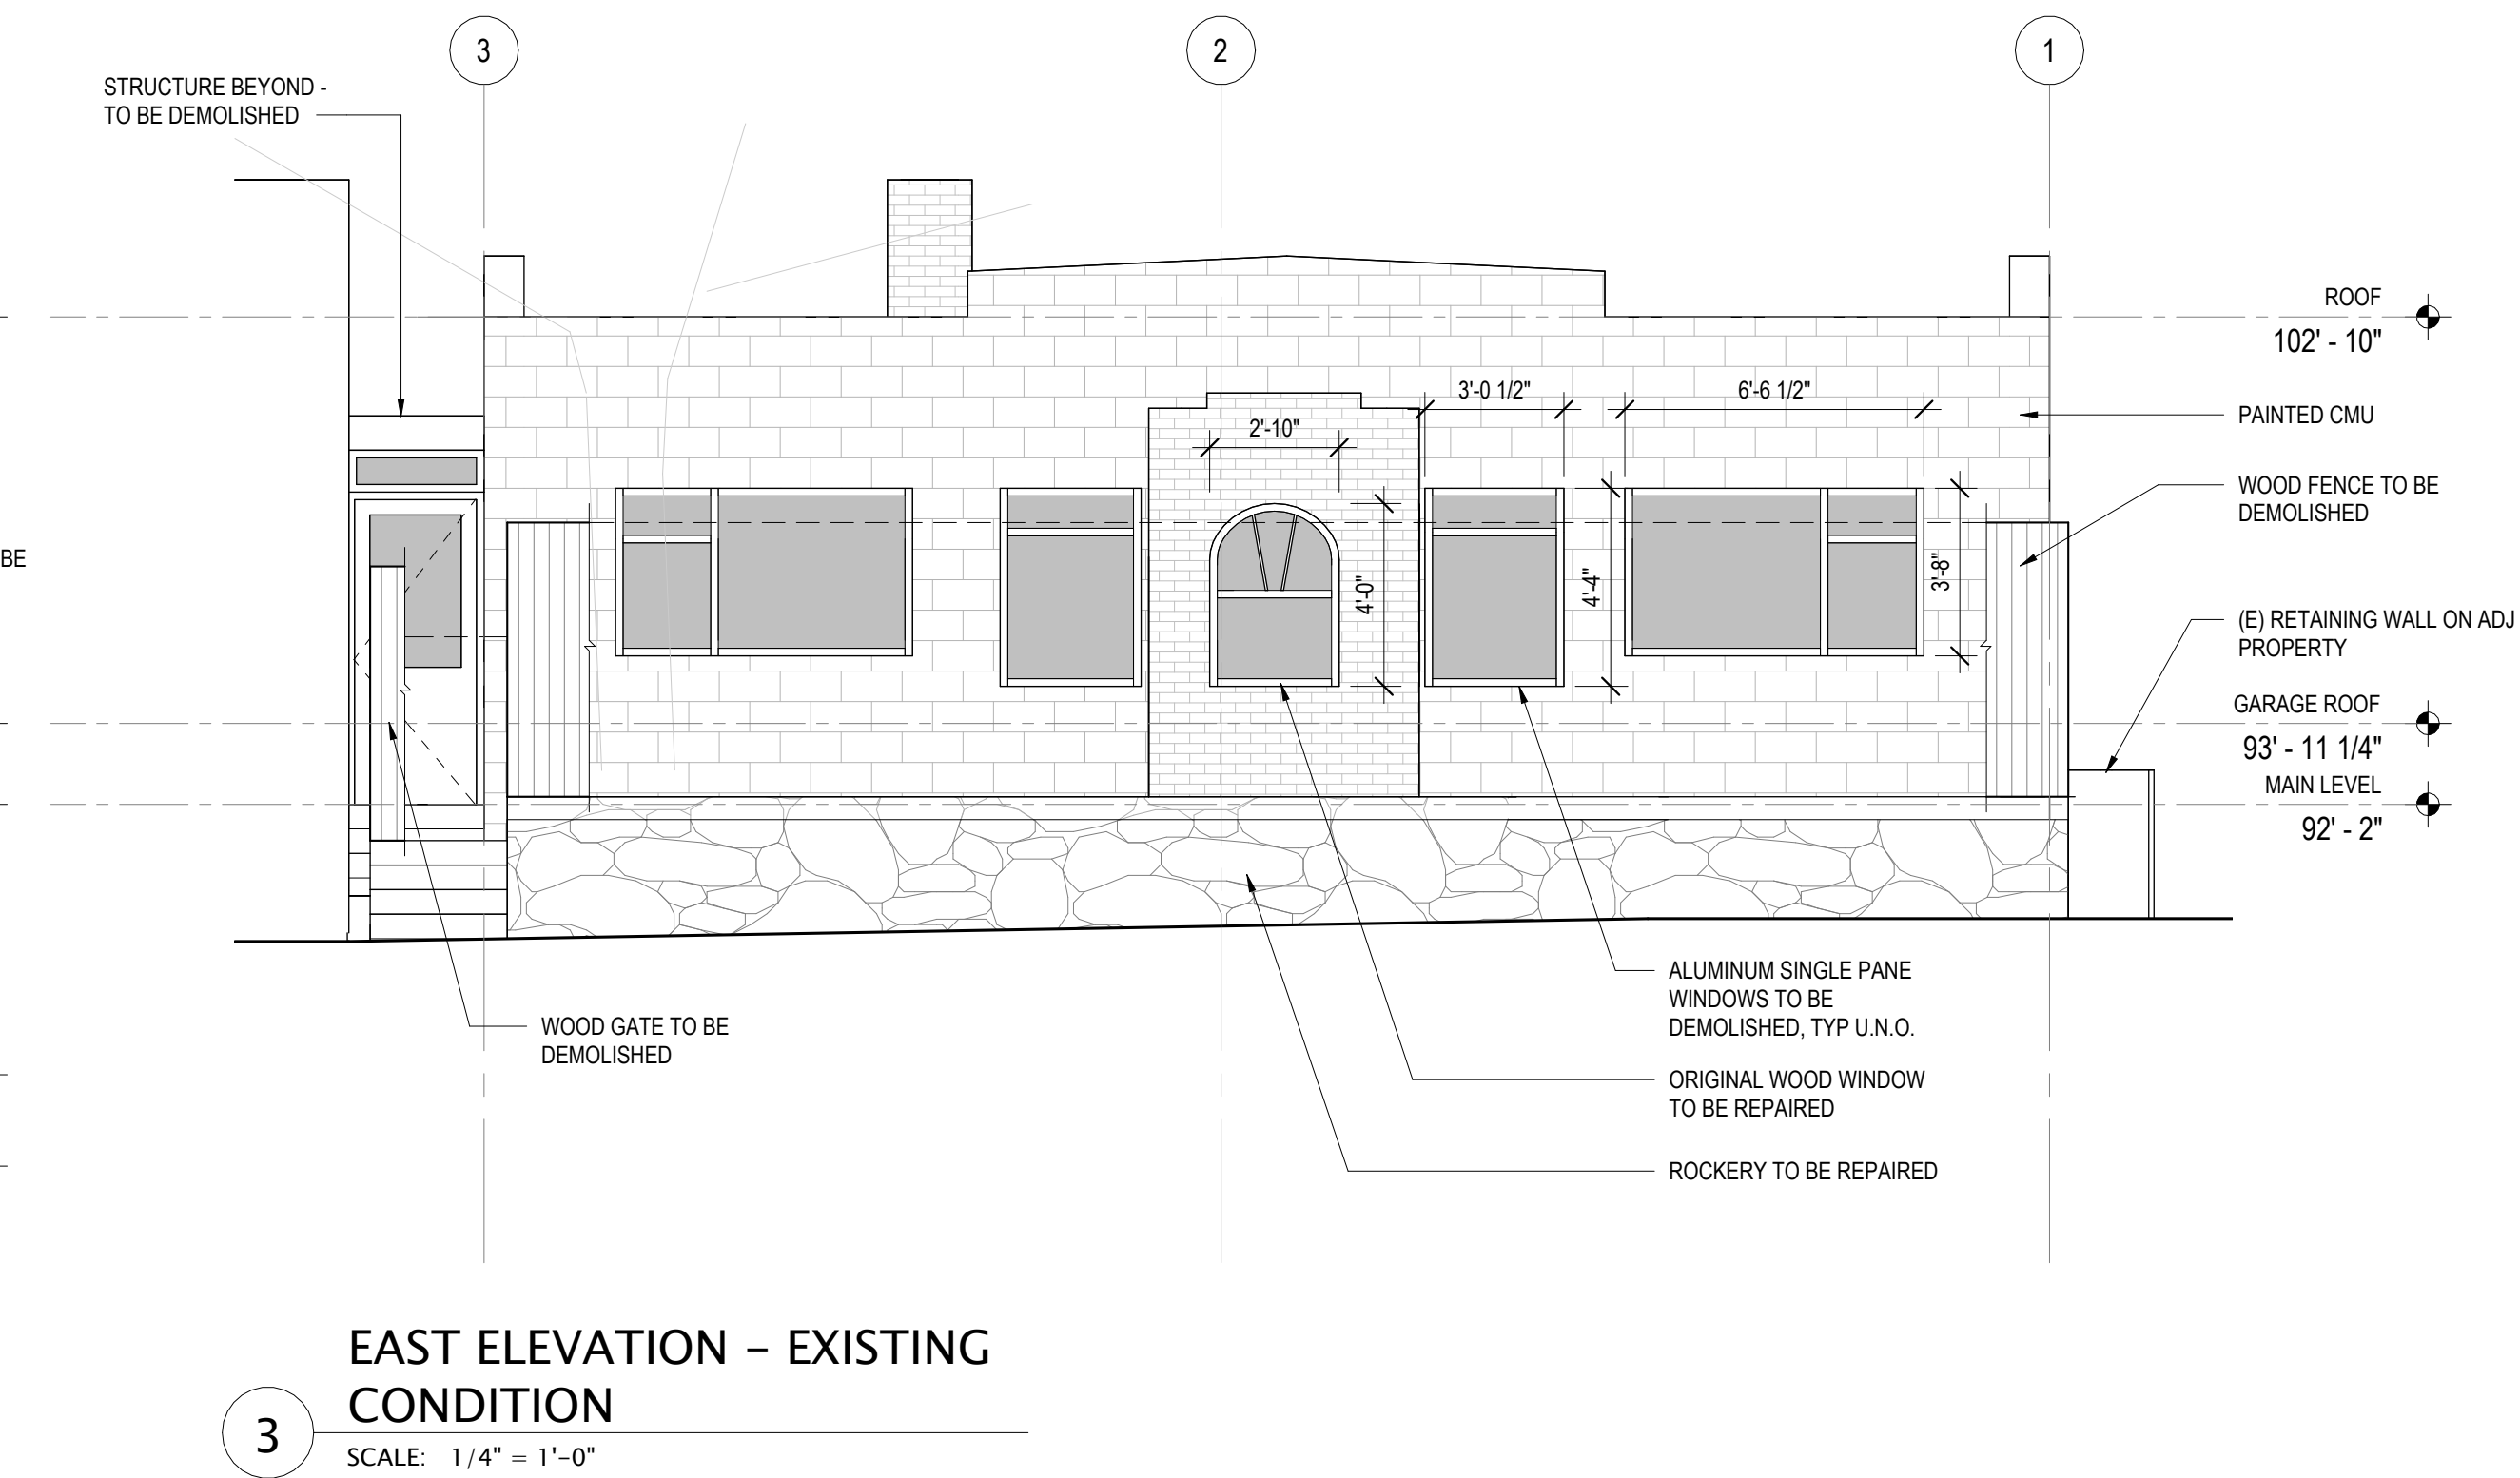
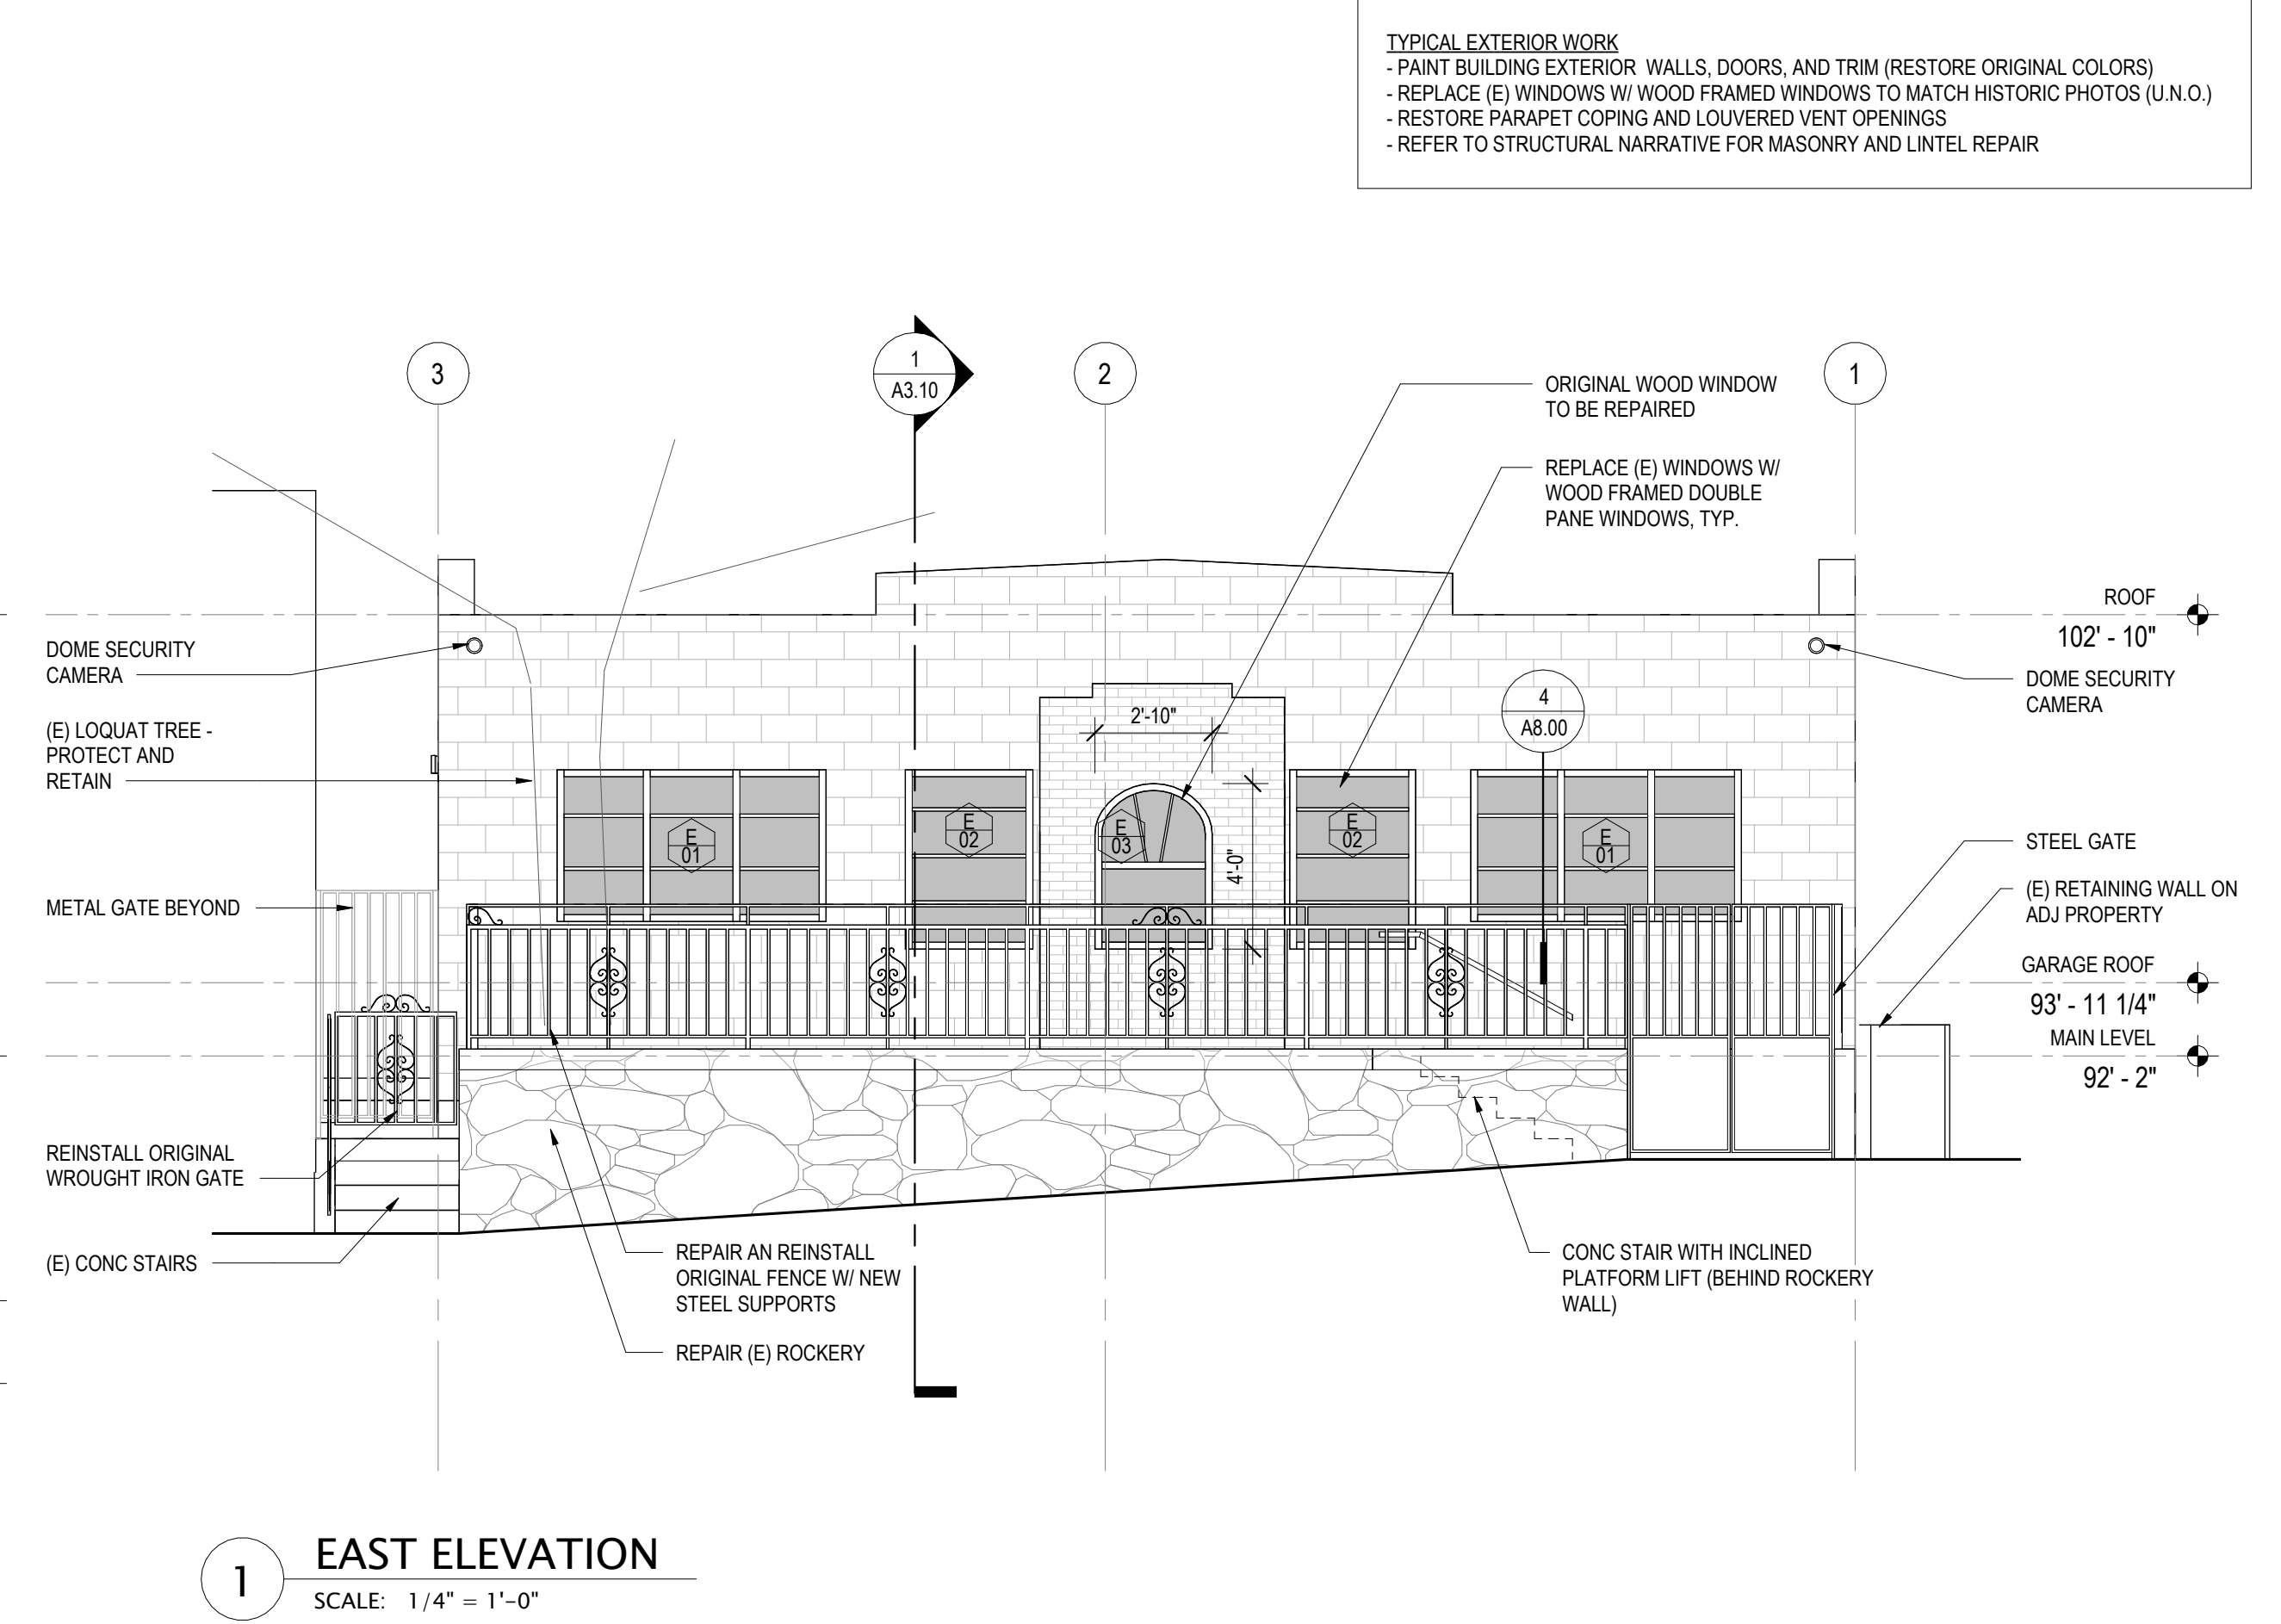
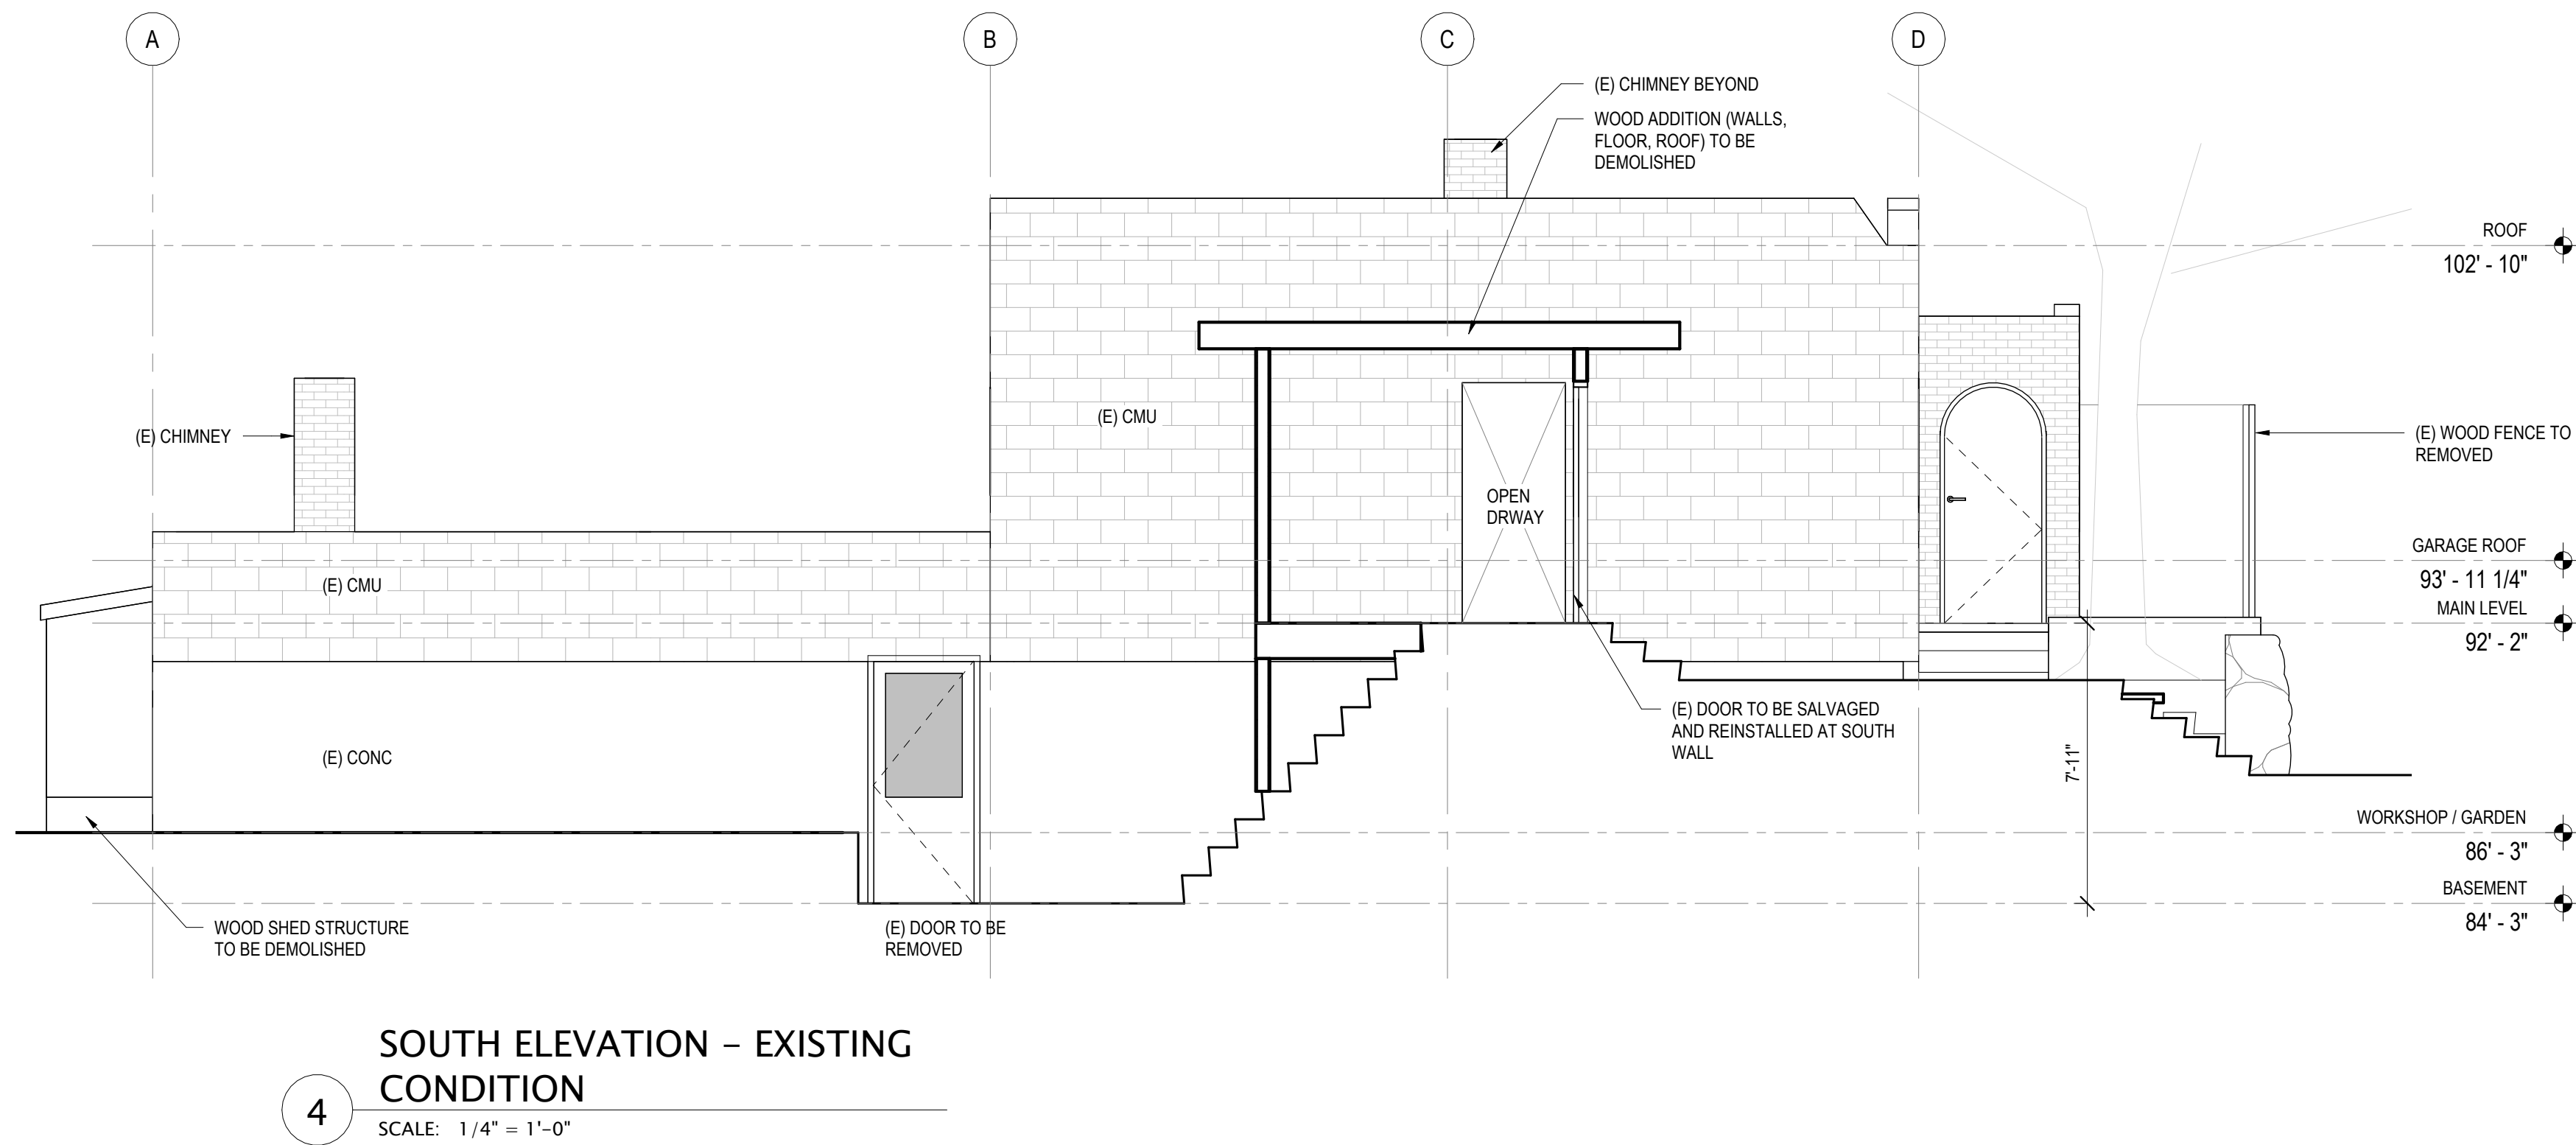


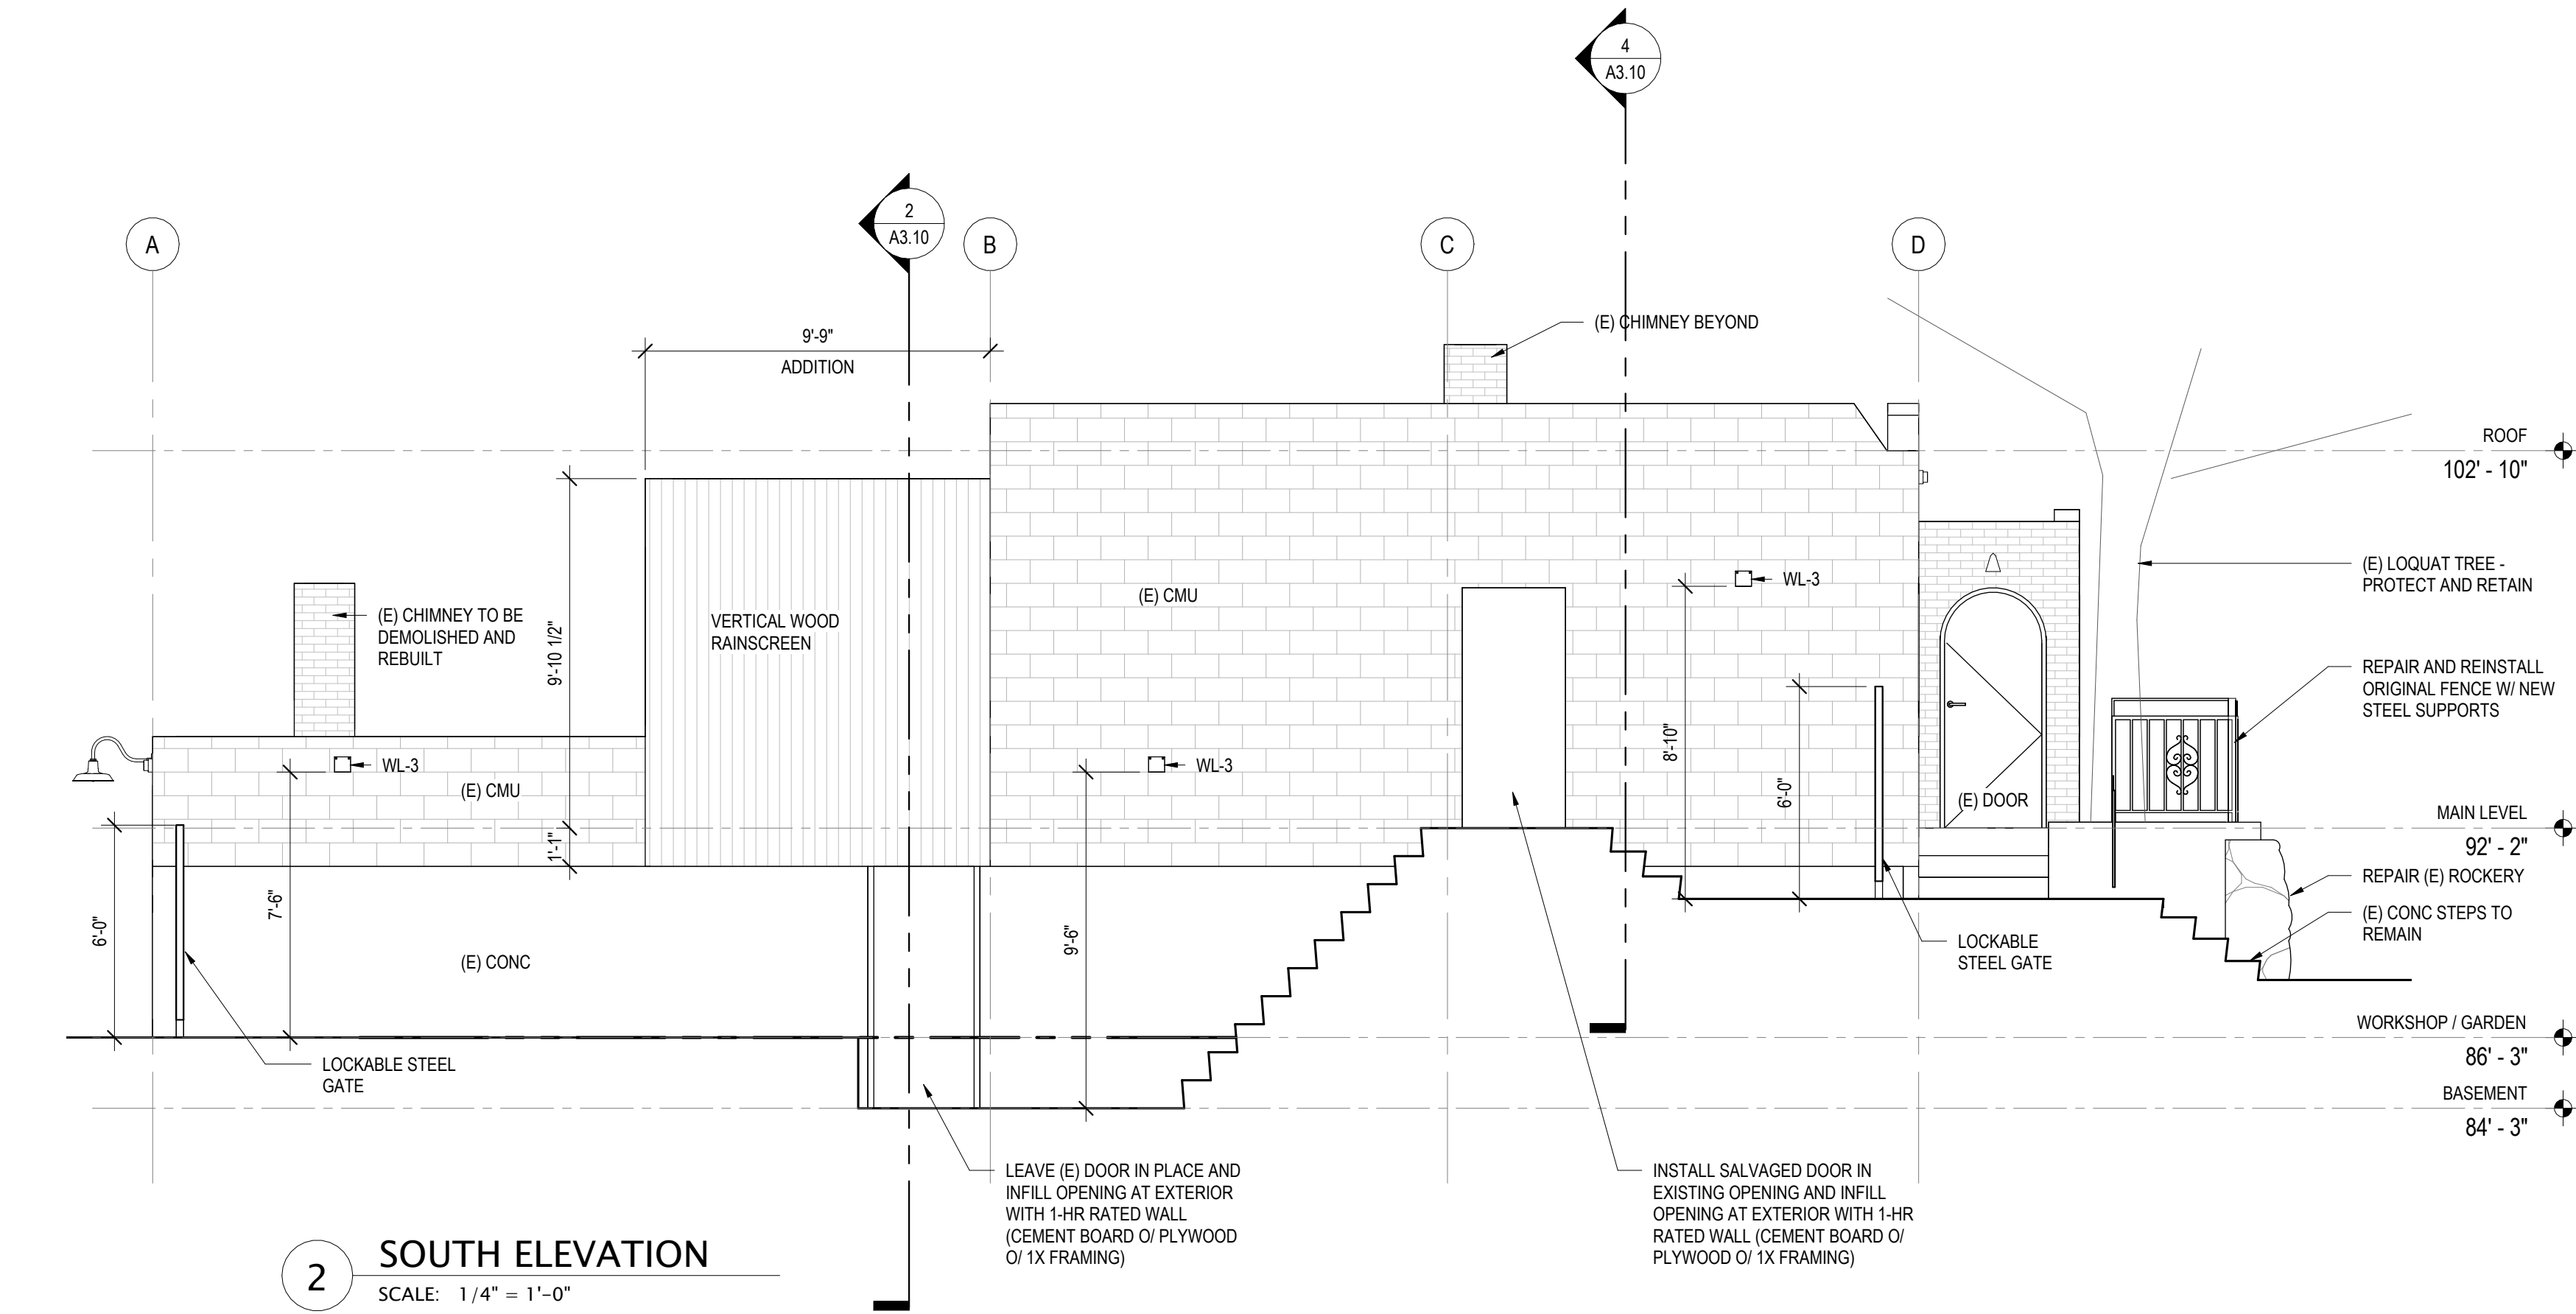

TYPICAL EXTERIOR WORK
- PAINT BUILDING EXTERIOR WALLS, DOORS, AND TRIM (RESTORE ORIGINAL COLORS)
- REPLACE (E) WINDOWS W/ WOOD FRAMED WINDOWS TO MATCH HISTORIC PHOTOS (U.N.O.)
- RESTORE PARAPET COPING AND LOUVERED VENT OPENINGS
- REFER TO STRUCTURAL NARRATIVE FOR MASONRY AND LINTEL REPAIR

SUNDBERG
KENNEDY
LY-AU YOUNG
ARCHITECTS

1501 E MADISON, SUITE 205
SEATTLE WA 98122-4465
206.322.1130

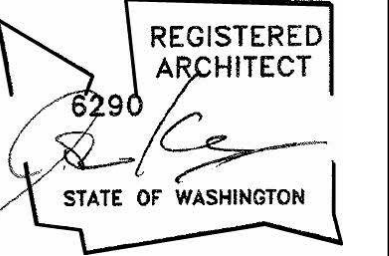

Official
Stamps:

Eng Family Homestead Renovation
611 8th Ave South, Seattle, WA 98104

NO.	DESCRIPTION	DATE	ISRD CERTIFICATE OF APPROVAL	2/23/2024

EXTERIOR ELEVATIONS - SOUTH AND EAST

Project number	22013	Project Manager	JK/NL	Checked by	1/4" = 1'-0"
Date	2/23/2024	Drawn by	NL	Scale	

A3.00