




Official
Stamps:

Eng Family Homestead Renovation
611 8th Ave South, Seattle, WA 98104


EXTERIOR ELEVATIONS - NORTH AND WEST

REVISIONS		DATE		ISRD CERTIFICATE OF APPROVAL		2/23/2024
NO.	DESCRIPTION	NO.	DESCRIPTION	NO.	DESCRIPTION	
22013	Project number	22013	Project number	JK/NL	Project Manager	Checked by
2/23/2024	Date	2/23/2024	Date	NL	Drawn by	
A3.01		Scale		1/4" = 1'-0"		Checker


TYPICAL EXTERIOR WORK
- PAINT BUILDING EXTERIOR, WALLS, DOORS, AND TRIM (RESTORE ORIGINAL COLORS)
- REPLACE (E) WINDOWS W/ WOOD FRAMED WINDOWS TO MATCH HISTORIC PHOTOS (U.N.O.)
- RESTORE PARAPET COPING AND LOUVERED VENT OPENINGS
- REFER TO STRUCTURAL NARRATIVE FOR MASONRY AND LINTEL REPAIR

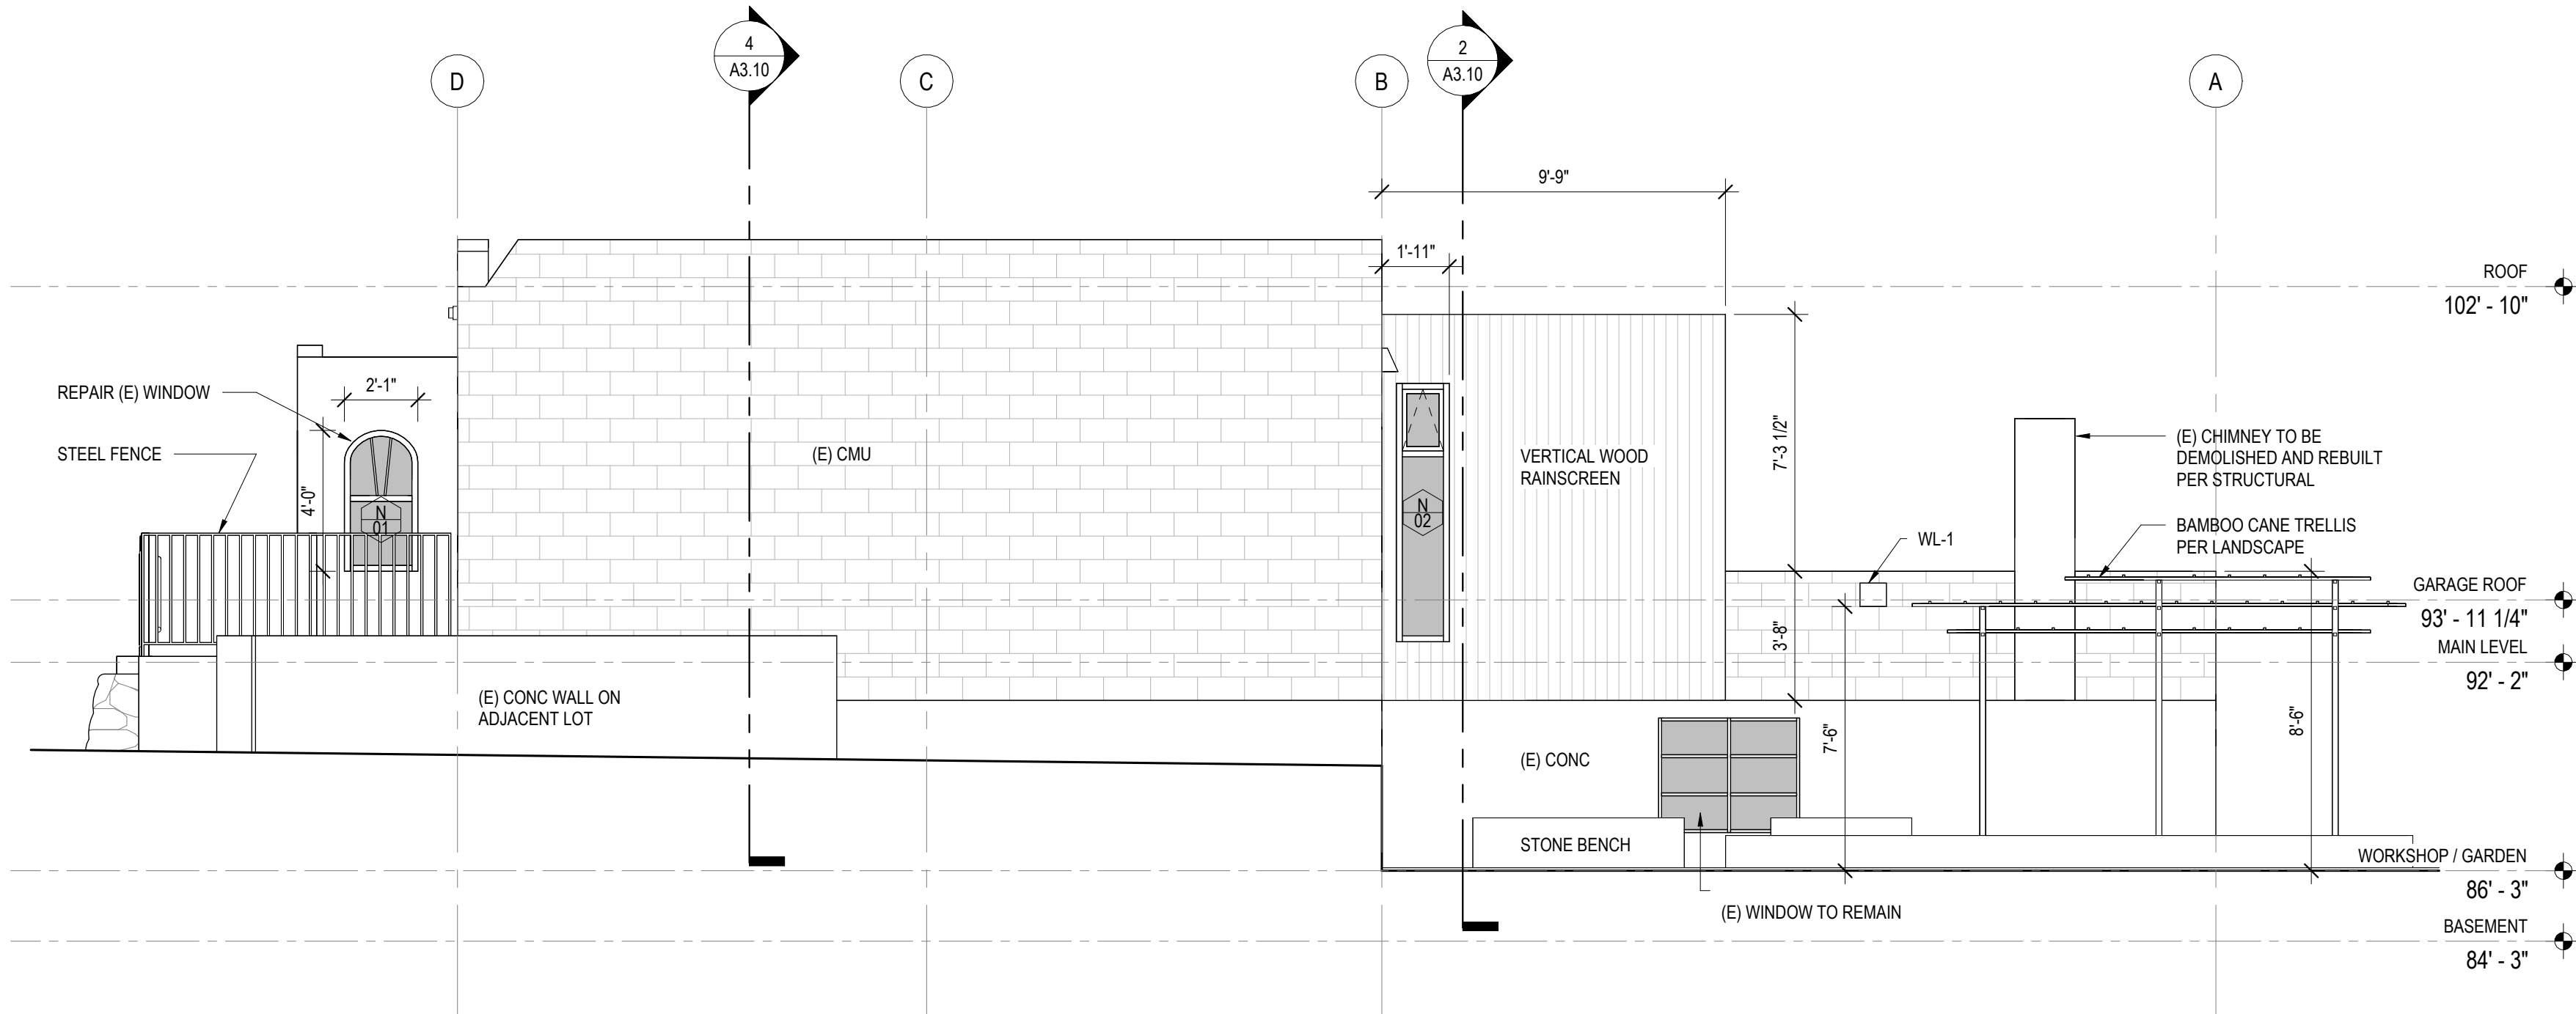


2 NORTH ELEVATION
SCALE: 1/4" = 1'-0"

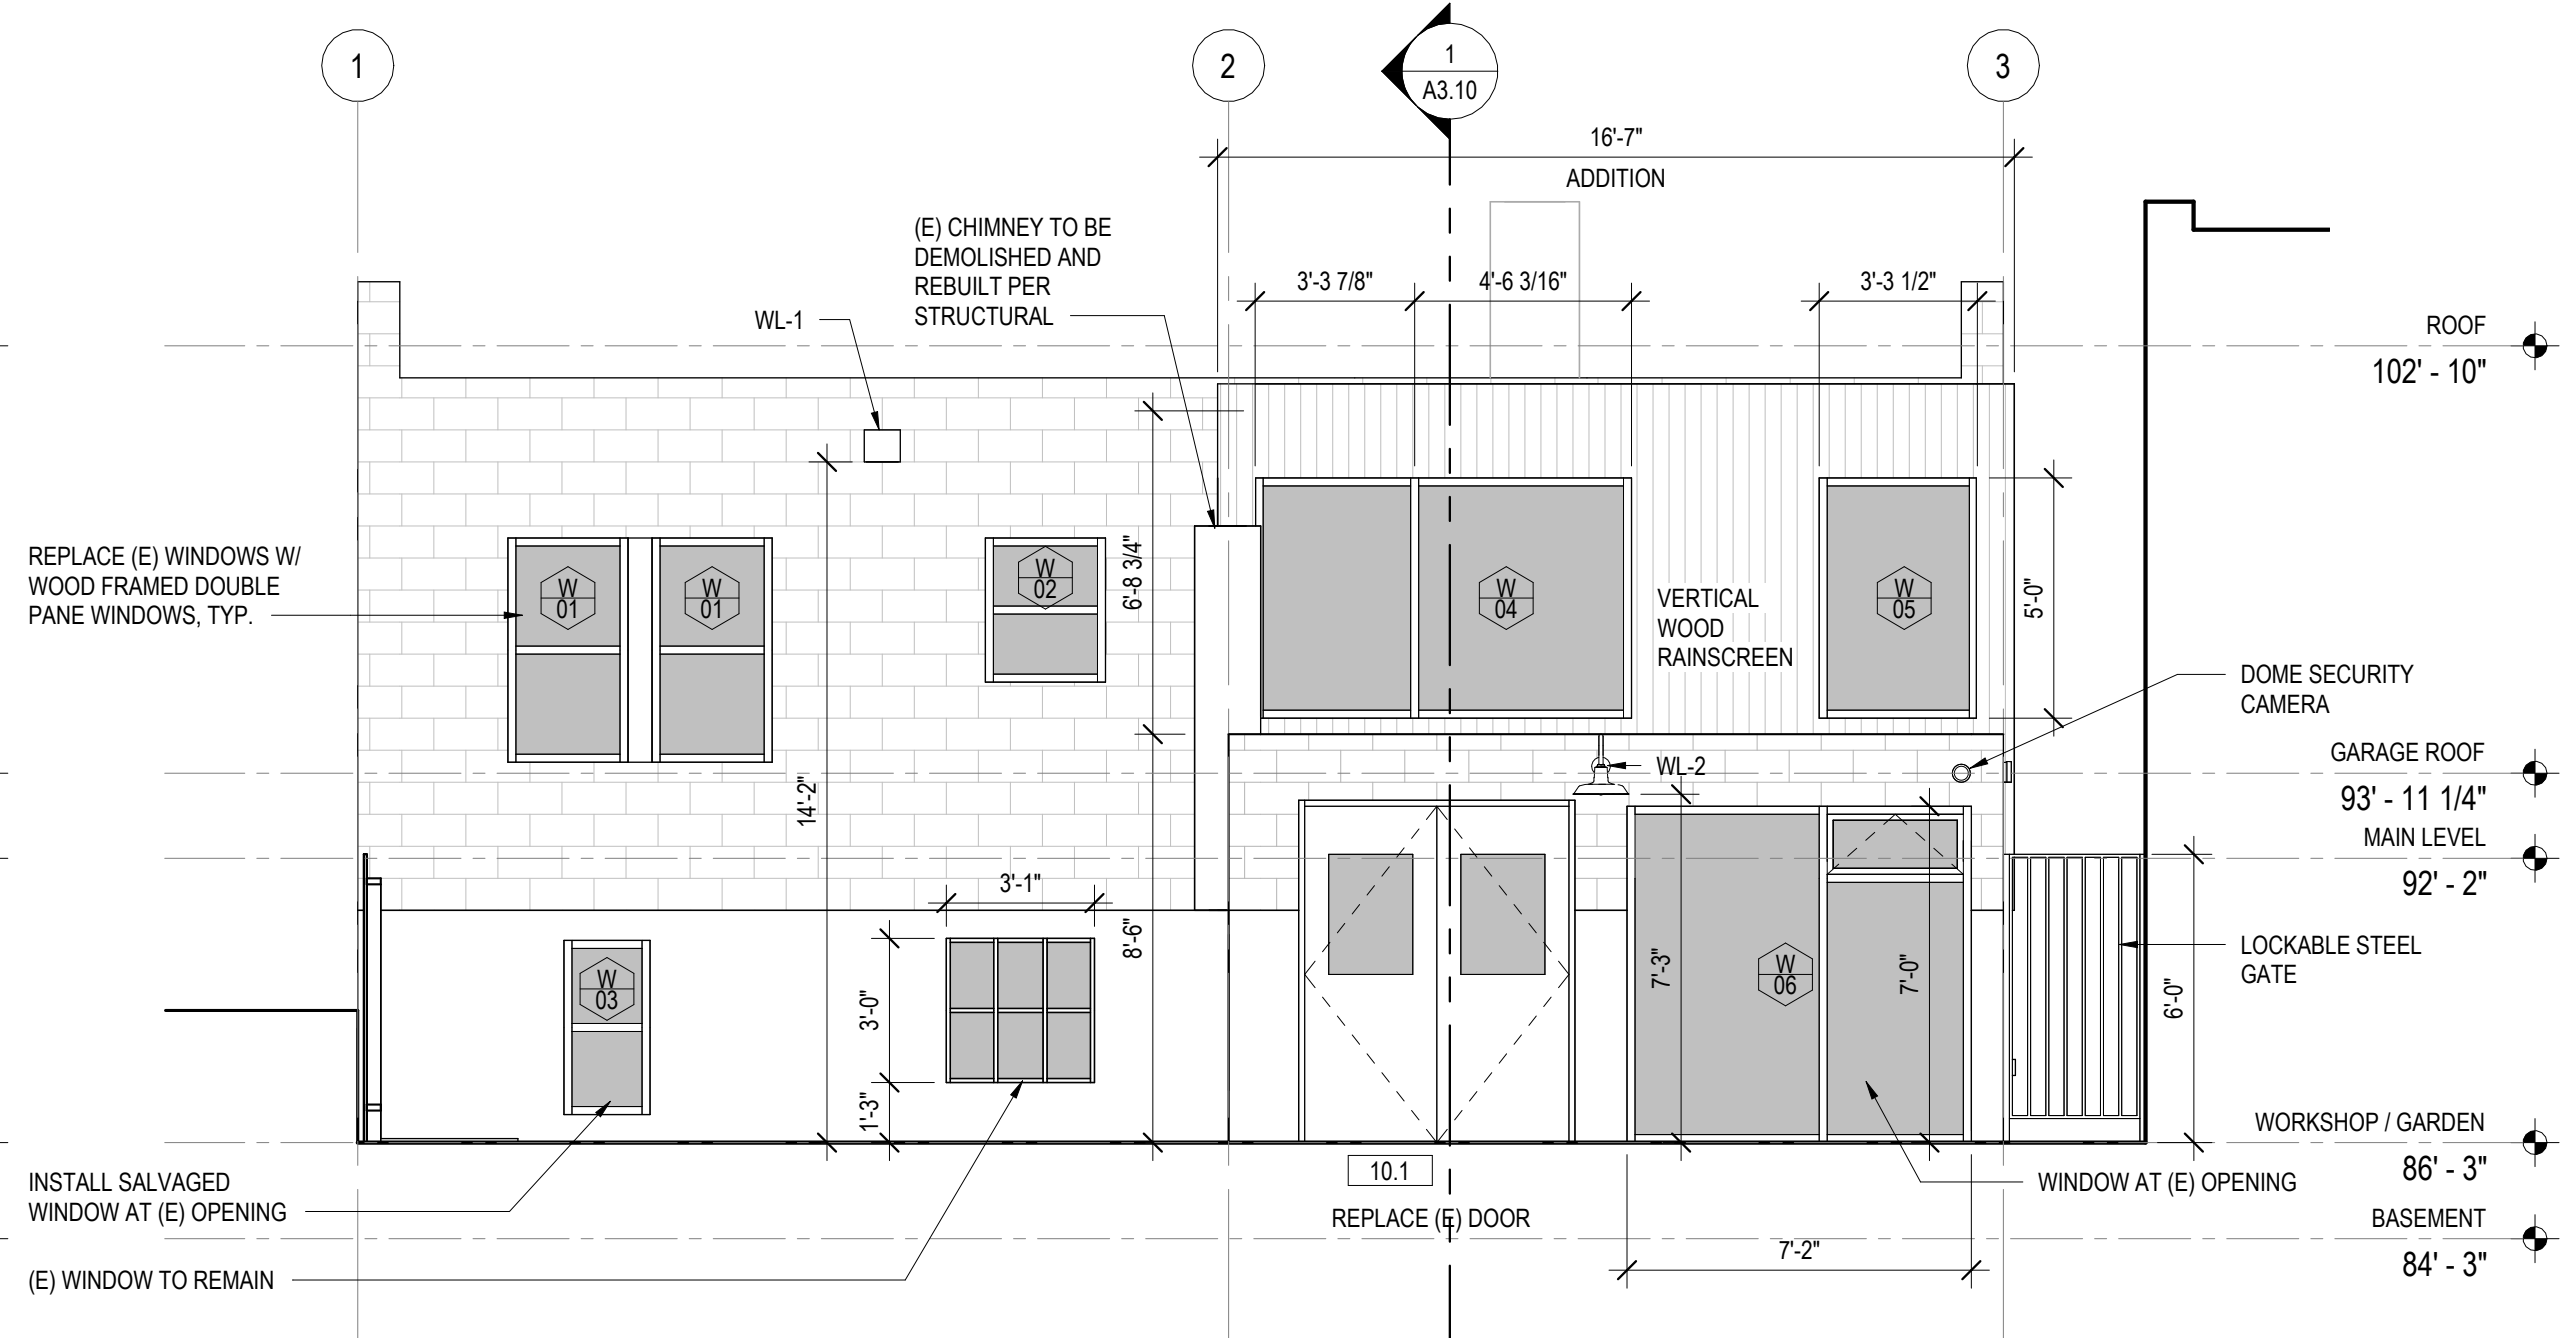

1 WEST ELEVATION
SCALE: 1/4" = 1'-0"

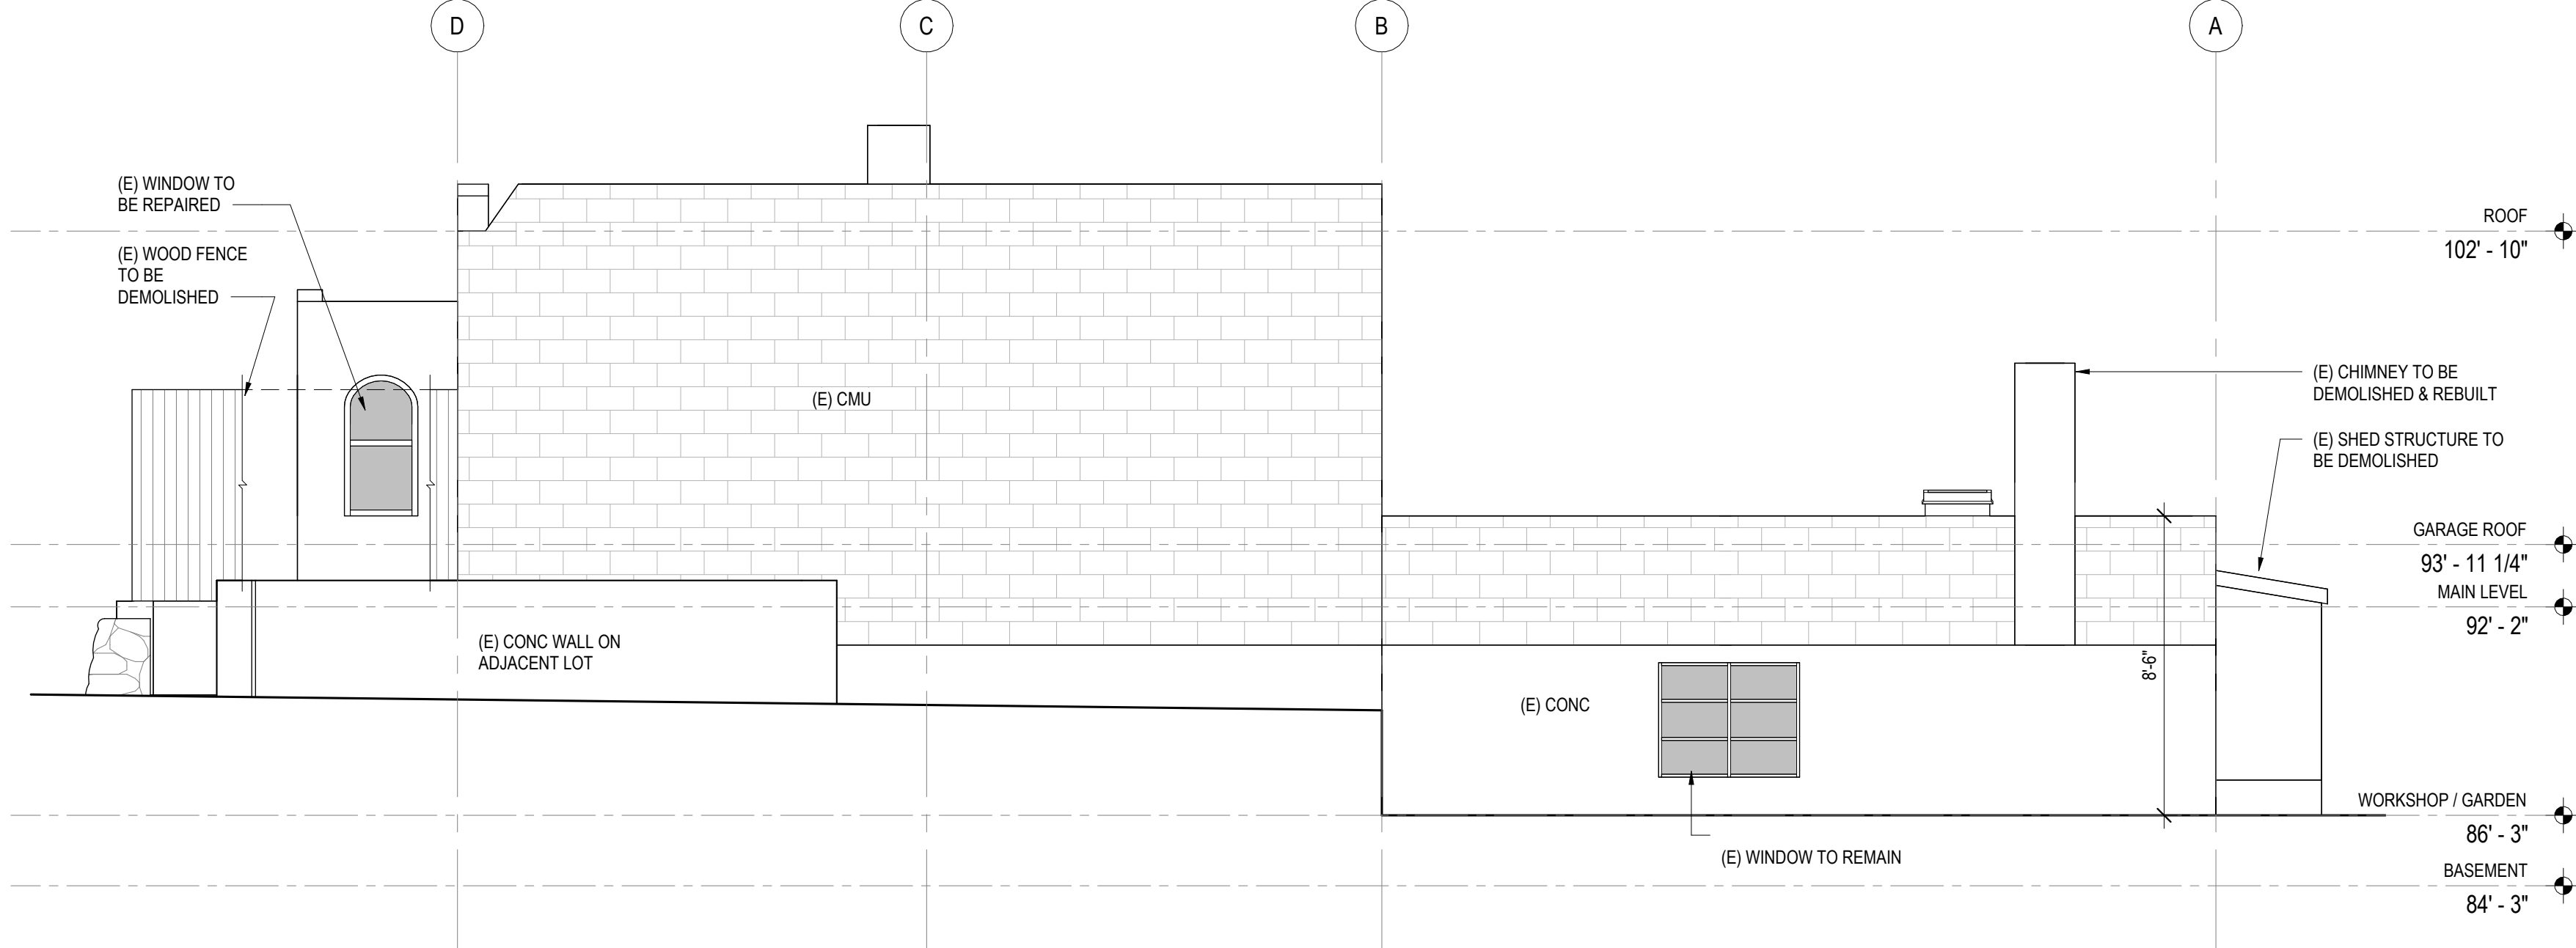

4 NORTH ELEVATION - EXISTING
CONDITION
SCALE: 1/4" = 1'-0"

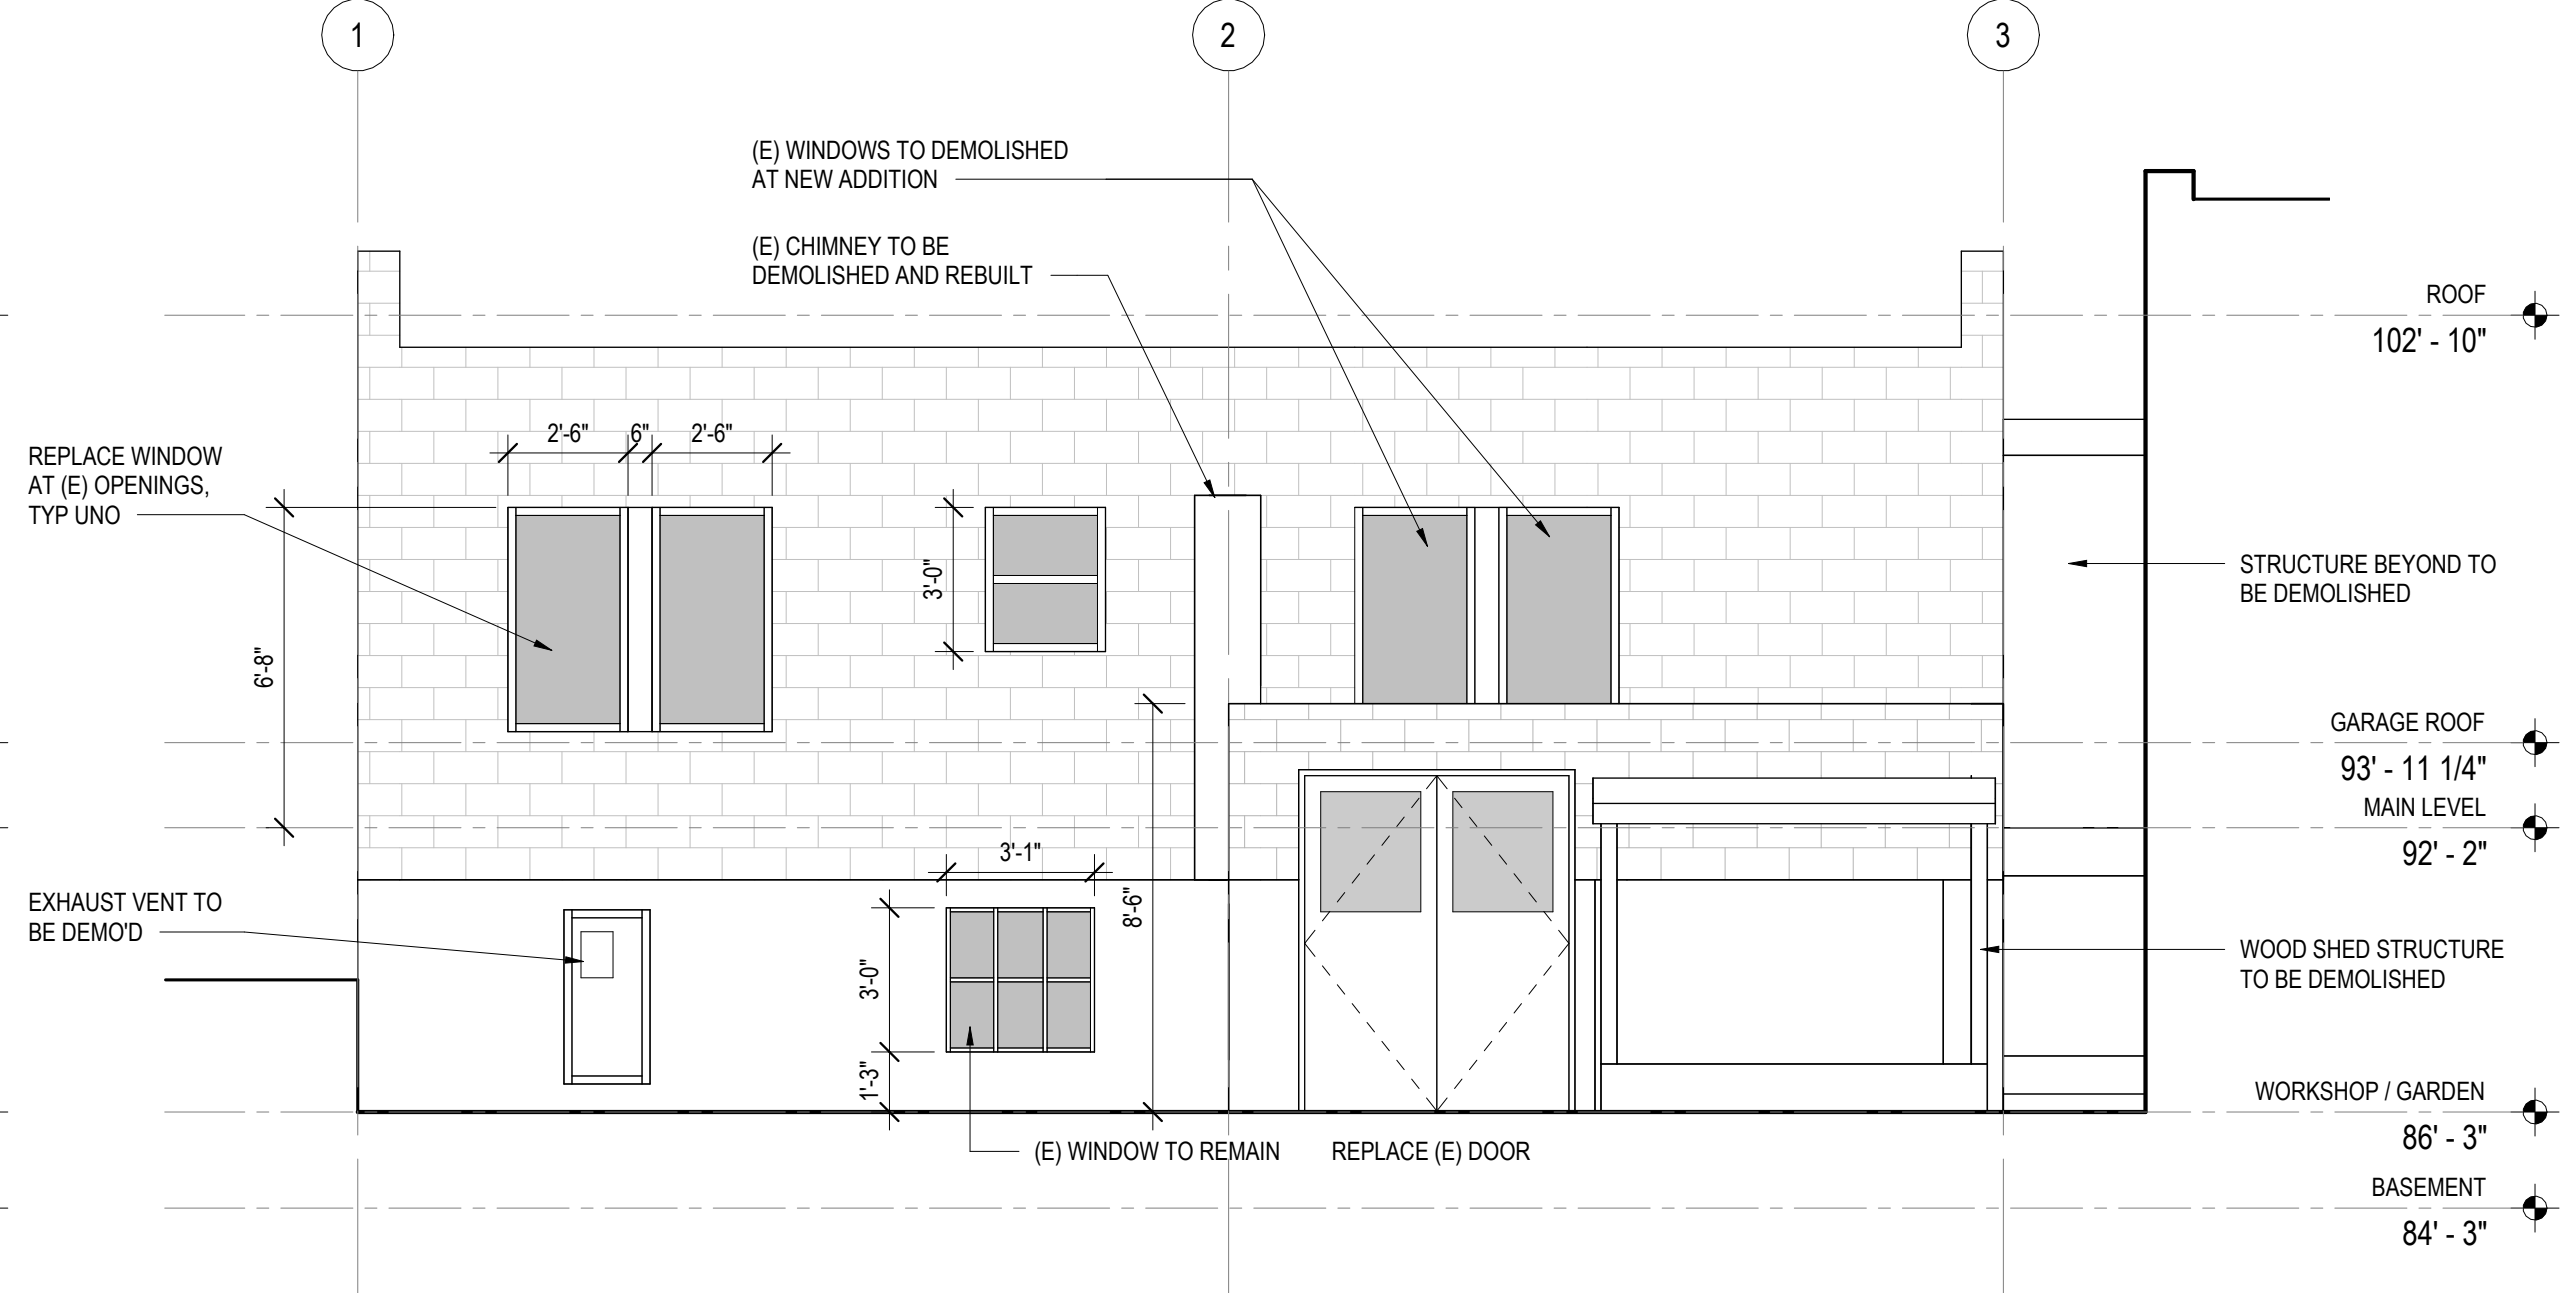

3 WEST ELEVATION - EXISTING
CONDITION
SCALE: 1/4" = 1'-0"