
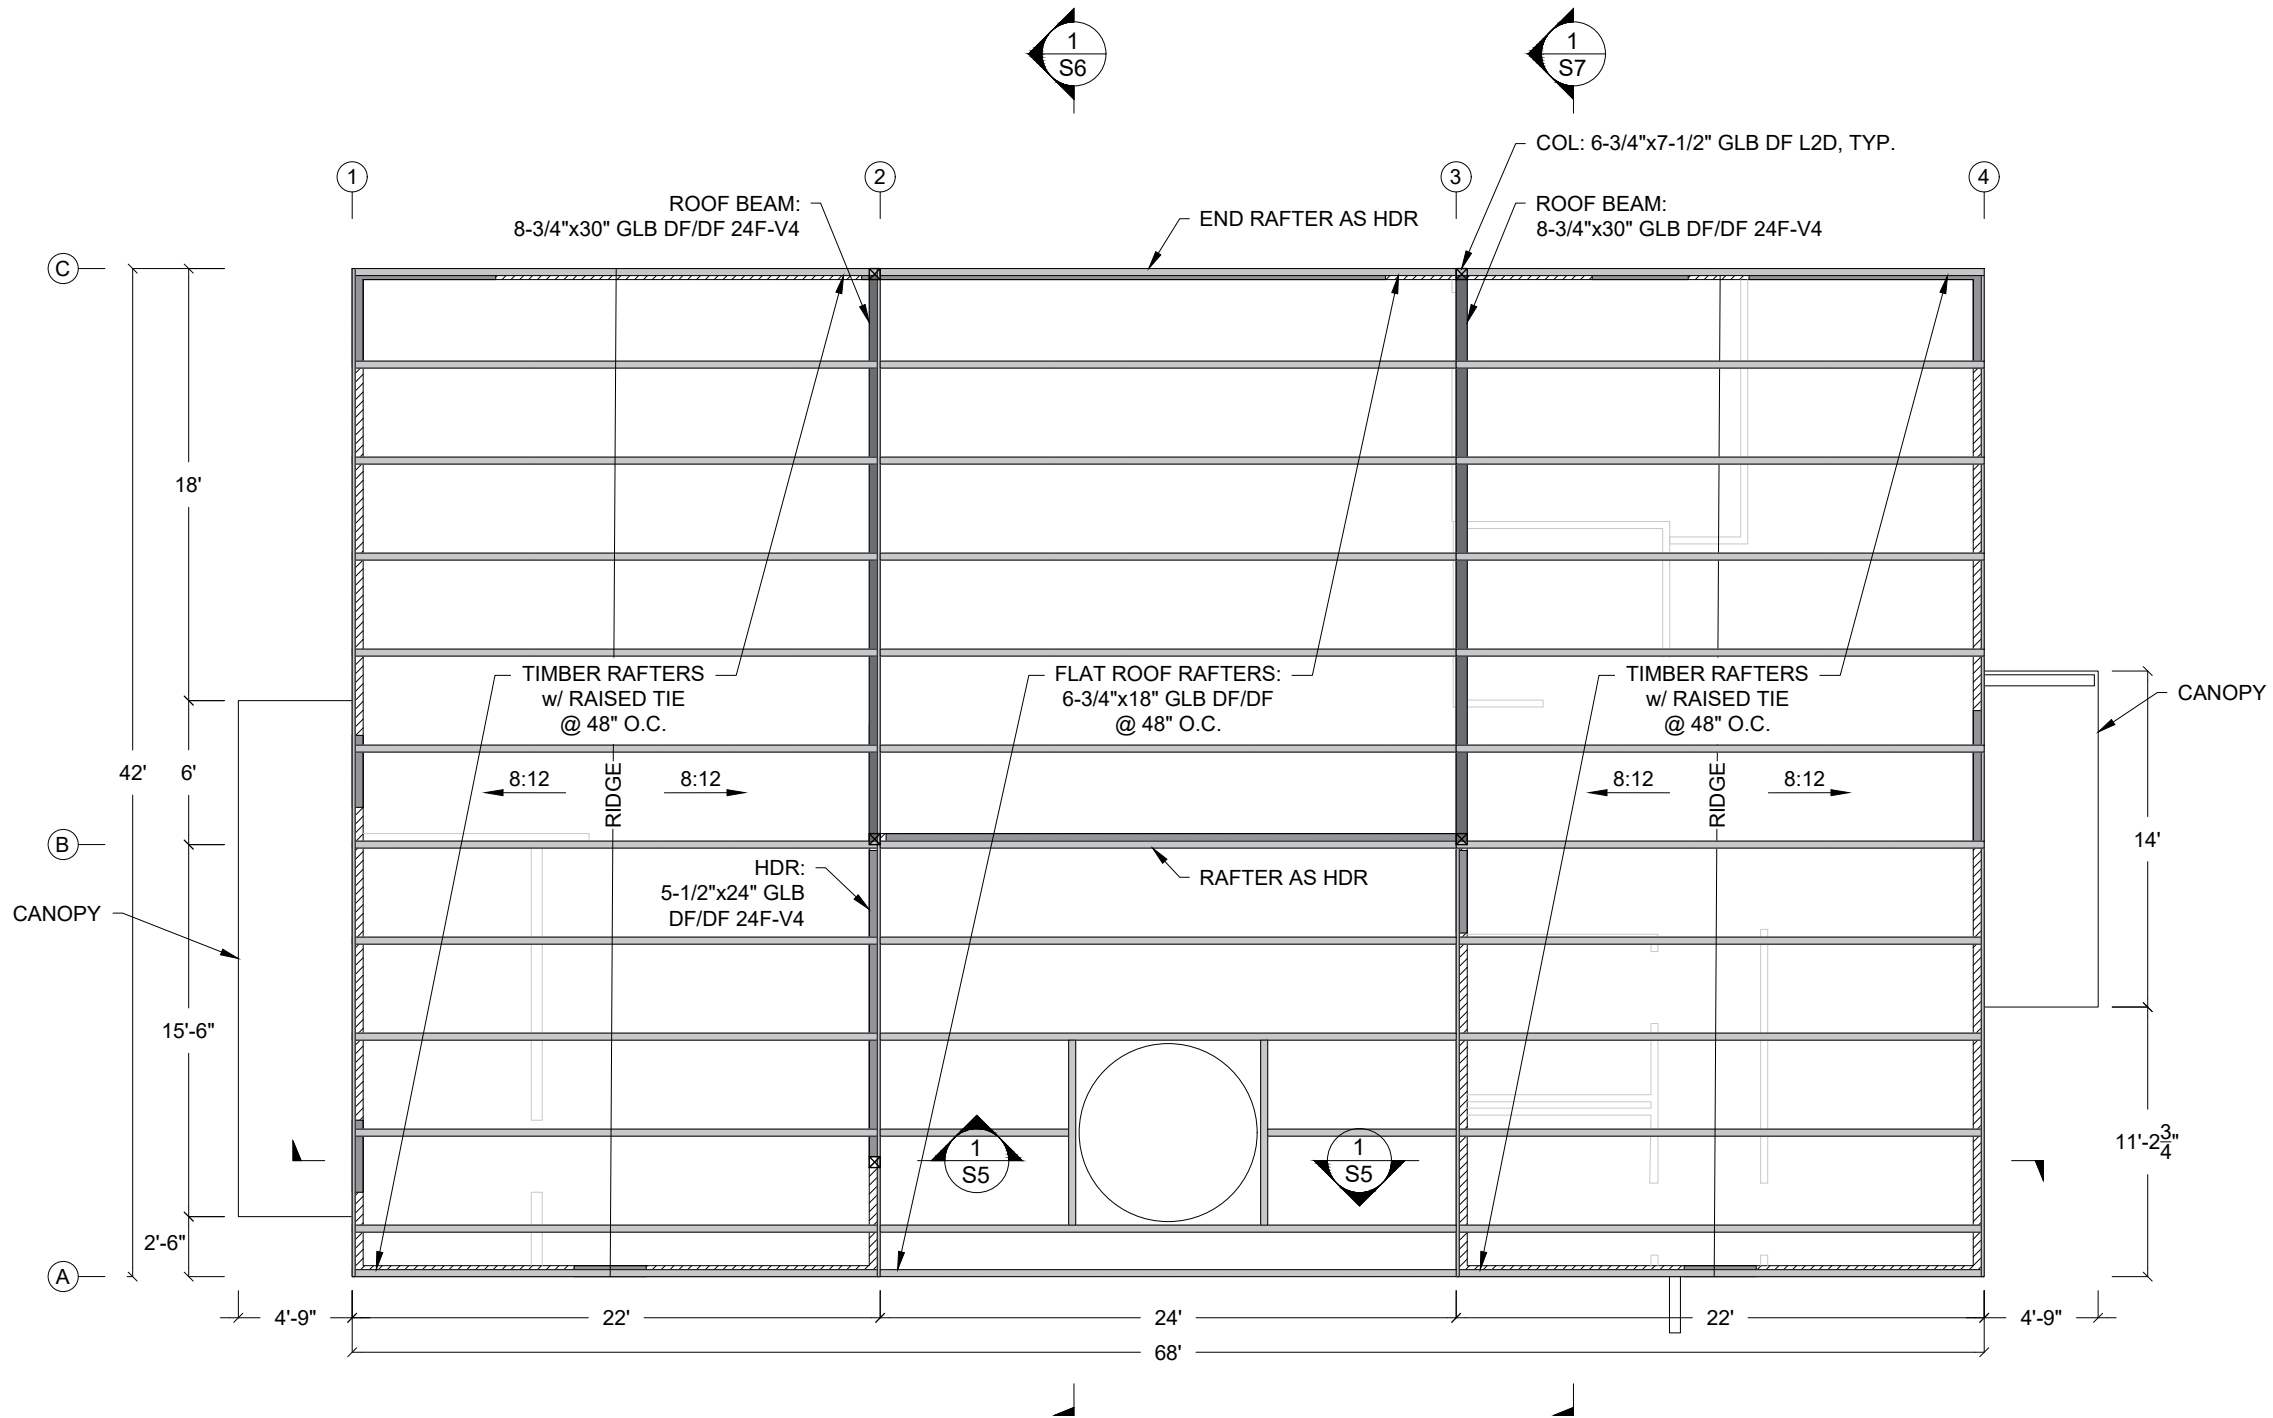


NOTE:
1. HEADERS 6x12 DF#2 U.N.O.

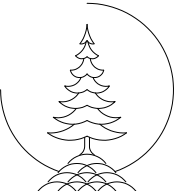


TIMBERLINE ENGINEERING
LLC
JUNEAU, ALASKA
907-635-1433
JAGRAVES77@GMAIL.COM

1" ACTUAL
IF THE ABOVE DIMENSION DOES NOT
MEASURE ONE INCH TO EXACTLY THIS
DRAWING WILL HAVE BEEN ENLARGED OR
REDUCED, AFFECTING ALL LABELED SCALES.

35% SUBMITTAL
**DOUGLAS INDIAN ASSOCIATION AND
TRIBAL GOVERNMENT CULTURAL CENTER**

DOUGLAS INDIAN ASSOCIATION AND TRIBAL GOVERNMENT
ST. ANN'S AVENUE, DOUGLAS, ALASKA

SHEET TITLE:
ROOF FRAMING PLAN

CHECKED	JG	
DRAWN	JG	
issue	date	description

SHEET #
S4