
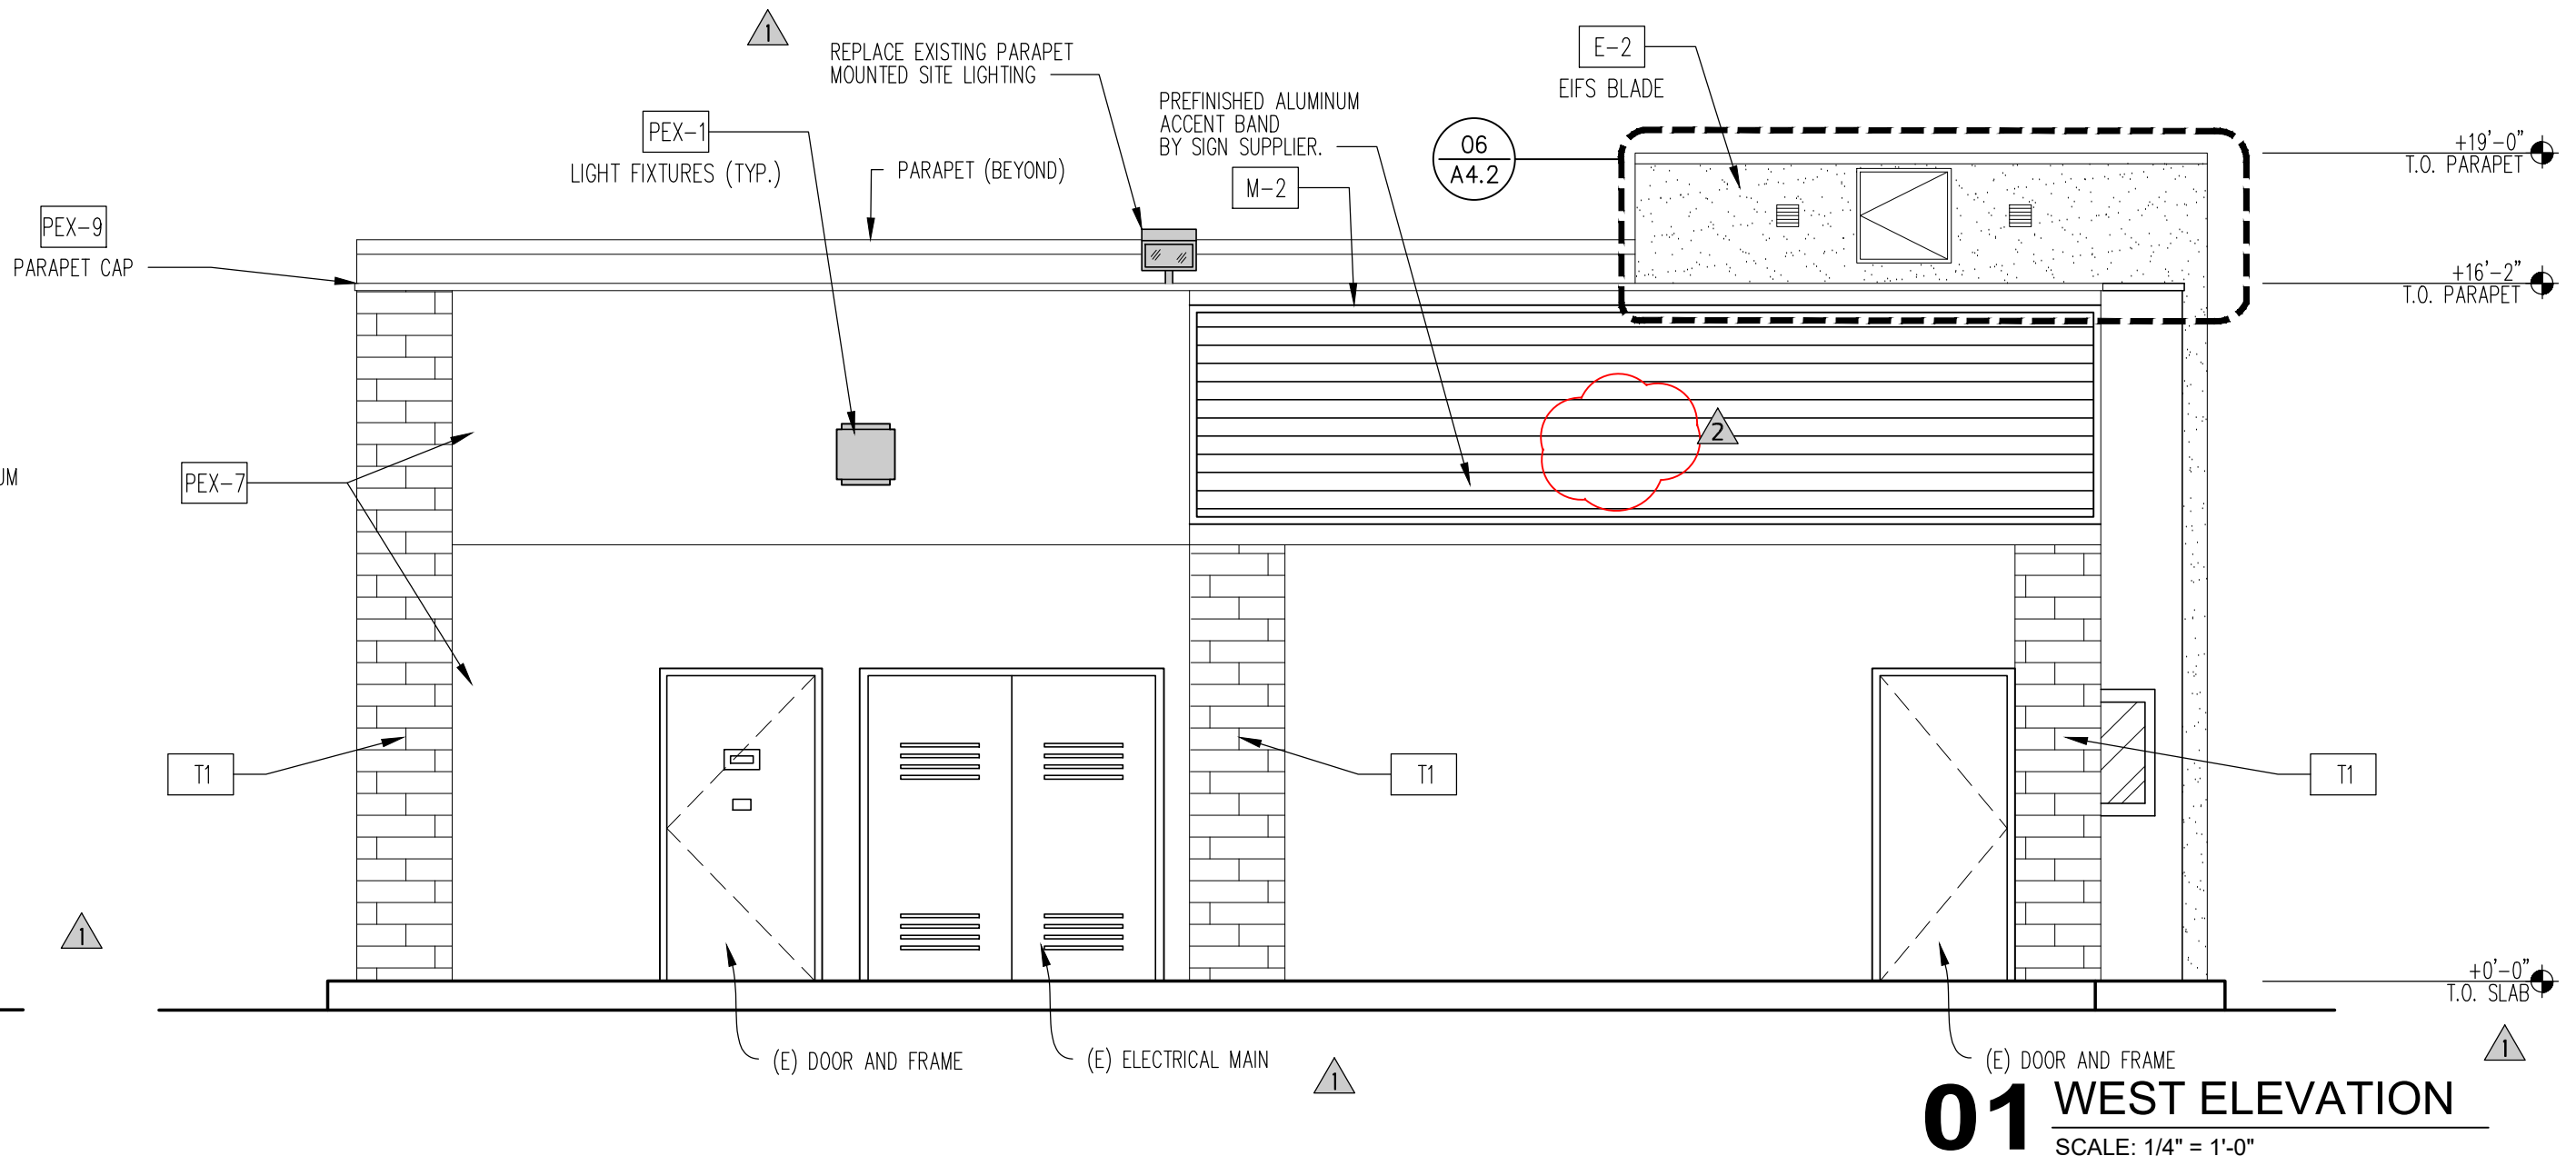
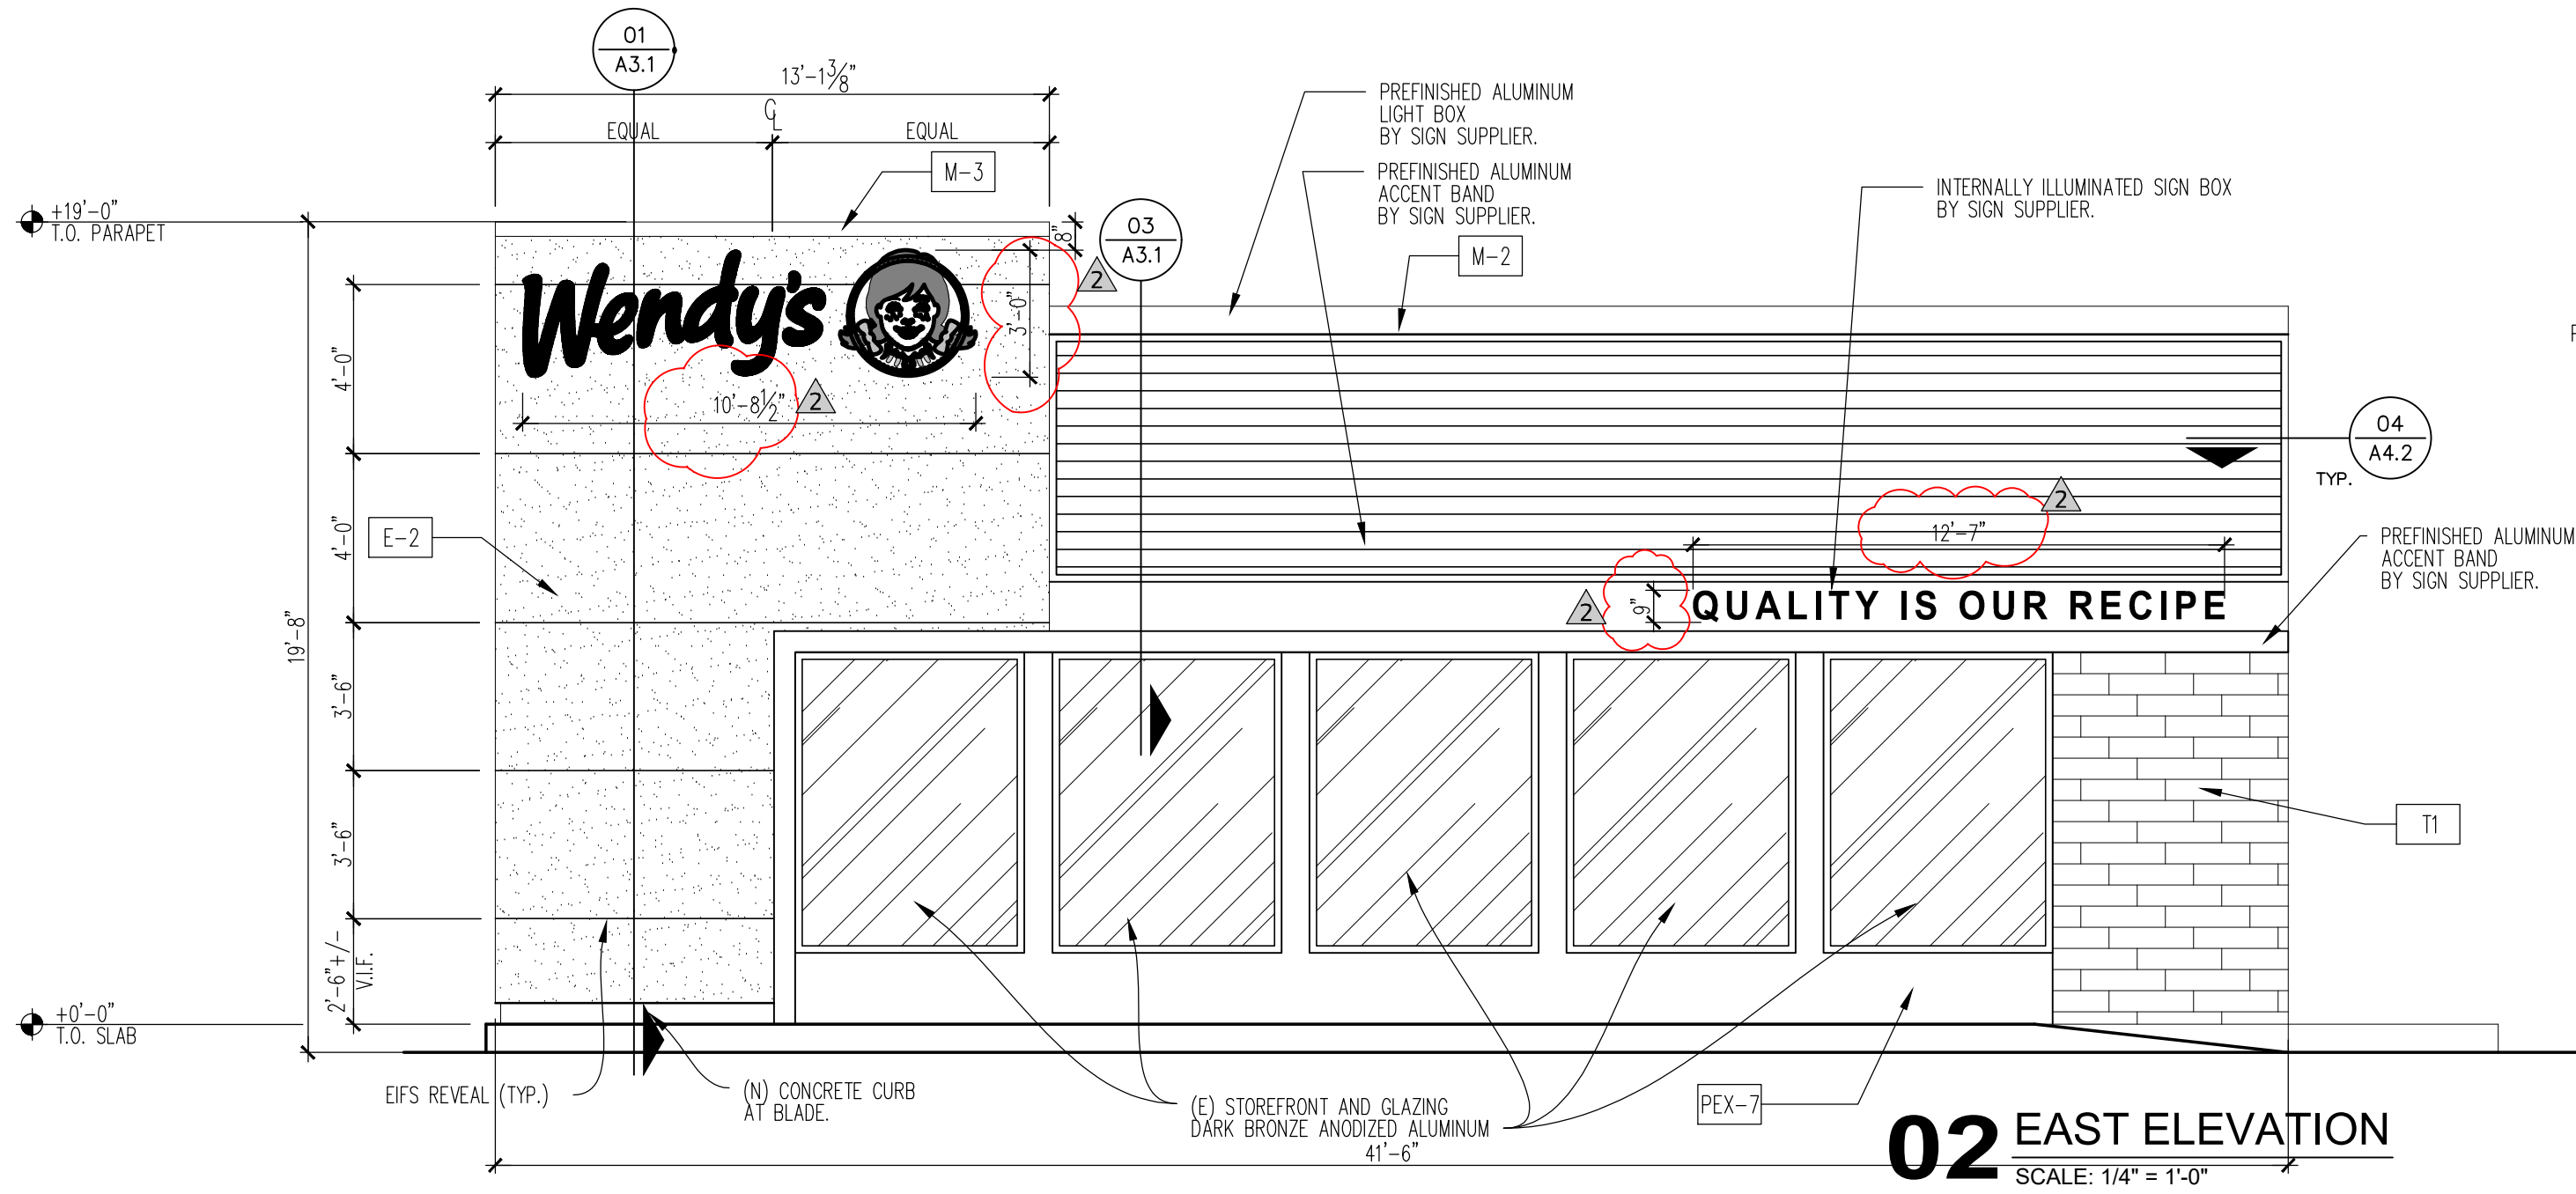
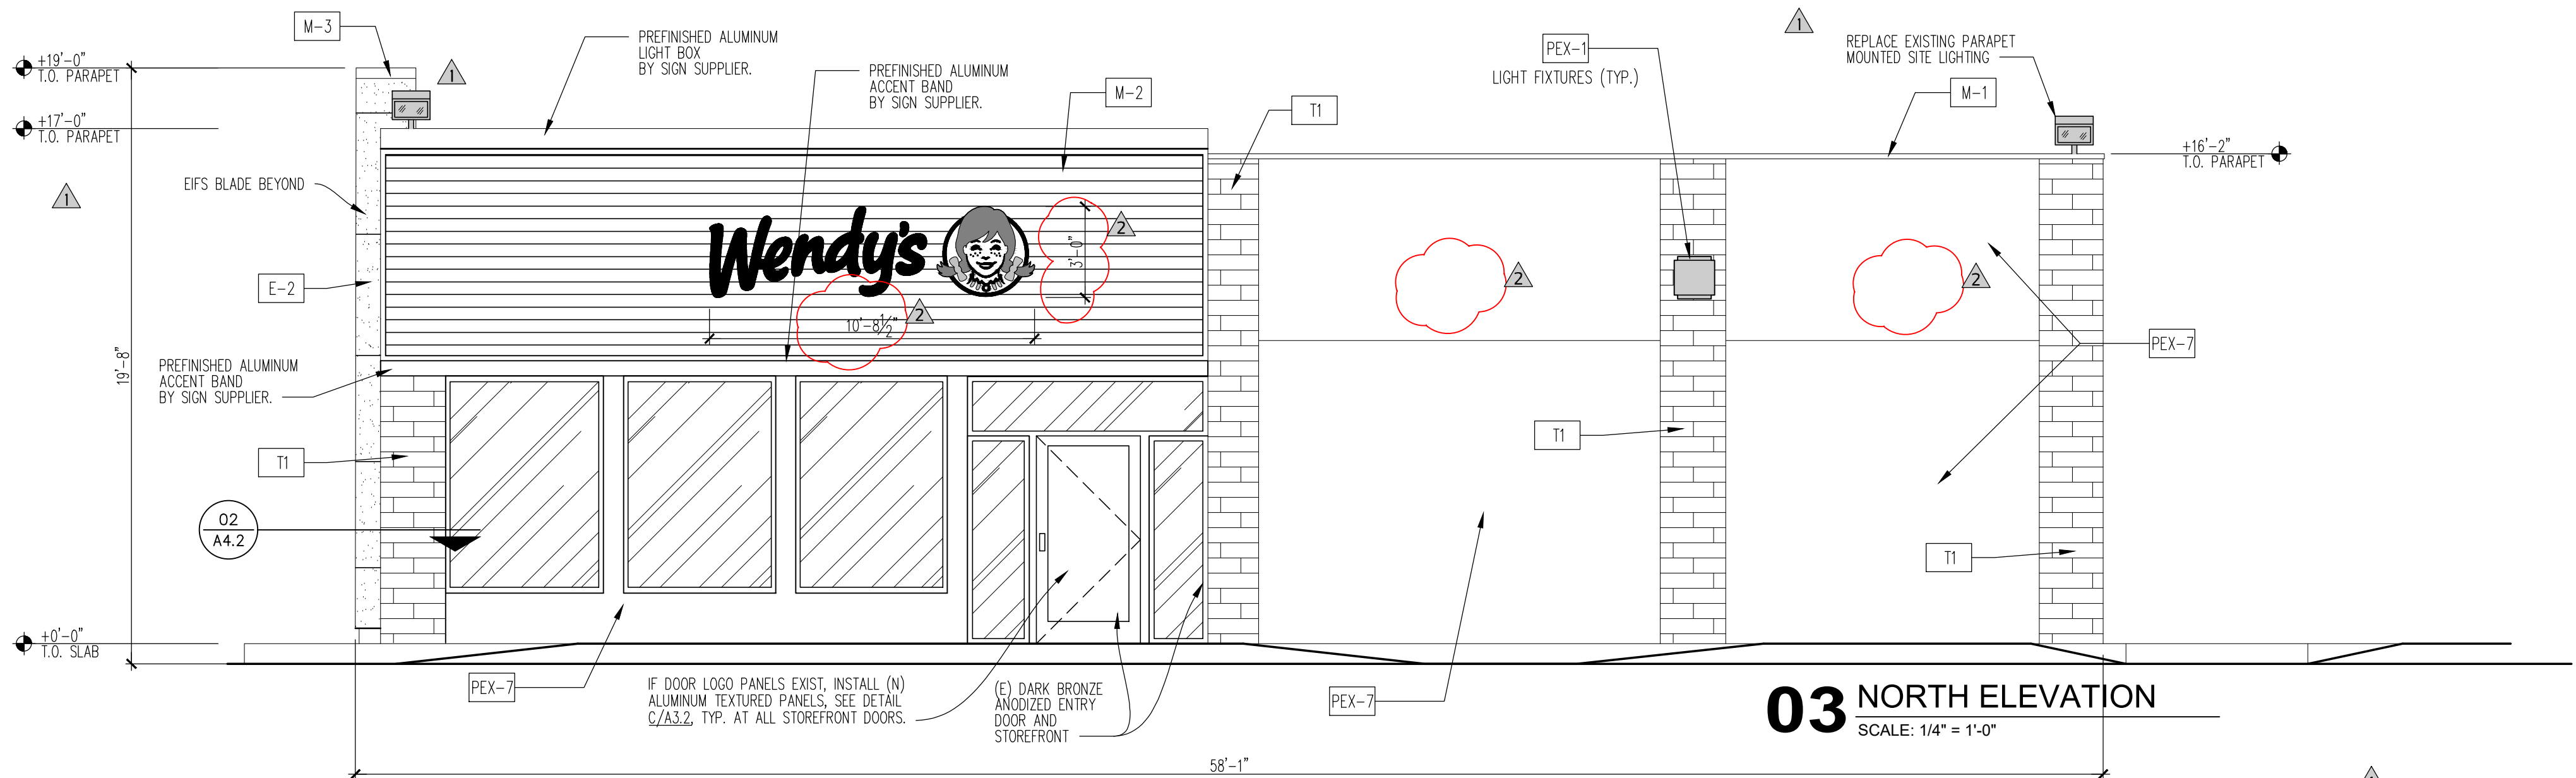


BUILDING SIGNAGE TABLE		
ELEVATION	EXISTING	PROPOSED
SOUTH	36.30 S.F.	16.25S.F.
NORTH	36.30 S.F.	16.25 S.F.
EAST	36.30 S.F.	22.1 S.F.
WEST	36.30 S.F.	0 S.F.

(N) WENDYS SIGN	
TOTAL	16.25 S.F.
(N) SIGN QUALITY IS OUR RECIPE	
TOTAL	5.85 S.F.

NOTE:

1. ALL LIGHT FIXTURES WILL BE SHIELDED AND POINTED DOWNWARD.
2. PAINT EXISTING TRASH ENCLOSURE, "BISCUIT" SW6112,
3. NEW PARAPET HEIGHT WILL NOT EXCEED 40' IN HEIGHT PER CBC 504.3

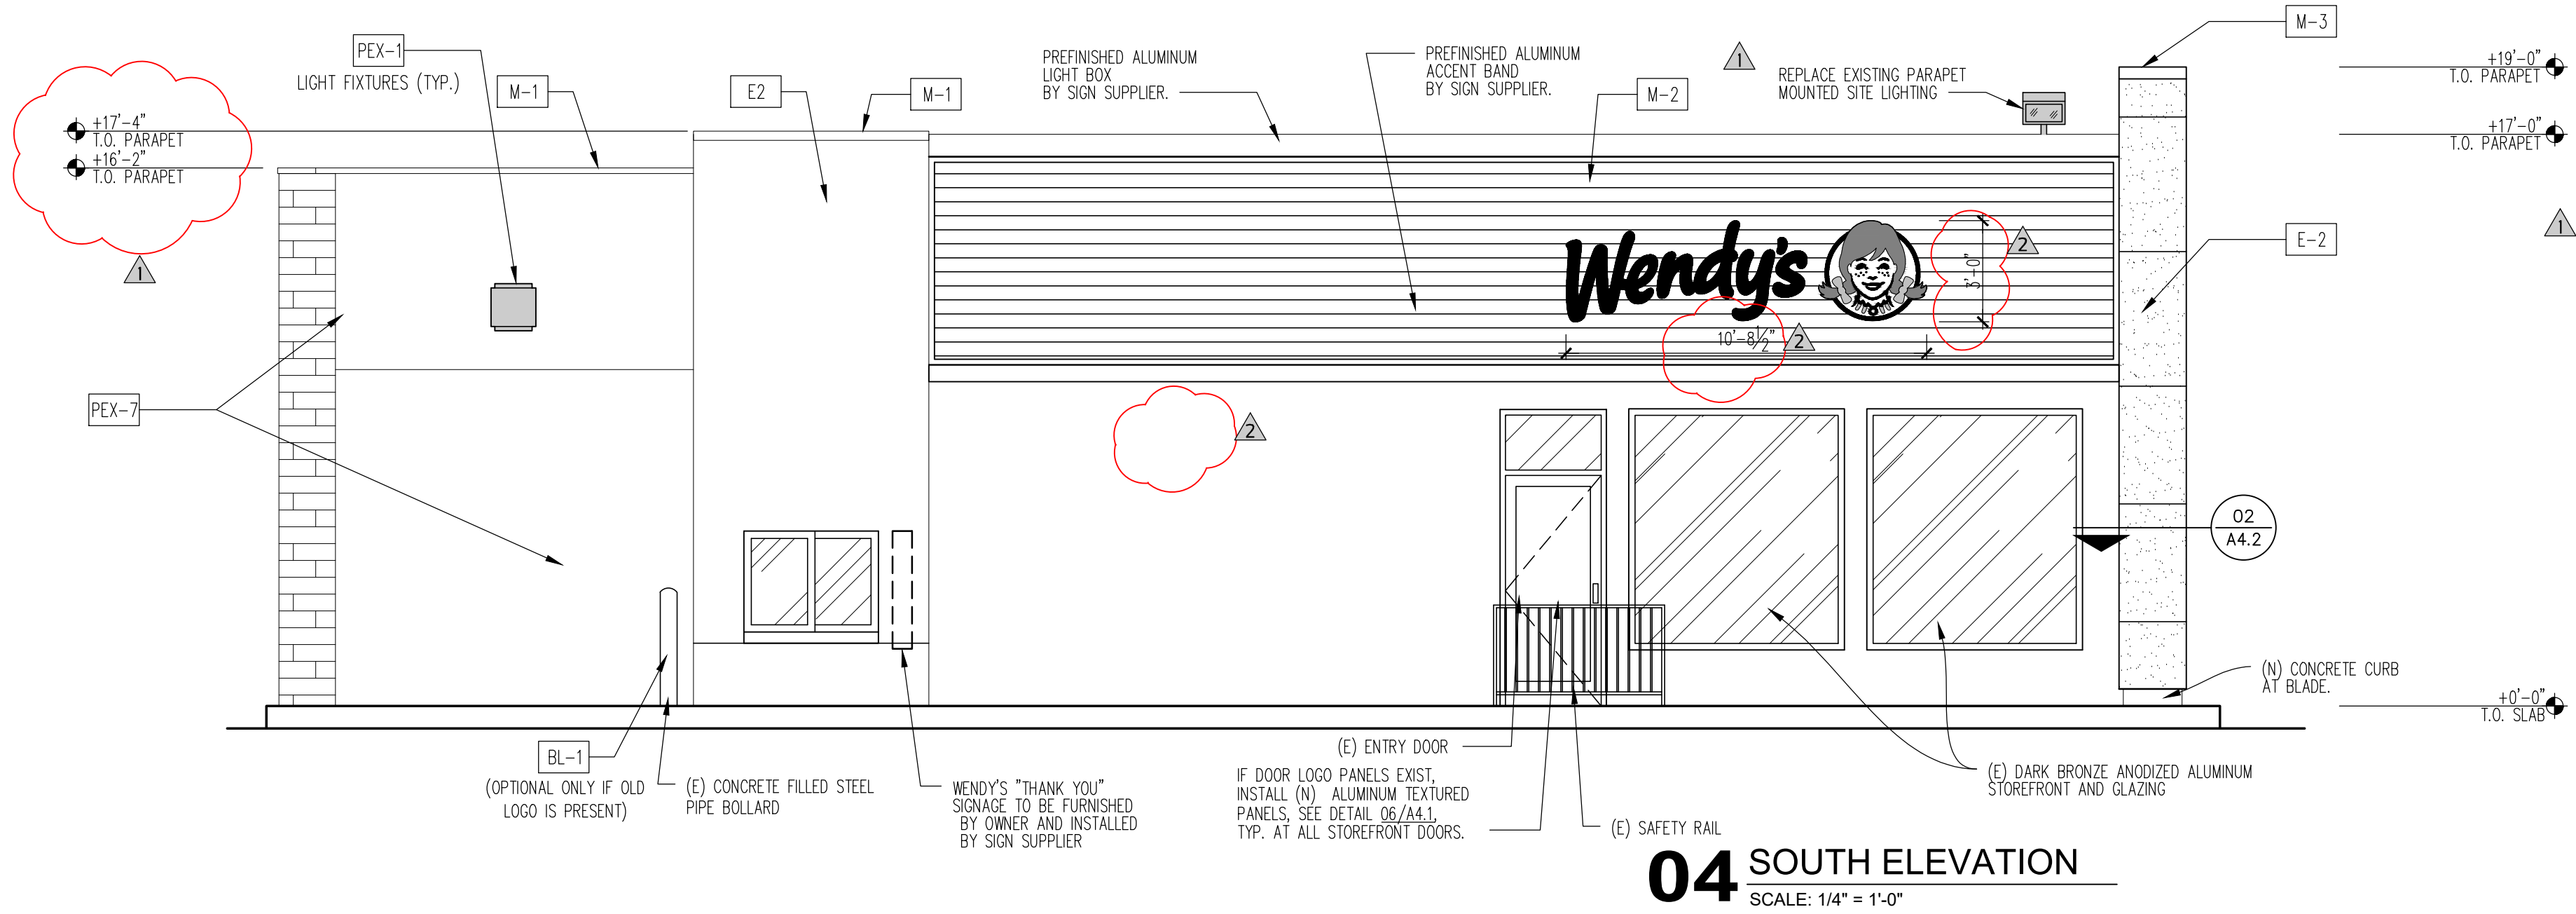

SITE NUMBER:	3835
BASE MODEL:	4058
ASSET TYPE:	COMPANY/FRANCHISE
CLASSIFICATION:	REFRESH LITE
OWNER:	OWNER NAME
BASE VERSION:	2017 SPRING
UPGRADE CLASSIFICATION:	N/A
PROJECT YEAR:	2018
FURNITURE PACKAGE:	2018
DRAWING RELEASE:	MARCH 2017



6930 DESTINY DRIVE
SUITE 100
ROCKLIN, CA 95677

(916) 415-5358
rpedro@pmdgnc.com

Roy W. Pedro, Architect

PROJECT TYPE: E4056
REFRESH LITE

Wendy's

102 ENCINITAS BLVD.
ENCINITAS, CA 92024

REV.	DATE	DESCRIPTION
	9/30/2019	BLDG 1ST SUBMITTAL
	10/10/2019	PLANNING REVISIONS
1	10/24/2019	BLDG./ HEALTH COMMENTS
2	10/31/2019	PLANNING COMMENTS
3	10/31/2019	QA/QC COMMENTS


ISSUE DATE: 04/20/2018

PROJECT NUMBER: WKS18003.0

DRAWN BY: XXXX

CHECKED BY: XXXX

SEAL

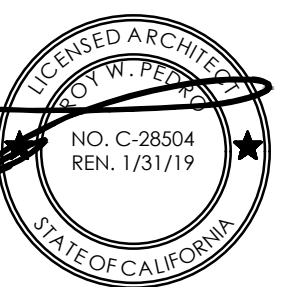

SHEET NAME
EXTERIOR ELEVATIONS

SHEET NUMBER
A2.2