



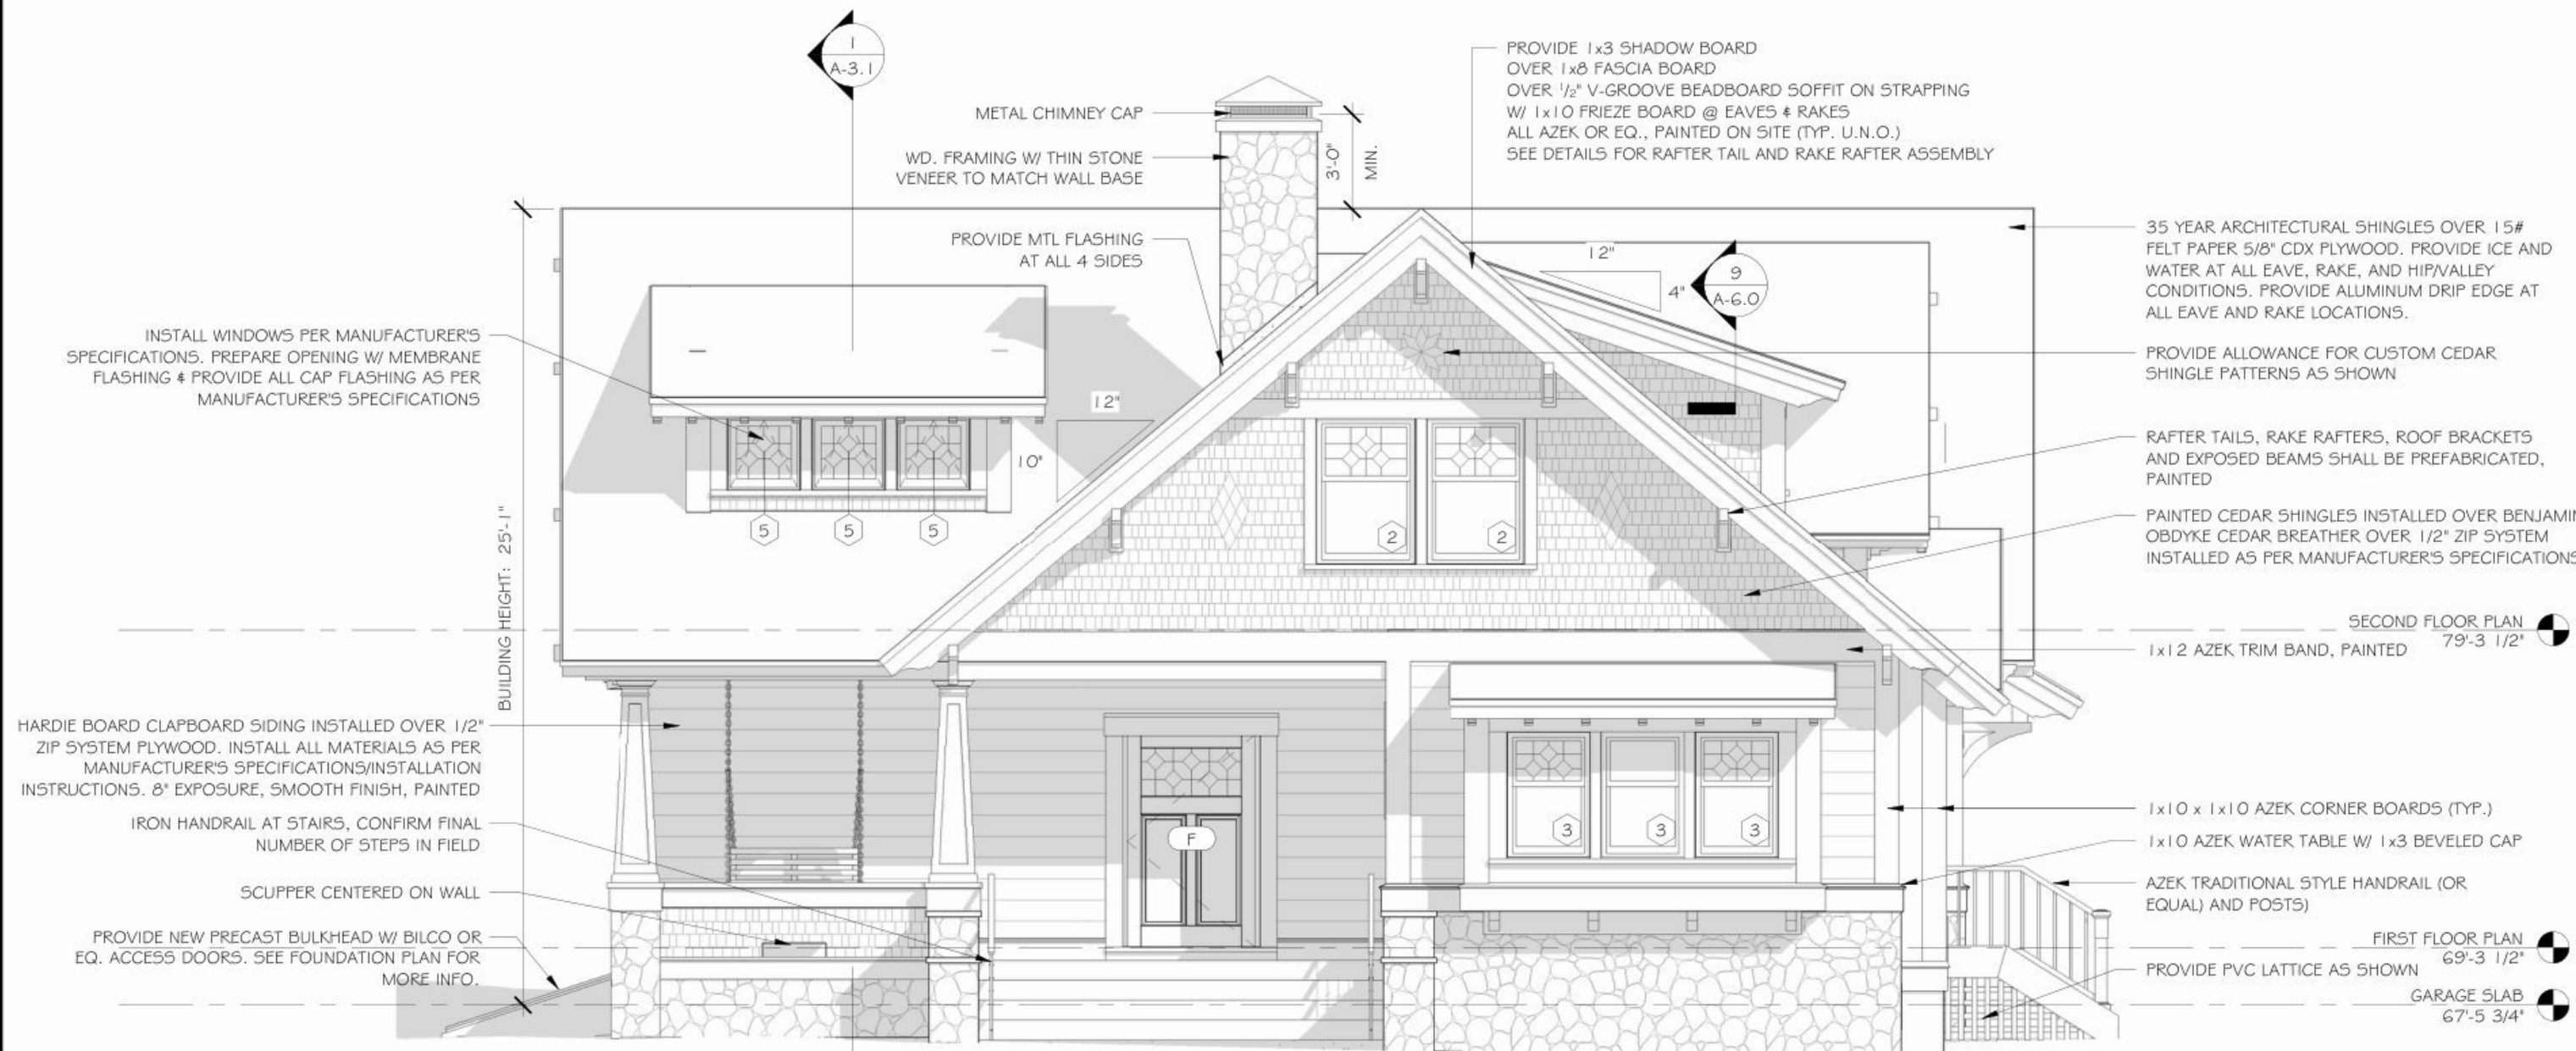

1 FRONT ELEVATION
1/4" = 1'-0"

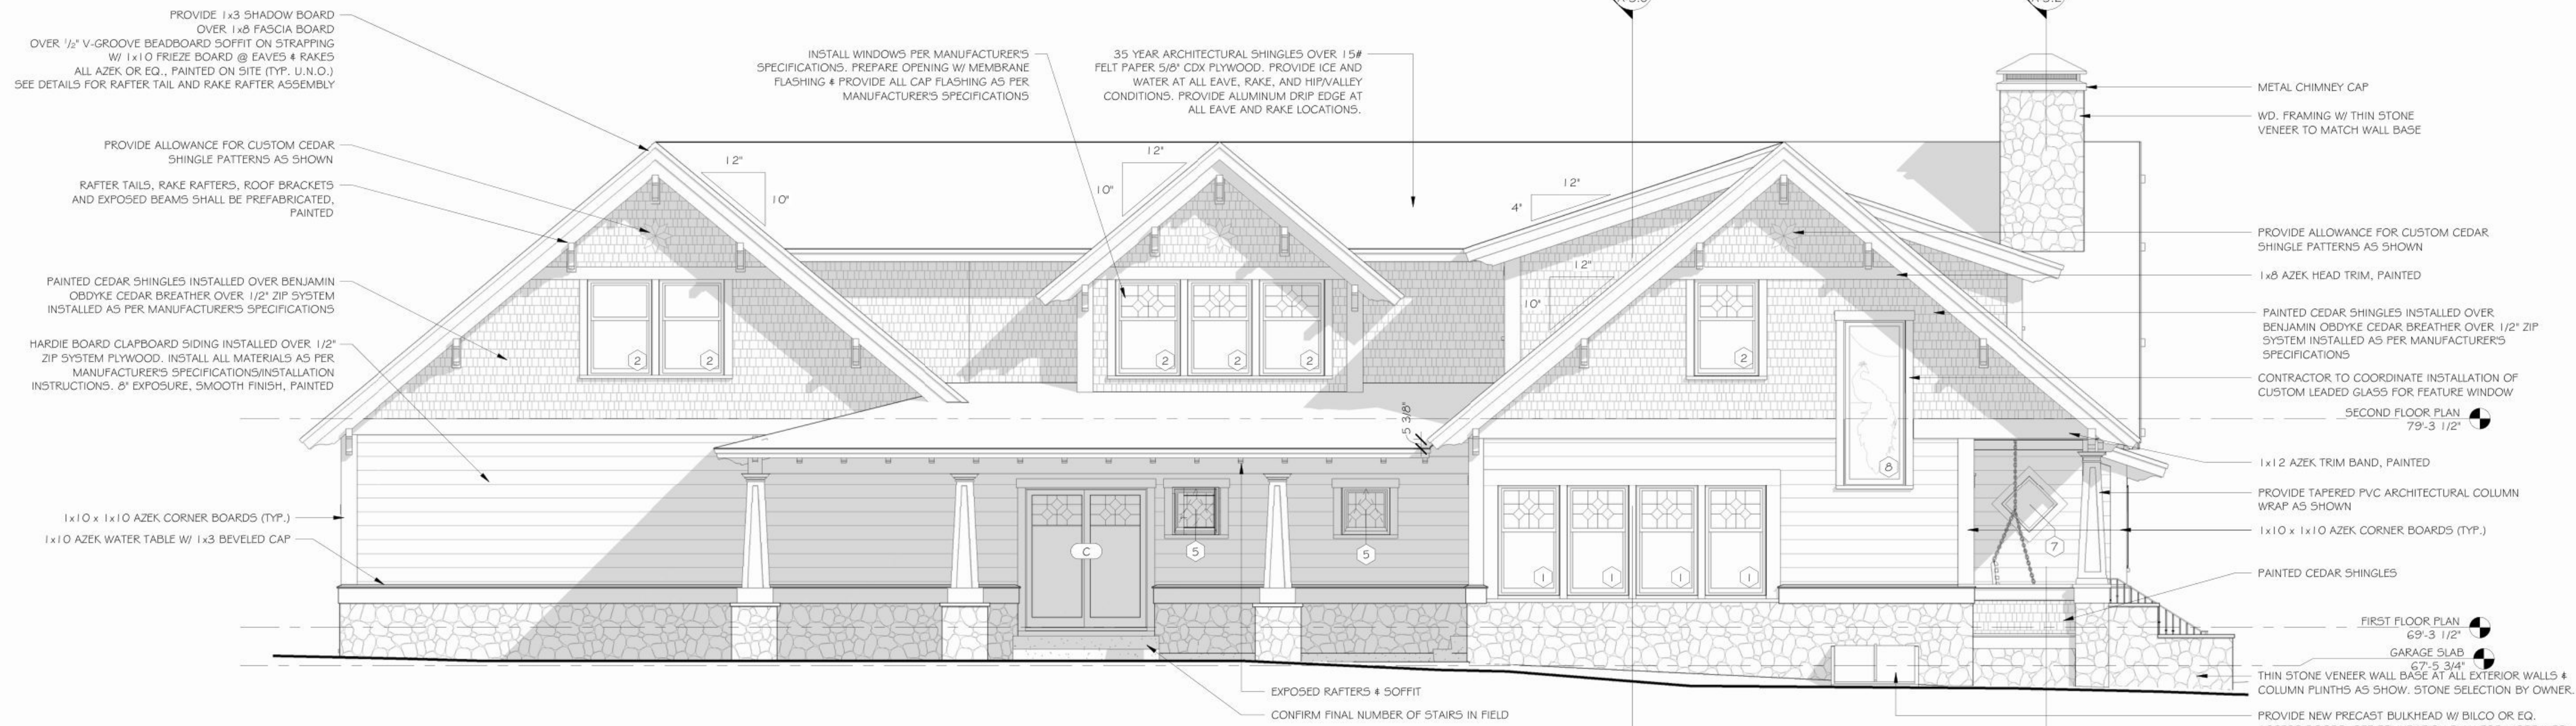

2 LEFT SIDE ELEVATION
1/4" = 1'-0"

ROUGH HEAD HEIGHT WINDOW SCHEDULE - ANDERSEN							
DES	MANUFACTURER	MODEL	LINE	ROUGH WIDTH	ROUGH HEIGHT	ROUGH HEAD HEIGHT	REMARKS
1	Andersen Corporation	ADH3054	A-Series Double Hung	3'-0"	5'-4"	6'-10 1/2"	CUSTOM ART GLASS PATTERN
2	Andersen Corporation	ADH3248	A-Series Double Hung	3'-2"	4'-8"	6'-9"	CUSTOM ART GLASS PATTERN
3	Andersen Corporation	ADH2840	A-Series Double Hung	2'-8"	4'-0"	6'-10 1/2"	CUSTOM ART GLASS PATTERN
4	Andersen Corporation	AAN3430	A-Series Awning	3'-4"	3'-0"	6'-10 1/2"	CUSTOM ART GLASS PATTERN
5	Andersen Corporation	AAN2424	A-Series Awning	2'-4"	2'-4"	6'-8 1/2"	CUSTOM ART GLASS PATTERN
7	Andersen Corporation		DIAMOND WINDOW			<varies>	STAINED GLASS INSERT - BY OWNER
8	Andersen Corporation	APW3080	A-Series Picture Window	3'-0"	8'-0"	14'-8 3/4"	STAINED GLASS INSERT - BY OWNER
9	Andersen Corporation	AAN3430	A-Series Awning	3'-4"	3'-0"	7'-0 3/4"	
10	Andersen Corporation	APW2424	A-Series Picture Window	2'-4"	2'-4"	6'-8 1/8"	FIXED INTERIOR UNITS
15	Andersen Corporation	APW5048	A-Series Picture Window	5'-0"	4'-8"	6'-8 1/4"	CUSTOM ART GLASS PATTERN

DOOR SCHEDULE					
DES.	MANUFACTURER	MODEL	ROUGH WIDTH	ROUGH HEIGHT	REMARKS
A	Simpsons Door Company	77662	3'-4"	6'-10 1/2"	
B	Simpsons Door Company	77662	3'-4"	6'-10 1/2"	
C	Andersen Corporation	6080	6'-0"	6'-10 1/2"	CUSTOM GRILLE PATTERN - SEE ELEVATIONS
D	BY SUBMITTAL	-	10'-6"	8'-1 1/2"	GARAGE DOOR
E	Andersen Corporation	6080	6'-0"	6'-10 1/2"	INTERIOR FRENCH DOORS
F	Simpsons Door Company	TBD	4'-4"	6'-10 1/2"	

- NOTE:
- ALL WINDOW FINISH HEADER HEIGHTS ARE 6'-8" @ FIRST & SECOND FLOOR UNLESS OTHERWISE SPECIFIED.
- CONTRACTOR SHALL VERIFY SCHEDULE W/ OWNER PRIOR TO CONSTRUCTION
 - VERIFY UNIT CLEAR OPENING WITH MANUFACTURER & THAT THE OPENING SHALL COMPLY WITH CMR 3603.10.4
 - PROVIDE TEMPERED GLASS AS REQUIRED BY CODE
 - ALL WINDOWS SHALL HAVE UV PROTECTION
 - ALL HARDWARE TO BE OIL-RUBBED BRONZE
 - SUBMIT WINDOW ORDER & SAMPLE TO OWNER
 - WINDOW SCHEDULE IS BASED UPON THE ANDERSEN A- SERIES. SEE ELEVATION NOTES FOR ADDITIONAL INFO.

Revisions/Project Status		
Issue	Date	Issue Description