


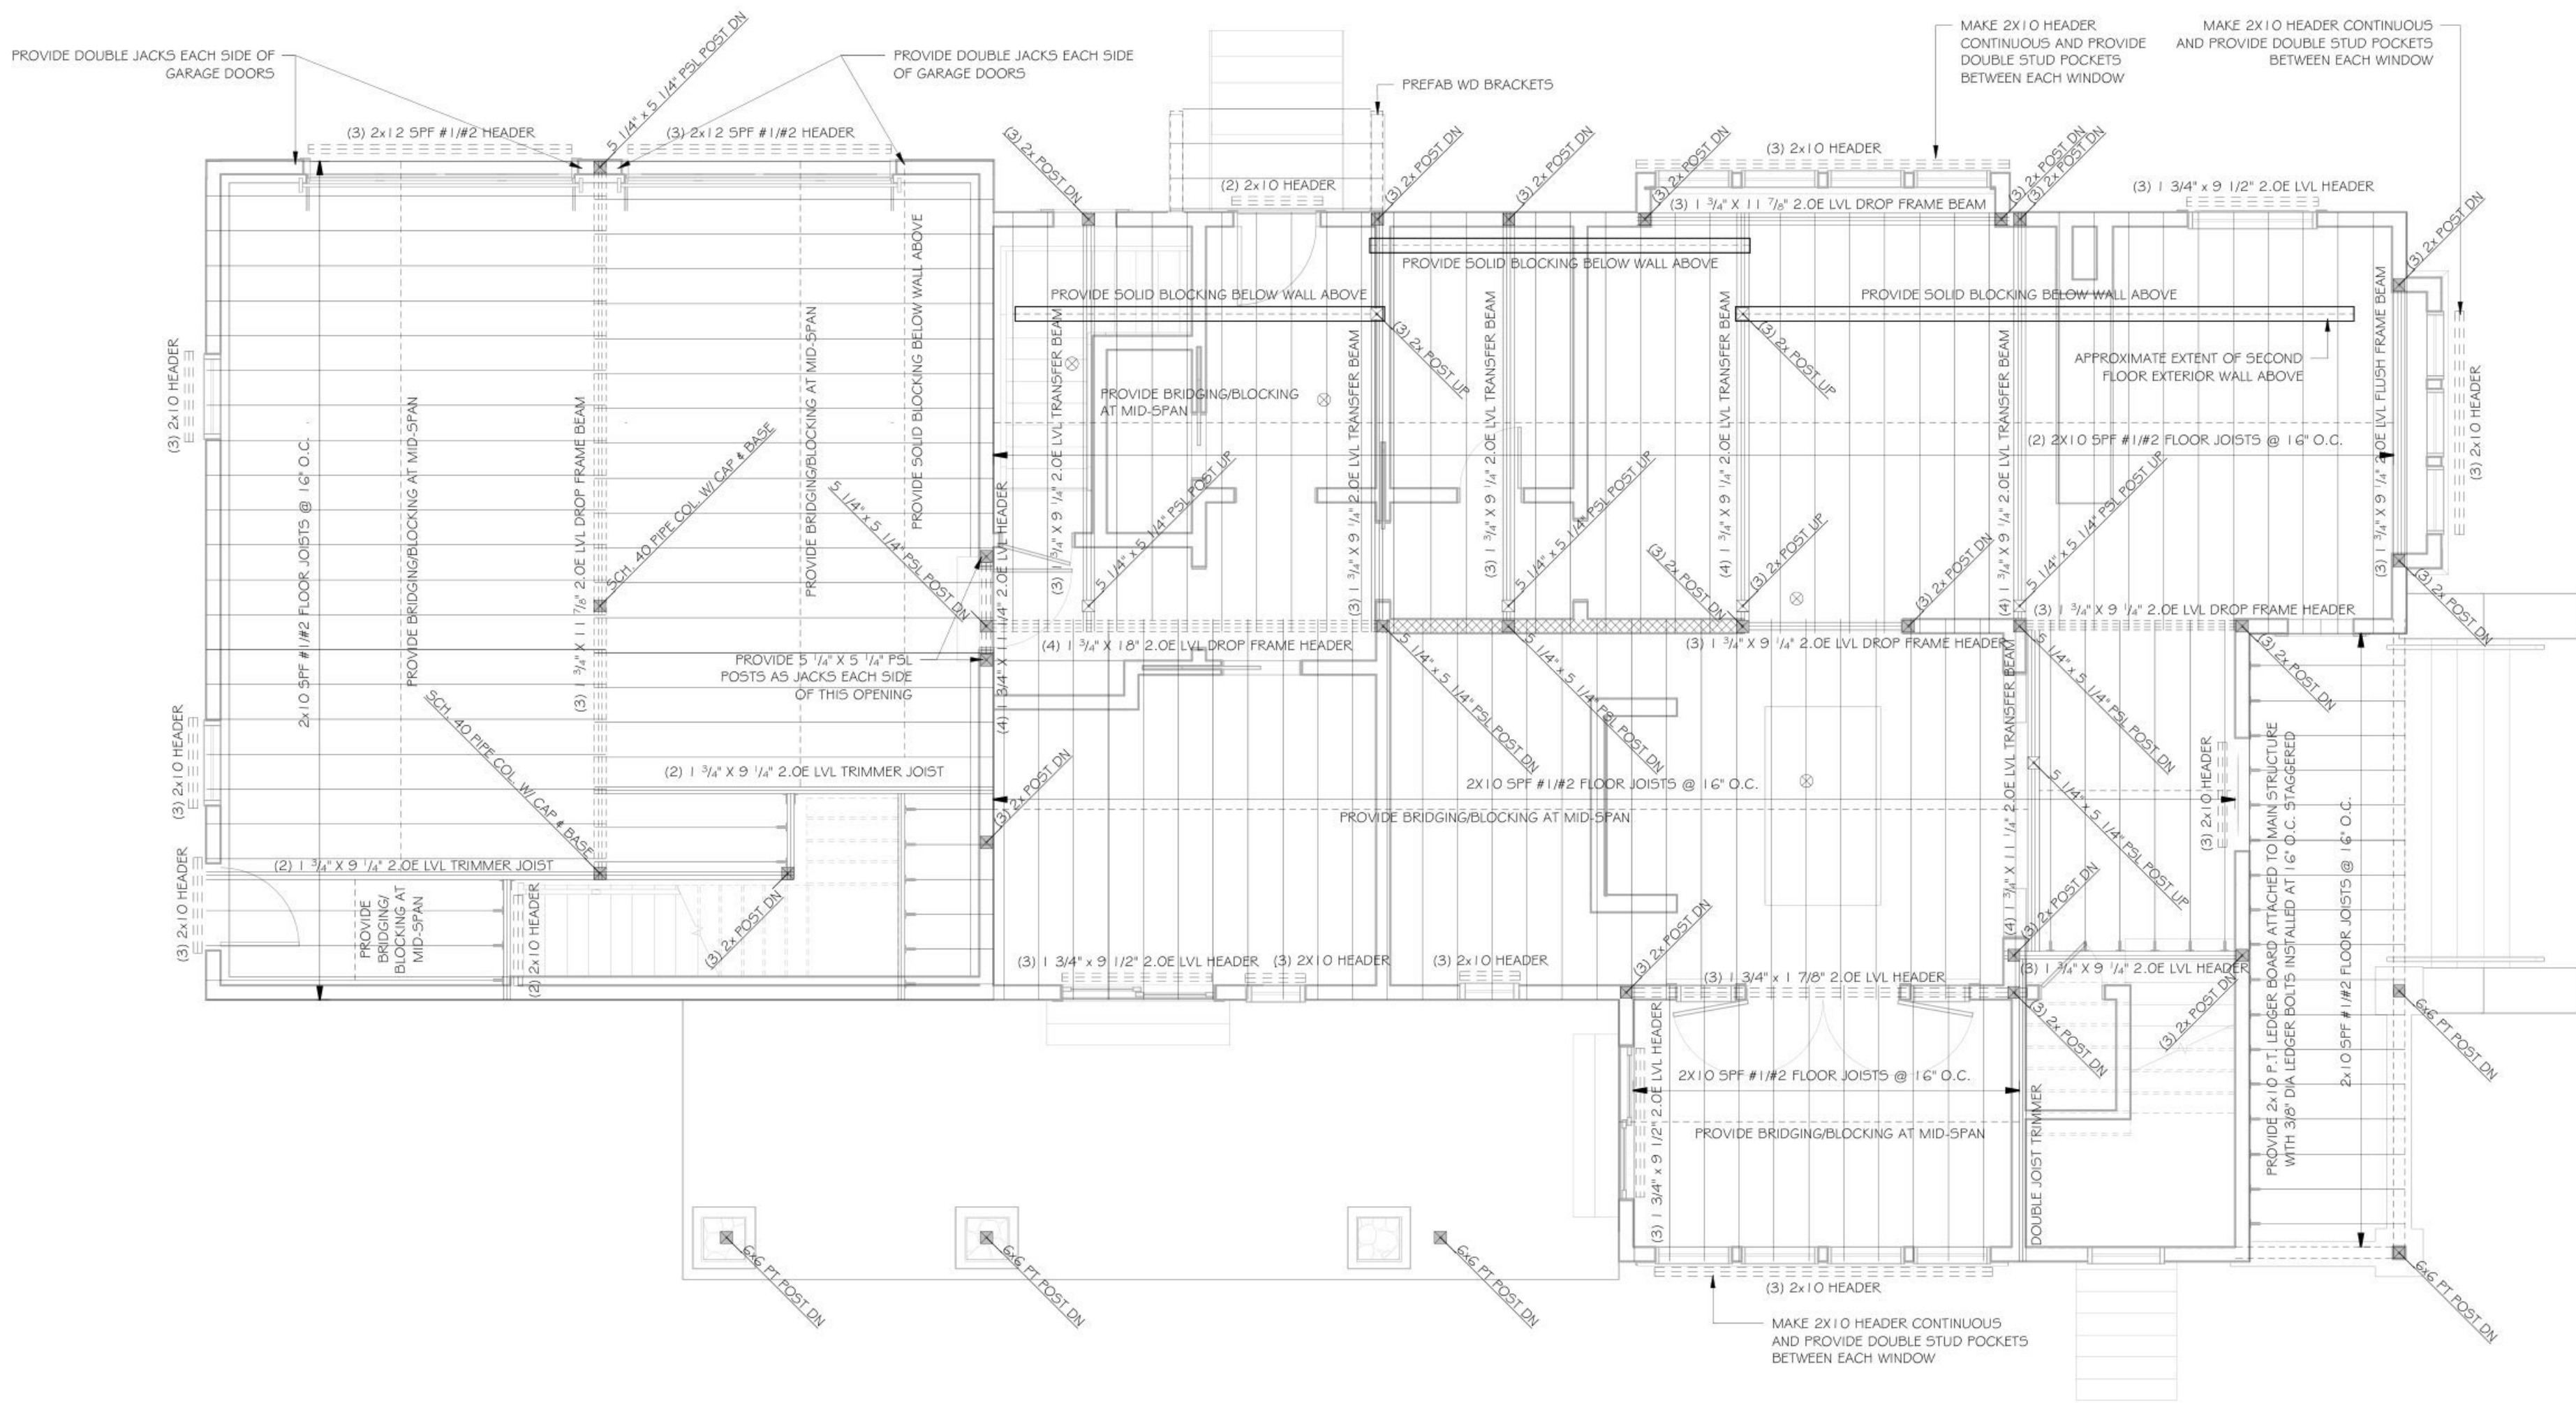

TYP. FLOOR FRAMING NOTES

1. NEW 4" AND 5" SLABS ON GRADE IS TO BE REINFORCED WITH 6 x 6 W2.0W2.0 WELDED WIRE FABRIC.
2. FOOTINGS ARE TO BE BEAR 4'-0" MIN. BELOW FINISH GRADE ON 2 TSF BEARING CAPACITY SOILS. SOIL BEARING CONDITIONS AND CAPACITY ARE TO BE VERIFIED DURING CONSTRUCTION.
3. PROVIDE PERFORATED PVC PERIMETER DRAIN IN CRUSHED STONE SURROUND WITH FILTER FABRIC PROTECTION IF APPLICABLE.
4. FOUNDATION WALLS MUST BE POURED MONOLITHICALLY. COLD JOINTS IN UNREINFORCED CONCRETE WALL ARE NOT ACCEPTABLE, AND SHALL BE REMOVED IF THEY OCCUR.
5. DO NOT BACKFILL FOUNDATION WALLS UNTIL FIRST FLOOR IS IN PLACE AND COMPLETE, NO MATTER WHAT YOUR PAST EXPERIENCE HAS BEEN.
6. PROVIDE 6" FREE DRAINING COMPACTED GRAVEL UNDER ALL NEW SLABS ON GRADE AND PROVIDE 6 MIL POLYETHYLENE VAPOR BARRIER.
7. COAT ALL STEEL BELOW GRADE WITH TWO HEAVY APPLICATIONS OF COAL-TAR EPOXY.
8. ALL EXTERIOR DECK FRAMING IS TO BE No. 2 PRESSURE TREATED SOUTHERN YELLOW PINE.
9. ALL CONNECTION HARDWARE ASSOCIATED WITH THE DECK FRAMING INCLUDING HANGERS, BOLTS, AND NAILS IS TO BE HOT DIPPED GALVANIZED OR STAINLESS STEEL. IF STAINLESS STEEL, VERIFY STEEL COMPATIBILITY WITH PRESERVATIVE TREATED WOOD.
10. SEE DRAWINGS SO FOR GENERAL NOTES, AND SKS DRAWINGS FOR SECTIONS AND DETAILS.
11. ALL NEW FLOOR DECKING IS 3/4" INCH APA SPAN-RATED PLYWOOD GLUED AND NAILED.
12. LVL - INDICATES LAMINATED VENEER LUMBER
13. PSL - INDICATES PARALLEL STRANDED LUMBER
14. NEW OUTSIDE WALLS ARE 2x6 AT 16" ON CENTER STUD BEARING WALLS BLOCKED AT MIDHEIGHT
15. ALL FLUSH-FRAMED CONNECTIONS ARE TO HAVE STEEL HANGERS, AND ALL POST TO BEAM CONNECTIONS SHALL HAVE STEEL POST CAPS. SUBMIT COMPLETE SCHEDULE OF ALL HANGERS, SELECTED FOR END REACTIONS INDICATED (EXAMPLE: 2.0k = 2000#) IN PLAN, FOR REVIEW AND APPROVAL. IMPROVISED CONNECTIONS ARE NOT PERMITTED, AND REMEDIAL DESIGN WORK TO CORRECT UNAPPROVED DEFICIENT CONNECTIONS SHALL BE PAID FOR BY THE CONTRACTOR.

FLOOR DESIGN LOADS:

- LIVE LOAD 40 PSF TYPICAL FLOOR FRAMING
- 40 PSF BALCONY/DECK

GRAPHICS LEGEND

- INDICATES POST UP
- INDICATES POST DOWN. FOR POSTS UP & DN, CONTINUE POST SIZE FROM LEVEL ABOVE UNLESS OTHERWISE NOTED
- INDICATES 2x6 @ 16" O.C. INTERIOR STUD BEARING WALL, TYP. U.O.N.
- INDICATES DRAIN LINE