



MYLES
NELSON
McKENZIE
DESIGN



Telephone: 949-683-6895
Email: info@mylesmckenzie.com
Web: www.mylesmckenzie.com

These drawings documents and specifications are an instrument of service, copyright and the property of MYLES NELSON MCKENZIE DESIGN and shall not be used or reproduced in any part or whole, except by written agreement with the Architect or Designer of MYLES NELSON MCKENZIE DESIGN. Their use for publication shall be restricted to the original project in which they are designed for.

Written dimensions shall be verified on the job site. Any discrepancy shall be brought to notice of the Architect or Designer of MYLES NELSON MCKENZIE DESIGN prior to the commencement of any construction.

These plans have been reviewed and approved by:

A NEW CUSTOM HOME DESIGN FOR:
MESECHER - CLOUTREAU
RESIDENCE
LOT 2221, BLOCK 104, RIVERBEND
BLUFFTON TOWNSHIP, SC

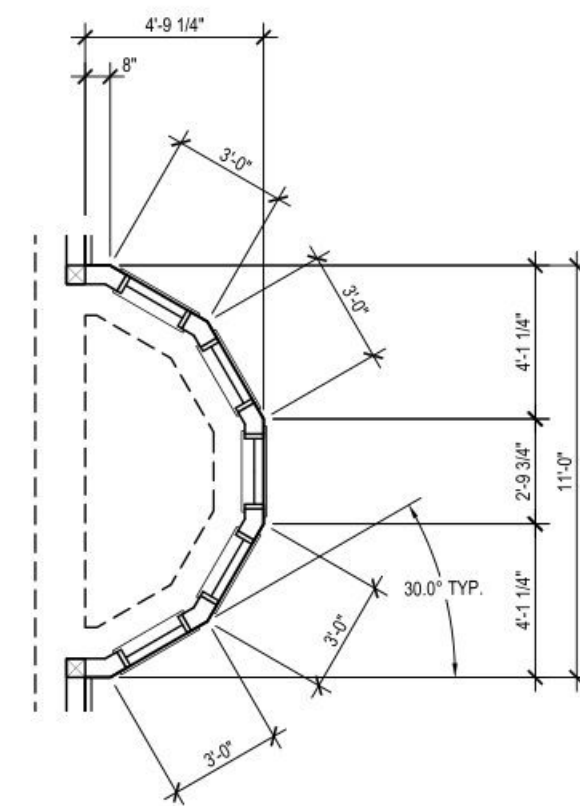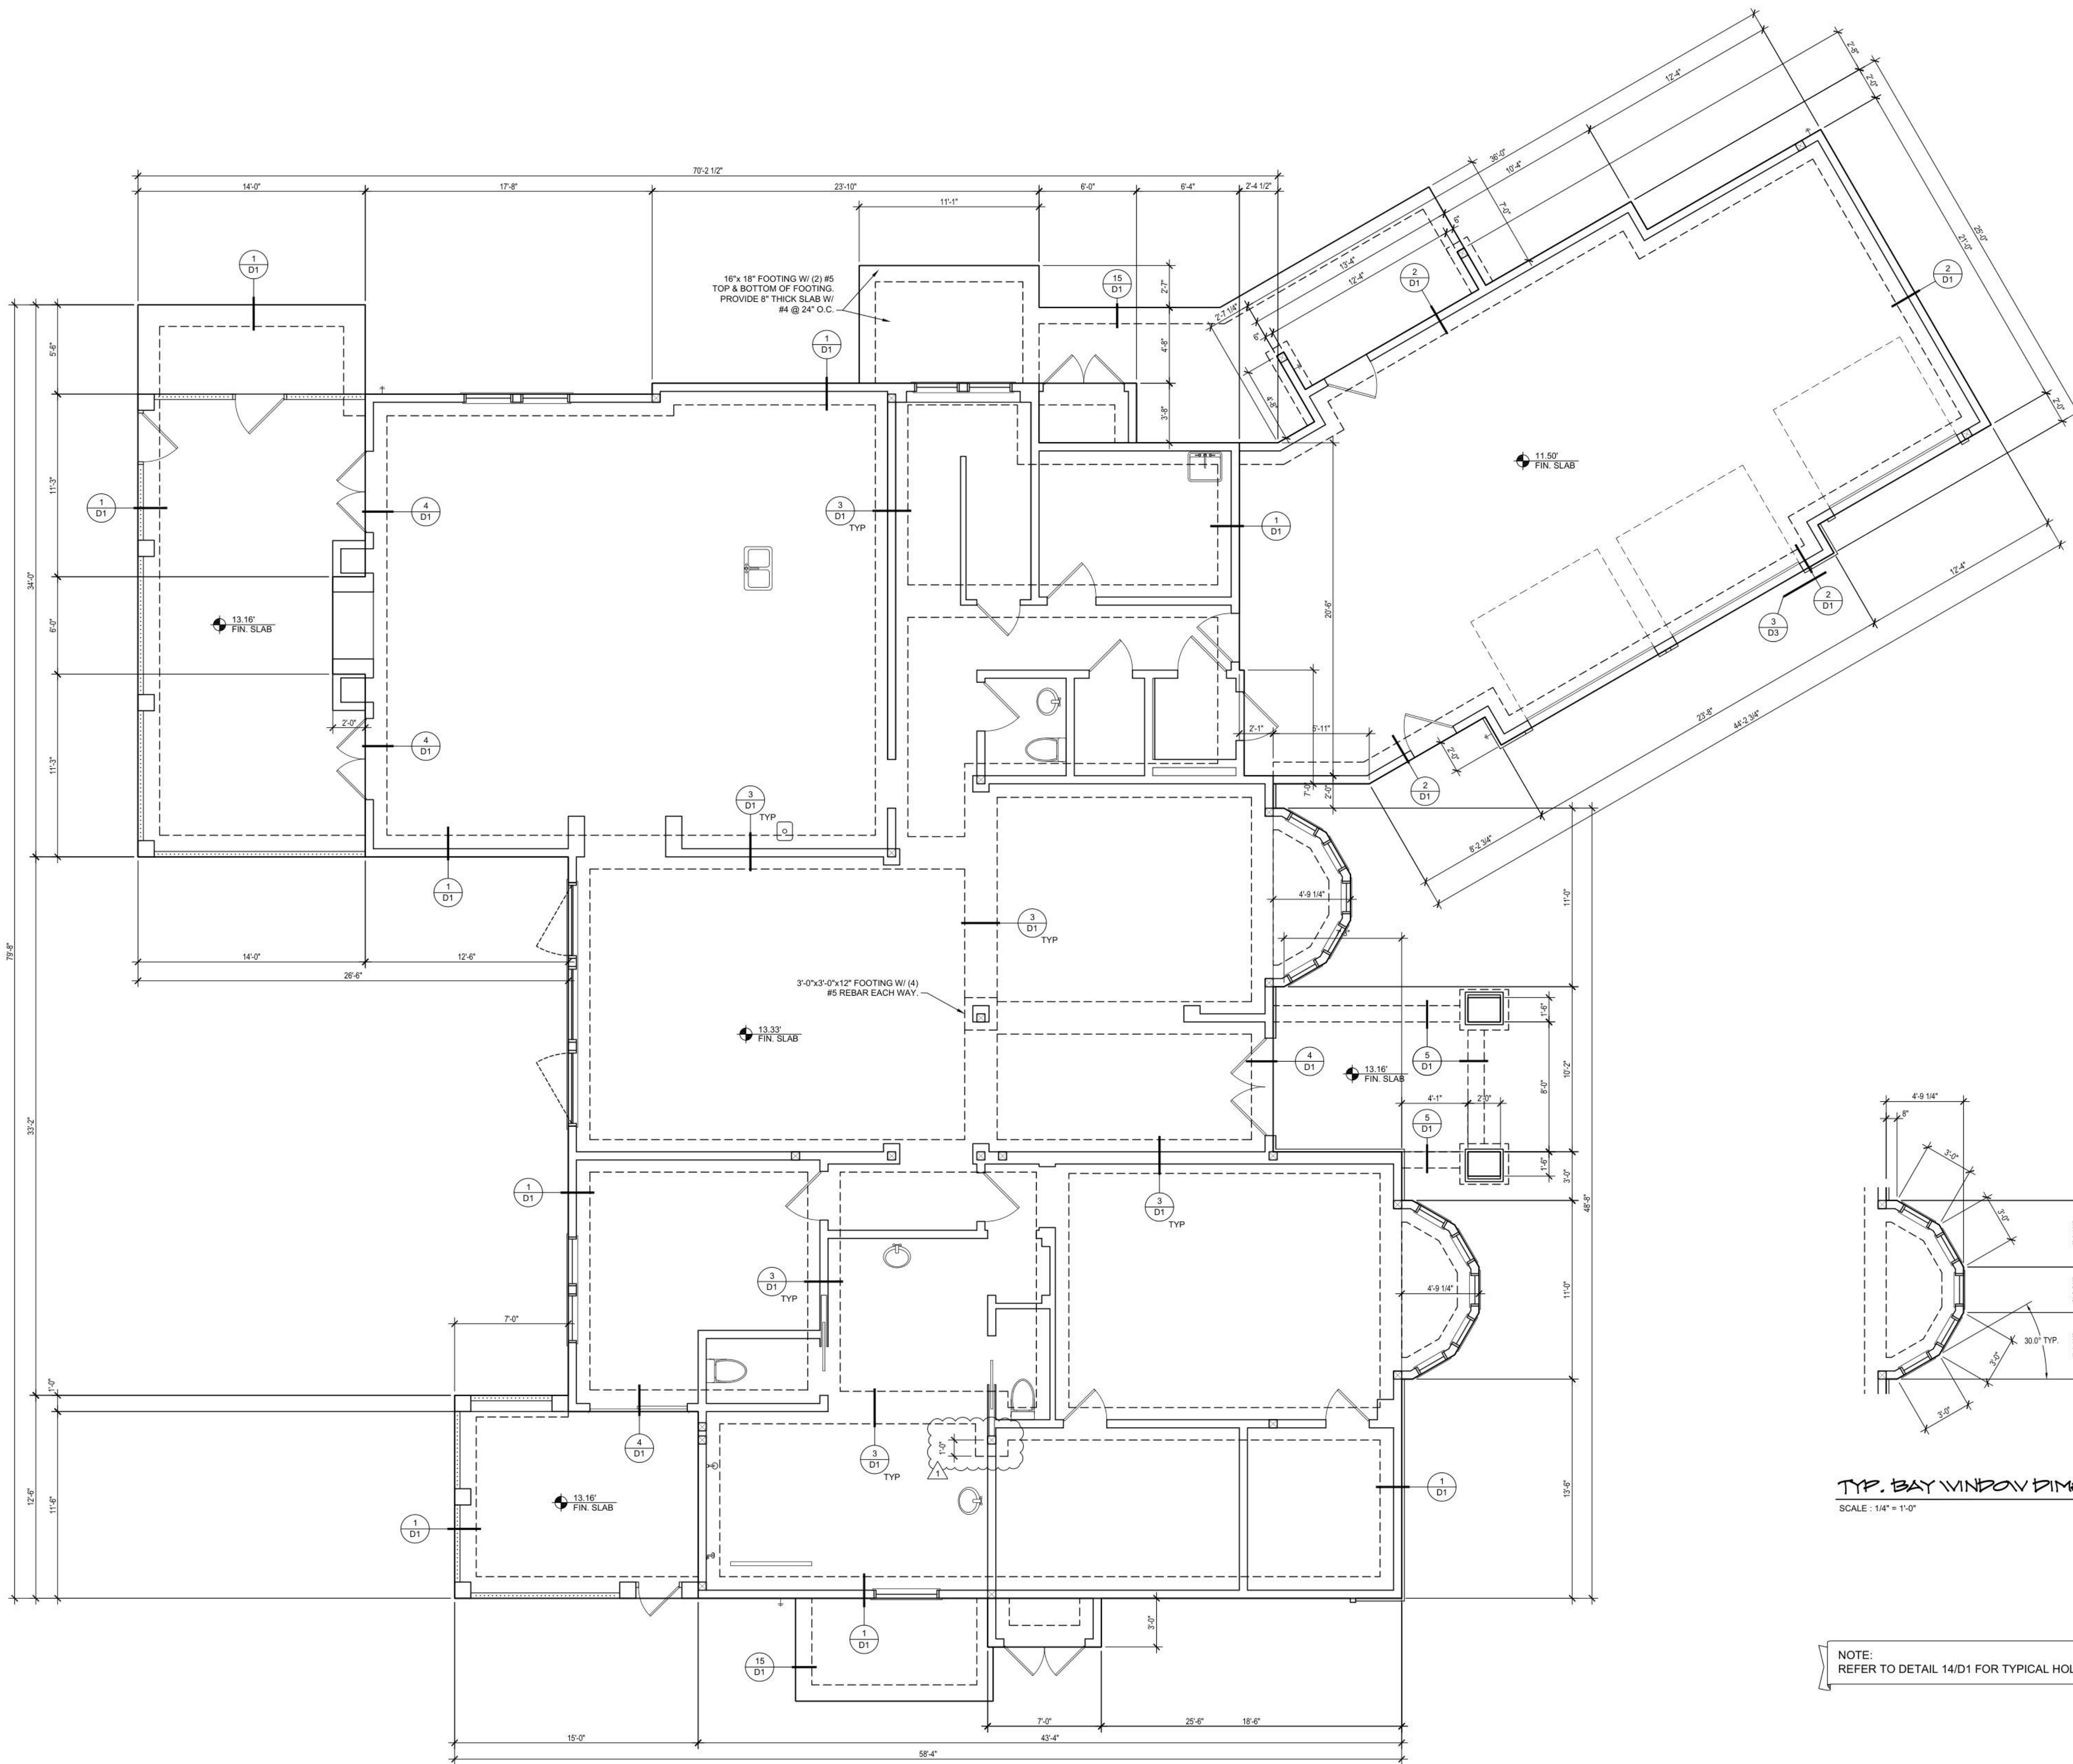

TYP. BAY WINDOW DIMENSIONS
SCALE: 1/4" = 1'-0"

NOTE:
REFER TO DETAIL 14/D1 FOR TYPICAL HOLDOWN DETAILS.



Project

Number	Date	Description
1	8/5/22	STRUCTURAL OWNER

Revisions
Issue Date 5/17/20
Plot Date 8/9/22
FOUNDATION PLAN

Sheet

S1