

GENERAL NOTES:

A. ALL BEAMS ARE (2) 1-3/4"x11-7/8" 2.0E LVL, UNLESS NOTED OTHERWISE.



MYLES
NELSON
McKENZIE
DESIGN


Telephone: 949-683-6895
843-505-1031
Email: info@mylesmckenzie.com
Web: www.mylesmckenzie.com

These drawings documents and specifications are an instrument of service, copyright and the property of MYLES NELSON MCKENZIE DESIGN and shall not be used or reproduced in any part or whole, except by written agreement with the Architect or Designer of MYLES NELSON MCKENZIE DESIGN. Their use for publication shall be restricted to the original project in which they are designed for.

Written dimensions shall be verified on the job site. Any discrepancy shall be brought to notice of the Architect or Designer of MYLES NELSON MCKENZIE DESIGN prior to the commencement of any construction.

These plans have been reviewed and approved by:

A NEW CUSTOM HOME DESIGN FOR:
MESECHER - CLOUTREAU
RESIDENCE
LOT 2221, BLOCK 104, RIVERBEND
BLUFFTON TOWNSHIP, SC

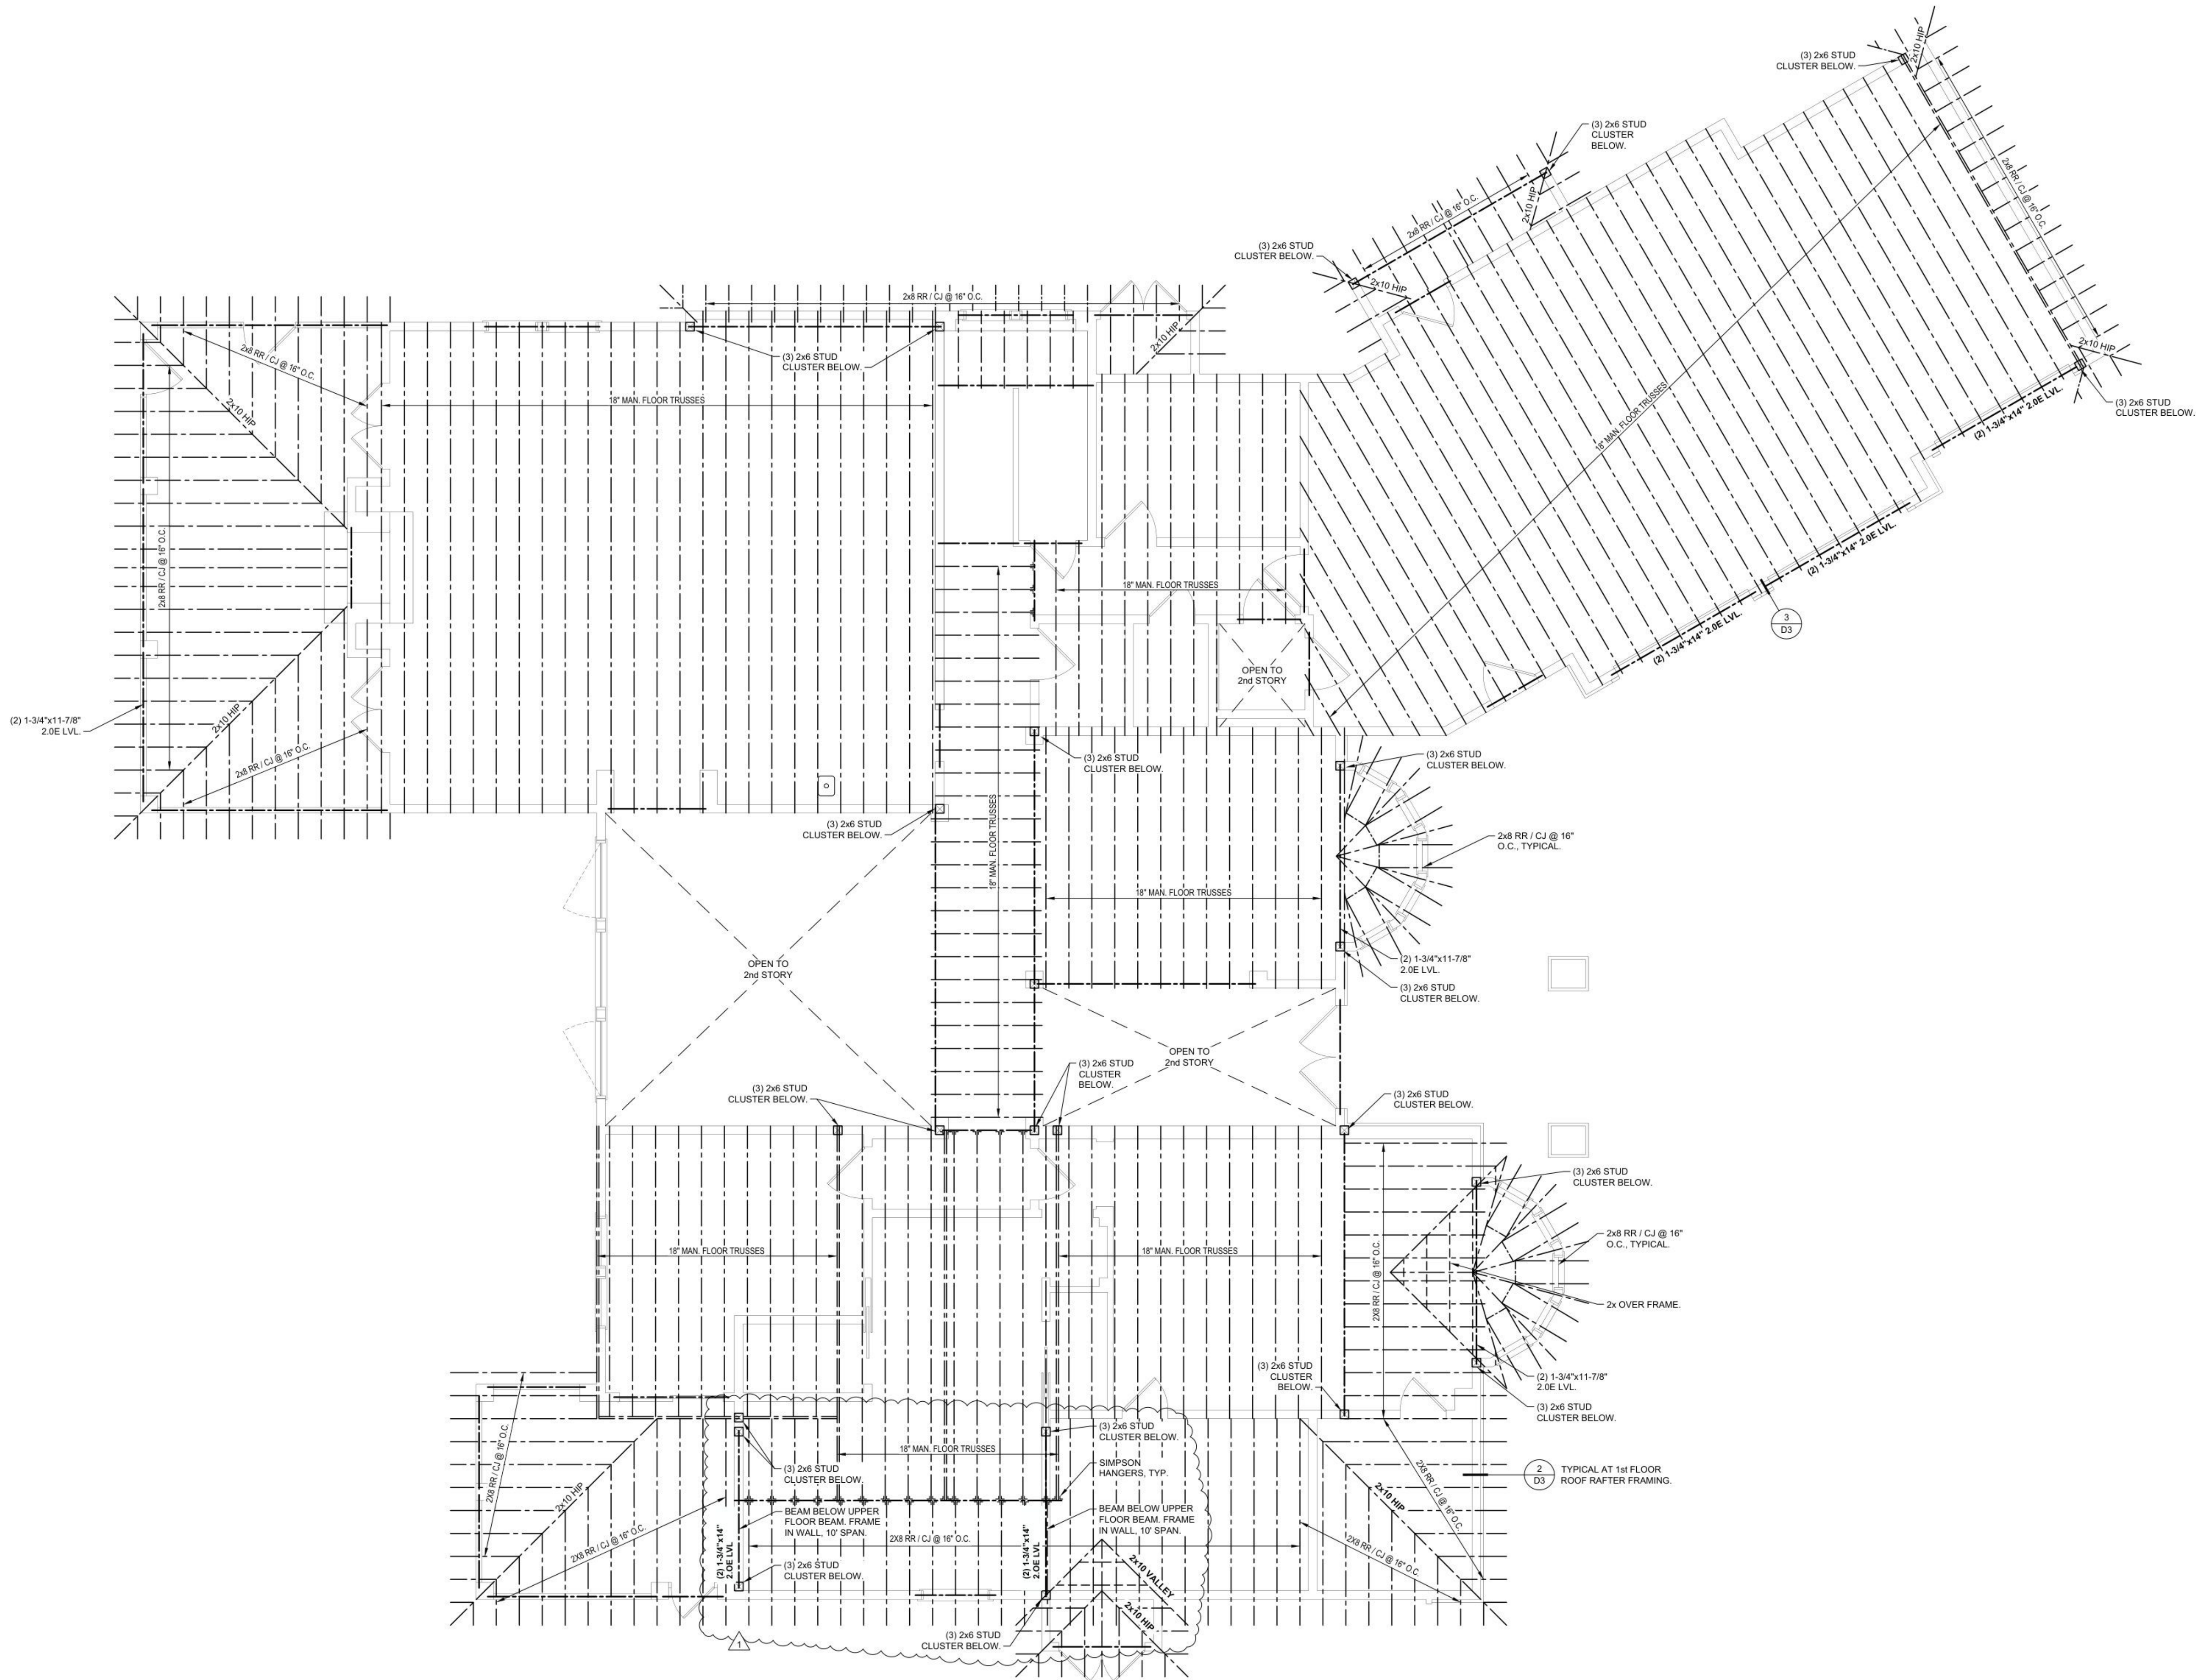

1 FRAMING PLAN - 2ND FLR & LOWER ROOF
SCALE : 1/4\" = 1'-0"



Project

Number	Date	Description
1	8/5/22	STRUCTURAL OWNER

Revisions

Issue Date 5/17/20

Plot Date 8/9/22

FRAMING PLAN - 2ND
FLOOR & LOWER ROOF

Sheet

S2