

SHEET NOTES

- SEE SHEET A-001 FOR GENERAL NOTES
- SEE SHEET A-601 FOR DOOR SCHEDULE AND TYPES
- SEE SHEET A-611 & A-613 FOR WINDOW & STOREFRONT TYPES.
- REFER TO MECHANICAL, PLUMBING, AND ELECTRICAL DRAWINGS FOR THE LOCATION OF ALL MEP WORK, INCLUDING BUT NOT LIMITED TO LIGHTS, DIFFUSERS, PIPES AND DUCTWORK.
- ELEVATIONS GIVEN ARE RELATIVE TO GROUND LEVEL T.O. SLAB (0'-0"). SEE CIVIL FOR HEIGHT ABOVE SEA LEVEL.

KEYNOTES

POND3500 Parkway Lane
Suite 500
Peachtree Corners
Georgia 30092

Copyright © 2023 by Pond & Company. All rights reserved. No copying or duplication of these documents is allowed without the expressed written agreement of Pond & Company.

EOR/AOR SEAL

100% DESIGN
SUBMITTAL - NOT FOR
CONSTRUCTION

CLIENT INFORMATION

City of Port
Wentworth Fire
Rescue

PROJECT NAME

PORT
WENTWORTH
FIRE STATION

DRAWING ISSUE

DATE

DESCRIPTION

MARK

DESIGNED BY: C.L.
DRAWN BY: C.L.
CHECKED BY: I.P.
SUBMITTED BY: M.M.
DATE: 9/08/2023
PROJECT #: 1230237

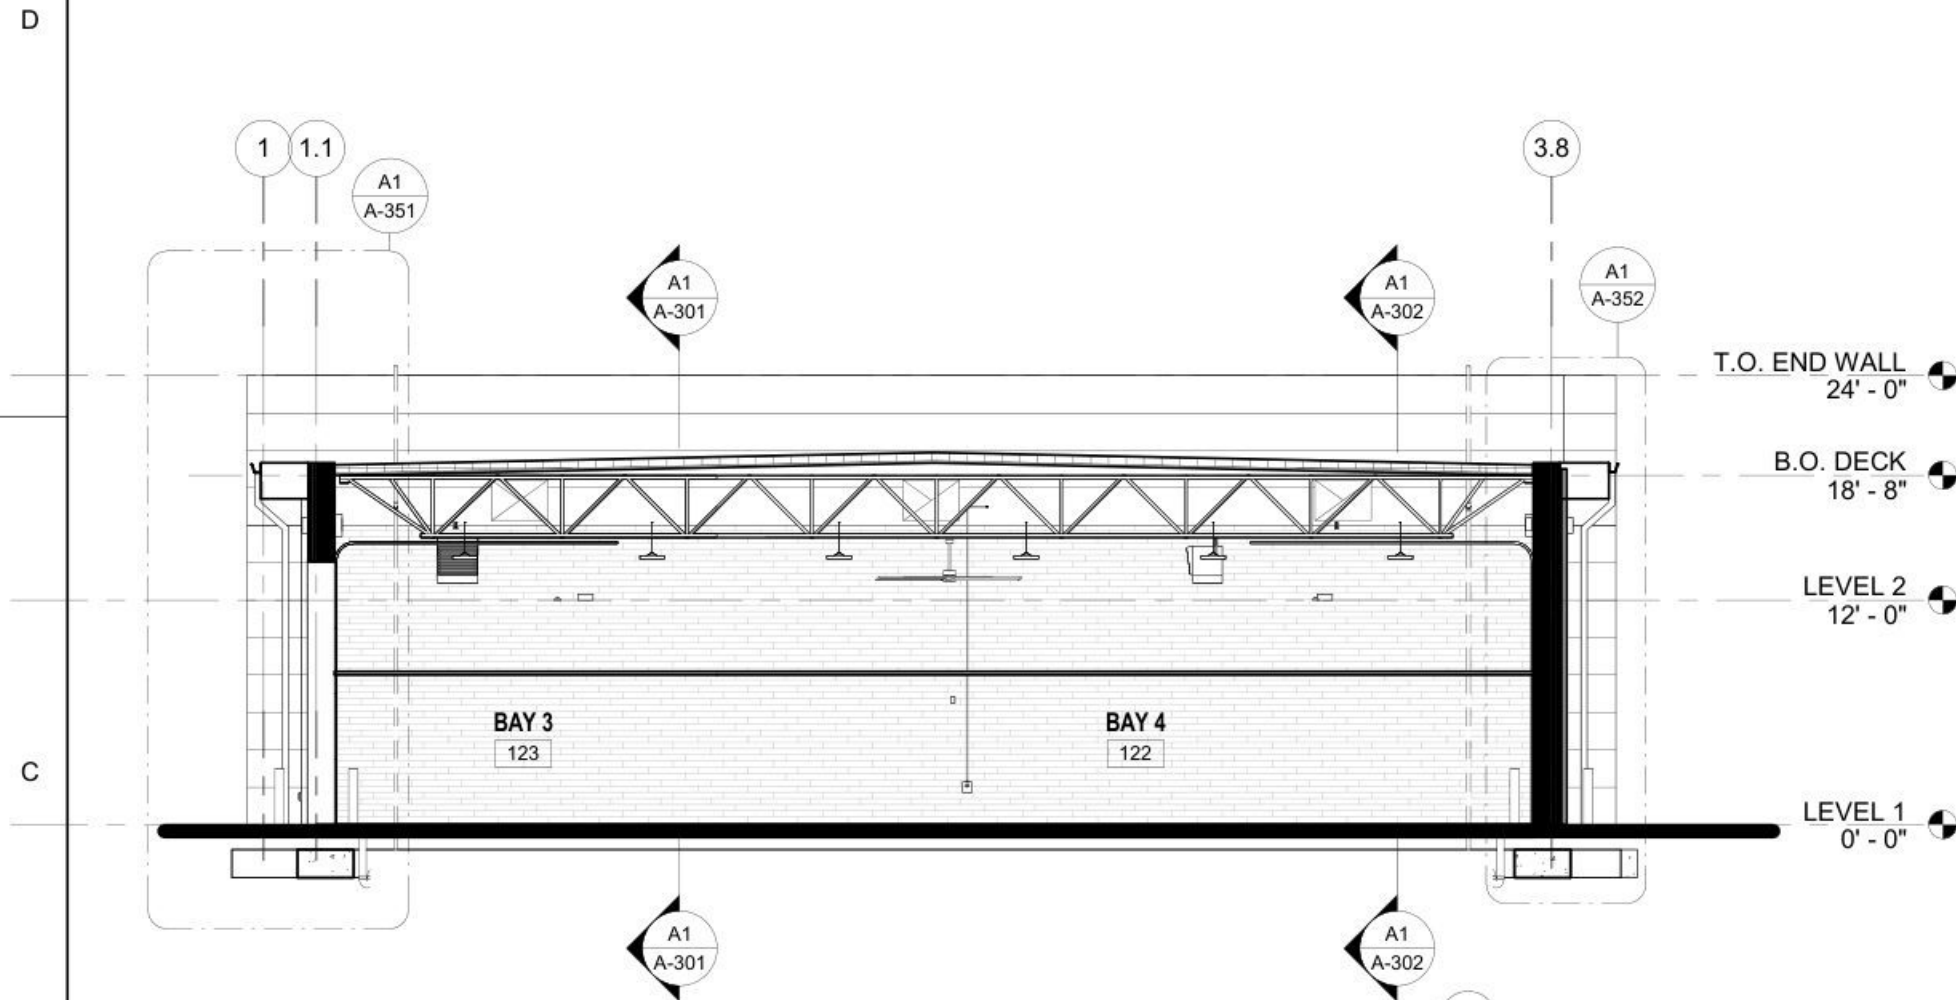
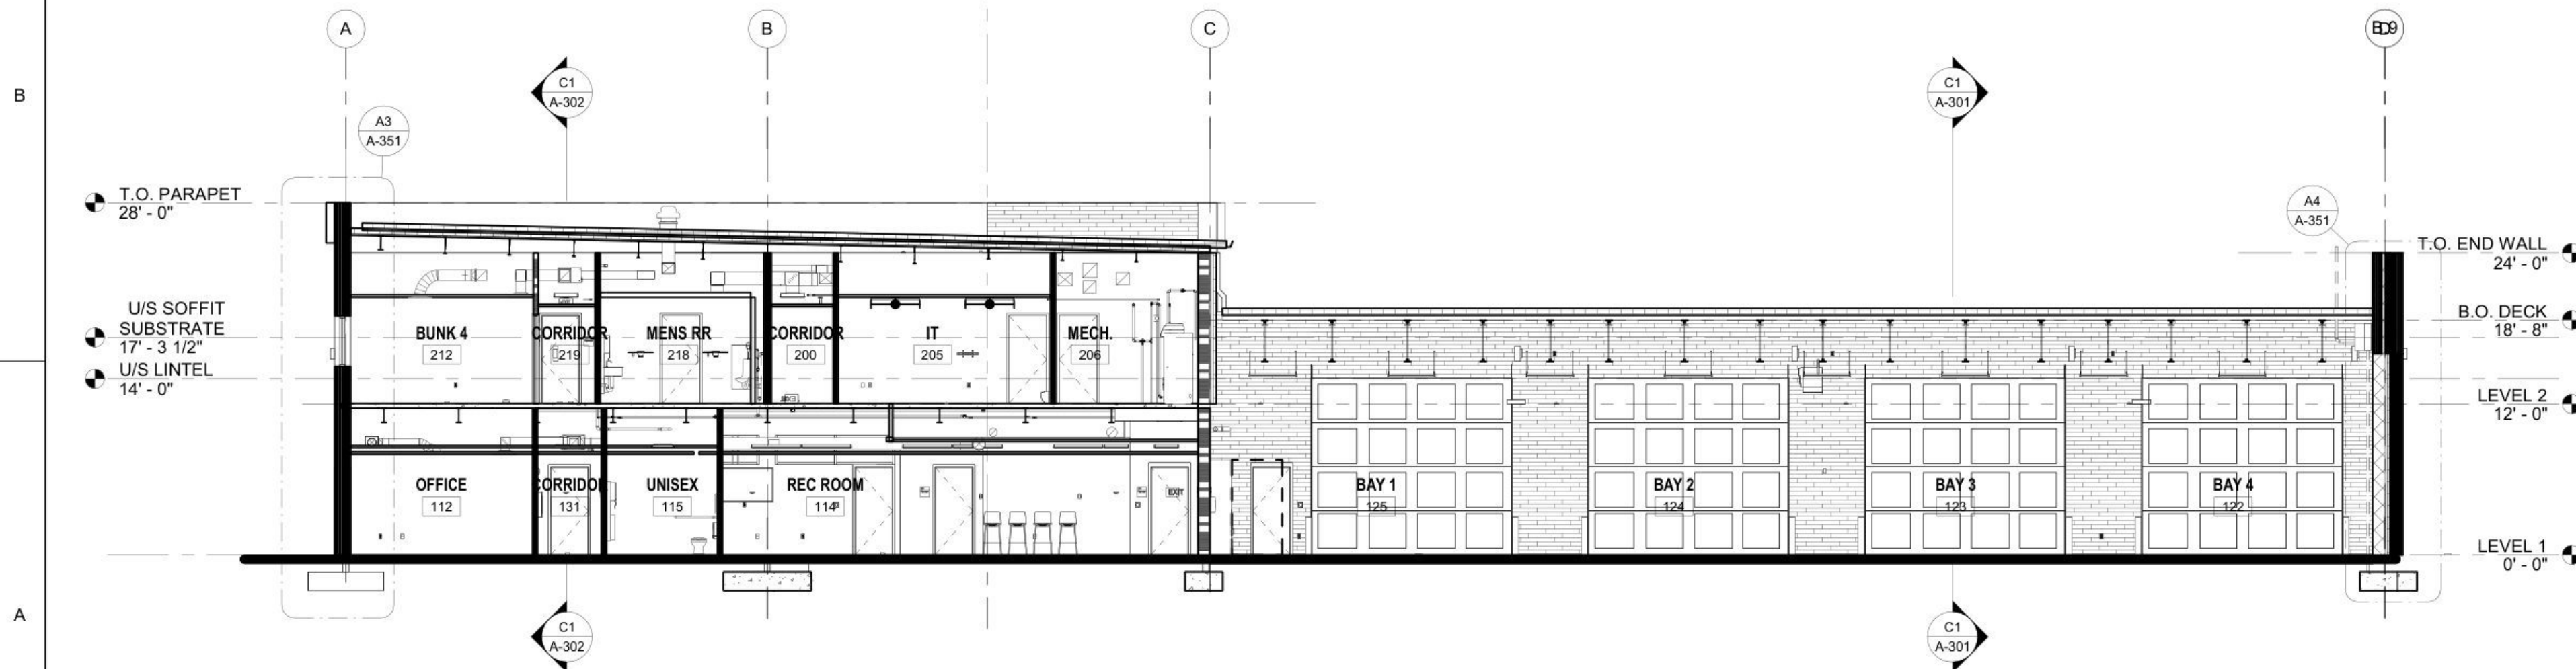
SHEET TITLE

BUILDING
SECTIONS

SHEET NUMBER

A-301ORIGINAL SHEET SIZE:
22" X 34"

100% DESIGN SUBMITTAL - NOT FOR CONSTRUCTION

**C1 BUILDING SECTION - EAST**
SCALE: 1/8" = 1'-0"**A1 BUILDING SECTION - NORTH**
SCALE: 1/8" = 1'-0"0 4' 8' 16'
SCALE: 1/8" = 1'-0"