
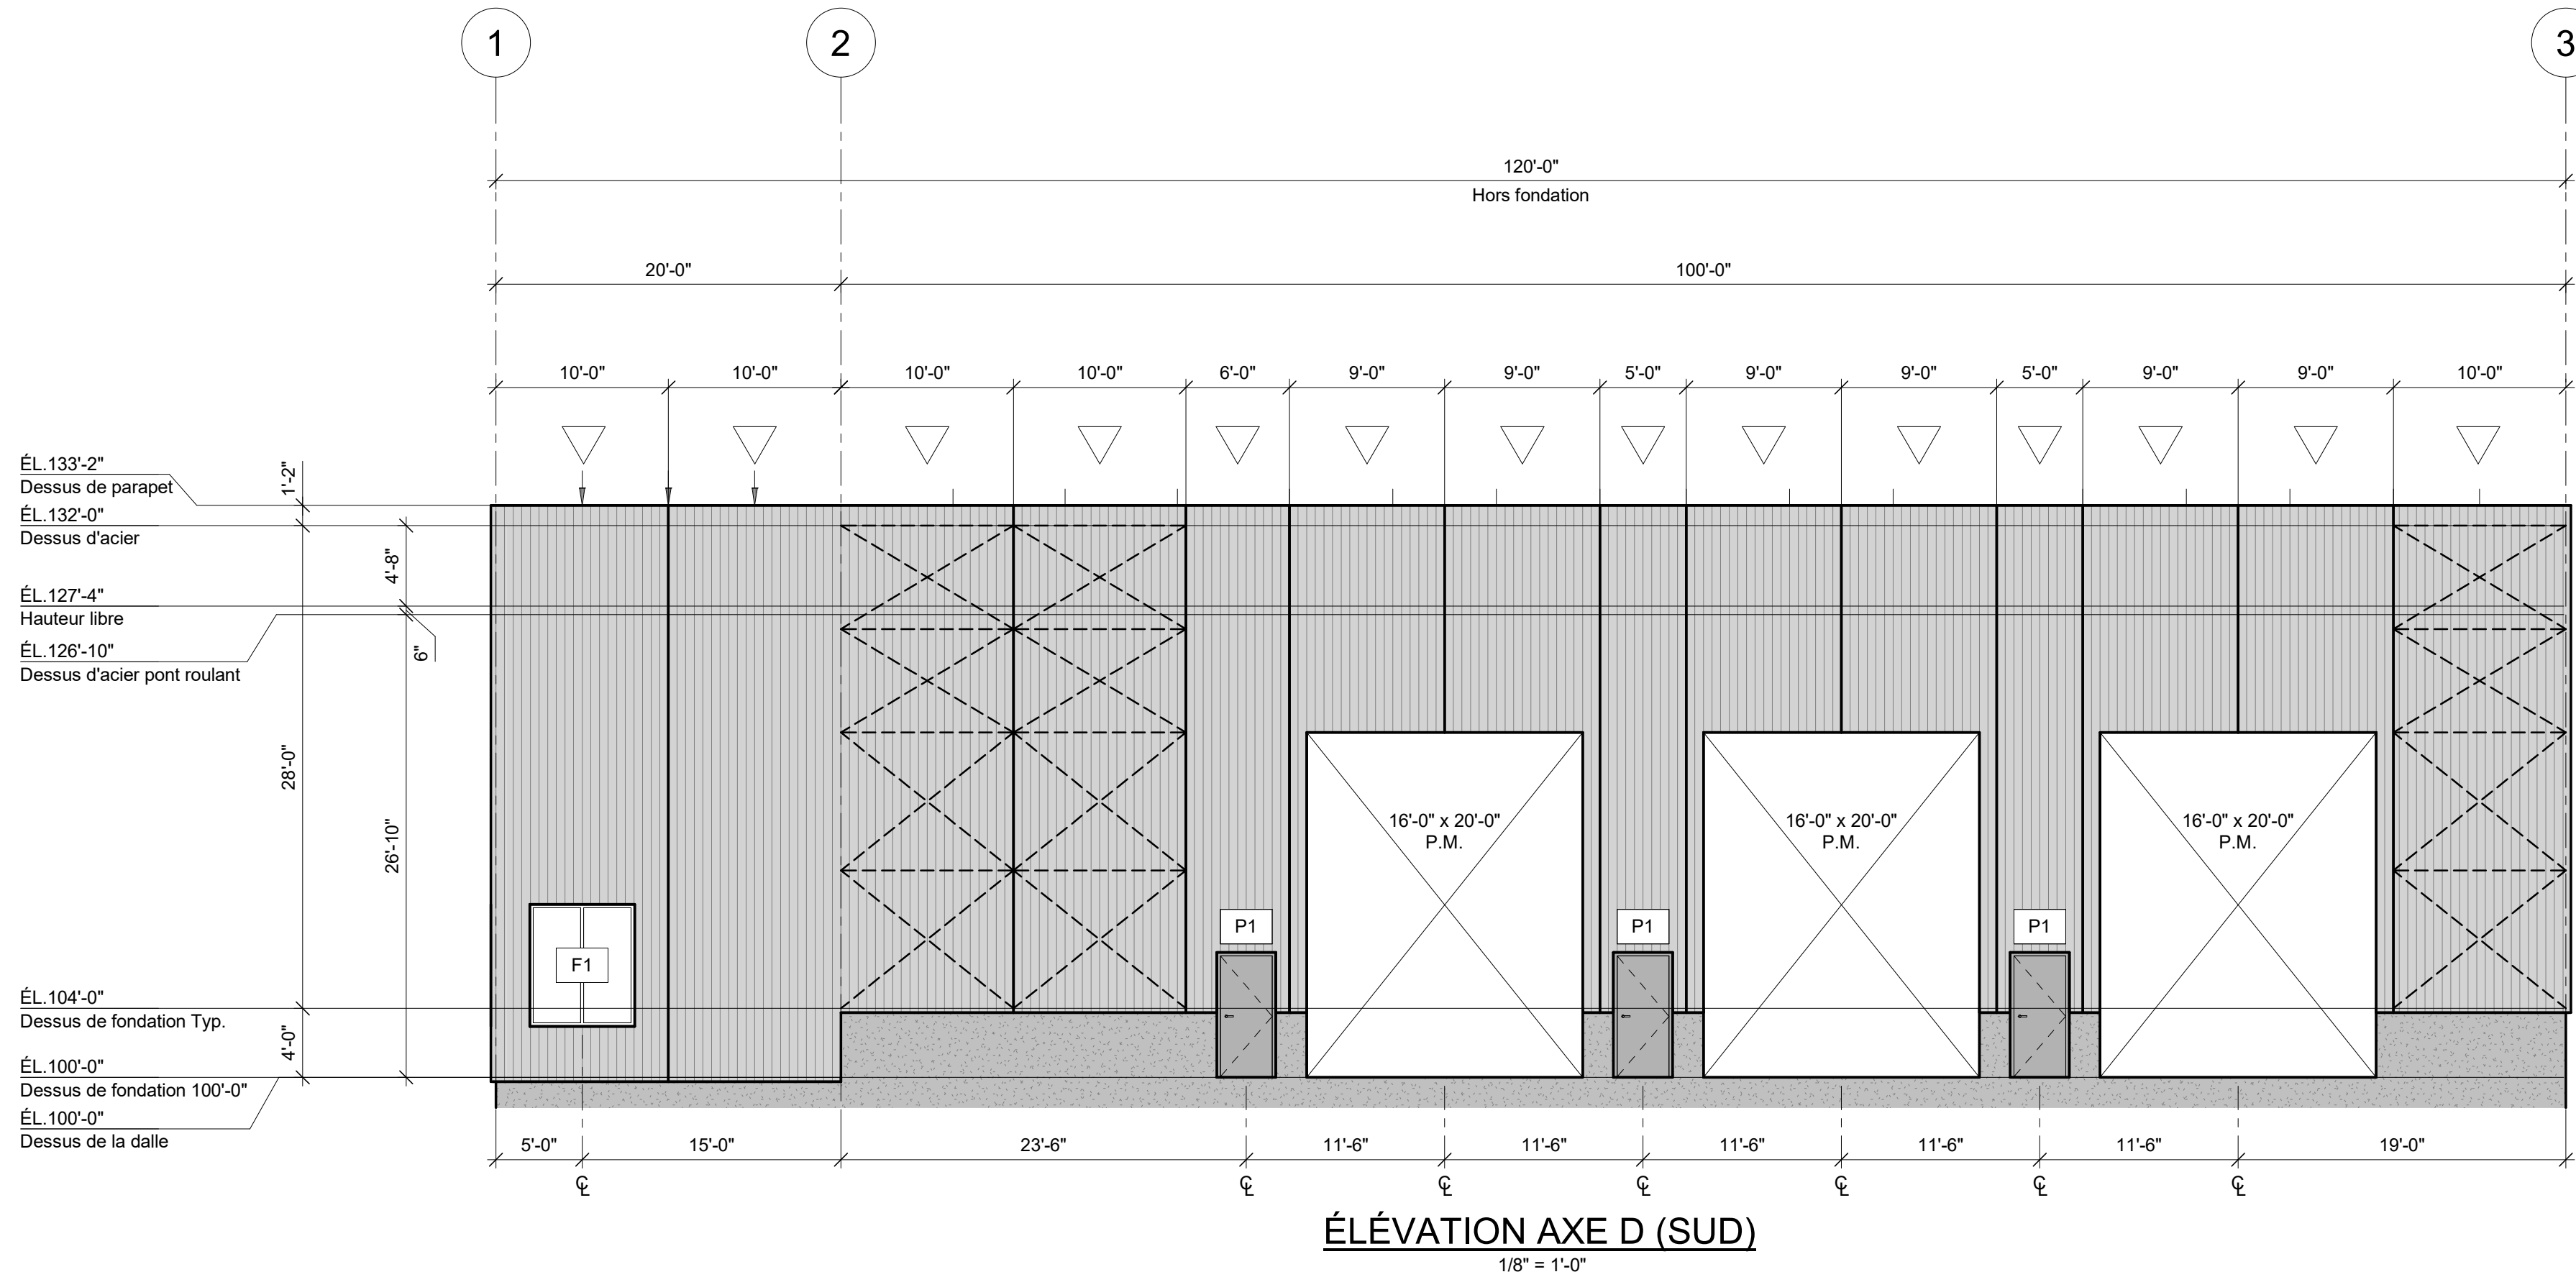
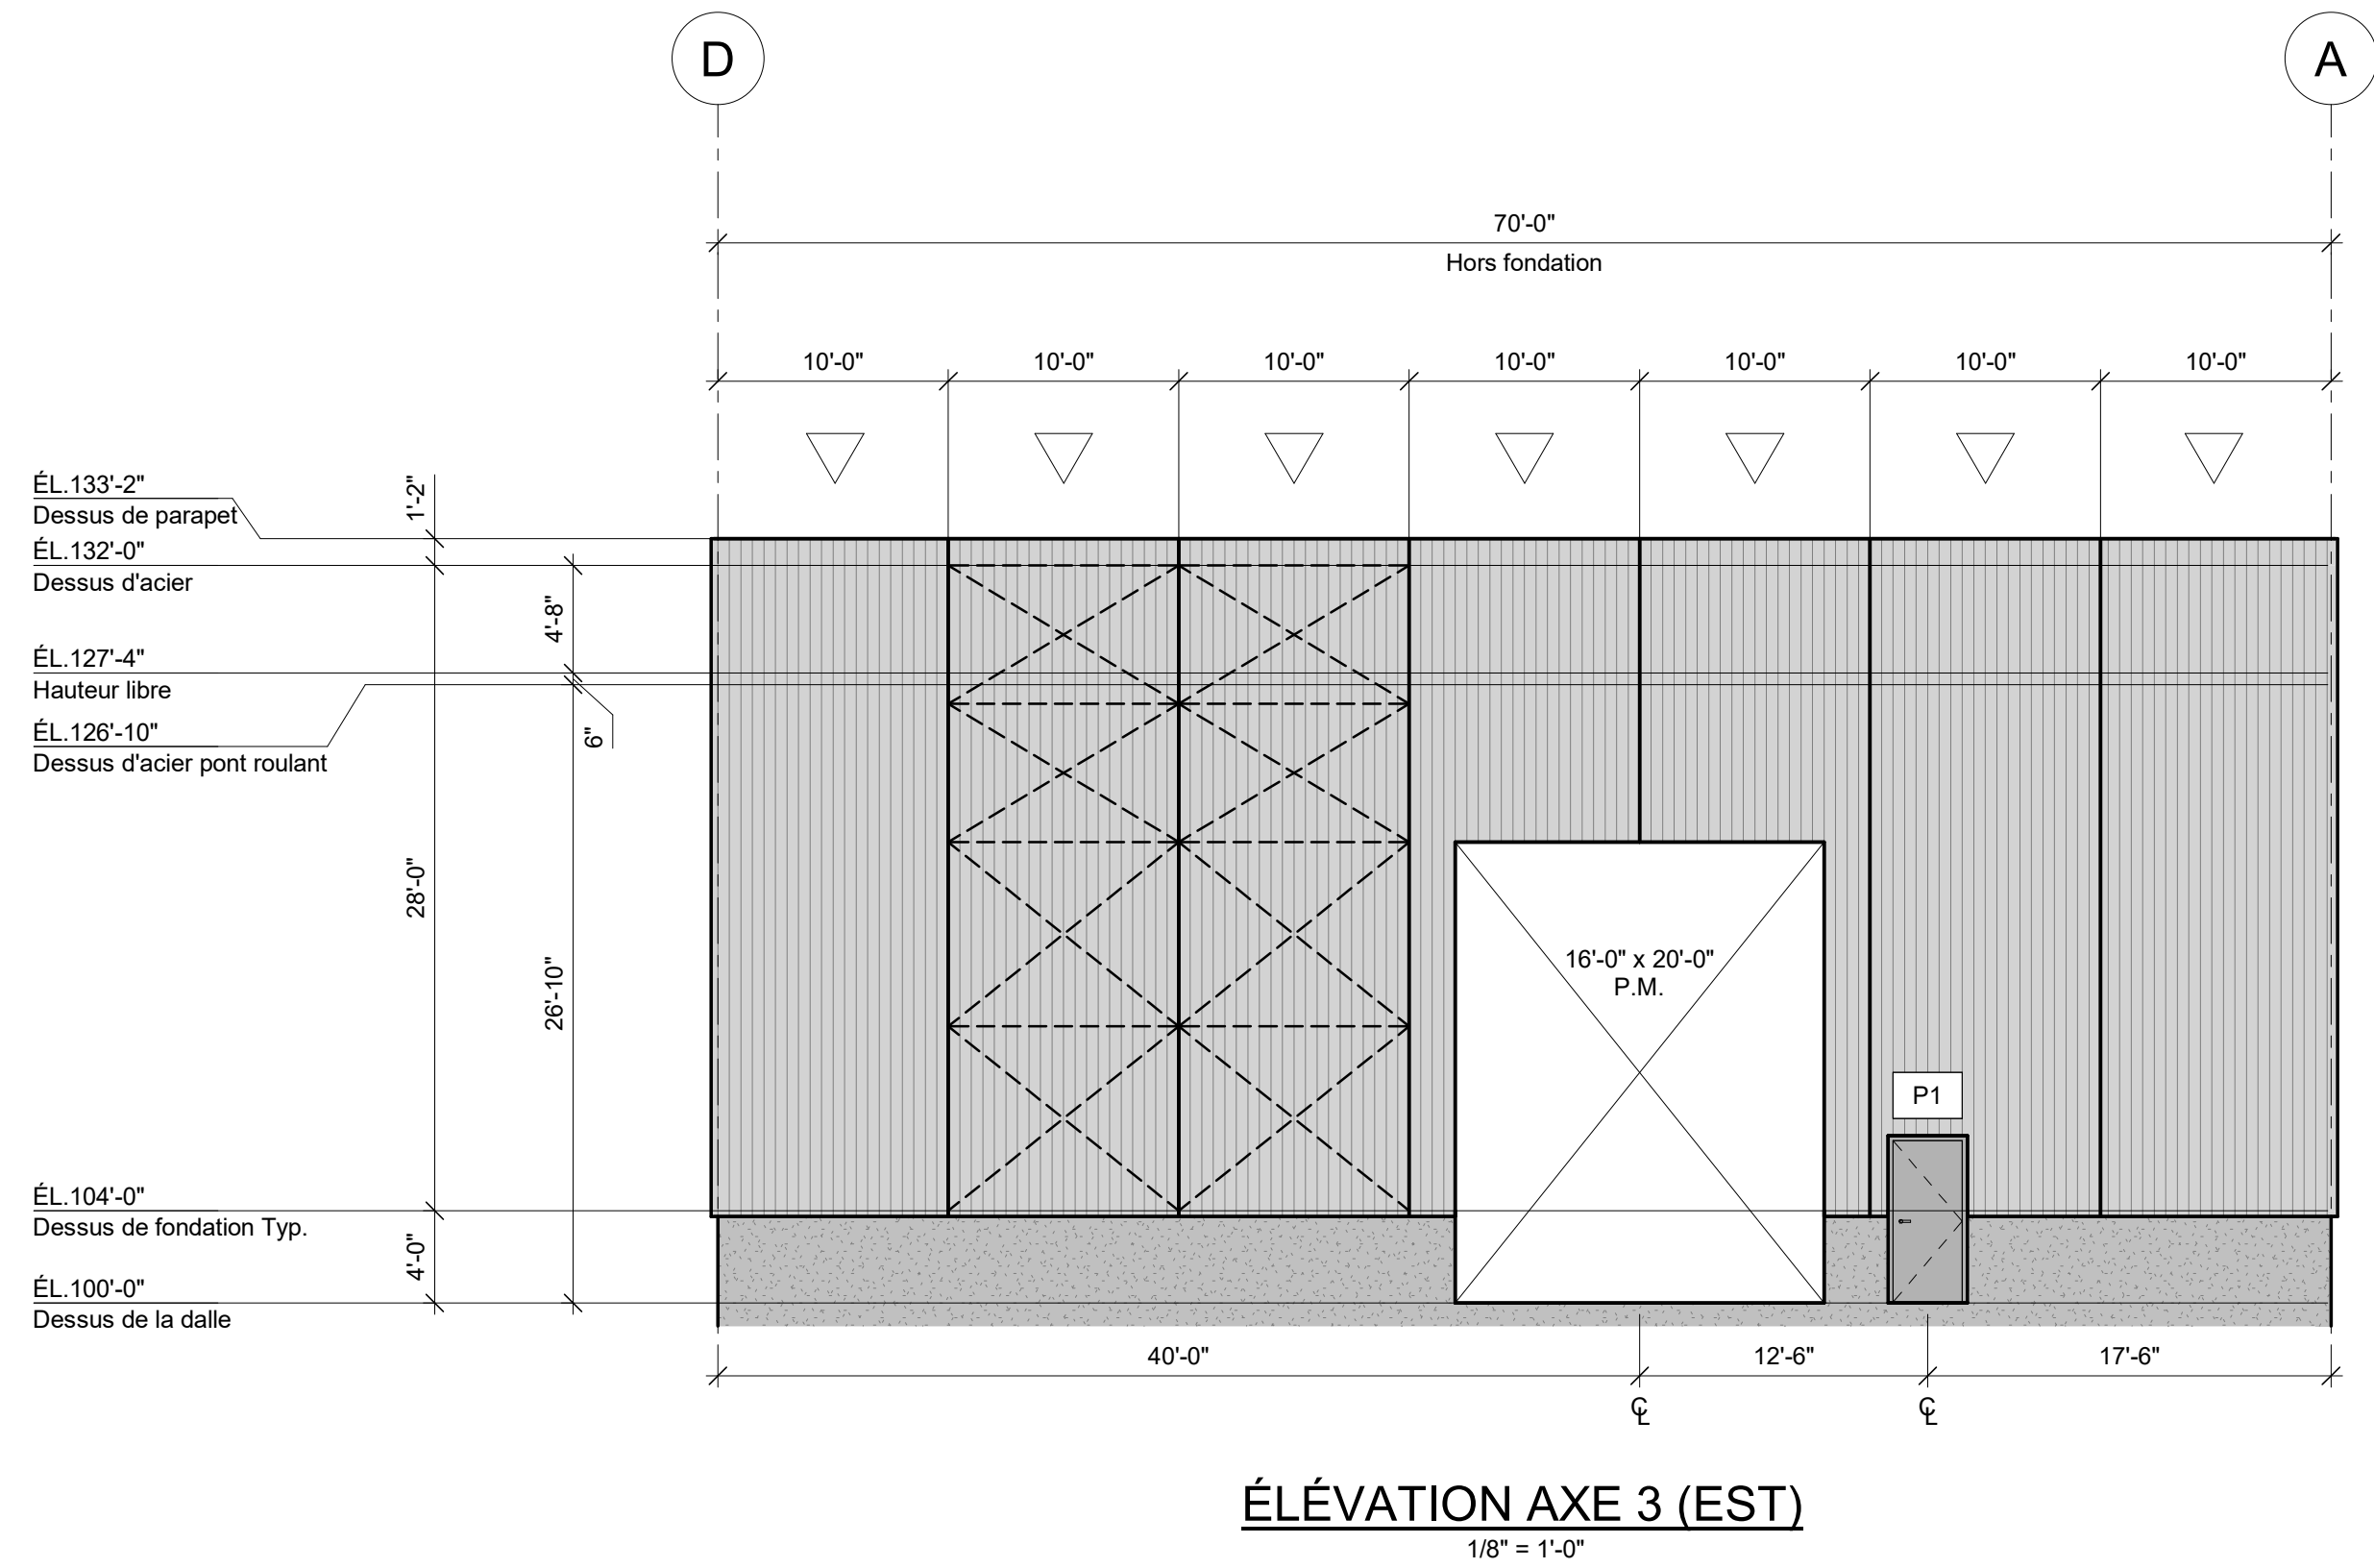


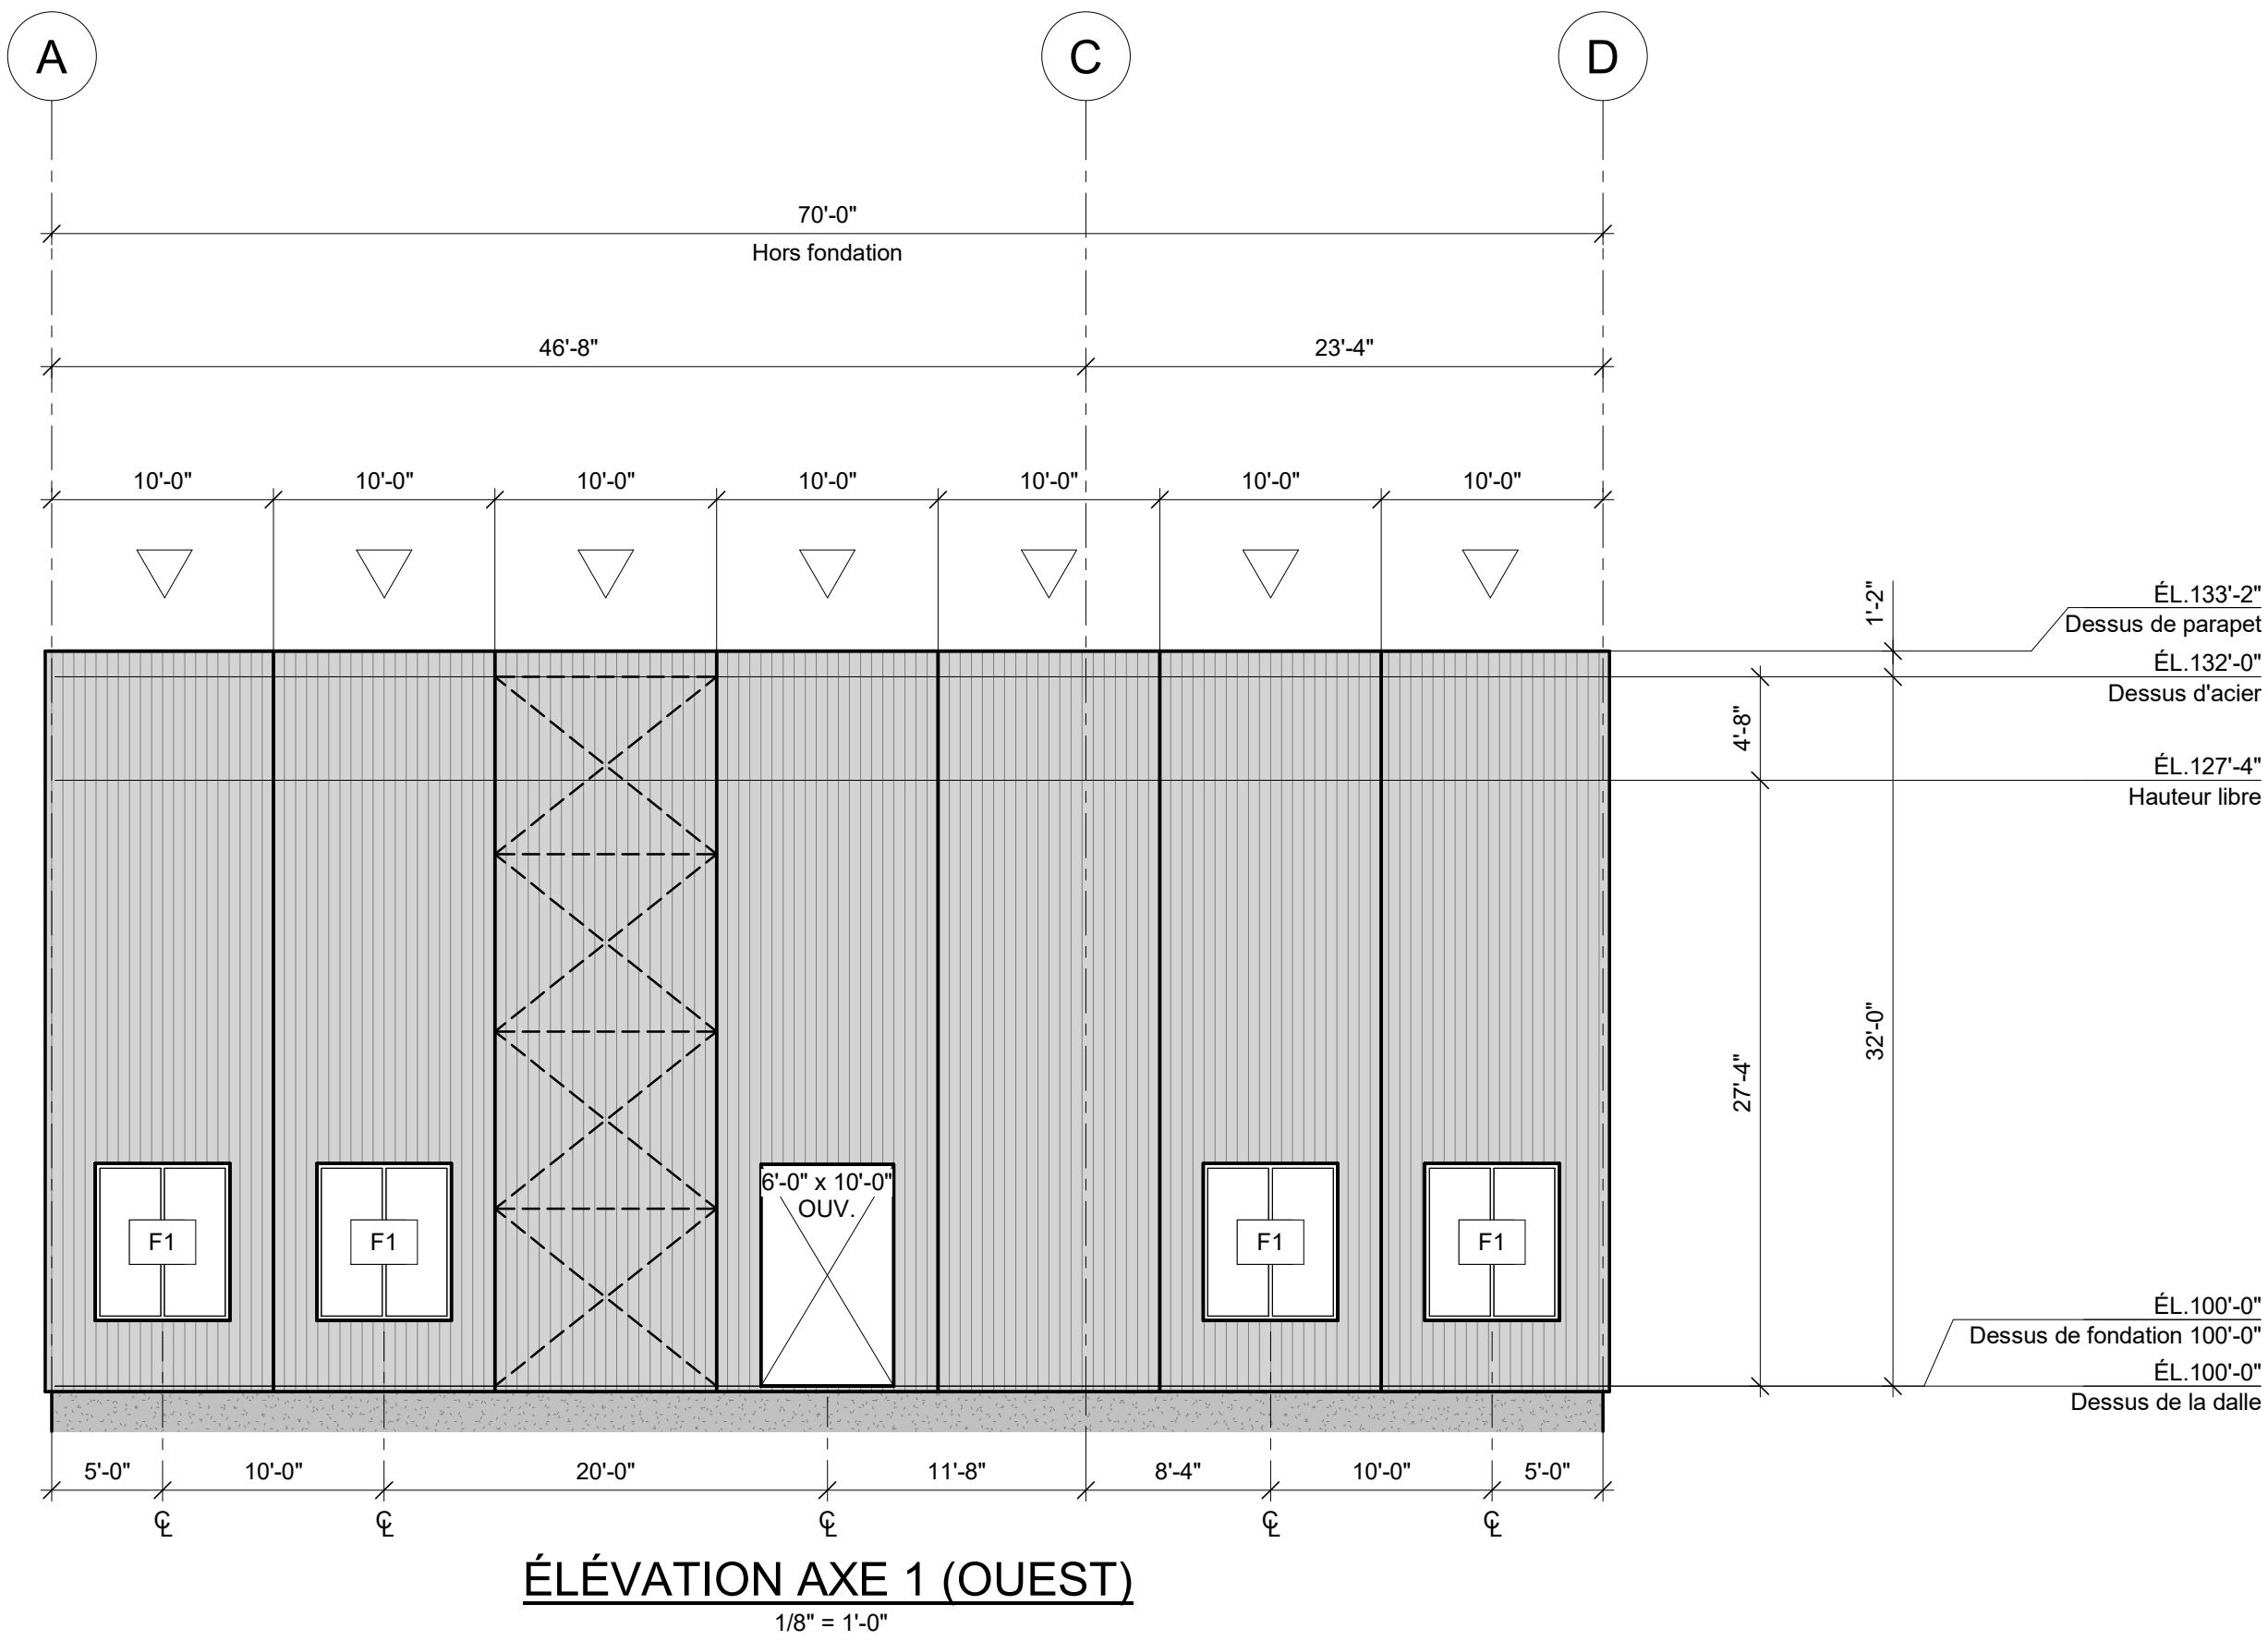

CÉDULE DES FENÊTRES					
Identifiant	Qté.	Installation	Description	Dimensions ext. cadre largeur X hauteur	Couleur du cadre
F1	6		Fenêtre en aluminium fixe avec bris thermique et verre scellé + Low-E argon clair (2 large x 1 haut)	6'-0" x 7'-0"	Cadre en aluminium (Blanc ext. et int.)

CÉDULE DES PORTES													
Identifiant	Qté.	Installation	Porte 18 ja.		Sens ouv.	Vitrage		Quincaillerie					
			Isolation (R12)	Dimensions 3'-0" x 7'-0"		Largeur	Hauteur	Cadre d'acier 16 ja., avec bris thermique	(3) Pentures @ tige fixe	Poignée seulement	Barre panique sans poignée ext. 22EO	Barre panique avec poignée ext. 230L	Verrou en surface (Porte inactive)
P1	4												

CÉDULE DES OUVERTURES POUR P.M., P.P. ET AUTRES			
Total	Type	Tag	Commentaires
1	6'-0" x 10'-0"	OUV.	
4	16'-0" x 20'-0"	P.M.	
Total général: 5			