

24x36

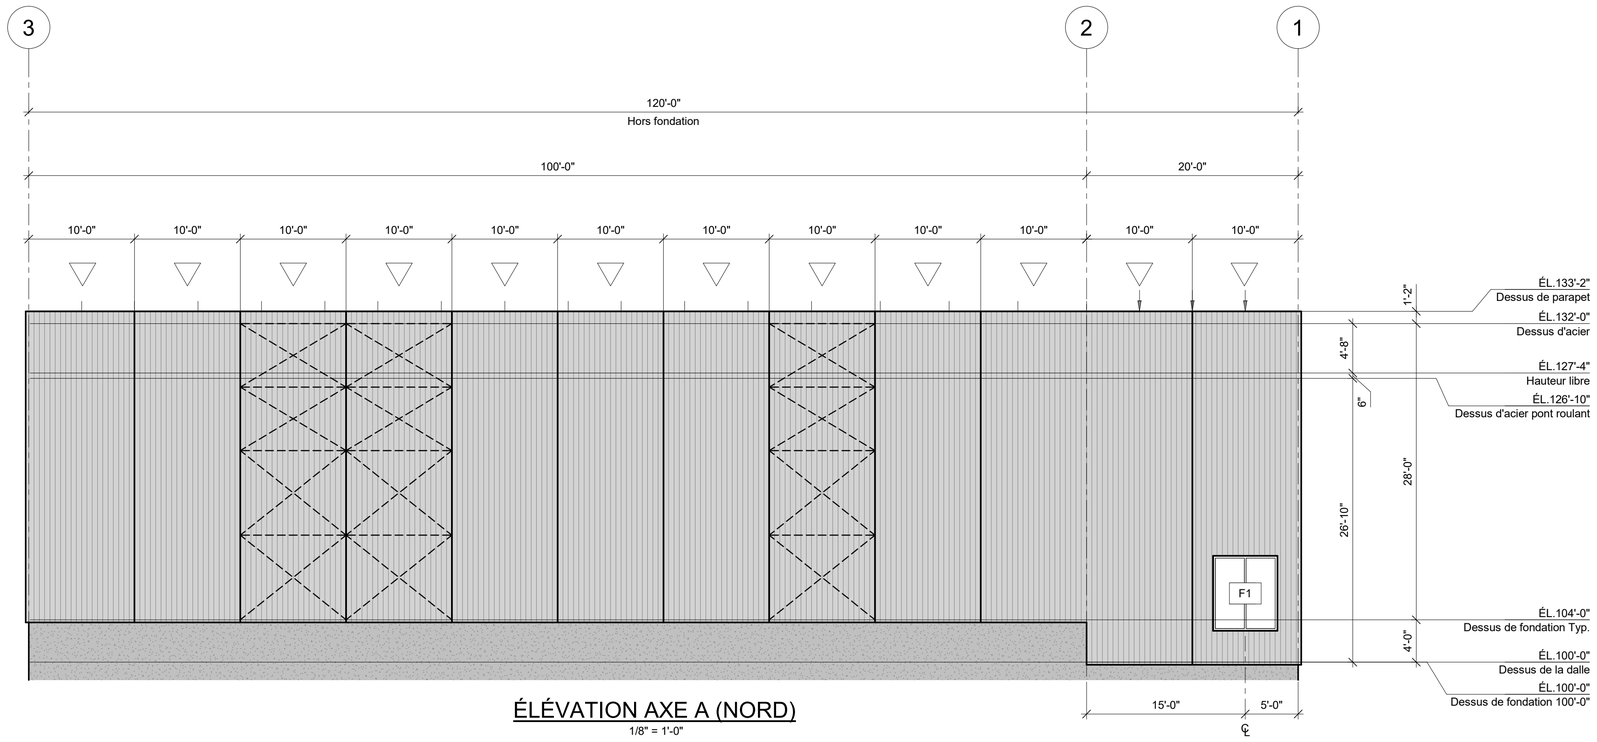


ÉLÉVATION AXE A (NORD)

1/8" = 1'-0"

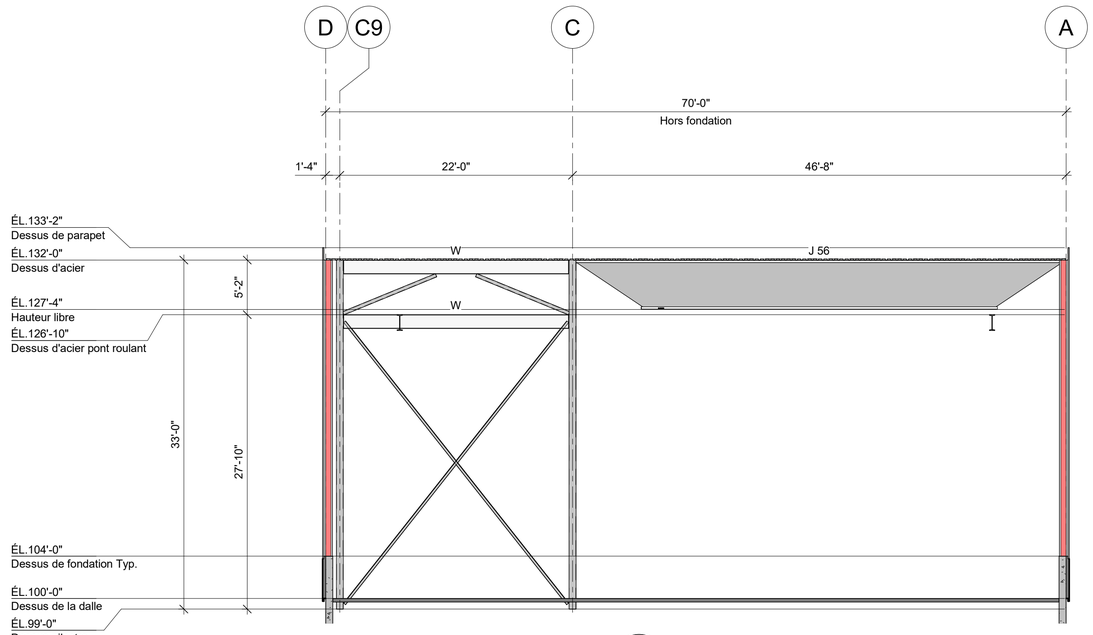

3 / Mx401 — COUPE AXE 2 (EST)

1/8" = 1'-0"

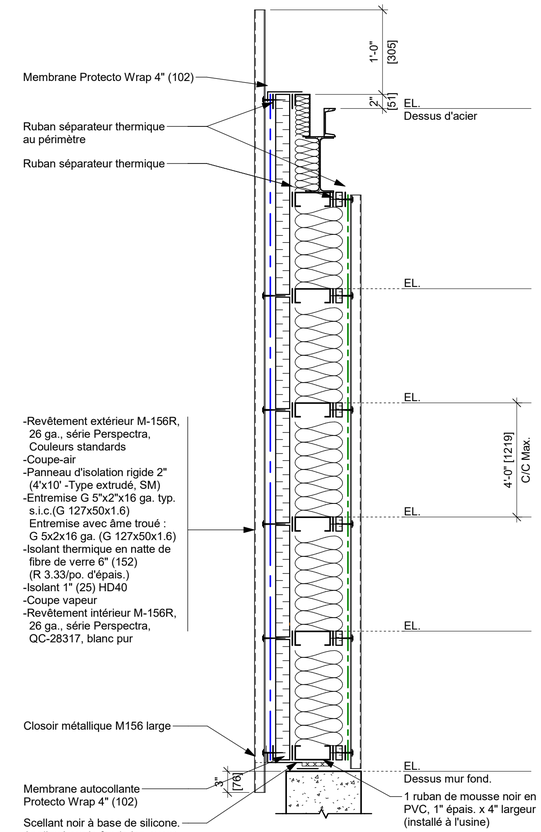

Panneaux Murox Ci R-25 Typique

CÉDULE DES FENÊTRES

Identifiant	Qté.	Installation	Description	Dimensions ext. cadre largeur X hauteur	Couleur du cadre	Remarques
F1	6		Fenêtre en aluminium fixe avec bris thermique et verre scellé + Low-E argon clair (2 large x 1 haut)	6'-0 x 7'-0"	Cadre en aluminium (Blanc ext. et int.)	

CÉDULE DES PORTES

Identifiant	Qté.	Porte 18 ja.			Sens ouv.	Vitrage		Quincaillerie												Remarques
		Installation	Isolation (R12)	Dimensions		Largeur	Hauteur	Cadre d'acier 16 ja., avec bris thermique	(3) Pentures @ tige fixe	Poignée seulement	Barre panique sans poignée ext. 22EO	Barre panique avec poignée ext. 230L	Verrou en surface (Porte inactive)	Seuil machiné	Astragale sur porte inactive	Ferme porte	Chaine	Coupe -froid	Chapeau en acier	
P1	4			3'-0" x 7'-0"																

CÉDULE DES OUVERTURES POUR P.M., P.P. ET AUTRES

Total	Type	Tag	Commentaires
1	6'-0" x 10'-0"	OUV.	
4	16'-0" x 20'-0"	P.M.	

Total général: 5

Initiales