




NORD POUR ÉRECTION SEULEMENT

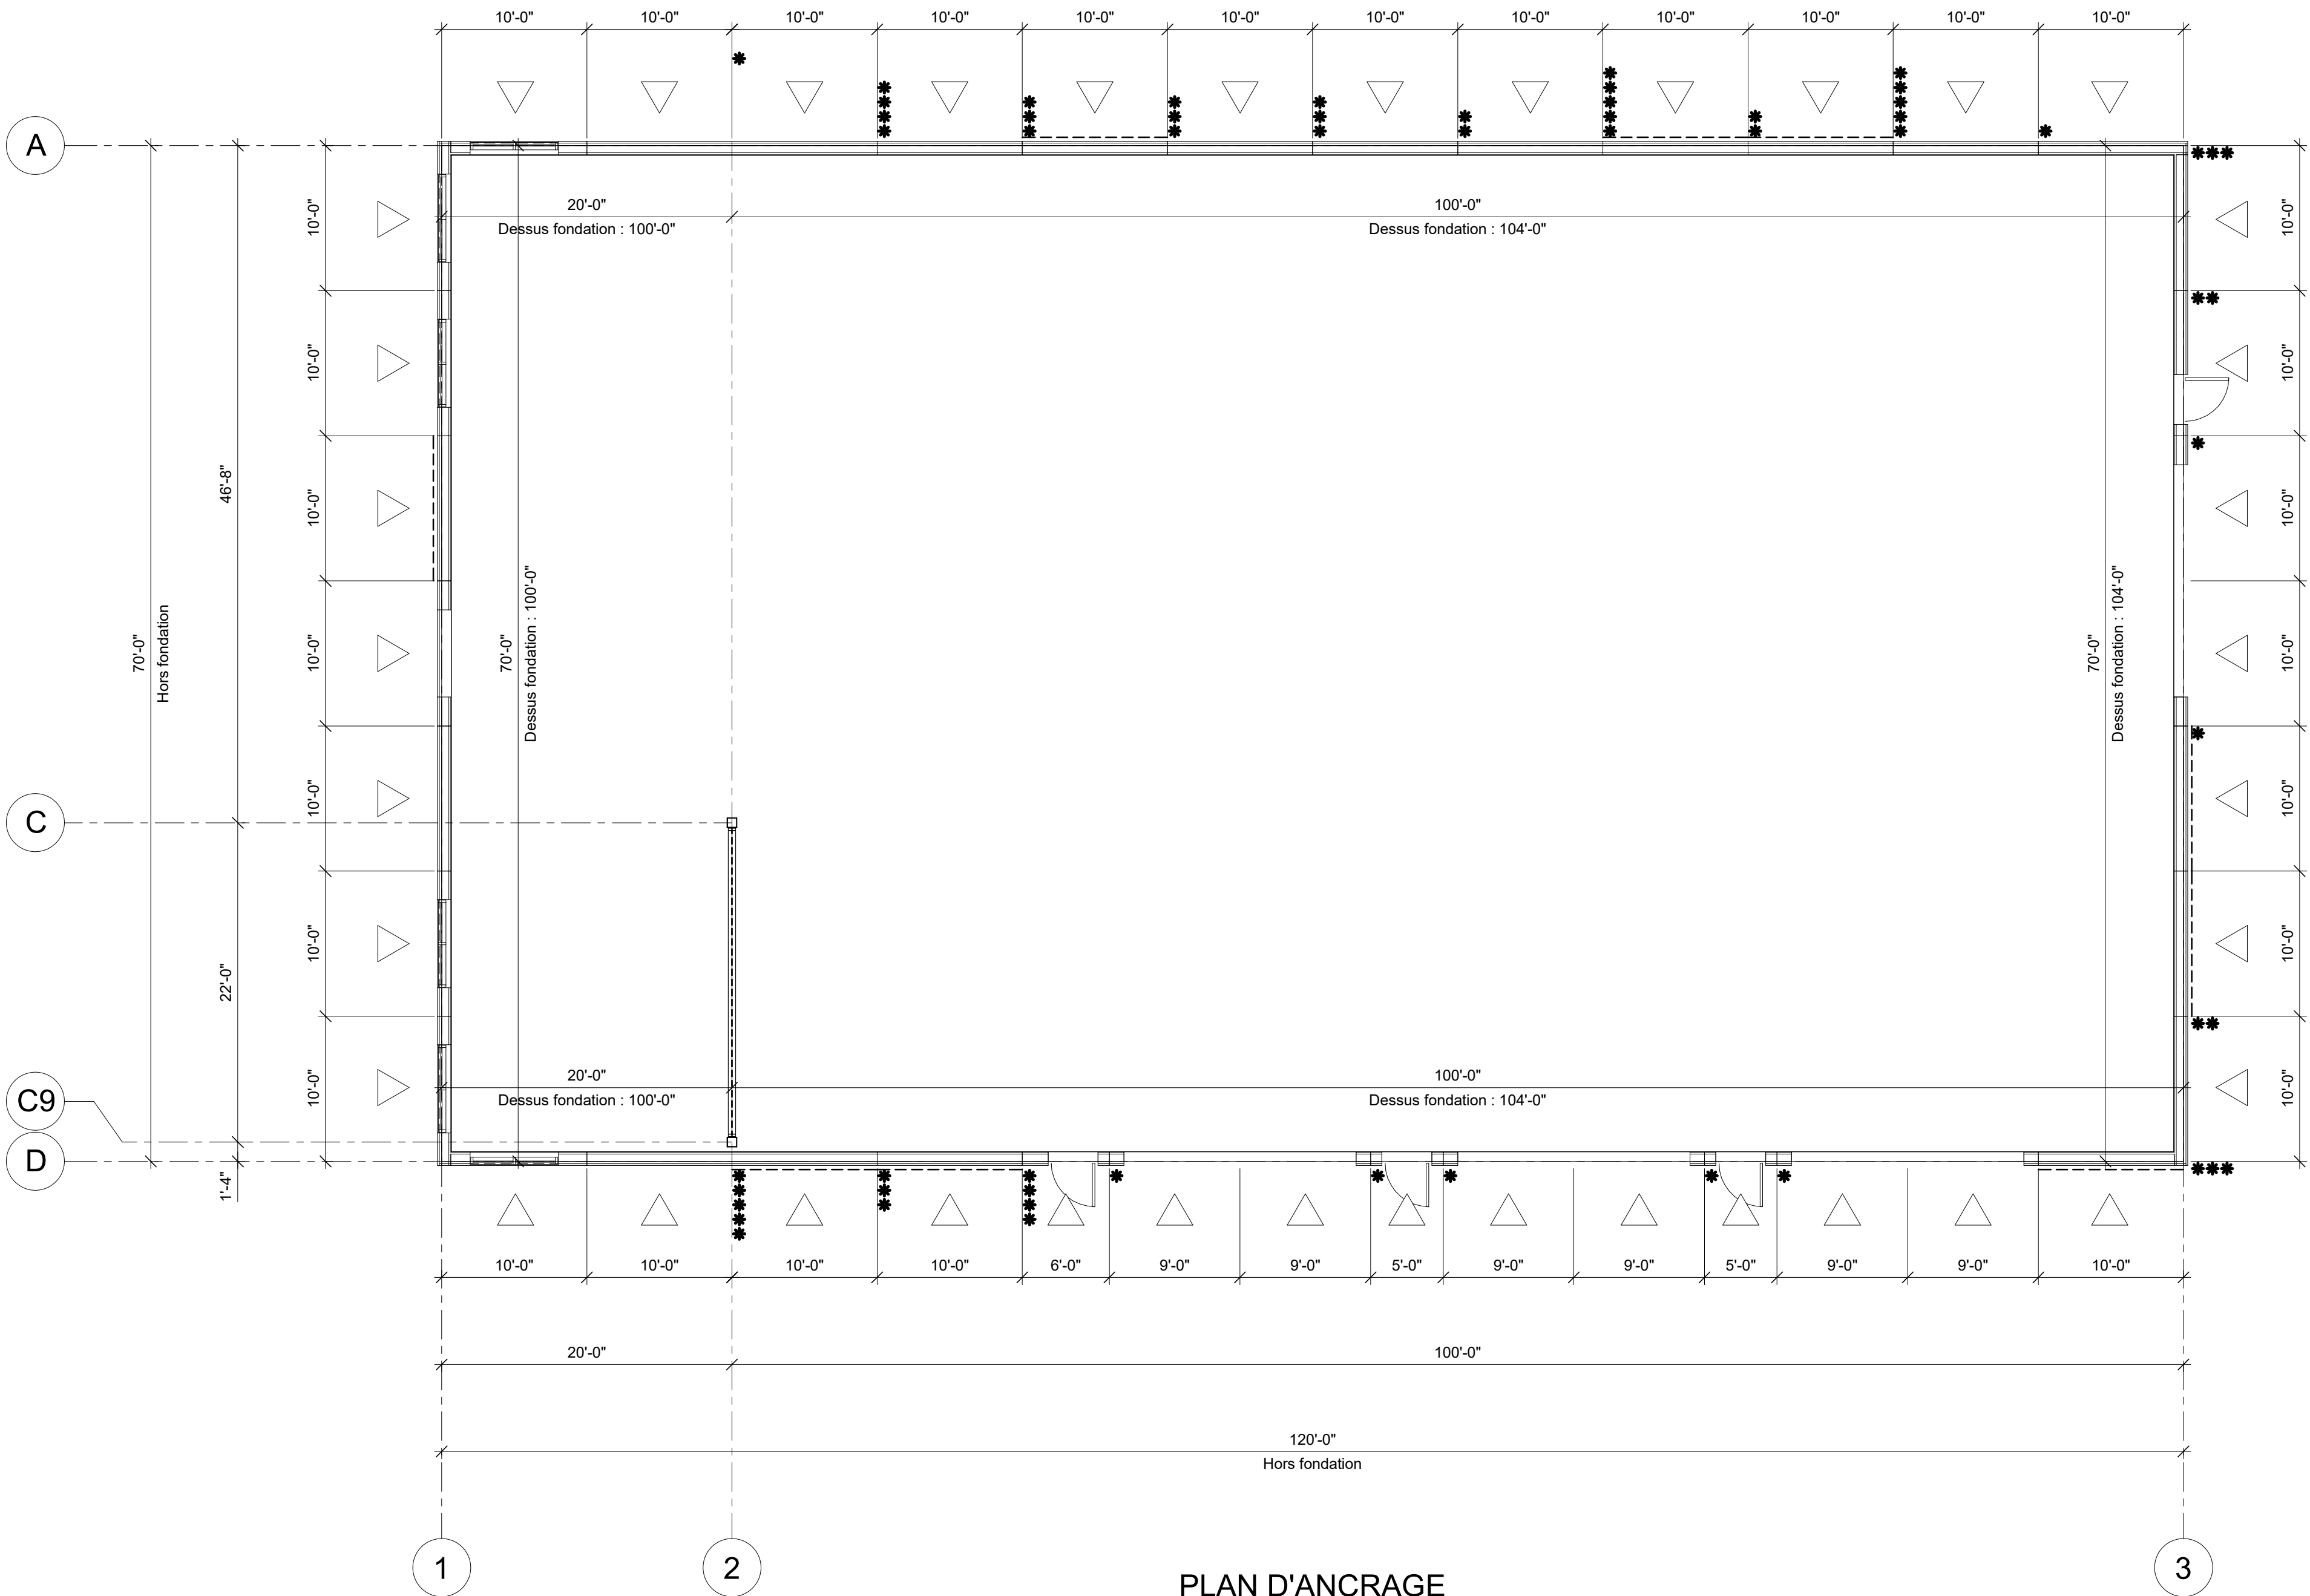

PLAN D'ANCRAGE

1/8" = 1'-0"

Bâtiment 70x120														
RÉACTIONS PRÉLIMINAIRES AUX FONDATIONS COLONNES DE PANNEAUX "MUROX" @ 10' c/c														
NOTE : TOUTES LES CHARGES DE SERVICES SONT EXPRIMÉES EN kips, TYP. S.I.C.. NE PAS UTILISER POUR CONSTRUCTION														
AXE	CHARGES VERTICALES							EFFORTS À LA BASE			CONTREVENTEMENTS			
	D	D	D	S	Lxc	C	W	PERP. À LA FONDATION			E		W	
	POIDS DU MUR		COL				SOUL. BRUT	W	E	C	H.	V.	H.	V.
1	2.6	7.5	0.1	2.0	0.0	0.0	-0.5	3.8	0.0	0.0	10.5	± 12.3	6.1	± 8.1
3	2.6	0.5	0.1	2.0	0.0	0.0	-0.5	3.3	0.0	0.0	16.7	± 46.8	7.5	± 21.0
3*	3.8	0.8	0.2	3.0	0.0	0.0	-0.7	5.0	0.0	0.0	16.7	± 46.8	7.5	± 21.0
3**	2.6	0.5	1.1	2.0	0.0	19.0	-0.5	3.3	0.0	0.0	16.7	± 46.8	7.5	± 21.0
3***	1.3	0.3	1.6	1.0	0.0	23.0	-0.2	1.7	0.0	0.0				
A (1 à 2) & D (1 à 2)	2.6	8.8	1.8	28.1	2.0	0.0	-6.9	3.8	0.0	0.0	10.5	± 12.3	10.8	± 12.6
A (2 à 3) & D (2 à 3)	2.6	8.1	1.9	30.9	0.0	0.0	-7.6	3.3	0.0	0.0	13.2	± 37.0	3.6	± 10.1
D*	3.1	10.3	4.4	39.2	0.0	27.0	-9.6	4.0	0.0	0.0				
D**	3.6	11.3	4.7	43.2	0.0	27.0	-10.6	4.6	0.0	0.0	13.2	± 37.0	3.6	± 10.1
D***	2.6	8.5	3.1	32.6	0.0	16.1	-8.0	3.3	0.0	0.0	13.2	± 37.0	3.6	± 10.1
D****	2.0	6.8	2.1	26.1	0.0	6.9	-6.4	2.6	0.0	0.0	13.2	± 37.0	3.6	± 10.1
A*	2.6	8.1	3.9	30.9	0.0	27.0	-7.6	3.3	0.0	0.0				
A**	2.6	8.5	5.0	32.6	0.0	40.5	-8.0	3.3	0.0	0.0				
A***	2.6	8.5	3.4	32.6	0.0	18.9	-8.0	3.3	0.0	0.0	13.2	± 37.0	3.6	± 10.1
A****	2.6	8.5	3.1	32.6	0.0	16.1	-8.0	3.3	0.0	0.0				
A*****	2.6	8.5	2.6	32.6	0.0	8.1	-8.0	3.3	0.0	0.0	13.2	± 37.0	3.6	± 10.1
D*****	2.6	9.2	2.0	32.6	0.0	0.0	-8.0	3.8	0.0	0.0	13.2	± 37.0	3.6	± 10.1
A*****	2.6	9.2	2.0	32.6	0.0	0.0	-8.0	3.8	0.0	0.0	10.5	± 12.3	10.8	± 12.6

CÉDULE PRÉLIMINAIRE DES COLONNES INTÉRIEURES

Bâtiment 70x120

TOUTES LES CHARGES DE SERVICES SONT EXPRIMÉES EN kips, TYP. S.I.C.. NE PAS UTILISER POUR CONSTRUCTION

NO. COL.	CHARGES VERTICALES						CONTREVENTEMENTS					
	D	D COL	S	Lxc	C	W SOUL. BRUT	E			W		
1	9.8	0.7	6.2	11.7	15.2	-1.5	H(N/S)	H(E/O)	V.	H(N/S)	H(E/O)	V.
2	19.6	1.9	12.5	23.3	9.5	-3.1	0.0	0.0	± 0.0	0.0	0.0	± 0.0
3	19.6	1.9	12.5	23.3	9.5	-3.1	56.6	0.0	± 75.2	26.6	0.0	± 34.6
4	9.8	0.7	6.2	11.7	15.2	-1.5	56.6	0.0	± 75.2	26.6	0.0	± 34.6

NOTE POUR LE CONTRACTEUR/ÉRECTEUR:

IL EST STRICTEMENT DÉFENDU DE MODIFIER, COPIER, REPRODUIRE OU DE DISTRIBUER CES DESSINS OU QUELQUES REPRÉSENTATIONS DE CES DESSINS, PAR TOUTES SOURCES DE MÉDIA INCLUANT ÉLECTRONIQUEMENT, SANS L'APPROBATION ÉCRITE DE GROUPE CANAM INC.

PRÉLIMINAIRE


NE DOIT PAS SERVIR À LA CONSTRUCTION

2	2026/05/02	R2	J.P.	
1	2026/02/24	R1	J.P.	
REVISION	DATE	DESCRIPTION	DESS	VER.

GERANT DE PROJET	-
	-
	-
	-

DESSIN:			
DESSINE PAR	CONÇU PAR	INGÉNIEUR DU PROJET	ECHELLE:
J.P.			1/8" = 1'-0"
VÉRIFIÉ PAR	INGÉNIEURS CONSEILS / ARCHITECTES		DATE (jj/mm/aaaa) :
			19/09/2025

CLIENT: Entreprise R. et G. St-Laurent Inc

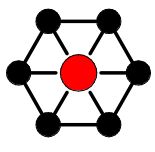**CANAM**

11505, 1re Avenue, bureau 500, Saint-Georges Beauce
Québec, Canada, G5Y 7X3
Téléphone : (418) 228-8031
Sans frais : (877) 499-6049
www.canam.com

SCEAU PROFESSIONNEL

PROJET

Bâtiment 70x120
Baie-Comeau, Québec

TITRE

CROQUIS PRÉLIMINAIRE - PLAN D'ANCRAGE

NUMÉRO CONTRAT	NUMÉRO DESSIN	DIVISION	REVISION
P2025-151	Mx101		2

Initiales