





NORD POUR ÉRECTION SEULEMENT

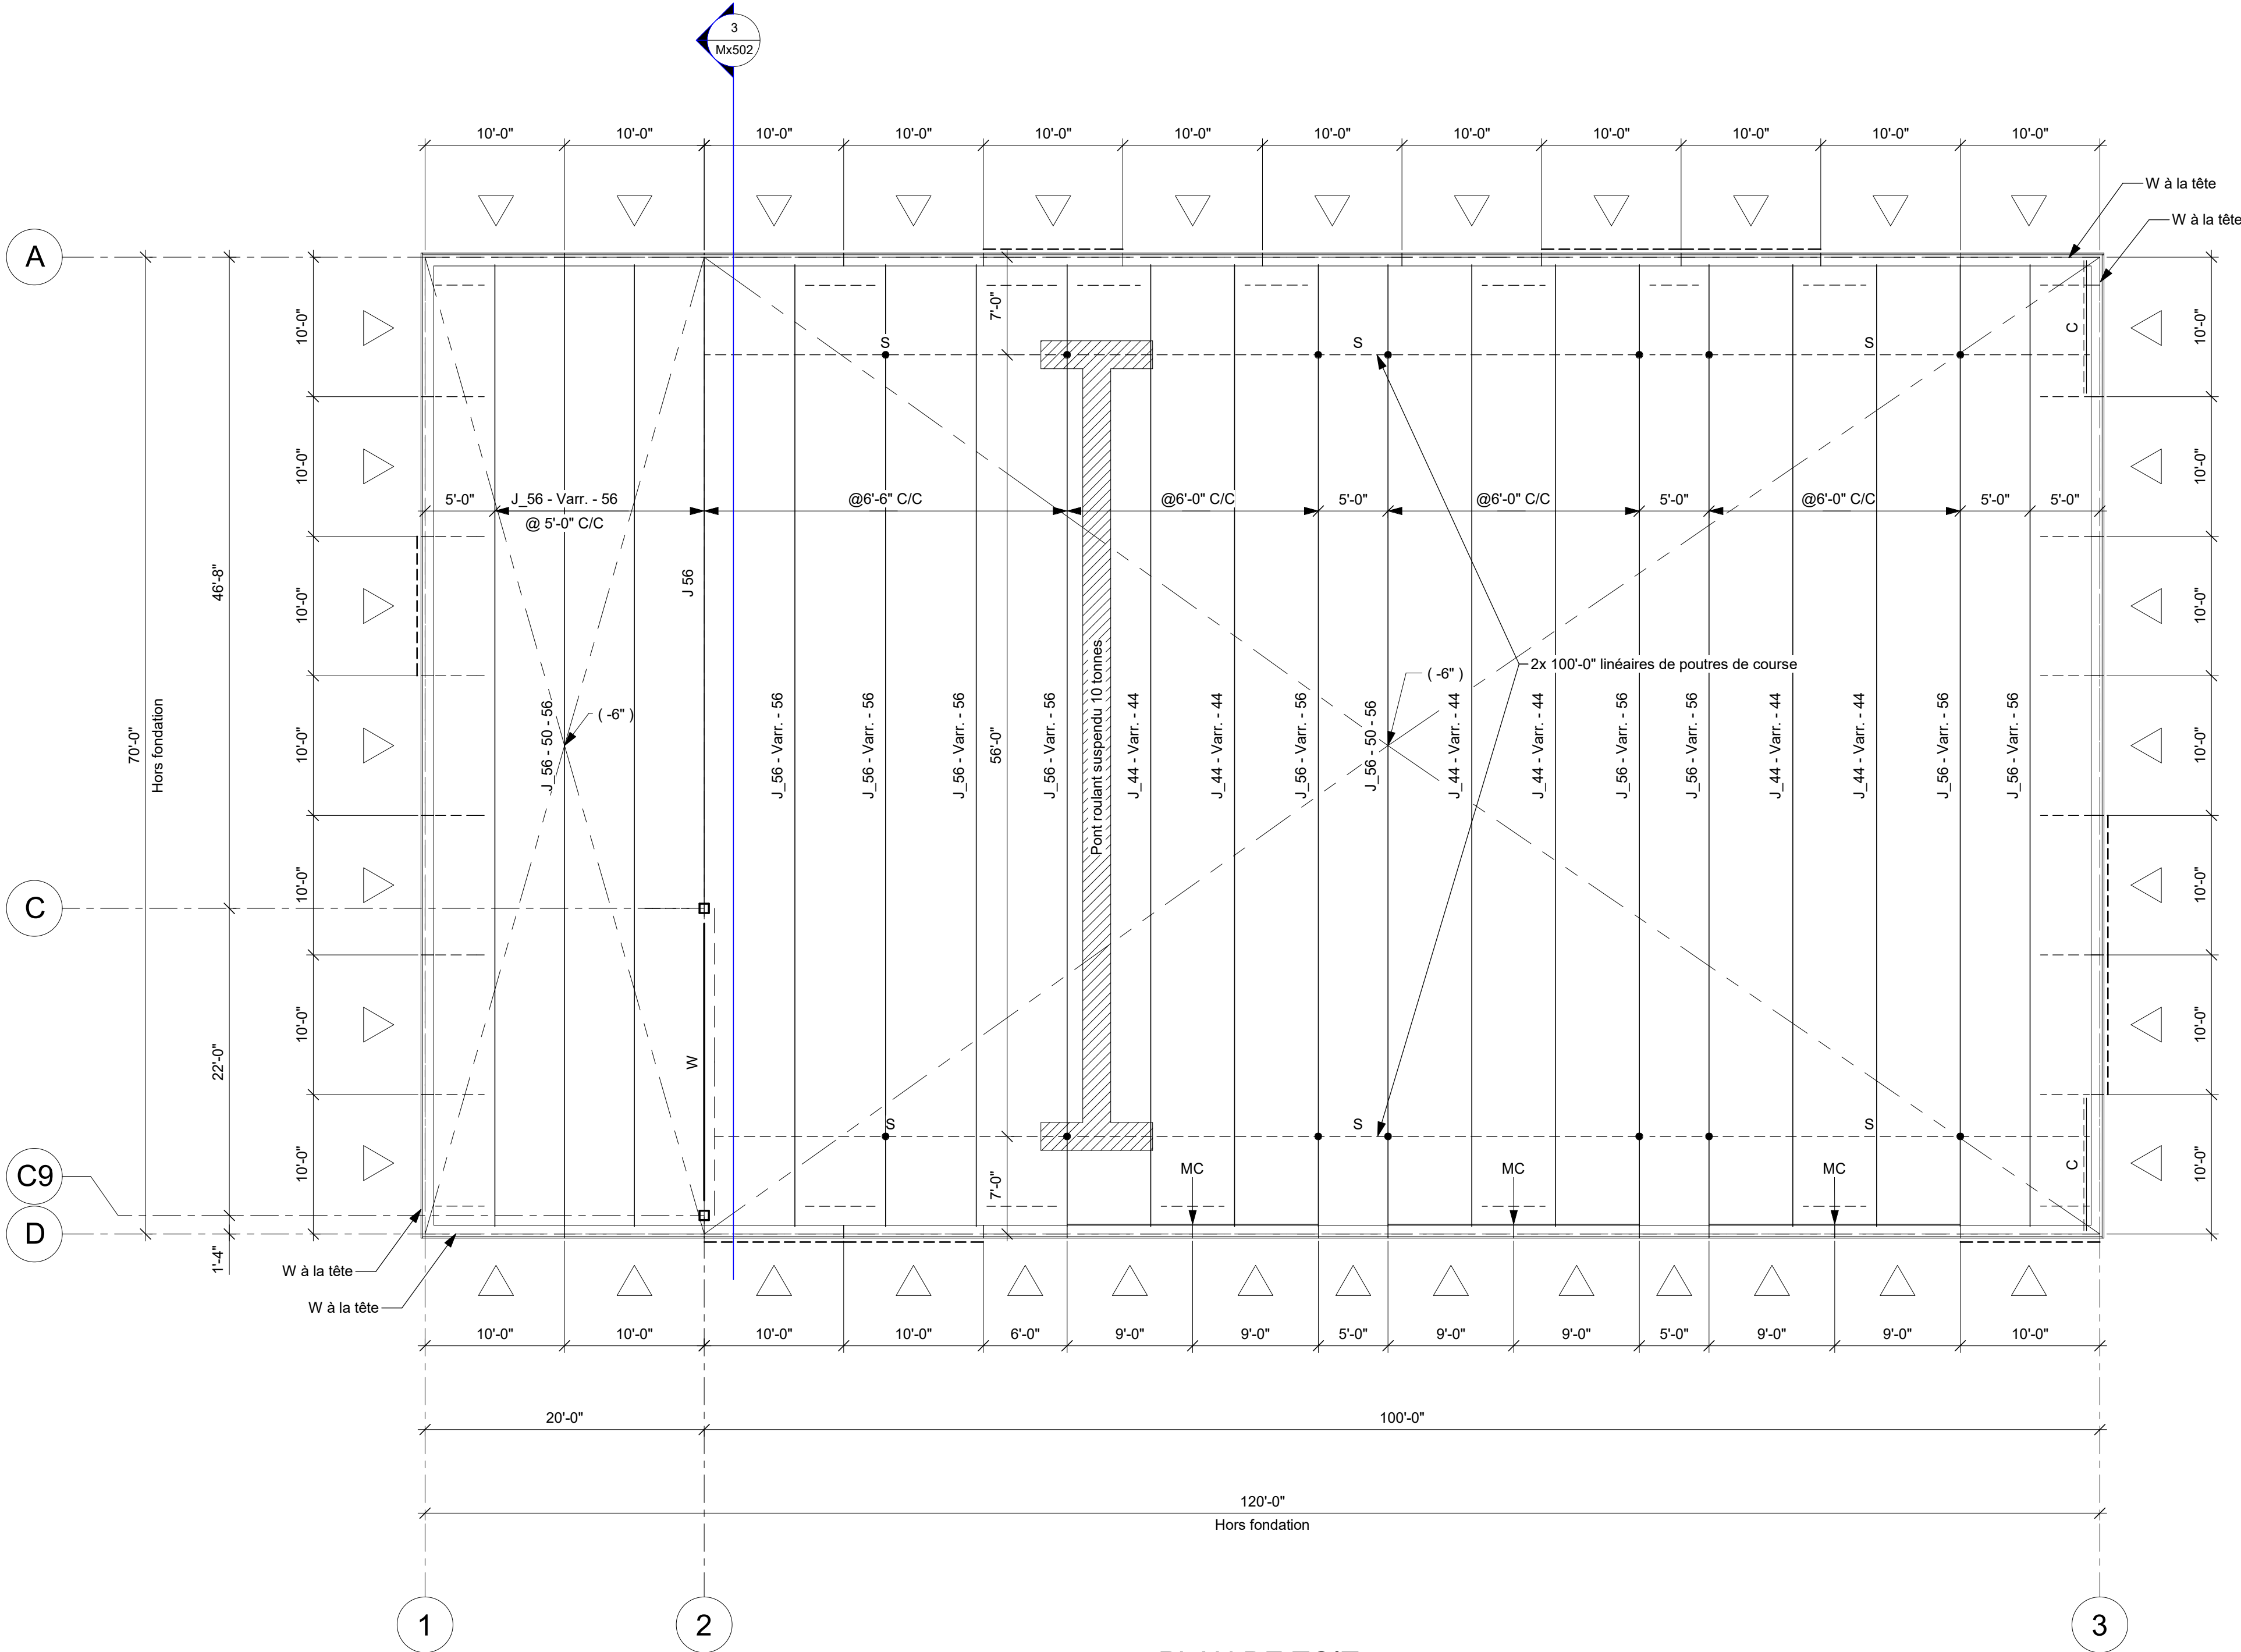

PLAN DE TOIT
1/8" = 1'-0"

TABLEAU CHARGES PONT ROULANT				
CAPACITÉ	POIDS DU PONT	CHARIOT	CHARGE MAX. PAR ROUE (DYNAMIQUE)	ESPACEMENT DES ROUES
10 Tonnes	13800 lb	1350 lb	19 kip	10'-6"

DIAGRAMME DE SOULEVEMENT BRUT (NON PONDÉRÉ)

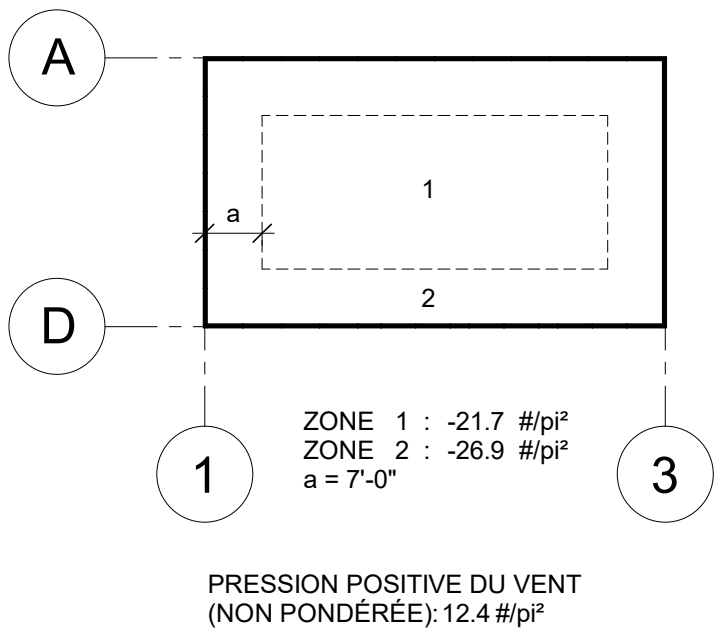

NOTE POUR LE CONTRACTEUR/ÉRECTEUR:

IL EST STRICTEMENT DÉFENDU DE MODIFIER, COPIER, REPRODUIRE OU DE DISTRIBUER CES DESSINS OU QUELQUES REPRÉSENTATIONS DE CES DESSINS, PAR TOUTES SOURCES DE MÉDIA INCLUANT ÉLECTRONIQUEMENT, SANS L'APPROBATION ÉCRITE DE GROUPE CANAM INC.

TOIT

NIVEAU DES PILASTRE DDT	: 98'-0"
NIVEAU DES PILASTRE	: 99'-0"
NIVEAU DE LA DALLE	: 100'-0"
NIVEAU DE LA FONDATION TYP. S.I.C.	: 104'-0"
HAUTEUR LIBRE	: 27'-4"
DESSUS D'ACIER	: 132'-0"
HAUTEUR DE PARAPET	: 1'-2"
DESSUS DE PARAPET	: 133'-2"

CHARGES

C.M.	: 18	#/pi²
Coll.	: 5	#/pi²
Ss	: 89.8	#/pi²
Sr	: 8.4	#/pi²
Cb x Cw	: 0.8	
C.V. au toit	: 0	#/pi²
Is	: 1.0	
Charge de neige au toit	: 80.2	#/pi²
Iw	: 1.0	
Vent q=	1/50	#/pi²

Seisme (Sol de classe D assumé)

Ie	: 1.0
Se (0.2)	: 0.425
Se (0.5)	: 0.219
Se (1.0)	: 0.107
Se (2.0)	: 0.051
Se (5.0)	: 0.014
Se (10.0)	: 0.005
PGA	: 0.274
PGV	: 0.182

CHARGES :

Code Applicable : Code National du Bâtiment du Canada
Code du bâtiment du Québec, dernières éditions adoptées
Code de Pratique Standard ICCA.

Type de sol assumé : classe D

NOTE : - Si toutefois la catégorie d'emplacement devient E ou F selon le rapport géotechnique, le concept structural préliminaire (localisation et géométrie des contreventements, etc.) devra être validé et coordonné par l'ingénieur de Canam.

PRÉLIMINAIRE


NE DOIT PAS SERVIR À LA CONSTRUCTION

2	2026/05/02	R2	J.P.	
1	2026/02/24	R1	J.P.	

REVISION	DATE	DESCRIPTION	DESS	VER.
GERANT DE PROJET				
-				
-				
-				
-				

DESSIN:			
DESSINE PAR J.P.	CONÇU PAR	INGÉNIEUR DU PROJET	ÉCHELLE: COMME INDiqué
VÉRIFIÉ PAR	INGÉNIEURS CONSEILS / ARCHITECTES		DATE (jj/mm/aaaa) : 19/09/2025

CLIENT: Entreprise R. et G. St-Laurent Inc

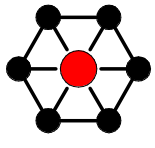**CANAM**

11505, 1re Avenue, bureau 500, Saint-Georges Beauce
Québec, Canada, G5Y 7X3
Téléphone : (418) 228-8031
Sans frais : (877) 499-6049
www.canam.com

SCEAU PROFESSIONNEL

PROJET

Bâtiment 70x120
Baie-Comeau, Québec

TITRE
CROQUIS PRÉLIMINAIRE - PLAN DE TOIT

NUMÉRO CONTRAT P2025-151	NUMÉRO DESSIN Mx401	DIVISION	RÉVISION 2
-----------------------------	------------------------	----------	---------------

Initiales