




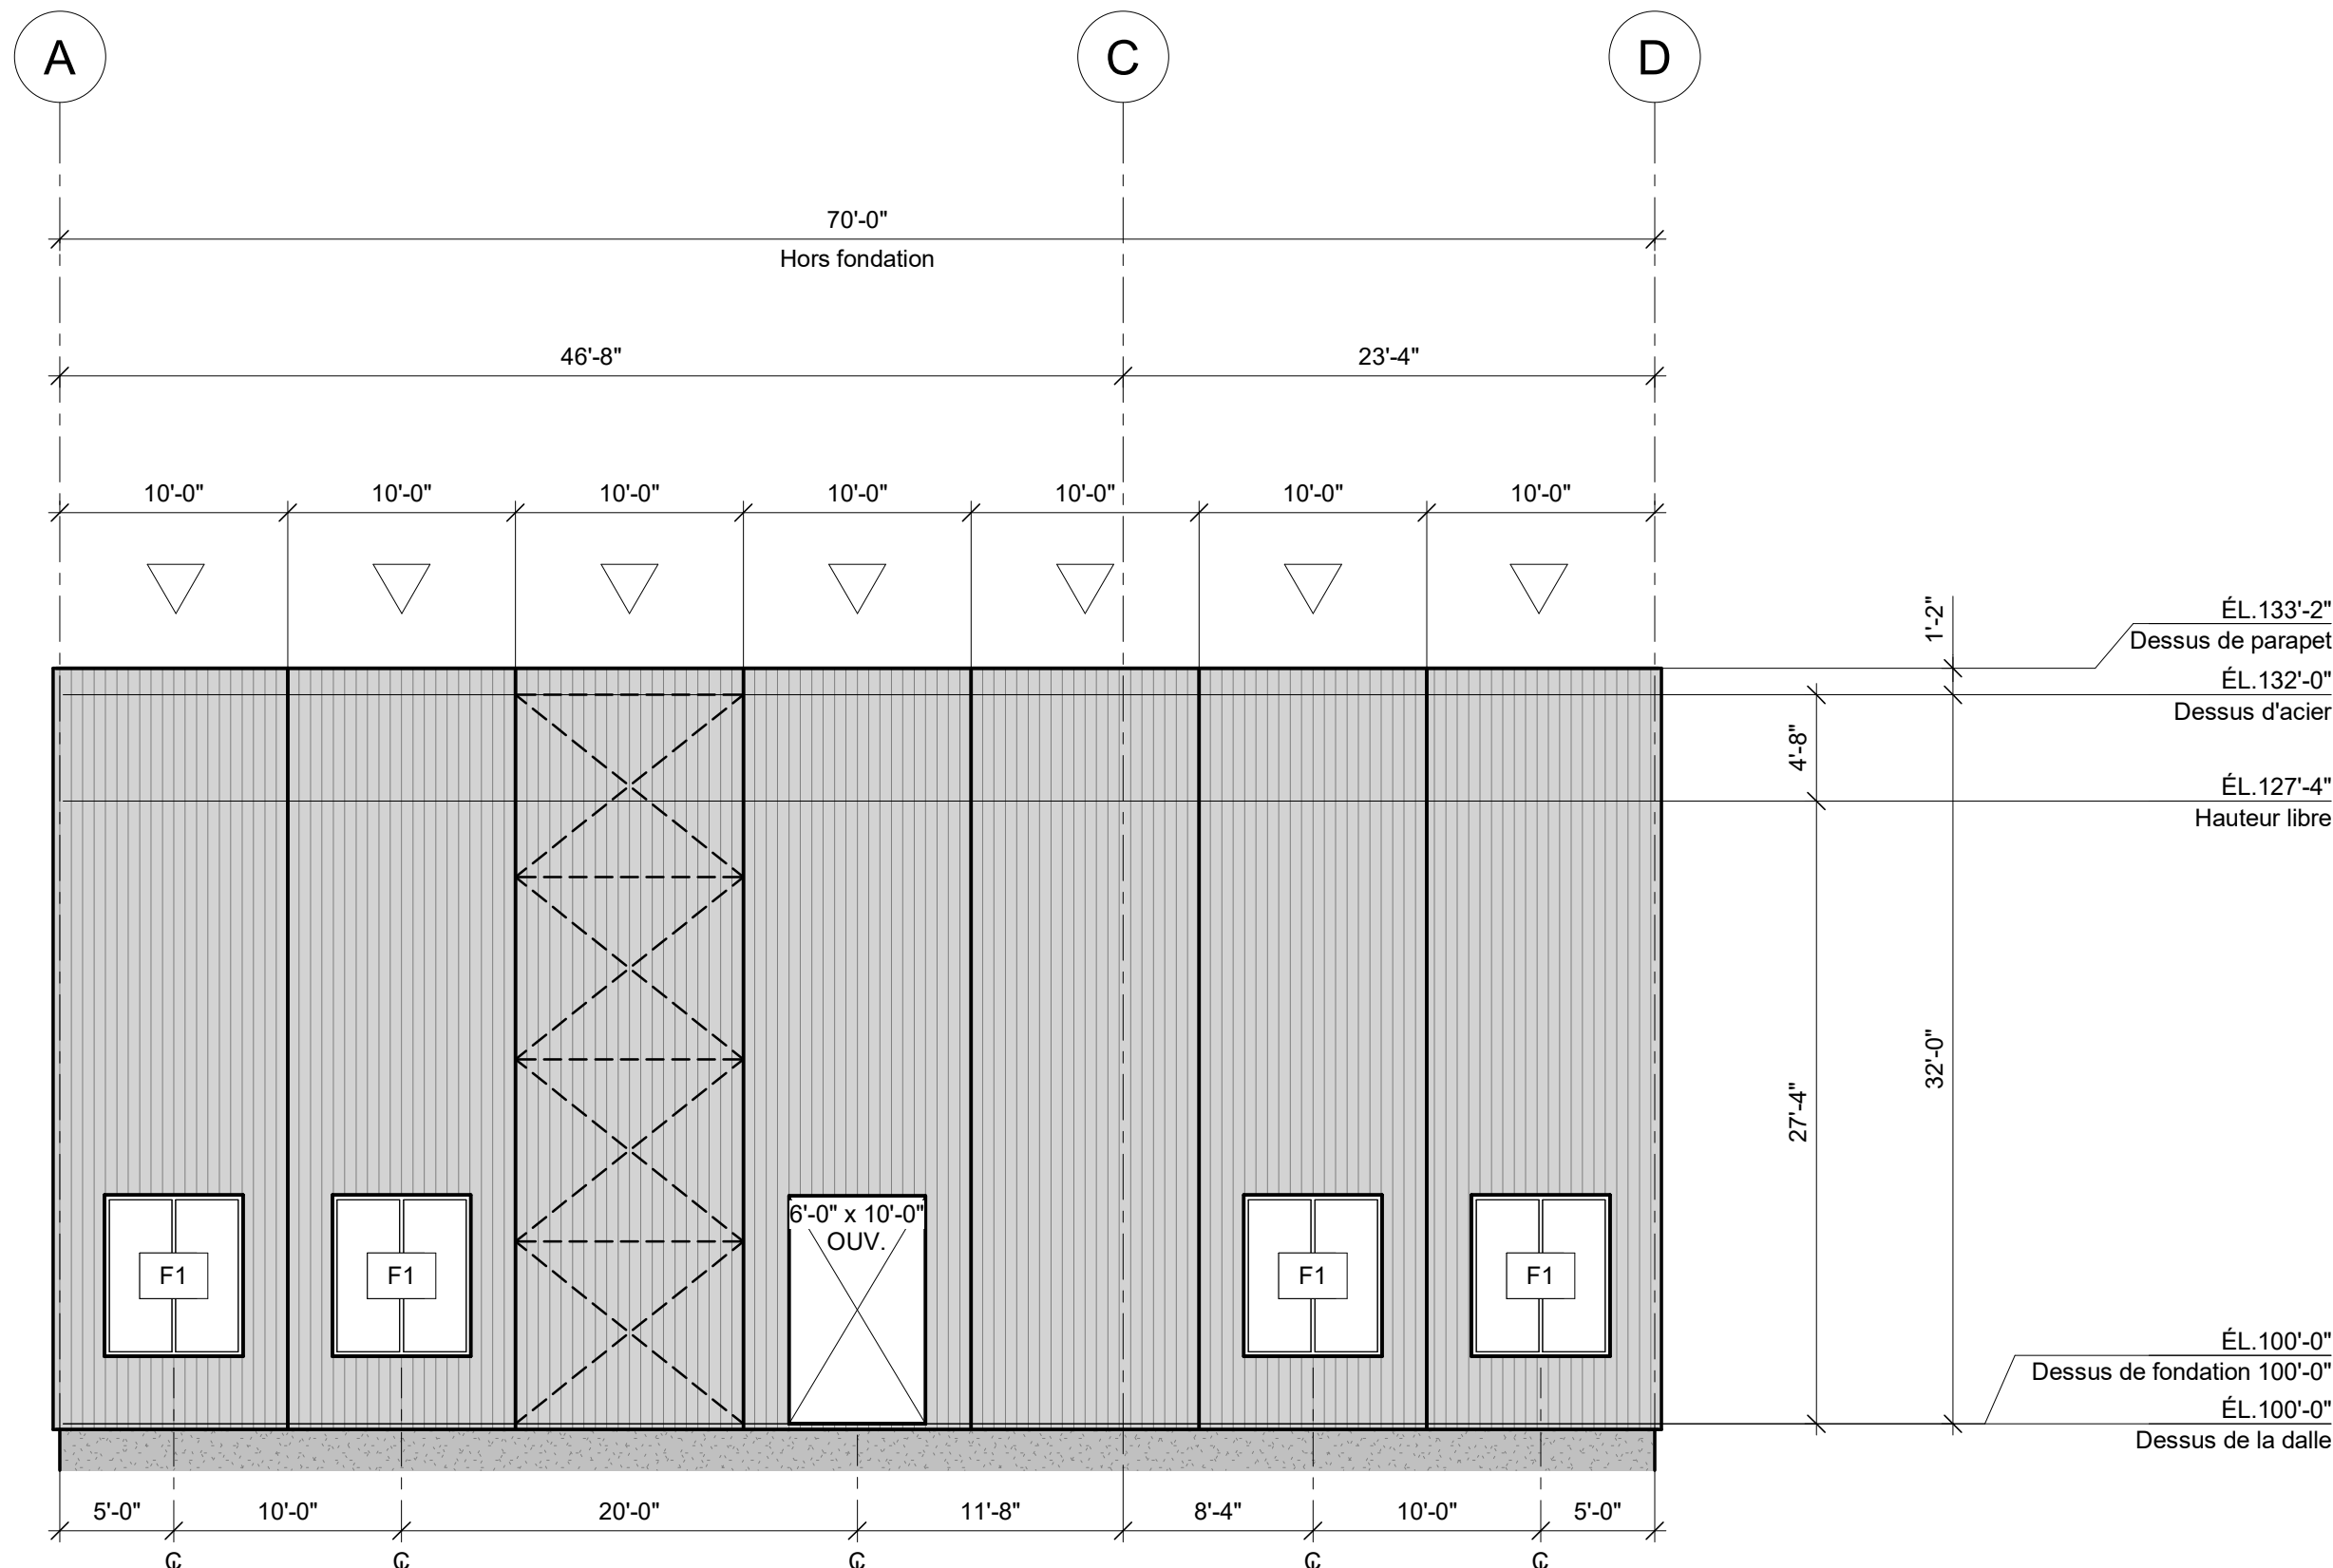

ÉLEVATION AXE 1 (OUEST)
1/8" = 1'-0"

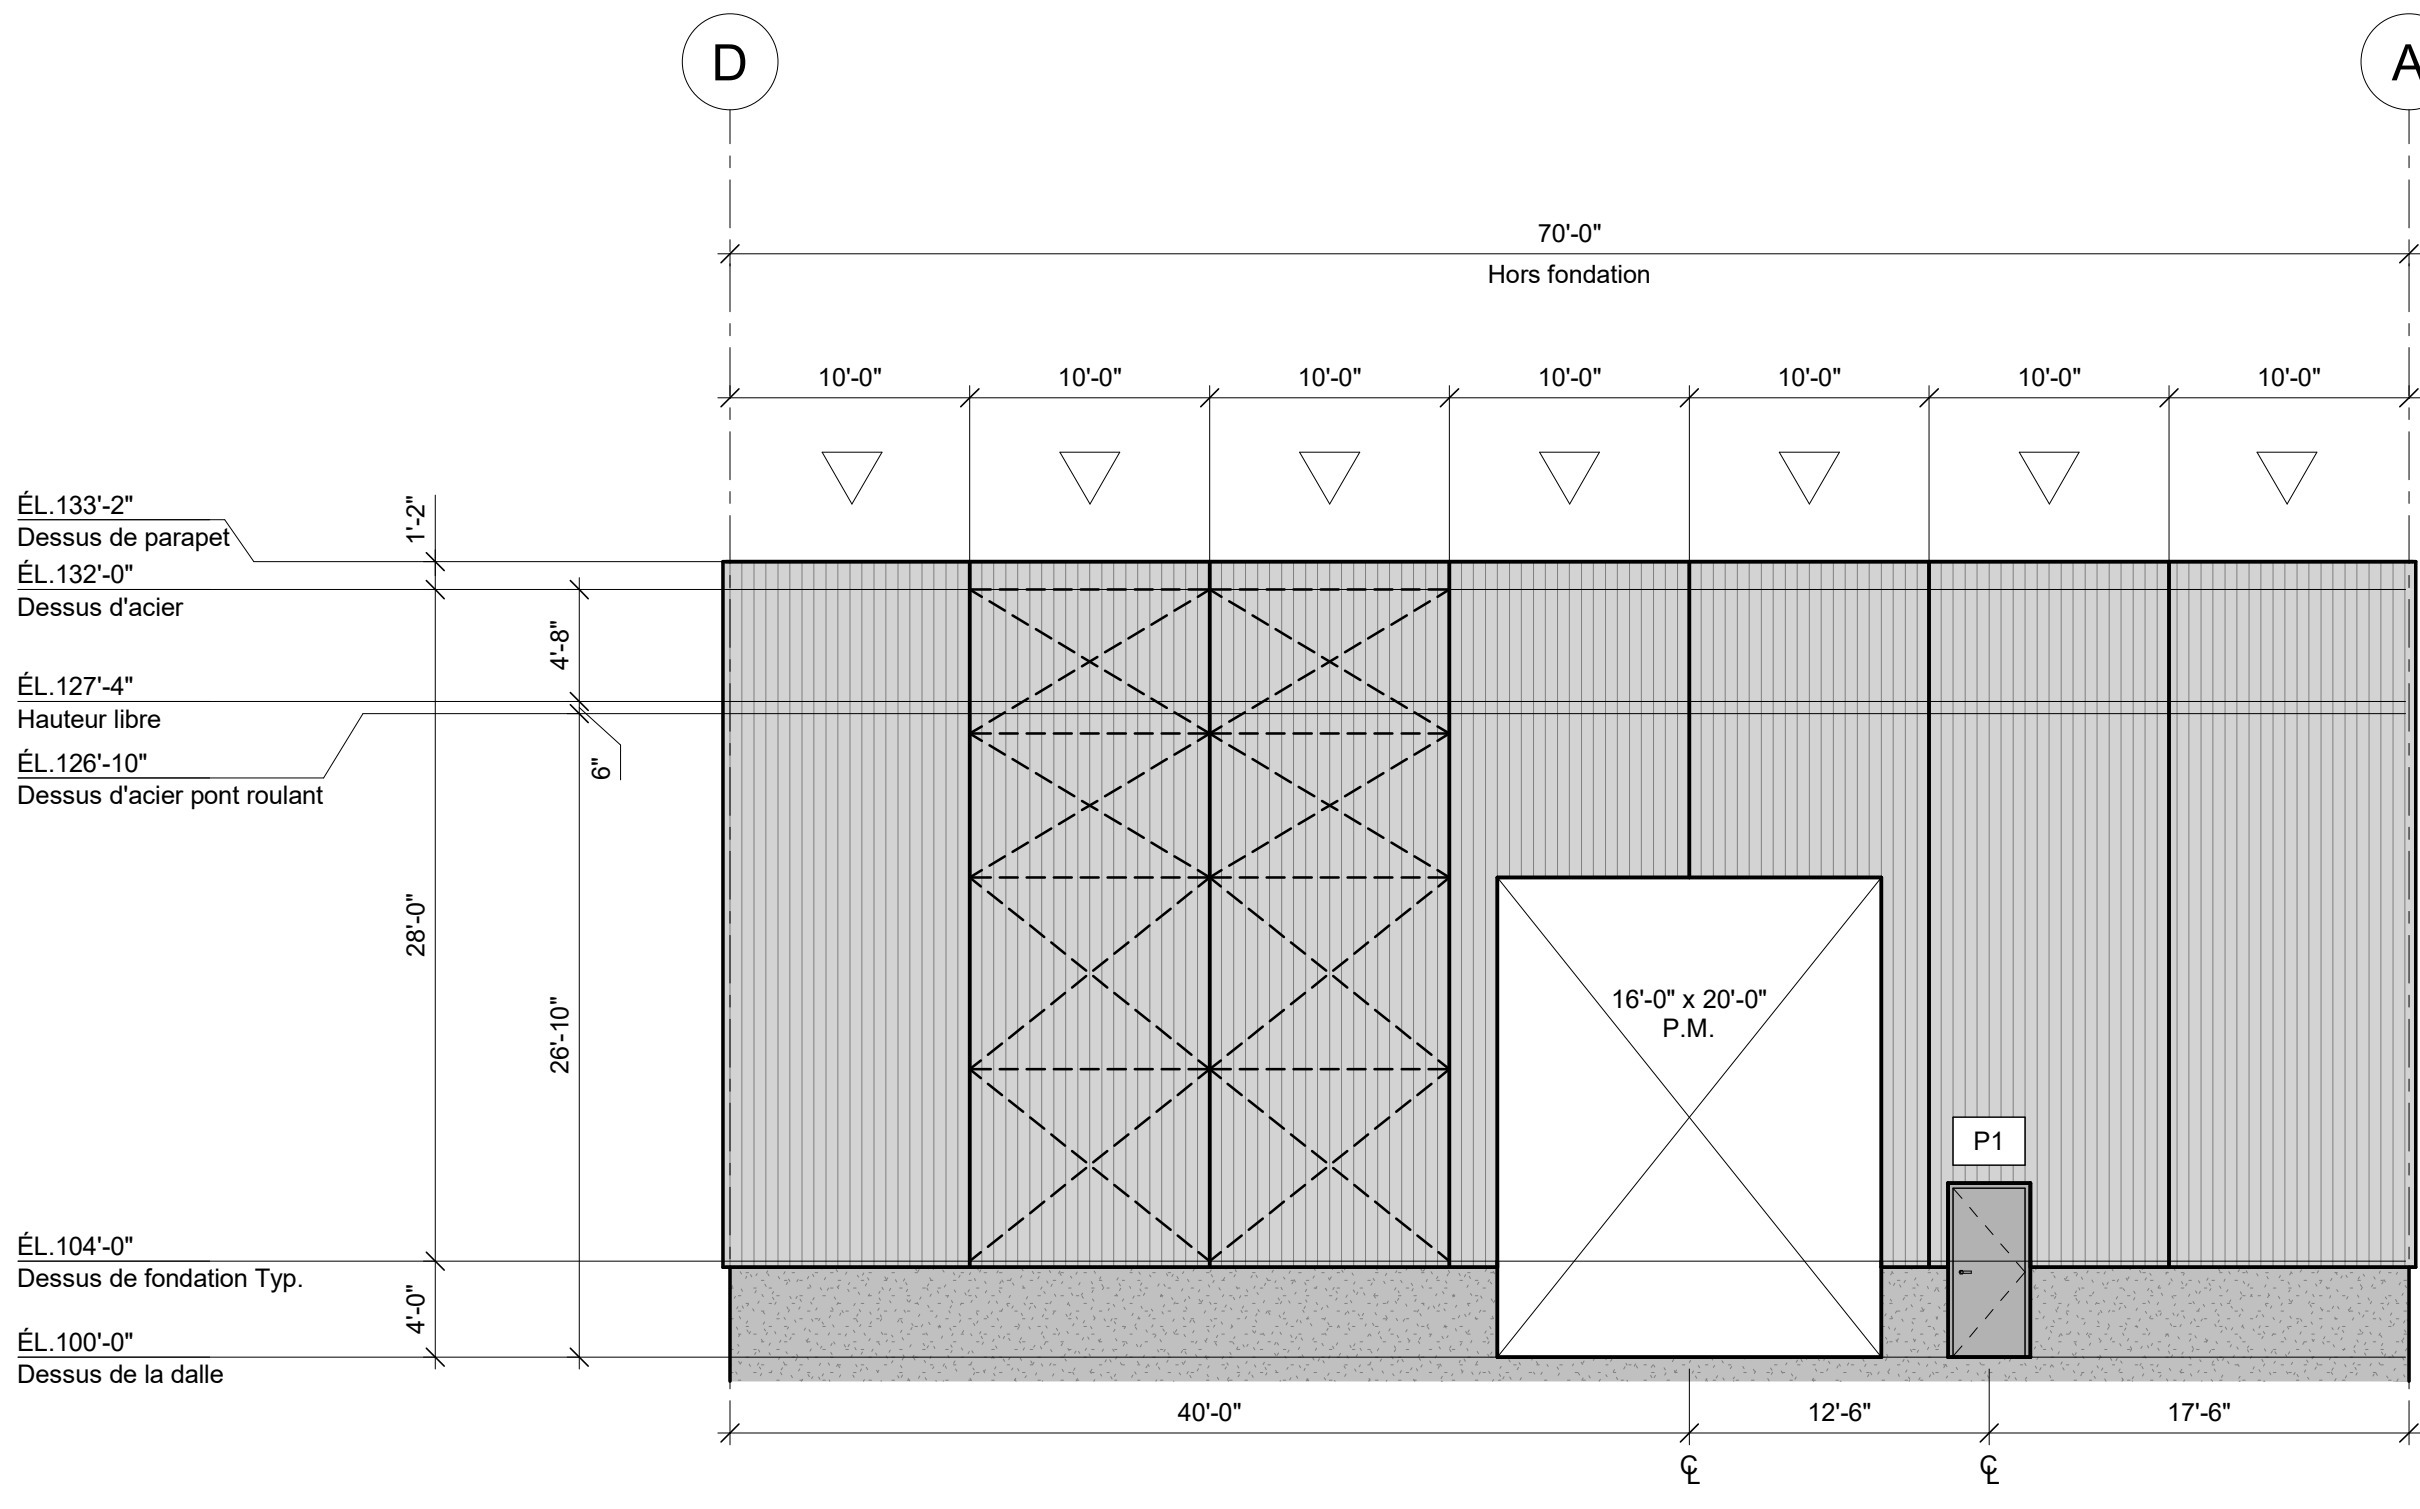

ÉLEVATION AXE 3 (EST)
1/8" = 1'-0"

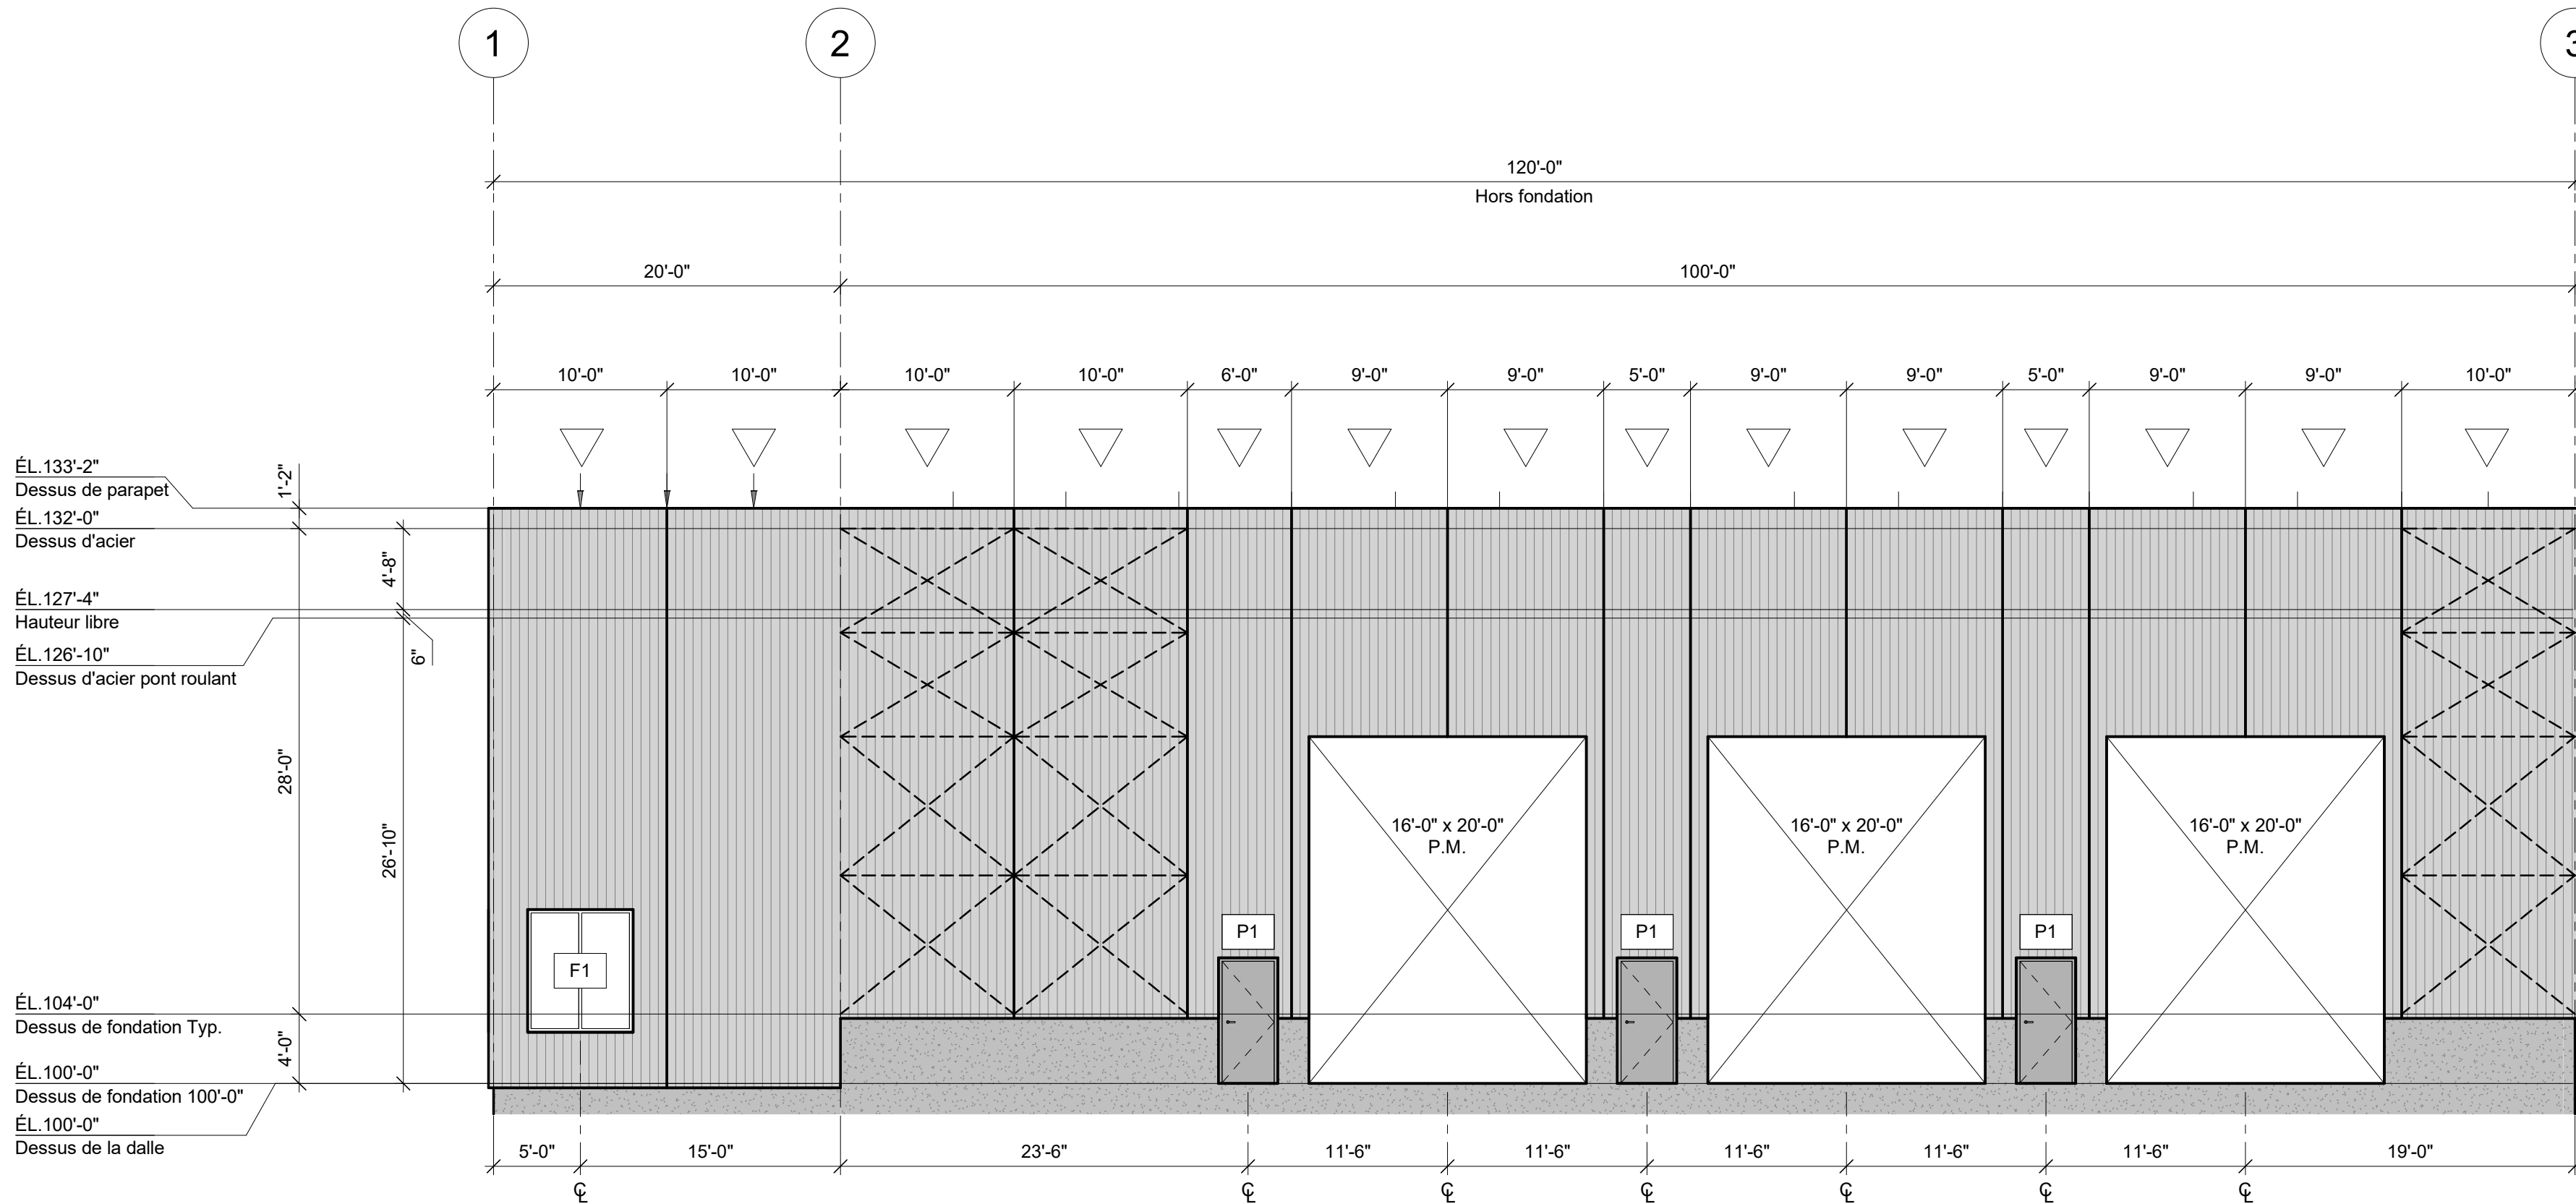

ÉLEVATION AXE D (SUD)
1/8" = 1'-0"

CÉDULE DES FENÊTRES					
Identifiant	Qté.	Installation	Description	Dimensions ext. cadre largeur X hauteur	Couleur du cadre
F1	6		Fenêtre en aluminium fixe avec bris thermique et verre scellé + Low-E argon clair (2 large x 1 haut)	6'-0 x 7'-0"	Cadre en aluminium (Blanc ext. et int.)

CÉDULE DES PORTES													
Identifiant	Qté.	Installation	Porte 18 ja.		Sens ouv.	Vitrage		Quincaillerie					
			Isolation (R12)	Dimensions 3'-0" x 7'-0"		Largeur	Hauteur	Cadre d'acier 16 ja. avec bris thermique	(3) Pentures @ tige fixe	Poignée seulement	Barre panique sans poignée ext. 22EO	Barre panique avec poignée ext. 230L	Verrou en surface (Porte inactive)
P1	4												

CÉDULE DES OUVERTURES POUR P.M., P.P. ET AUTRES			
Total	Type	Tag	Commentaires
1	6'-0" x 10'-0"	OUV.	
4	16'-0" x 20'-0"	P.M.	
Total général: 5			

NOTE POUR LE CONTRACTEUR/ÉRECTEUR:

IL EST STRICTEMENT DÉFENDU DE MODIFIER, COPIER, REPRODUIRE OU DE DISTRIBUER CES DESSINS OU QUELQUES REPRÉSENTATIONS DE CES DESSINS, PAR TOUTES SOURCES DE MÉDIA INCLUANT ÉLECTRONIQUEMENT, SANS L'APPROBATION ÉCRITE DE GROUPE CANAM INC.

PRÉLIMINAIRE

NE DOIT PAS SERVIR À LA
CONSTRUCTION

2	2026/05/02	R2	J.P.	
1	2026/02/24	R1	J.P.	
REVISION	DATE	DESCRIPTION	DESS	VER.

GERANT DE PROJET	-
	-
	-
	-

DESSIN:			
DESSINE PAR	CONÇU PAR	INGÉNIEUR DU PROJET	ÉCHELLE:
J.P.			COMME INDIQUÉ
VÉRIFIÉ PAR	INGÉNIEURS CONSEILS / ARCHITECTES	DATE (jj/mm/aaaa) :	
		19/09/2025	

CLIENT: Entreprise R. et G. St-Laurent Inc



SCEAU PROFESSIONNEL

PROJET

Bâtiment 70x120
Baie-Comeau, Québec

TITRE

CROQUIS PRÉLIMINAIRE -
ÉLÉVATIONS

NUMÉRO CONTRAT P2025-151	NUMÉRO DESSIN Mx501	DIVISION	REVISION 2
-----------------------------	------------------------	----------	---------------

Initiales