

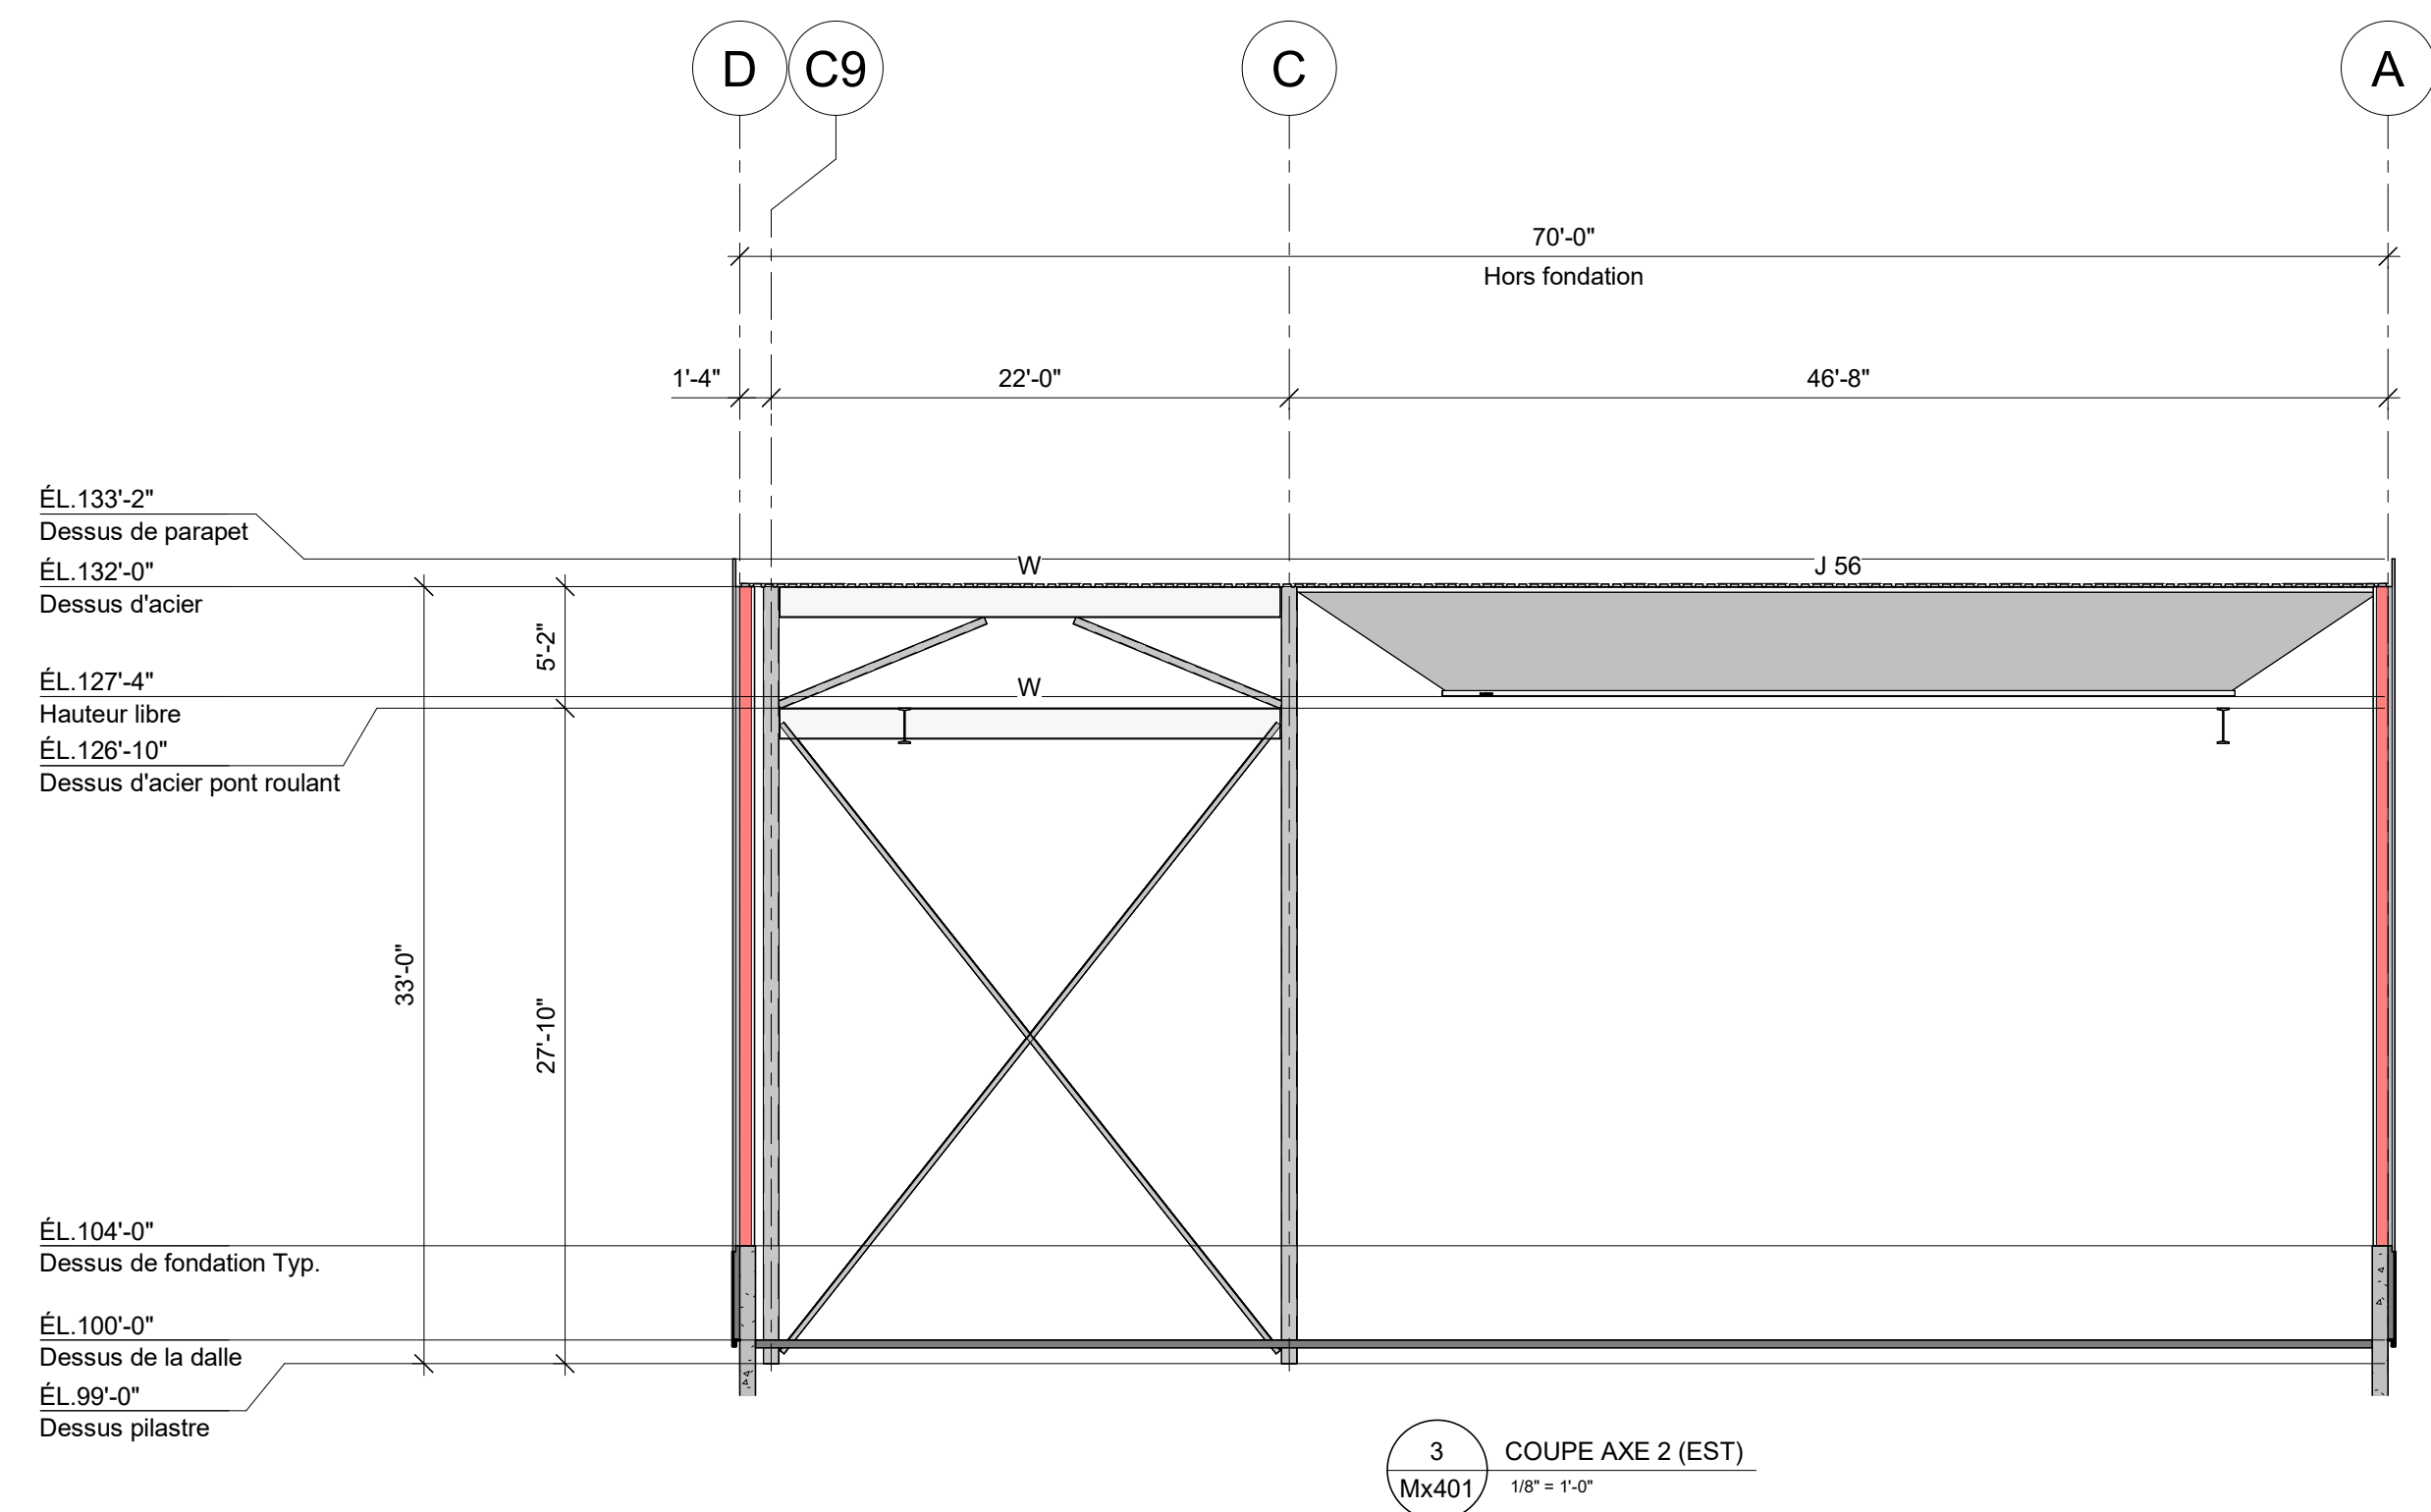


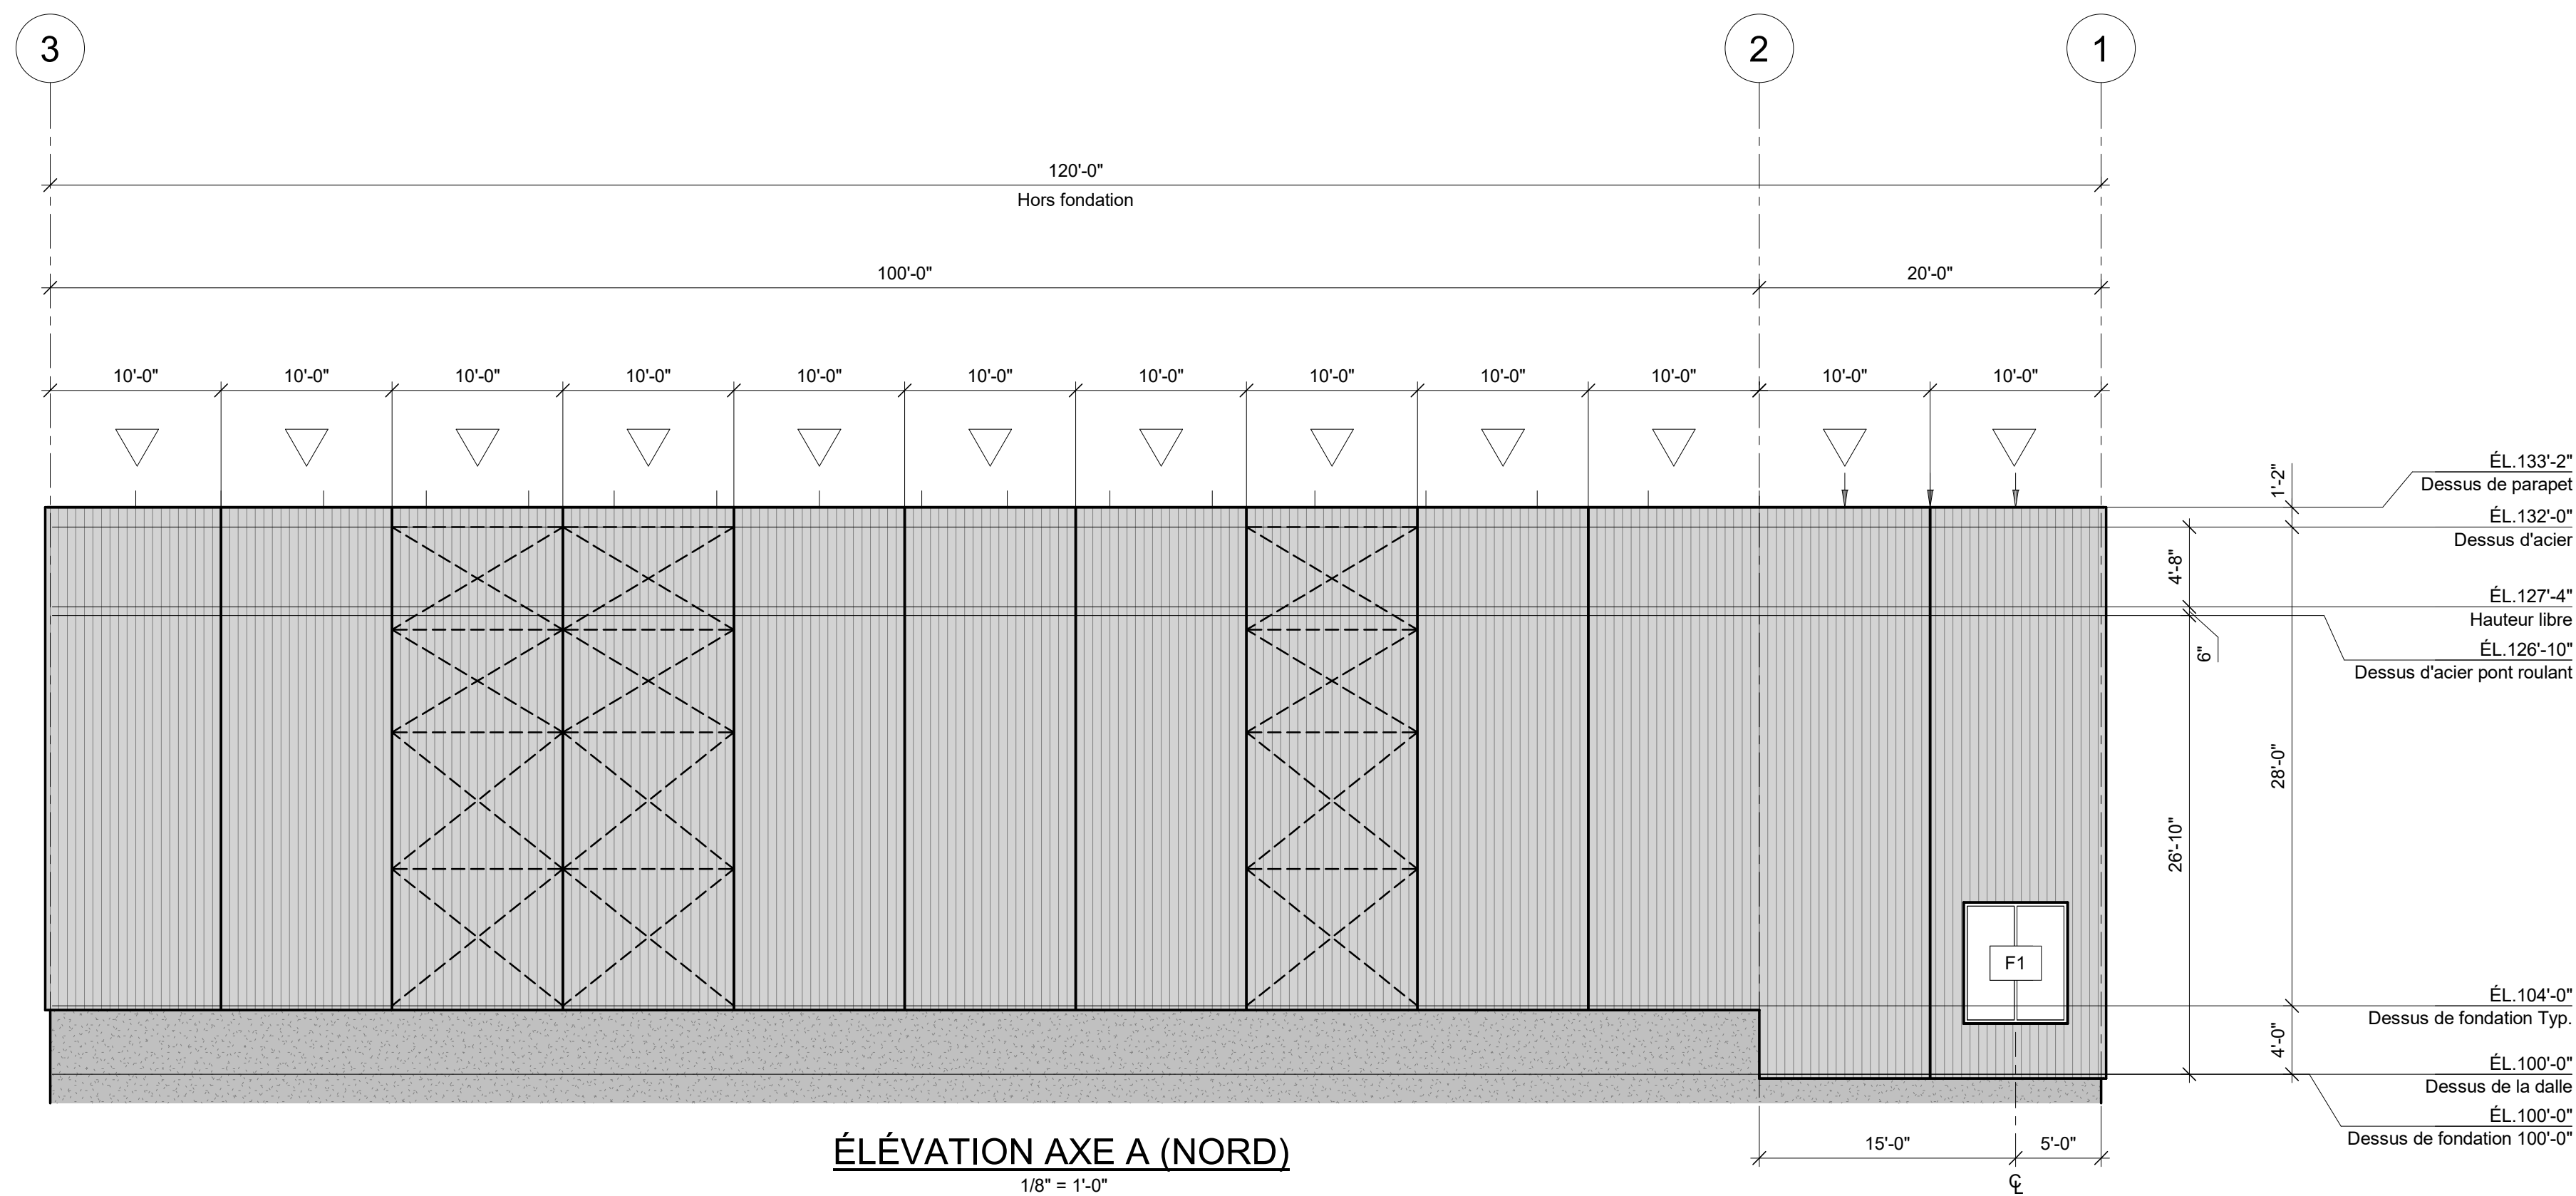

CÉDULE DES FENÊTRES						
Identifiant	Qté.	Installation	Description	Dimensions ext. cadre largeur X hauteur	Couleur du cadre	Remarques
F1	6		Fenêtre en aluminium fixe avec bris thermique et verre scellé + Low-E argon clair (2 large x 1 haut)	6'-0 x 7'-0"	Cadre en aluminium (Blanc ext. et int.)	

[illegible]

CÉDULE DES OUVERTURES POUR P.M., P.P. ET AUTRES			
Total	Type	Tag	Commentaires
1	6'-0" x 10'-0"	OUV.	
4	16'-0" x 20'-0"	P.M.	
Total général: 5			

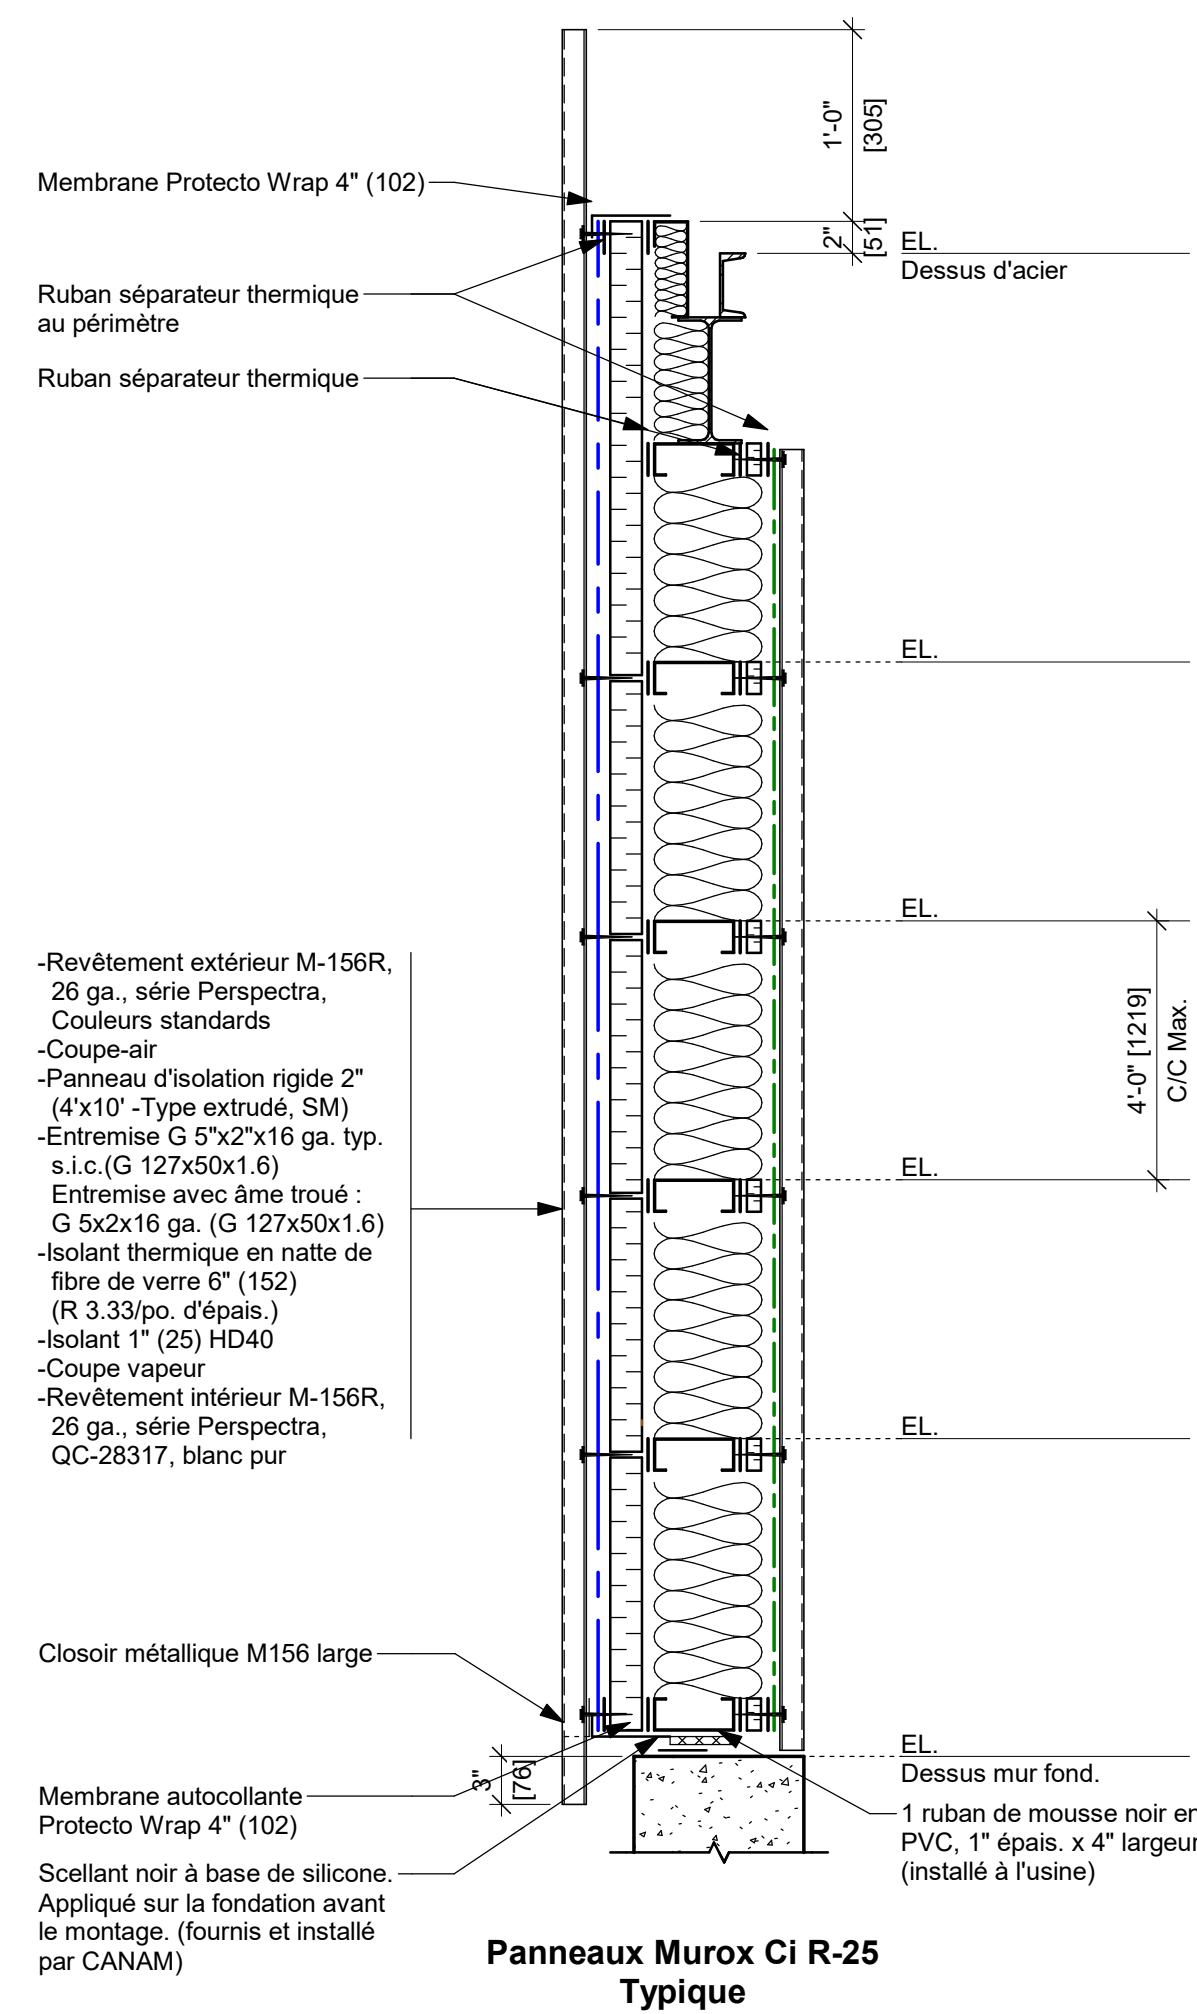

NOTE POUR LE CONTRACTEUR/ÉRECTEUR:

IL EST STRICTEMENT DÉFENDU DE MODIFIER, COPIER, REPRODUIRE OU DE DISTRIBUER CES DESSINS OU QUELQUES REPRÉSENTATIONS DE CES DESSINS, PAR TOUTES SOURCES DE MÉDIA INCLUANT ÉLECTRONIQUEMENT, SANS L'APPROBATION ÉCRITE DE GROUPE CANAM INC.

PRÉLIMINAIRE

NE DOIT PAS SERVIR À LA
CONSTRUCTION

2	2026/05/02	R2	J.P.	
1	2026/02/24	R1	J.P.	
REVISION	DATE	DESCRIPTION	DESS	VÉR.
GERANT DE PROJET				
-				
-				
CLIENT: Entreprise R. et G. St-Laurent Inc.



11505, 1re Avenue, bureau 500, Saint-Georges Beauce
Québec, Canada, G5Y 7X3
Téléphone : (418) 228-8031
Sans frais : (877) 499-6049
www.canam.com

SCEAU PROFESSIONNEL

PROJE

Bâtiment 70x120
Baie-Comeau, Québec

TITRE

CROQUIS PRÉLIMINAIRE - ÉLÉVATION
ET COUPE DE MUR

NUMÉRO CONTRAT P2025-151	NUMÉRO DESSIN Mx502	DIVISION	RÉVISION 
-----------------------------	------------------------	----------	---