


NORD POUR ÉRECTION SEULEMENT

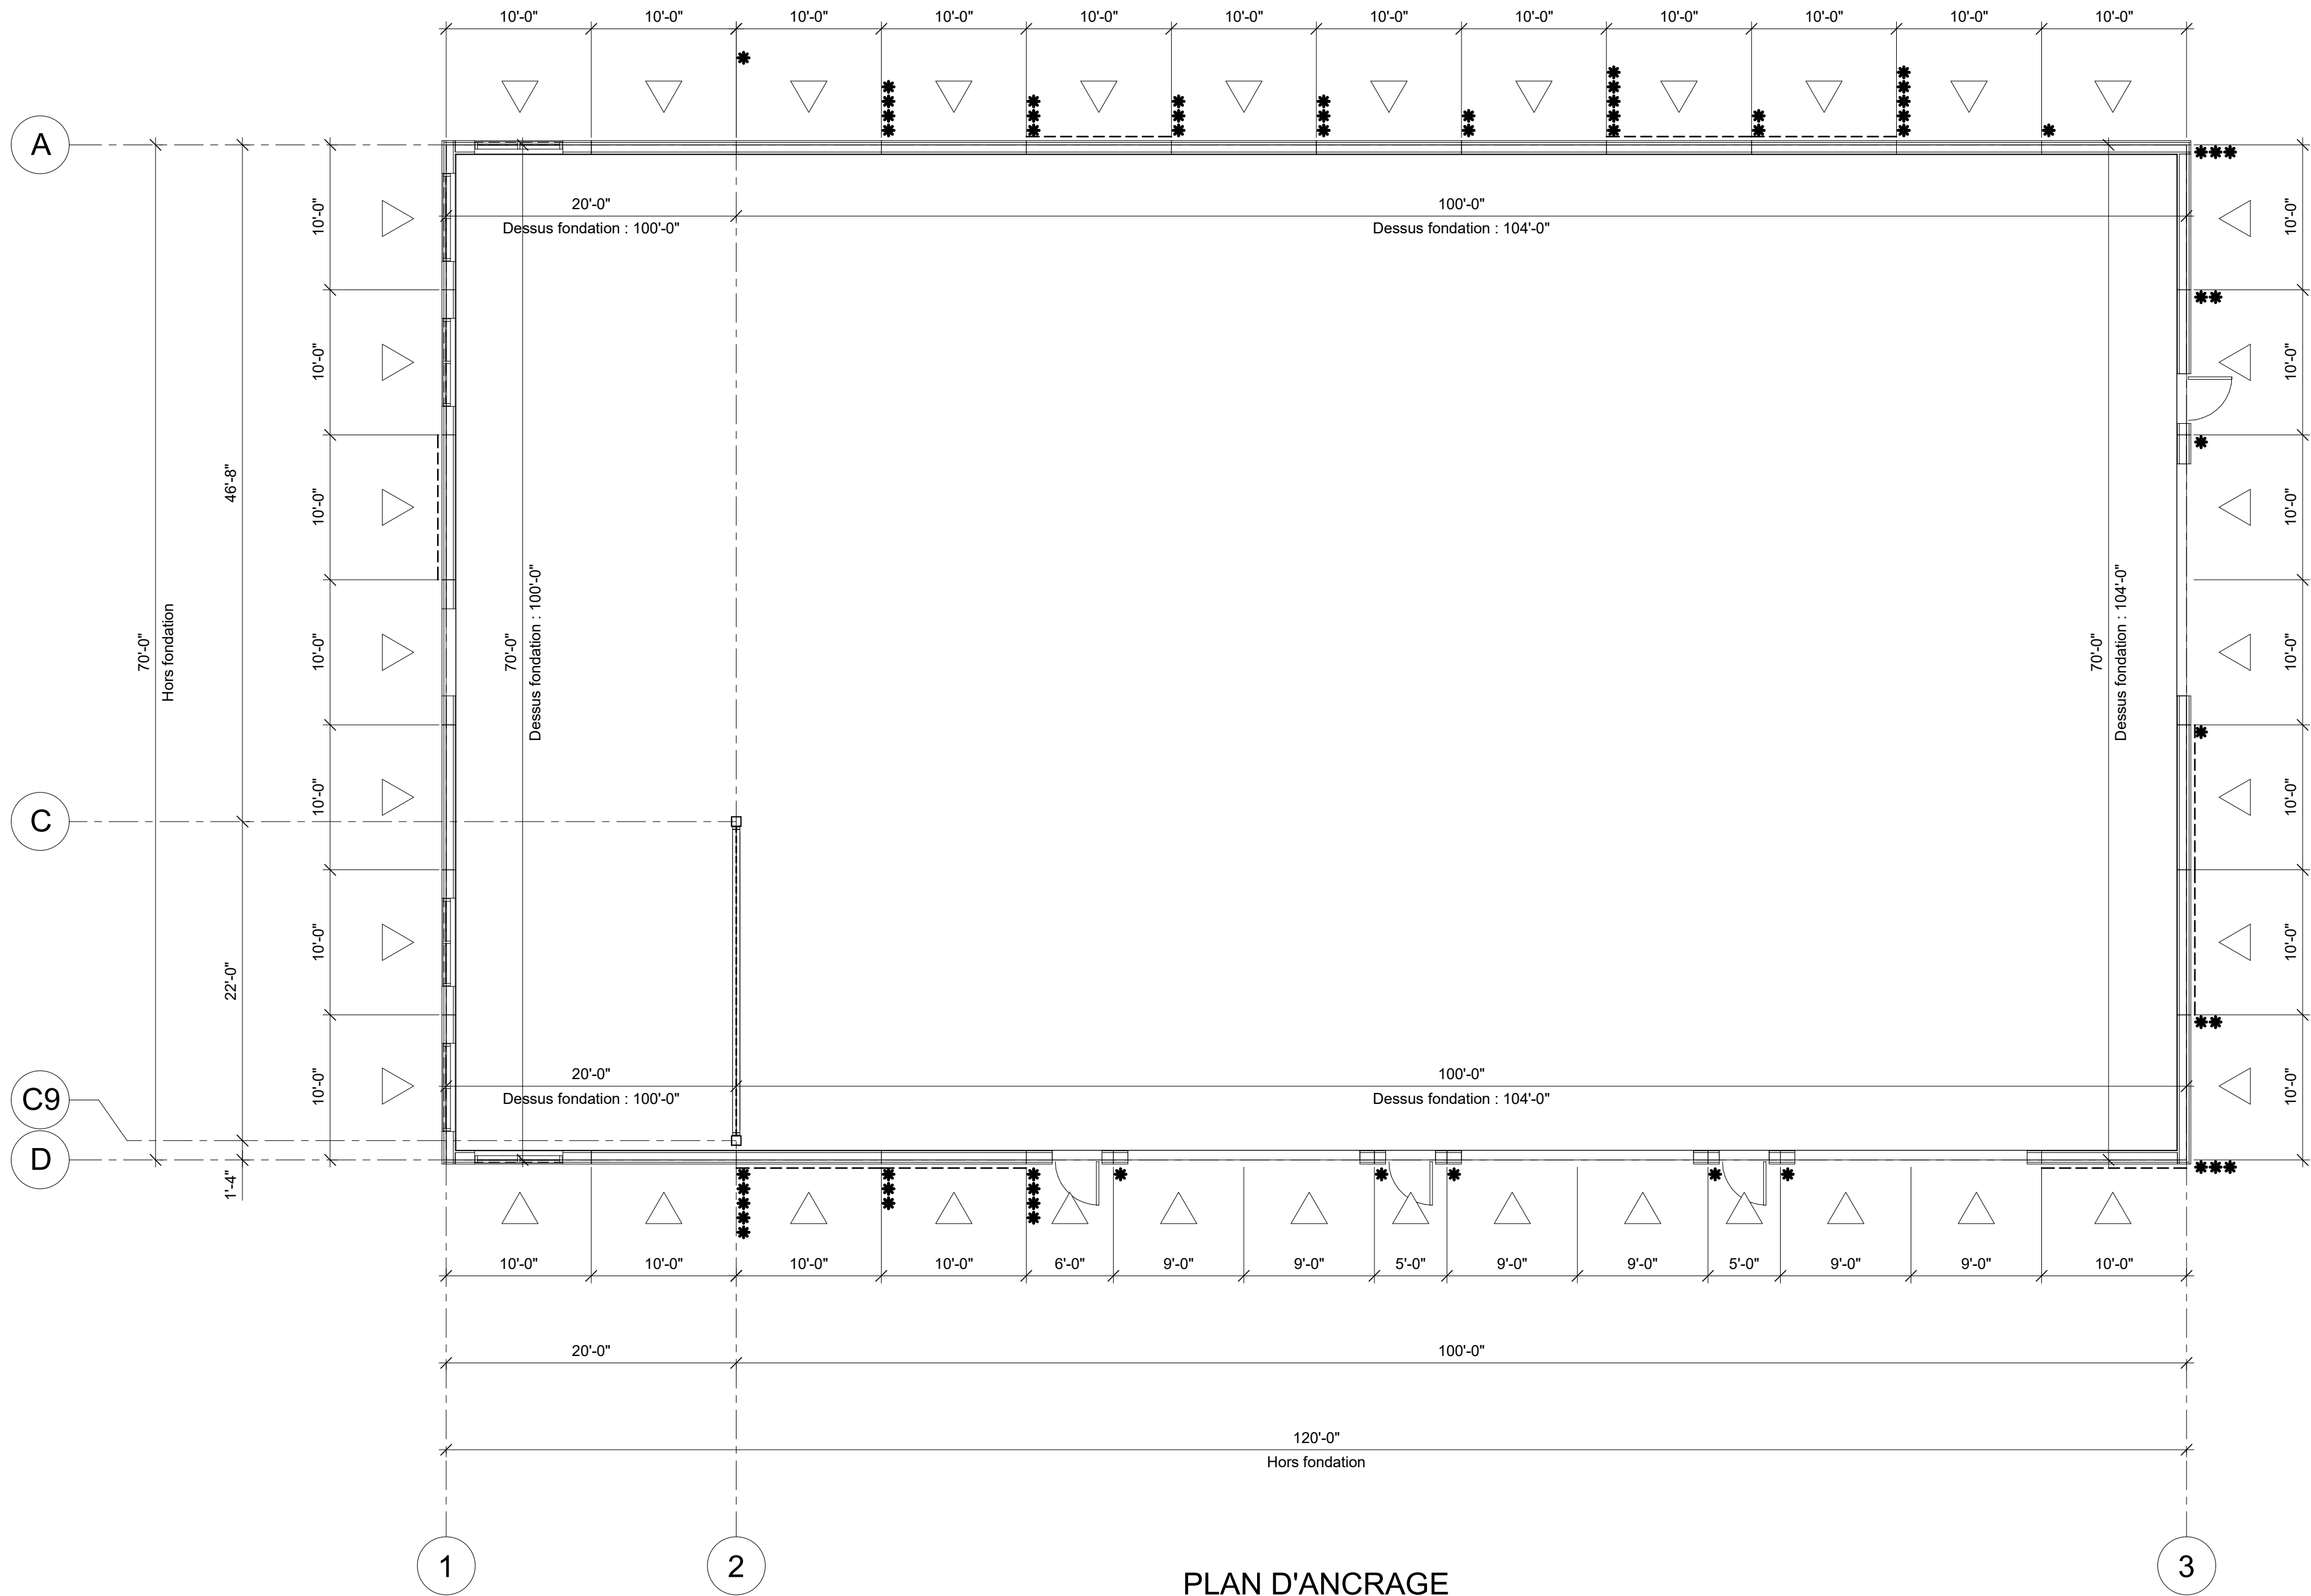

PLAN D'ANCRAGE
1/8" = 1'-0"

Bâtiment 70x120																
RÉACTIONS PRÉLIMINAIRES AUX FONDATIONS COLONNES DE PANNEAUX "MUROX" @ 10' c/c																
NOTE : TOUTES LES CHARGES DE SERVICES SONT EXPRIMÉES EN kips, TYP. S.I.C.. NE PAS UTILISER POUR CONSTRUCTION																
AXE	CHARGES VERTICALES							EFFORTS À LA BASE			CONTREVENTEMENTS					
	D	D	D	S	Lxc	C	W	PERP. À LA FONDATION			E		W		C	
	POIDS DU MUR	COL	COL				SOUL. BRUT	W	E	C	H.	V.	H.	V.	H.	V.
1	2.6	7.5	0.1	2.0	0.0	0.0	-0.5	3.8	0.0	0.0	10.5	± 12.3	6.1	± 8.1		
3	2.6	0.5	0.1	2.0	0.0	0.0	-0.5	3.3	0.0	0.0	16.7	± 46.8	7.5	± 21.0	2.4	± 6.7
3*	3.8	0.8	0.2	3.0	0.0	0.0	-0.7	5.0	0.0	0.0	16.7	± 46.8	7.5	± 21.0	2.4	± 6.7
3**	2.6	0.5	1.1	2.0	0.0	19.0	-0.5	3.3	0.0	0.0	16.7	± 46.8	7.5	± 21.0	2.4	± 6.7
3***	1.3	0.3	1.6	1.0	0.0	23.0	-0.2	1.7	0.0	0.0						
A (1 à 2) & D (1 à 2)	2.6	8.8	1.8	28.1	2.0	0.0	-6.9	3.8	0.0	0.0	10.5	± 12.3	10.8	± 12.6		
A (2 à 3) & D (2 à 3)	2.6	8.1	1.9	30.9	0.0	0.0	-7.6	3.3	0.0	0.0	13.2	± 37.0	3.6	± 10.1	1.0	± 2.8
D*	3.1	10.3	4.4	39.2	0.0	27.0	-9.6	4.0	0.0	0.0						
D**	3.6	11.3	4.7	43.2	0.0	27.0	-10.6	4.6	0.0	0.0	13.2	± 37.0	3.6	± 10.1	1.0	± 2.8
D***	2.6	8.5	3.1	32.6	0.0	16.1	-8.0	3.3	0.0	0.0	13.2	± 37.0	3.6	± 10.1	1.0	± 2.8
D****	2.0	6.8	2.1	26.1	0.0	6.9	-6.4	2.6	0.0	0.0	13.2	± 37.0	3.6	± 10.1	1.0	± 2.8
A*	2.6	8.1	3.9	30.9	0.0	27.0	-7.6	3.3	0.0	0.0						
A**	2.6	8.5	5.0	32.6	0.0	40.5	-8.0	3.3	0.0	0.0						
A***	2.6	8.5	3.4	32.6	0.0	18.9	-8.0	3.3	0.0	0.0	13.2	± 37.0	3.6	± 10.1	1.0	± 2.8
A****	2.6	8.5	3.1	32.6	0.0	16.1	-8.0	3.3	0.0	0.0						
A*****	2.6	8.5	2.6	32.6	0.0	8.1	-8.0	3.3	0.0	0.0	13.2	± 37.0	3.6	± 10.1	1.0	± 2.8
D*****	2.6	9.2	2.0	32.6	0.0	0.0	-8.0	3.8	0.0	0.0	13.2	± 37.0	3.6	± 10.1	1.0	± 2.8
A*****	2.6	9.2	2.0	32.6	0.0	0.0	-8.0	3.8	0.0	0.0	10.5	± 12.3	10.8	± 12.6		

CÉDULE PRÉLIMINAIRE DES COLONNES INTÉRIEURES

Bâtiment 70x120

TOUTES LES CHARGES DE SERVICES SONT EXPRIMÉES EN kips, TYP. S.I.C.. NE PAS UTILISER POUR CONSTRUCTION

NO. COL.	CHARGES VERTICALES						CONTREVENTEMENTS								
	D	D	S	Lxc	C	W	E		W		C				
	COL	COL				SOUL. BRUT	H(N/S)	H(E/O)	V.	H(N/S)	H(E/O)	V.	H(N/S)	H(E/O)	V.
1	9.8	0.7	6.2	11.7	15.2	-1.5	0.0	0.0	± 0.0	0.0	0.0	± 0.0	0.0	0.0	0.0
2	19.6	1.9	12.5	23.3	9.5	-3.1	0.0	0.0	± 0.0	0.0	0.0	± 0.0	0.0	0.0	0.0
3	19.6	1.9	12.5	23.3	9.5	-3.1	56.6	0.0	± 75.2	26.6	0.0	± 34.6	4.8	0.0	7.2
4	9.8	0.7	6.2	11.7	15.2	-1.5	56.6	0.0	± 75.2	26.6	0.0	± 34.6	4.8	0.0	7.2