





NORD POUR ÉRECTION SEULEMENT

DIAGRAMME DE SOULÈVEMENT BRUT (NON PONDÉRÉ)

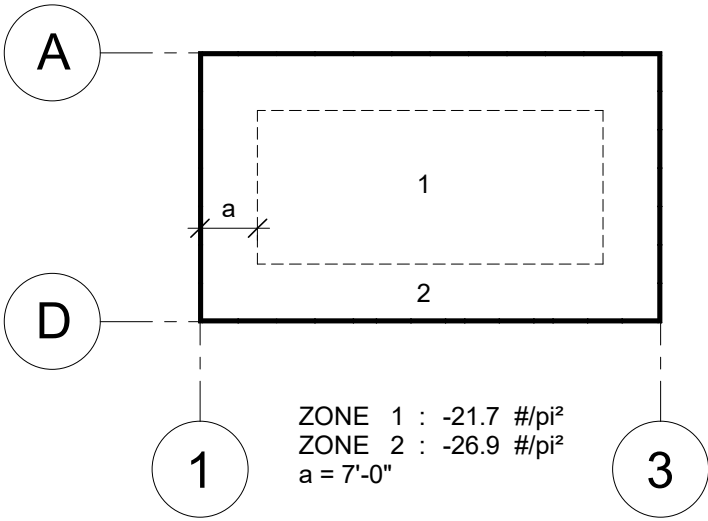

PRESSION POSITIVE DU VENT
(NON PONDÉRÉE): 12.4 #/pi²

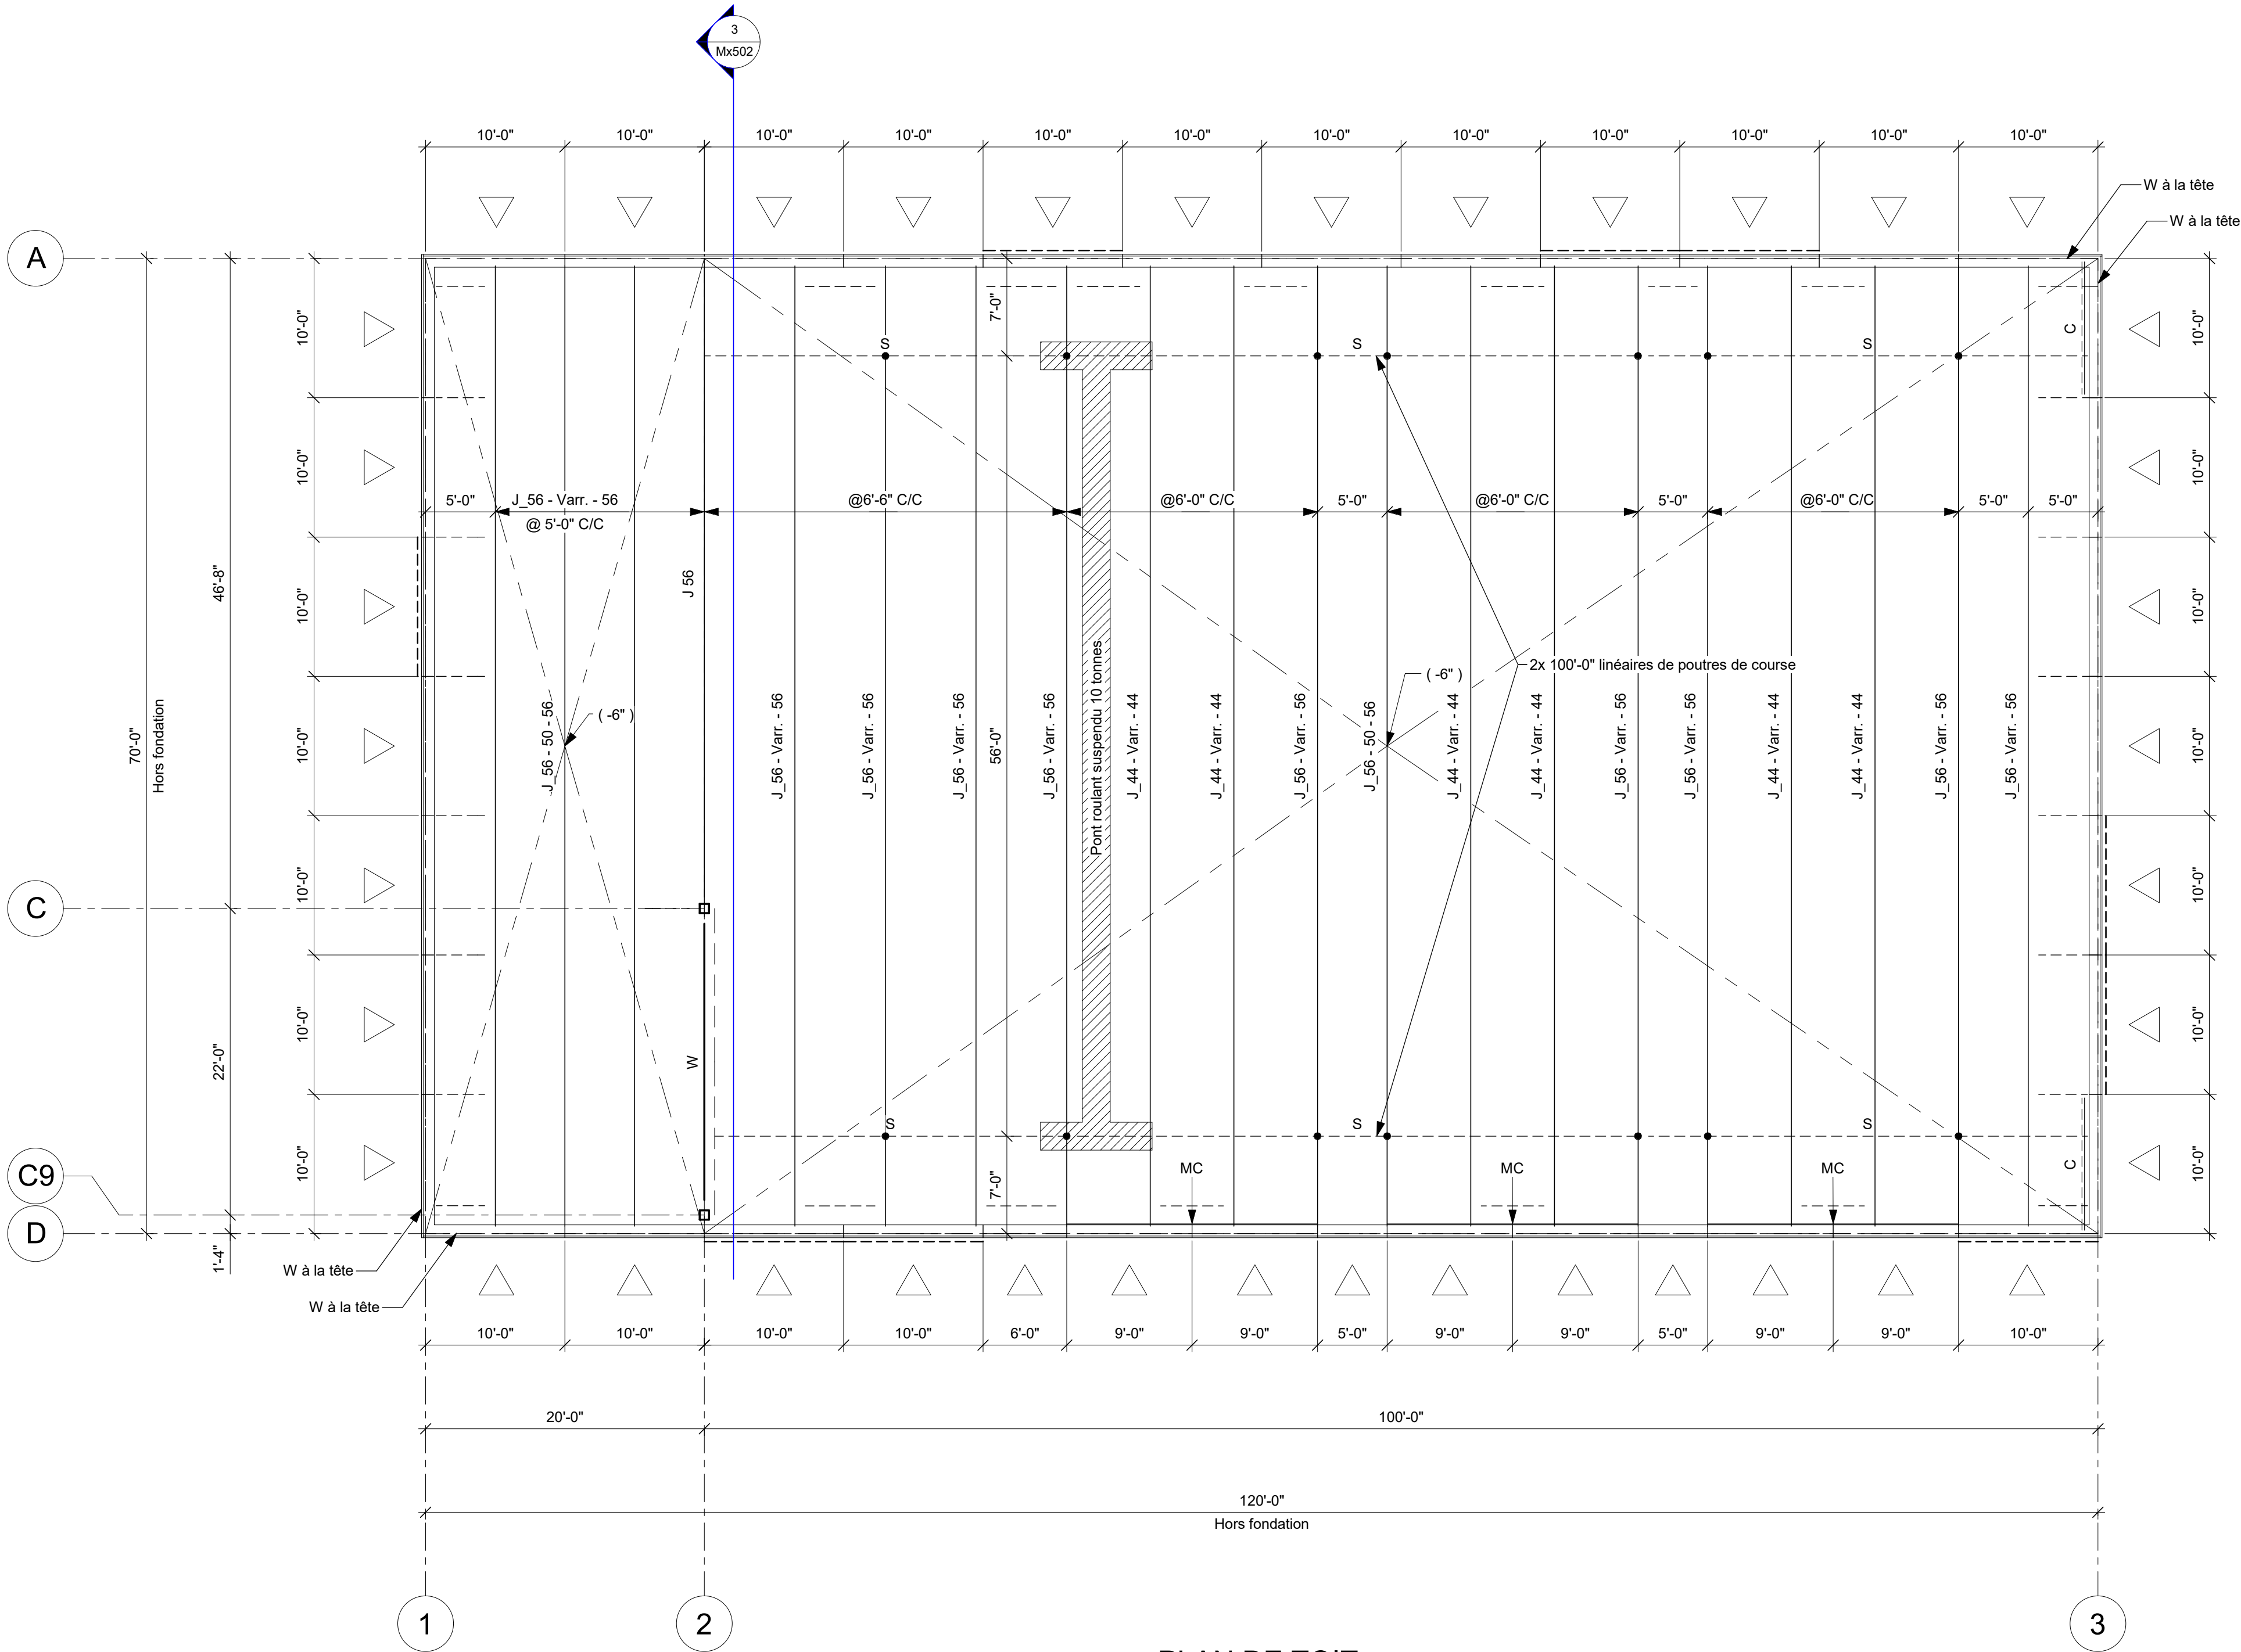

PLAN DE TOIT
1/8" = 1'-0"

TABLEAU CHARGES PONT ROULANT				
CAPACITÉ	POIDS DU PONT	CHARIOT	CHARGE MAX. PAR ROUE (DYNAMIQUE)	ESPACEMENT DES ROUES
10 Tonnes	13800 lb	1350 lb	19 kip	10'-6"