



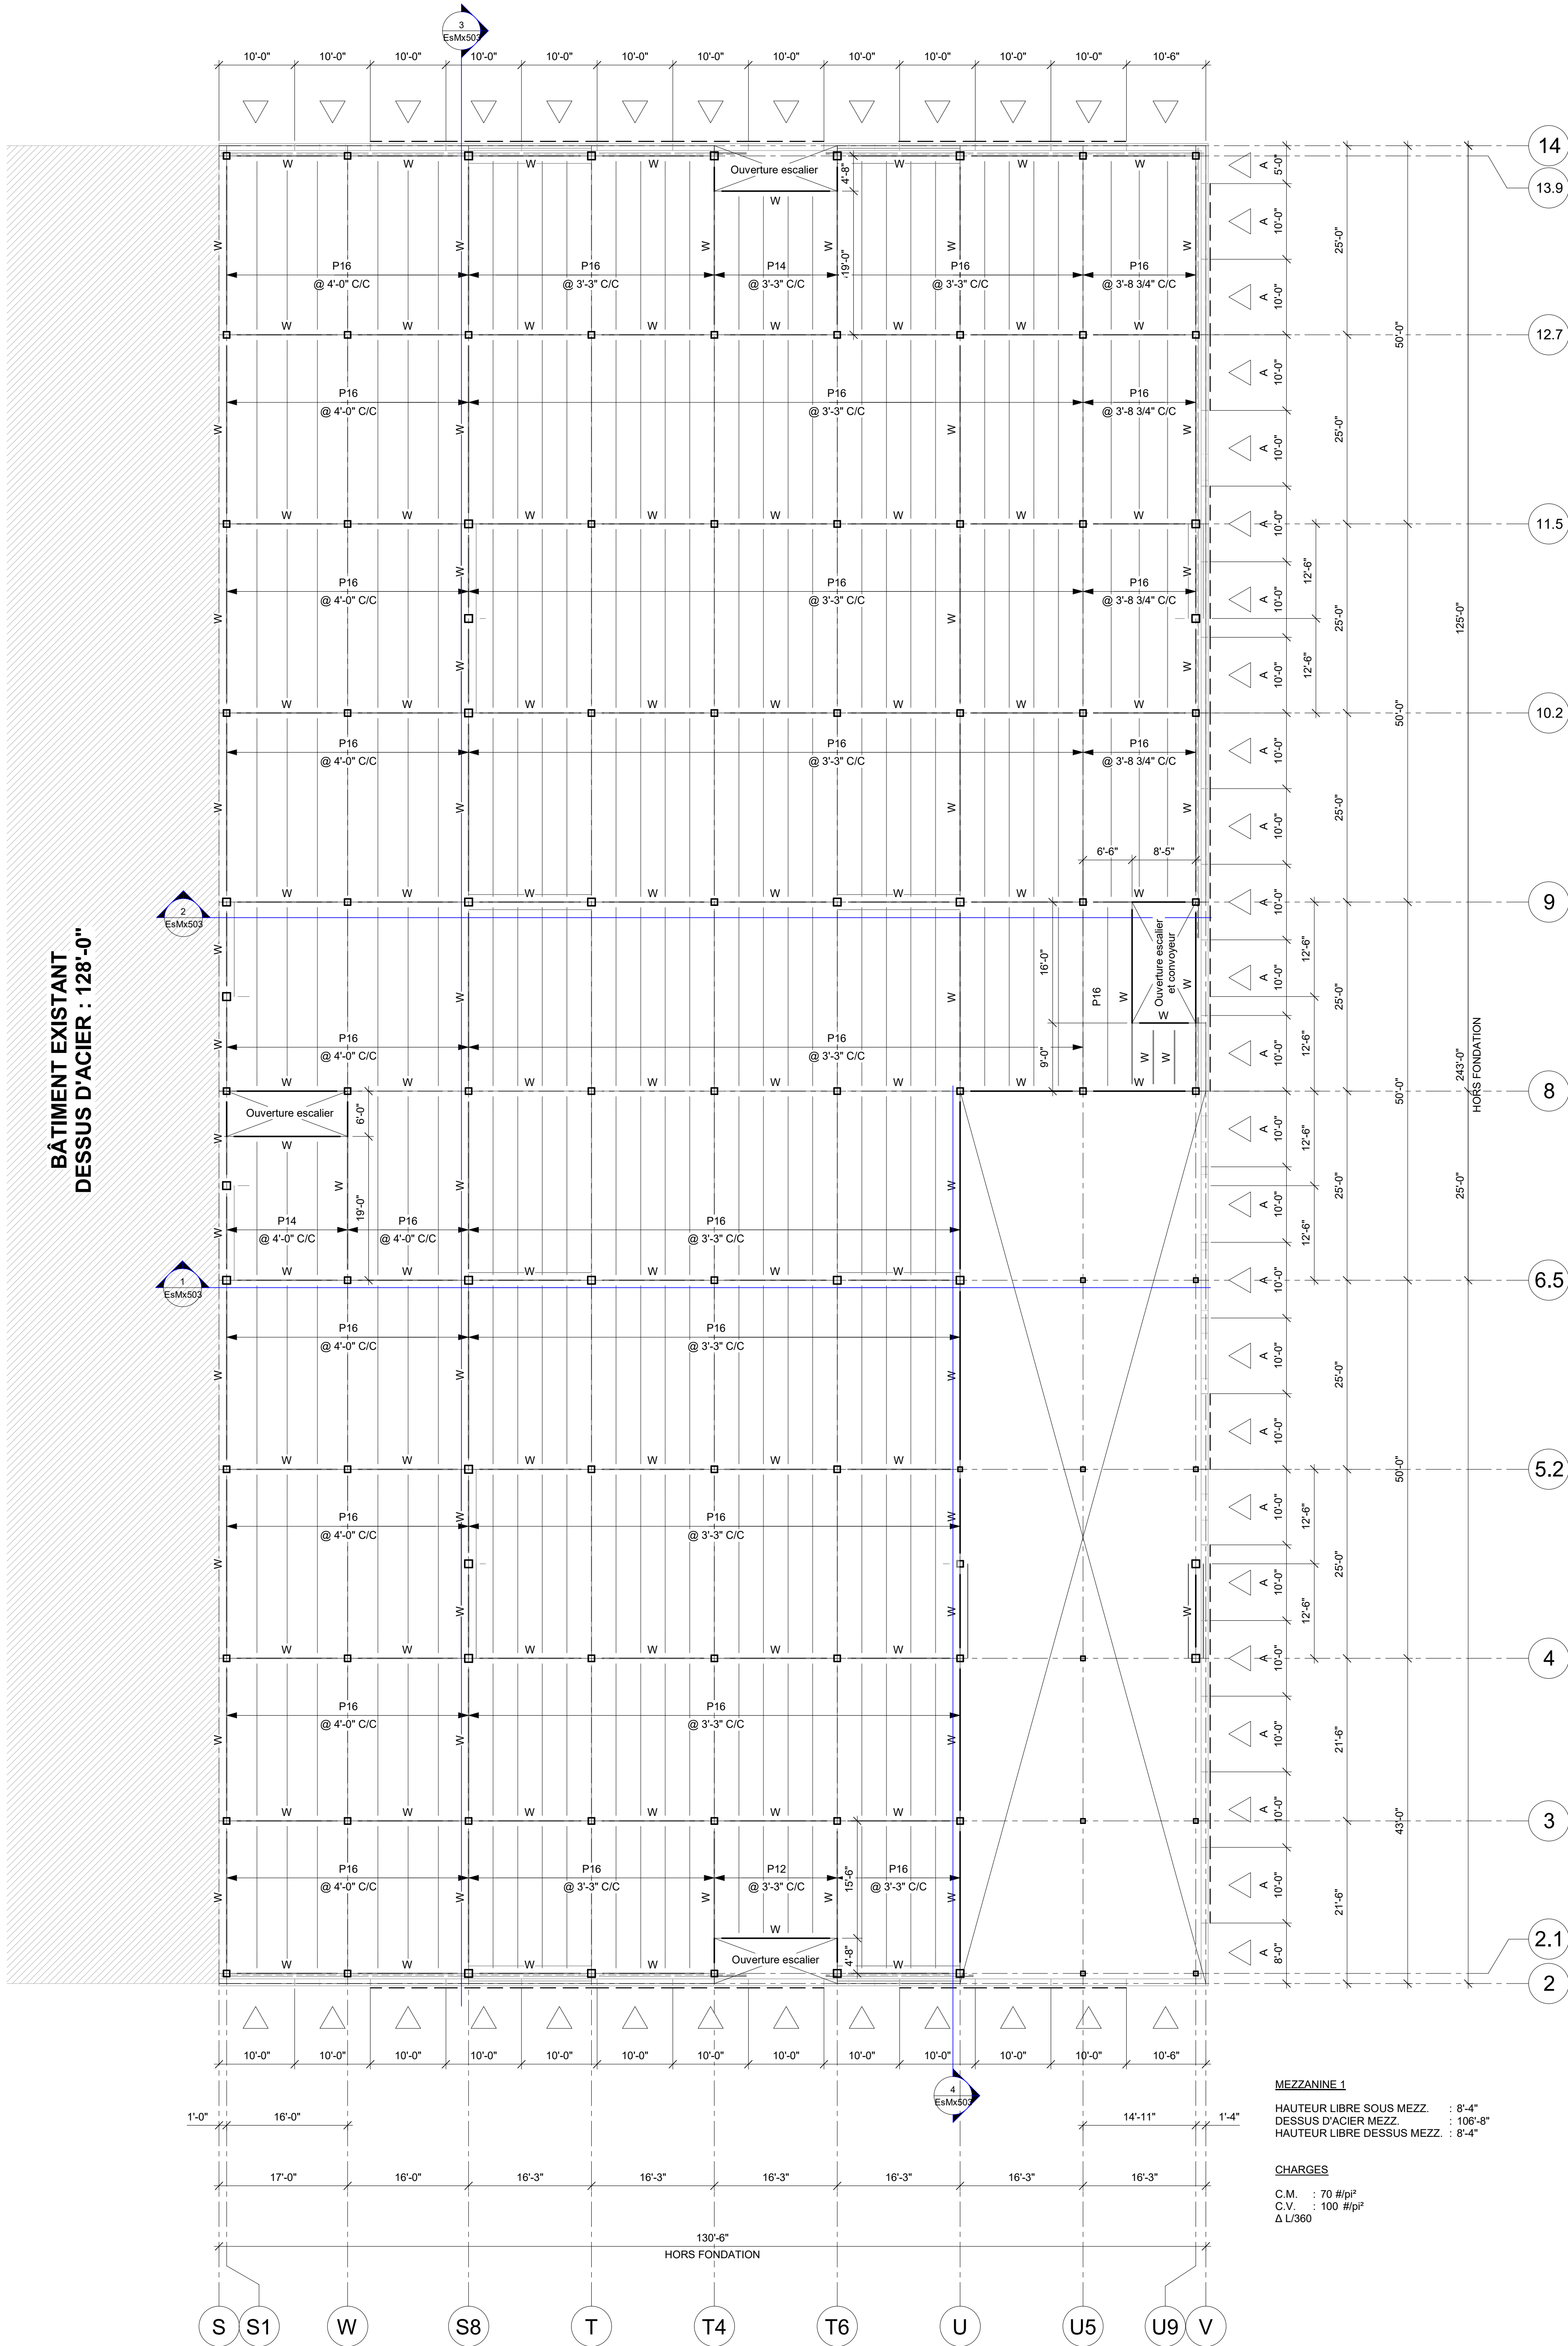

PLAN DE MEZZANINE 1
3/32" = 1'-0"

MEZZANINE 1
HAUTEUR LIBRE SOUS MEZZ. : 8'-4"
DESSUS D'ACIER MEZZ. : 106'-8"
HAUTEUR LIBRE DESSUS MEZZ. : 8'-4"

CHARGES
C.M. : 70 #/pi²
C.V. : 100 #/pi²
Δ L/360

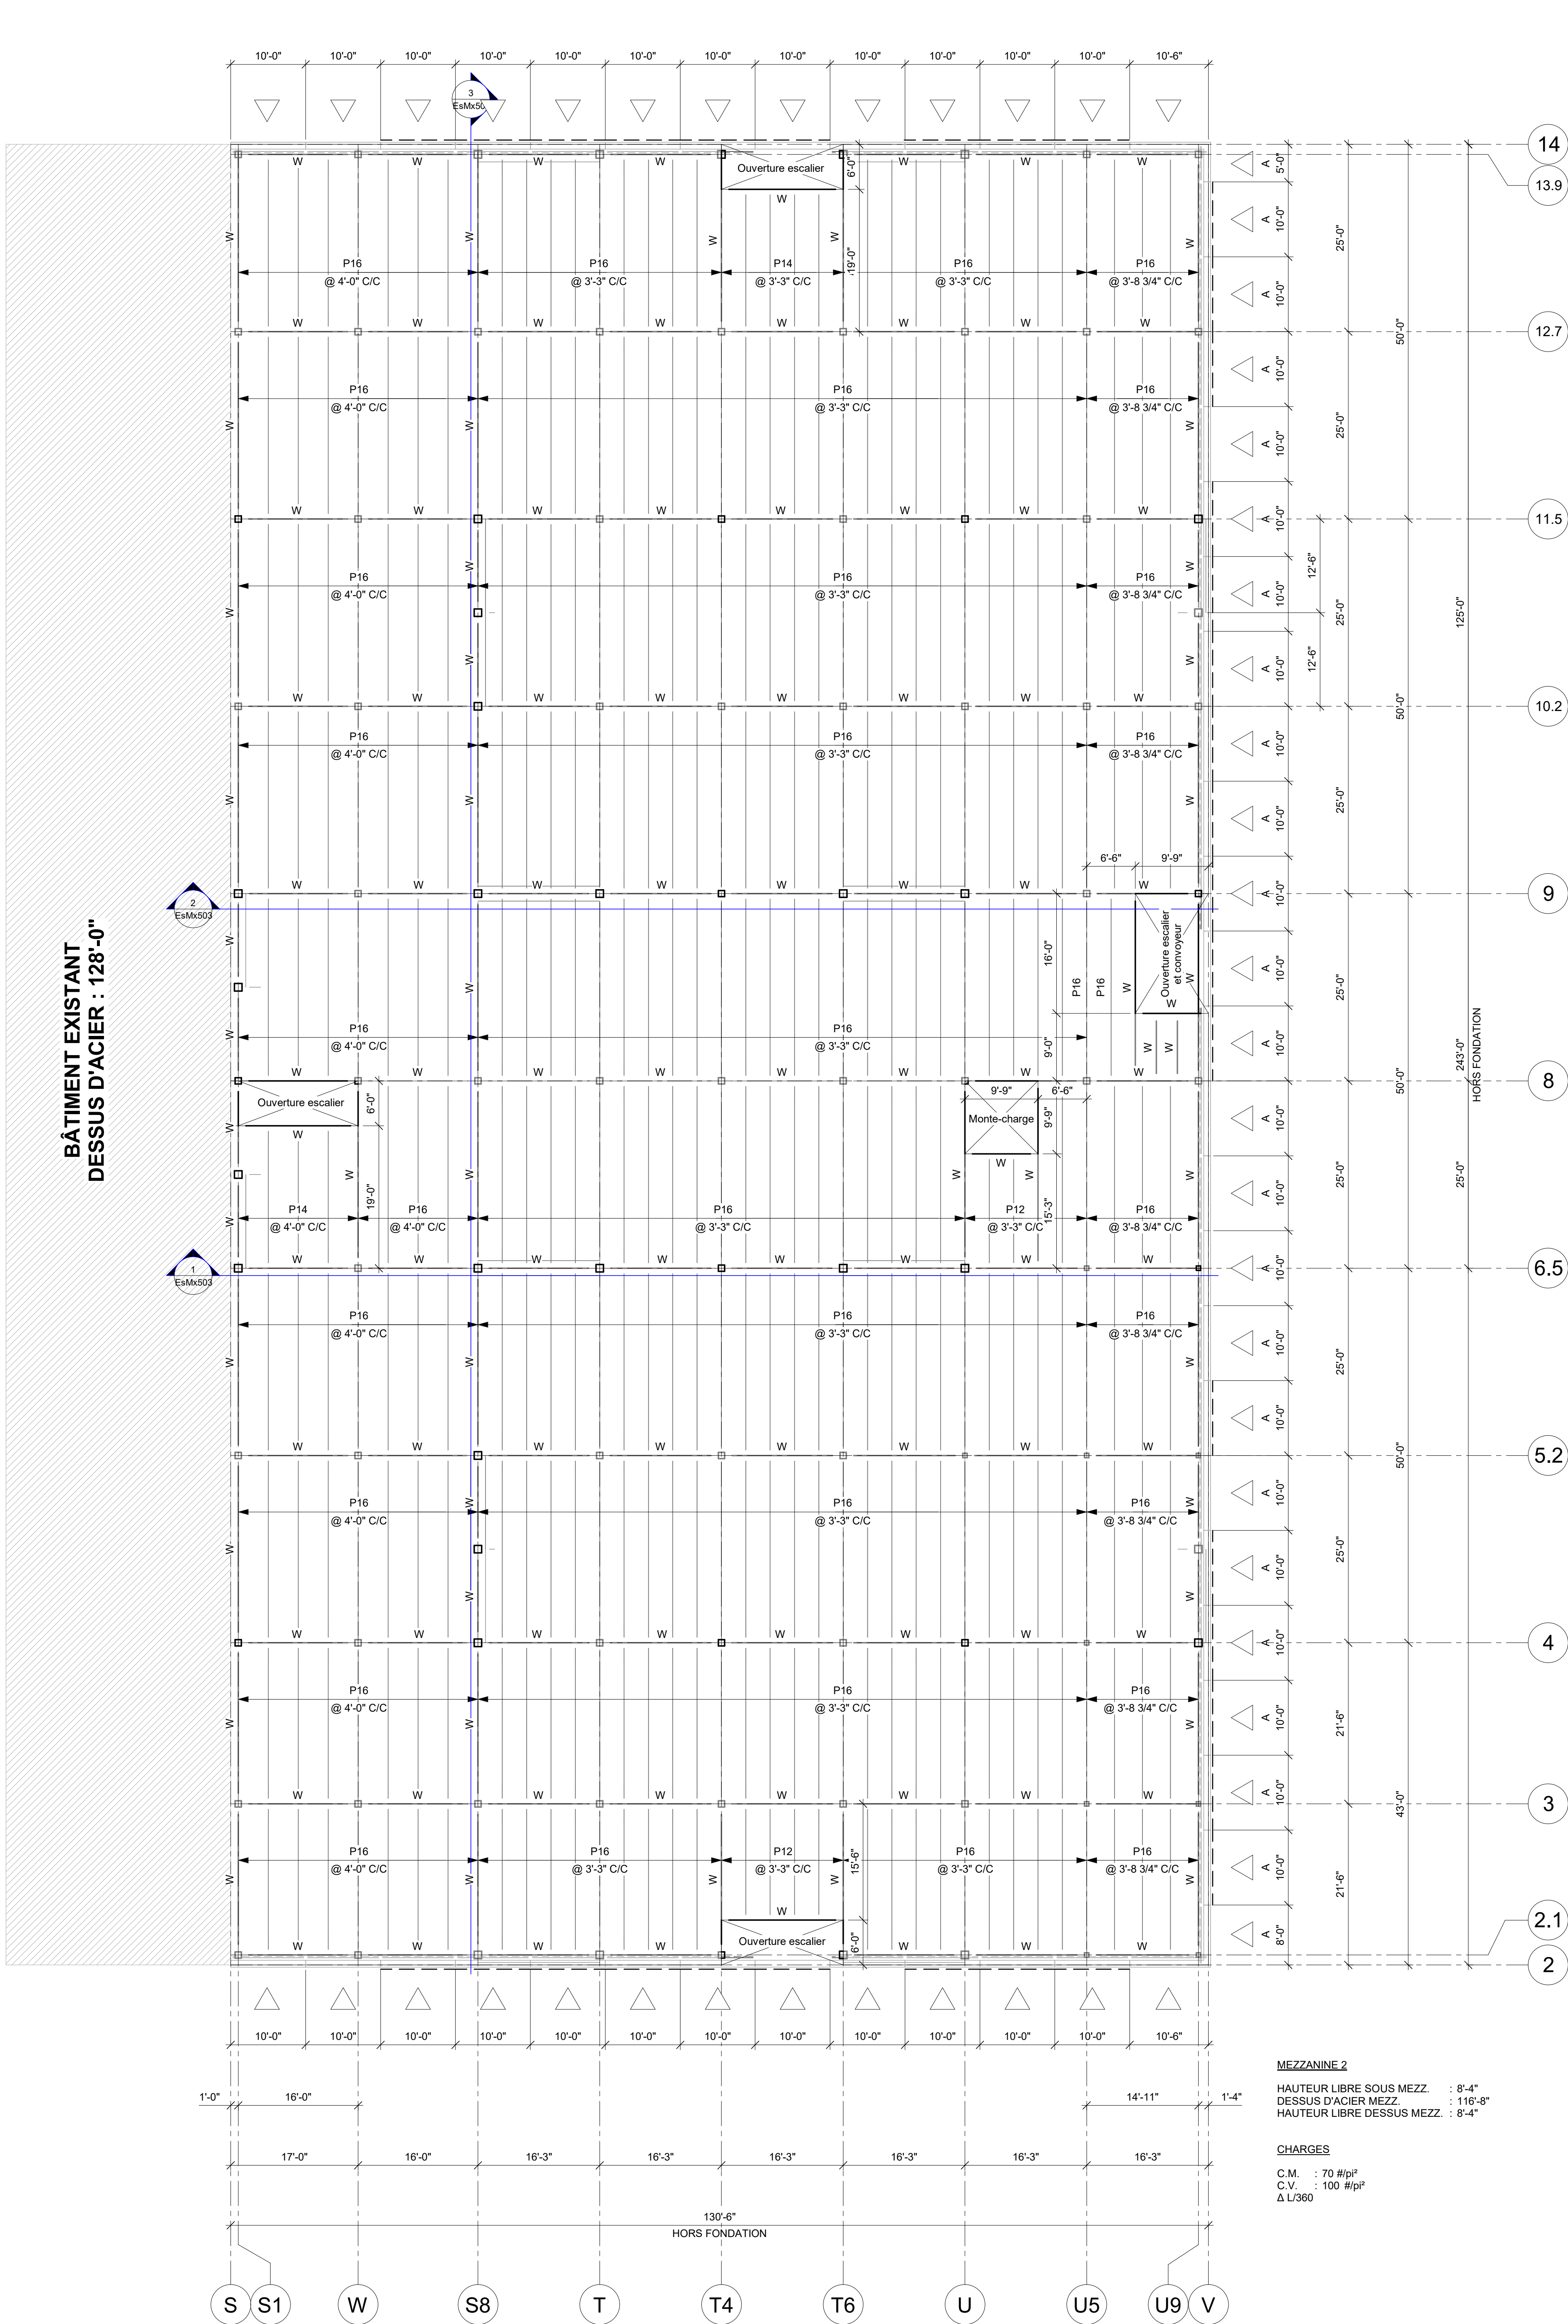

PLAN DE MEZZANINE 2
3/32" = 1'-0"

MEZZANINE 2
HAUTEUR LIBRE SOUS MEZZ. : 8'-4"
DESSUS D'ACIER MEZZ. : 116'-8"
HAUTEUR LIBRE DESSUS MEZZ. : 8'-4"

CHARGES
C.M. : 70 #/pi²
C.V. : 100 #/pi²
Δ L/360

NOTE POUR LE CONTRACTEUR/ÉRECTEUR:
IL EST STRICTEMENT DÉFENDU DE MODIFIER, COPIER, REPRODUIRE OU
DE DISTRIBUER CES DESSINS OU QUELQUES REPRÉSENTATIONS DE
CES DESSINS, PAR TOUTES SOURCES DE MÉDIA INCLUANT
ÉLECTRONIQUEMENT, SANS L'APPROBATION ÉCRITE DE GROUPE
CANAM INC.

PRÉLIMINAIRE

NE DOIT PAS SERVIR À LA
CONSTRUCTION

3	01/06/2025	R2	J.P.	
2	01/06/2025	R2	J.P.	
1	01/11/2025	R1	J.P.	
REVISION	DATE	DESCRIPTION	DESS	VER

DESSIN	CONÇU PAR	INGÉNIEUR DU PROJET	ÉCHELLE:
J.P.			3/32" = 1'-0"
VERIFIÉ PAR	INGÉNIEURS CONSEILS / ARCHITECTES	DATE (préliminaire)	
		03/11/2025	

CLIENT:	Gestion DMJ
TITRE	



SCAUX PROFESSIONNELS	
PROJET	

Entrepôt U-Haul Gatineau
Gatineau, Québec

CROQUIS PRÉLIMINAIRE - PLAN DE
MEZZANINES

NUMÉRO CONTRAT	NUMÉRO DESSIN	DIVISION	REVISION
P2025-177	EsMx201		3