

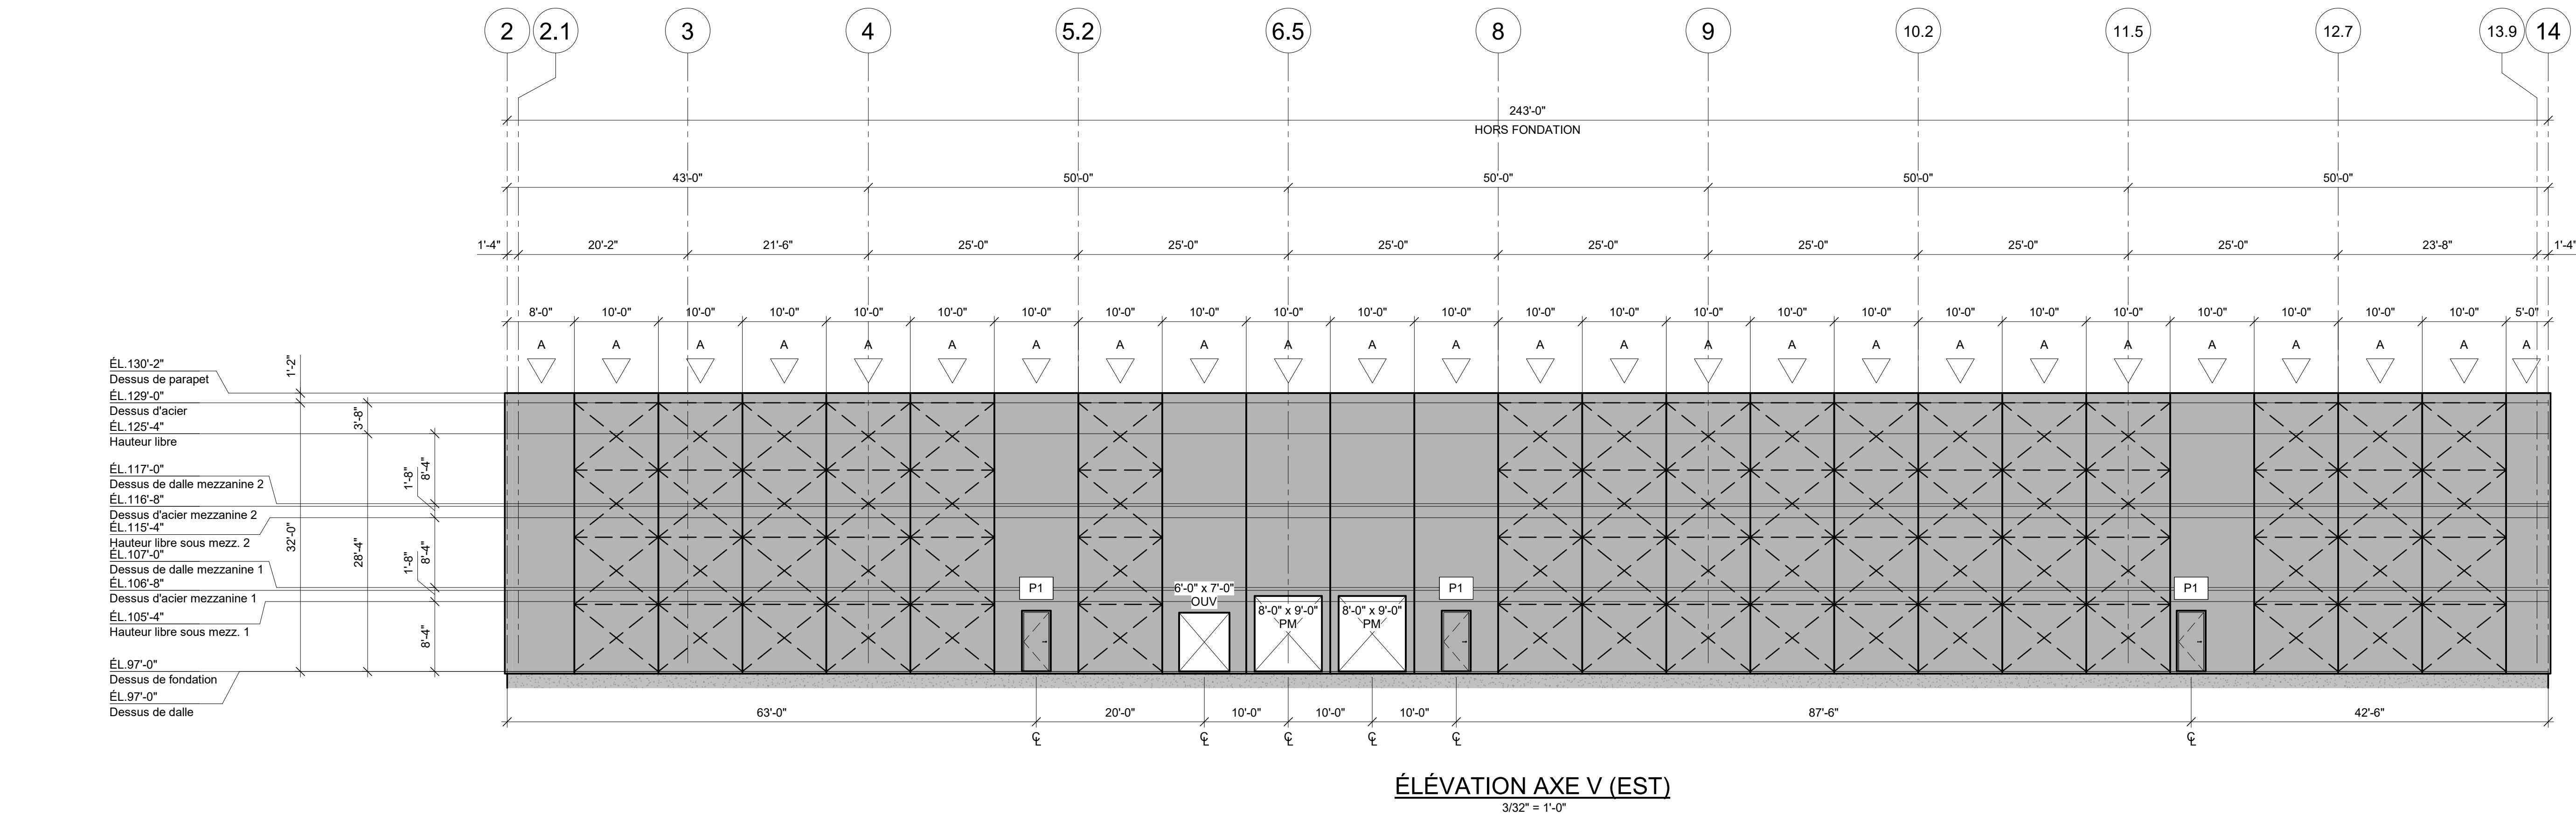
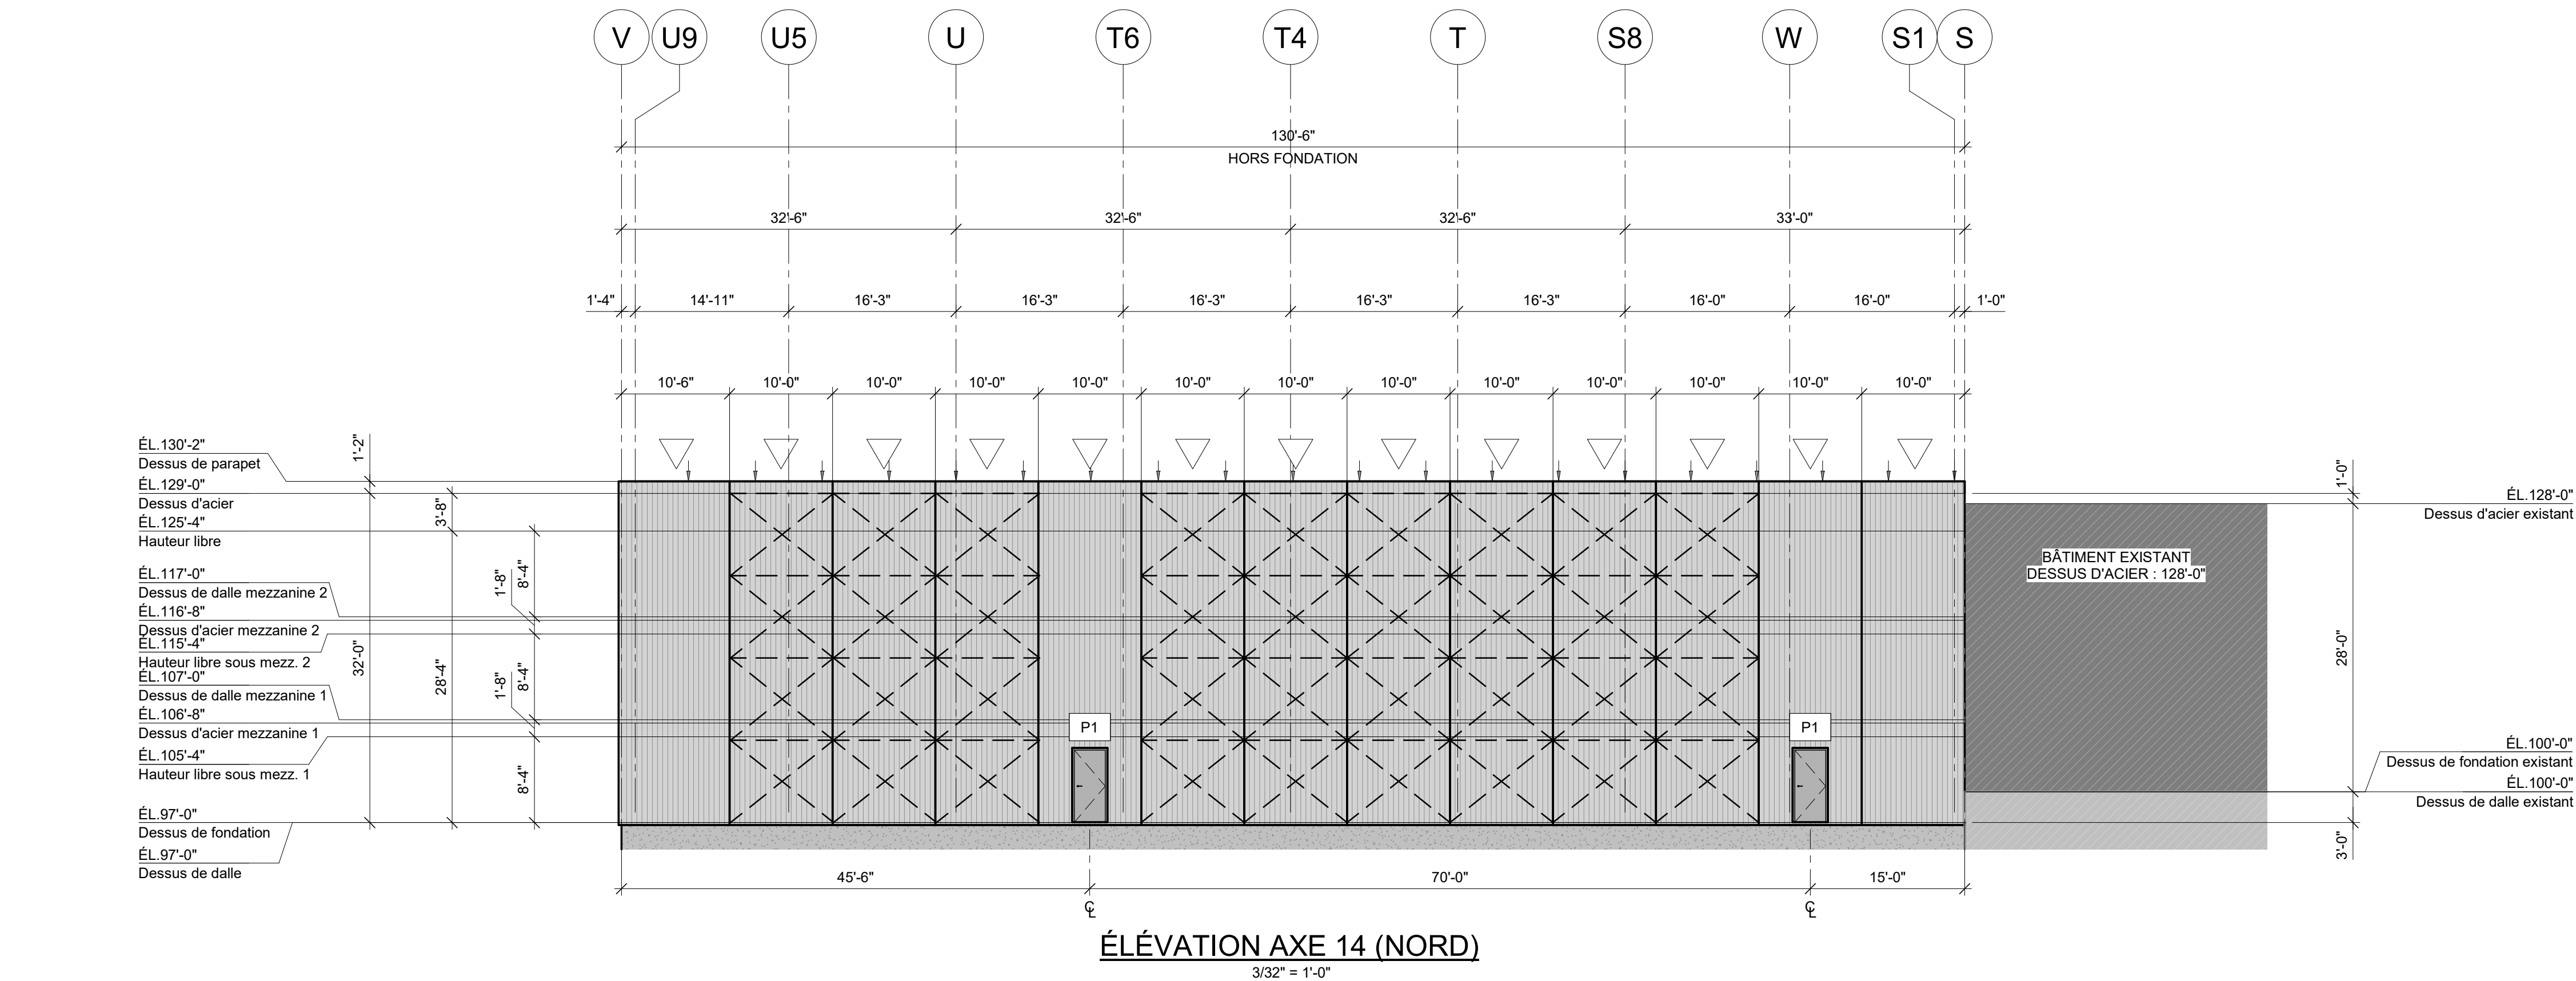
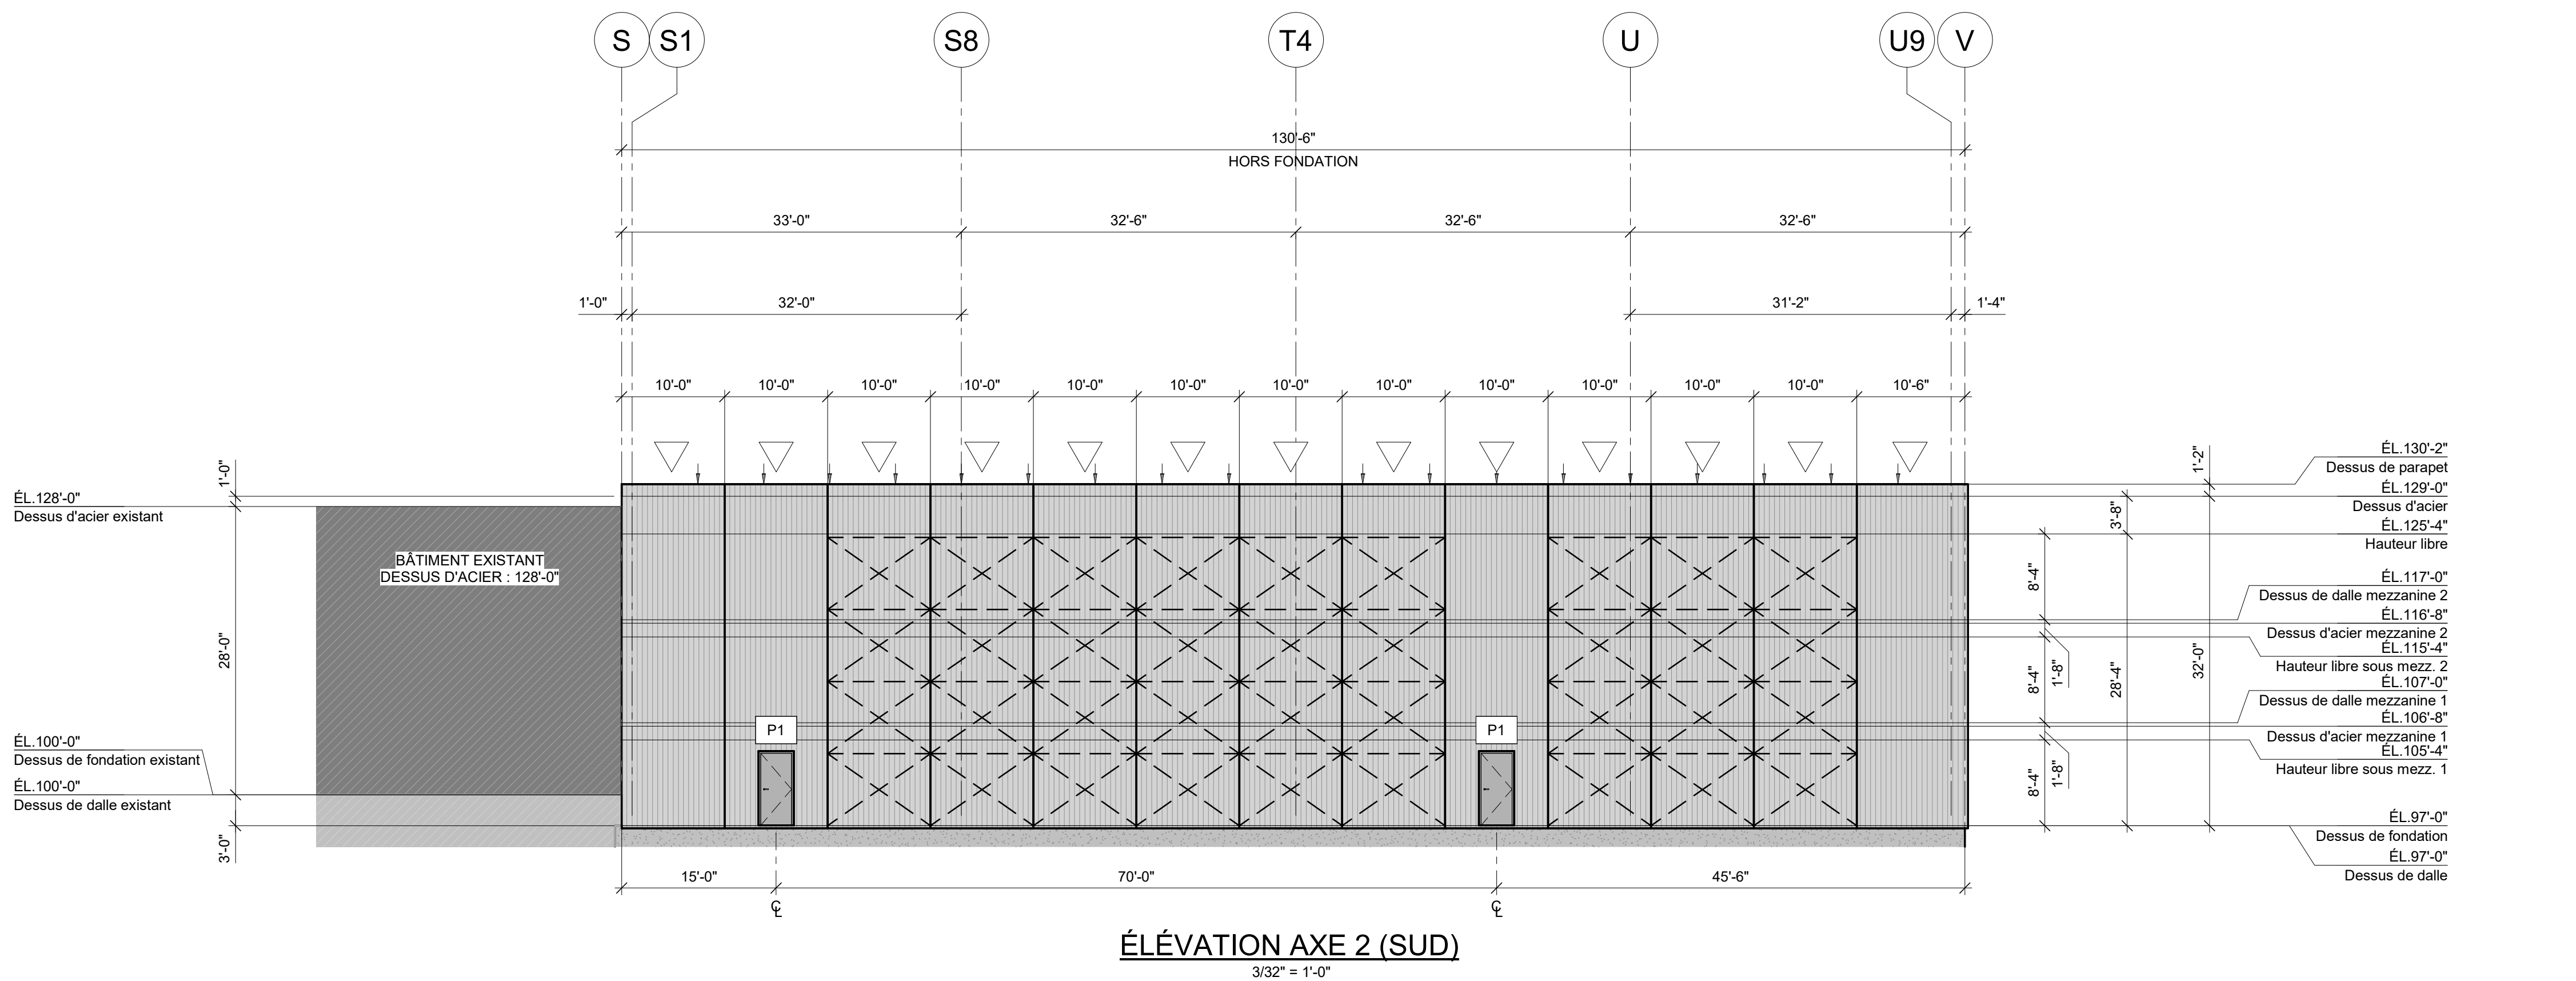


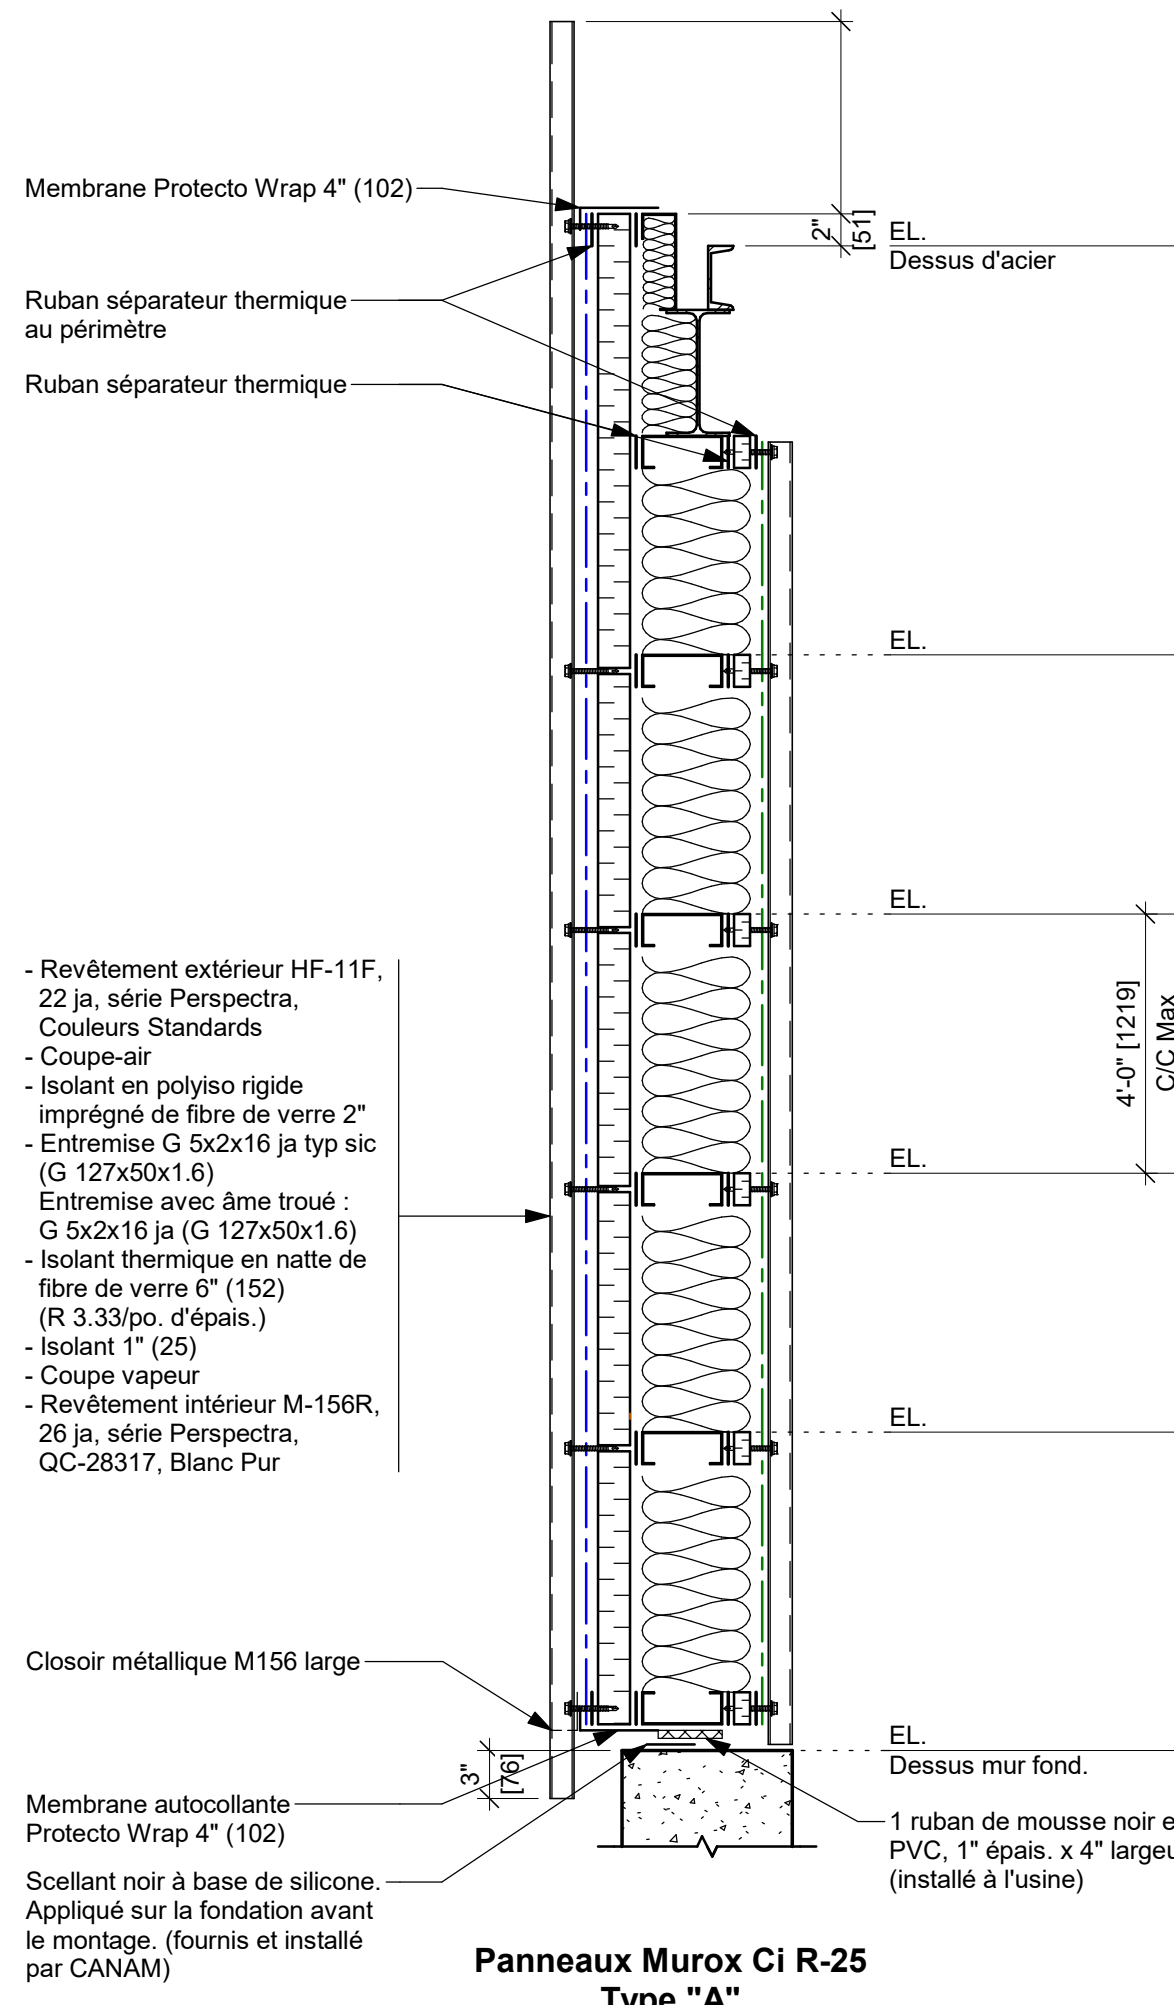

CÉDULE DES PORTES													
Identifiant	Qté	Porte 18 ja.		Isolation (R1)	Dimensions	Sens ouv.	Vitrage		Cadre d'acier 16 ja. avec bris thermique	(3) Pentures 6 tige fixe	Poignée seulement	Barre panique sans poignée ext. ZREO	Barre panique avec poignée ext. ZREO
		Installation					Largeur	Hauteur					
P1	7				3'-0" x 7'-0"								

CÉDULE DES P.M. ET DES OUVERTURES			
Total	Type	Tag	Commentaires
1	6'-0" x 7'-0"	OUV	
2	8'-0" x 9'-0"	PM	
Total général: 3			

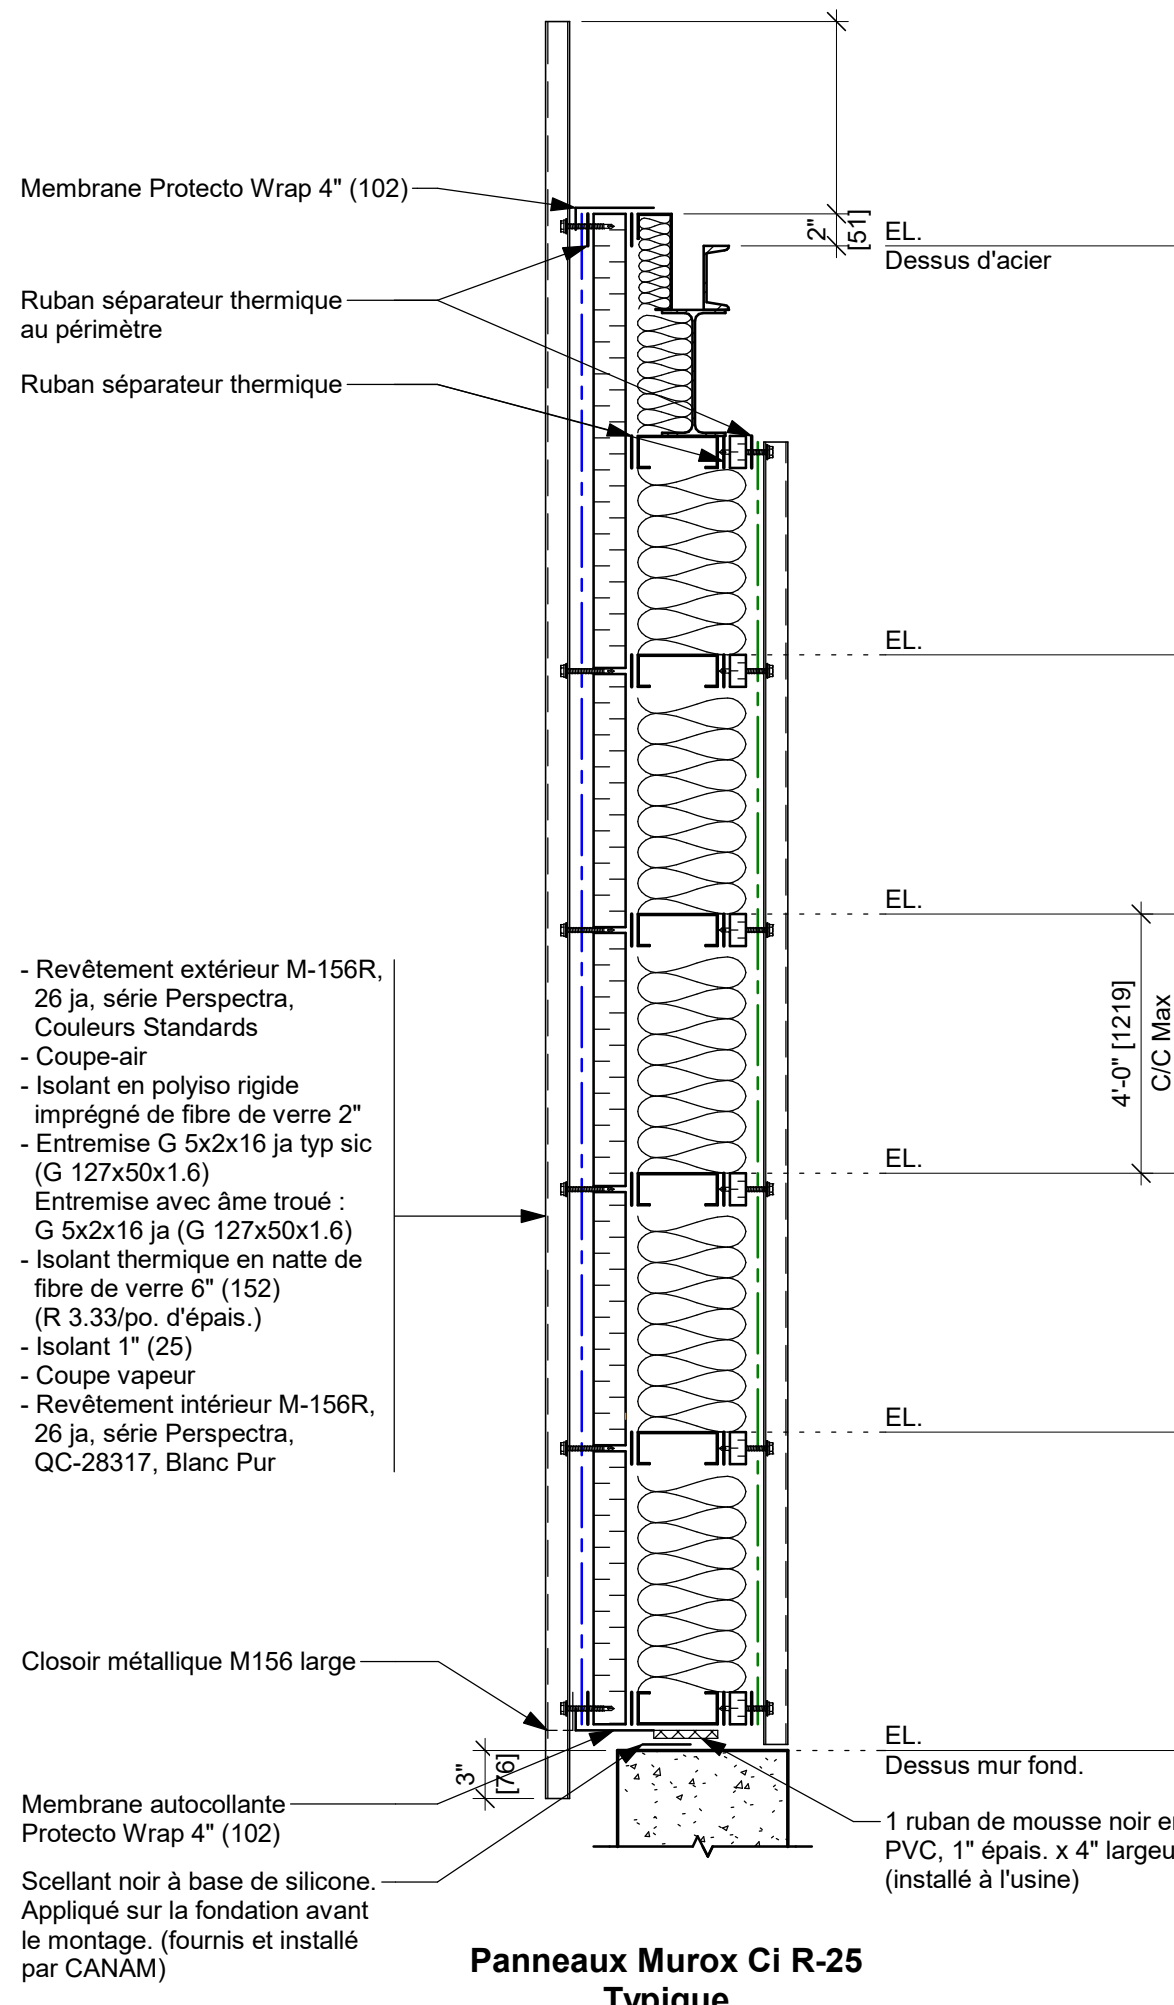

PRÉLIMINAIRE

NE DOIT PAS SERVIR À LA CONSTRUCTION

3	01/06/2025	R2	J.P.	
2	05/02/2025	R2	J.P.	
1	03/11/2025	R1	J.P.	

REVISION	DATE	DESCRIPTION	DESS	VER

DESSIN			
DESSINÉ PAR	CONÇU PAR	INGÉNIEUR OU PROJET	ECHELLE
J.P.			Comme indiqué
VERIFIÉ PAR	INGÉNIEURS CONSEILS / ARCHITECTES	DATE (mm/aaaa)	
		03/11/2025	

CLIENT:	Gestion DMJ
---------	-------------



SCAUX PROFESSIONNEL

PROJET

Entrepôt U-Haul Gatiéau
Gatiéau, Québec

TITRE

CROQUIS PRÉLIMINAIRE -
ÉLEVATIONS, COUPES DE MUR ET
CÉDULES

NUMERO CONTRAT	NUMERO DESSIN	DIVISION	REVISION
P2025-177	EsMx501		3