
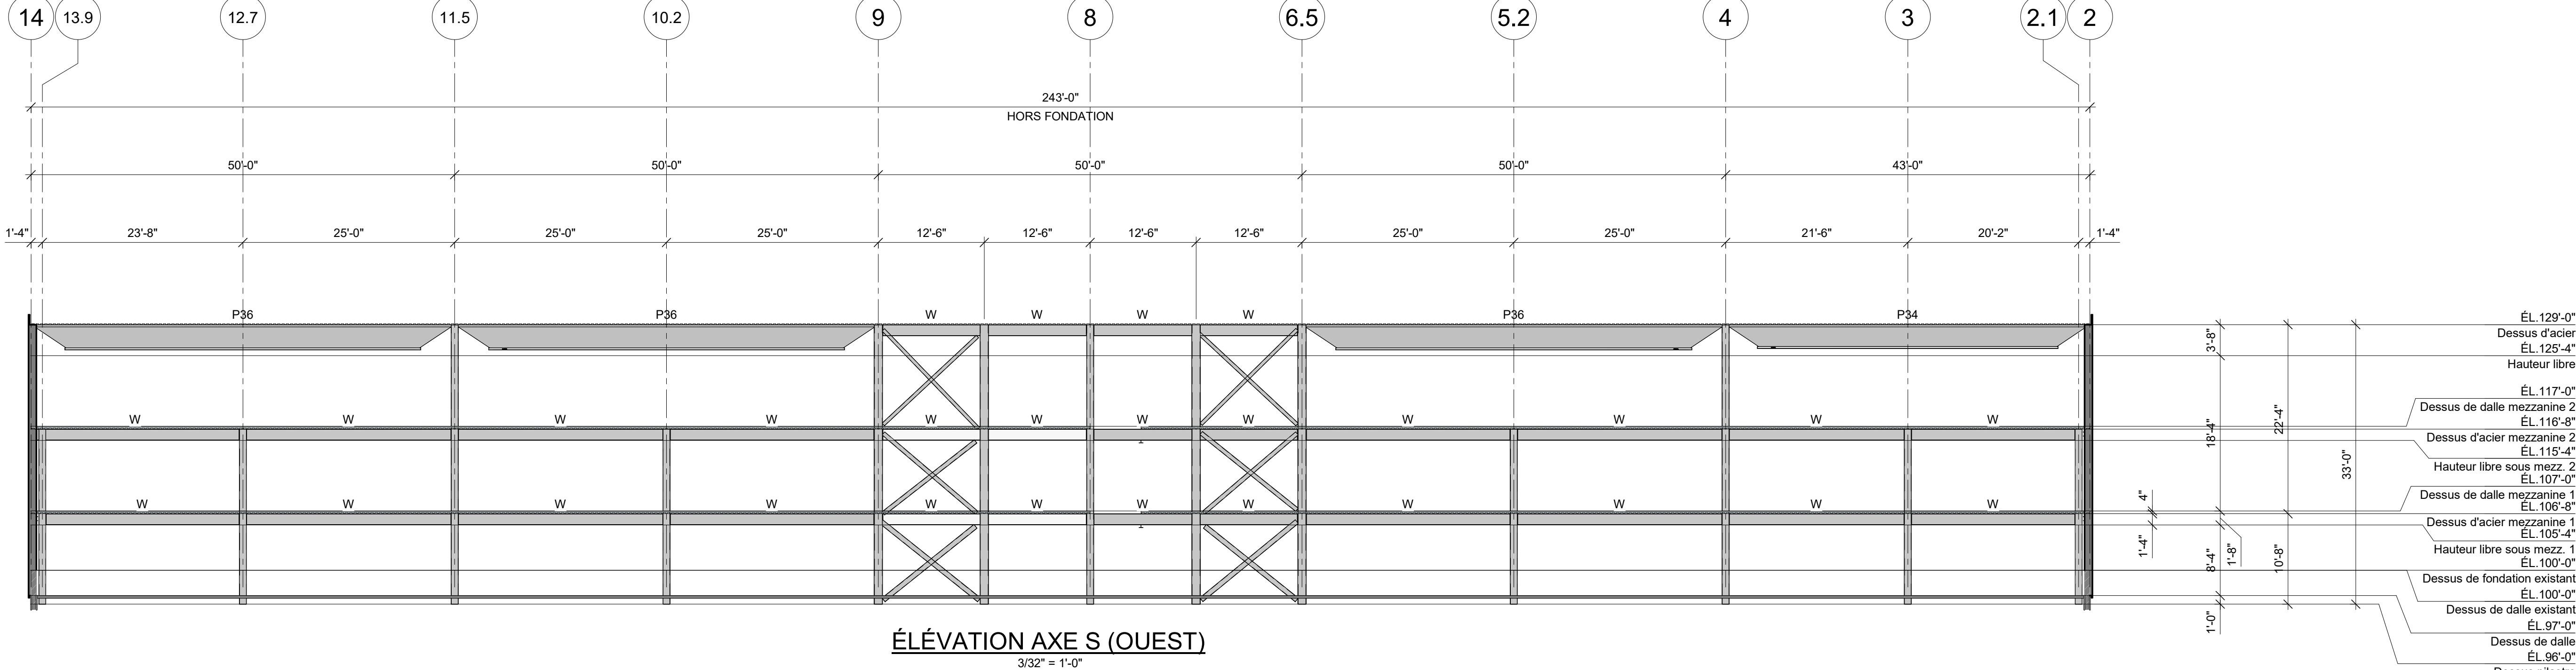
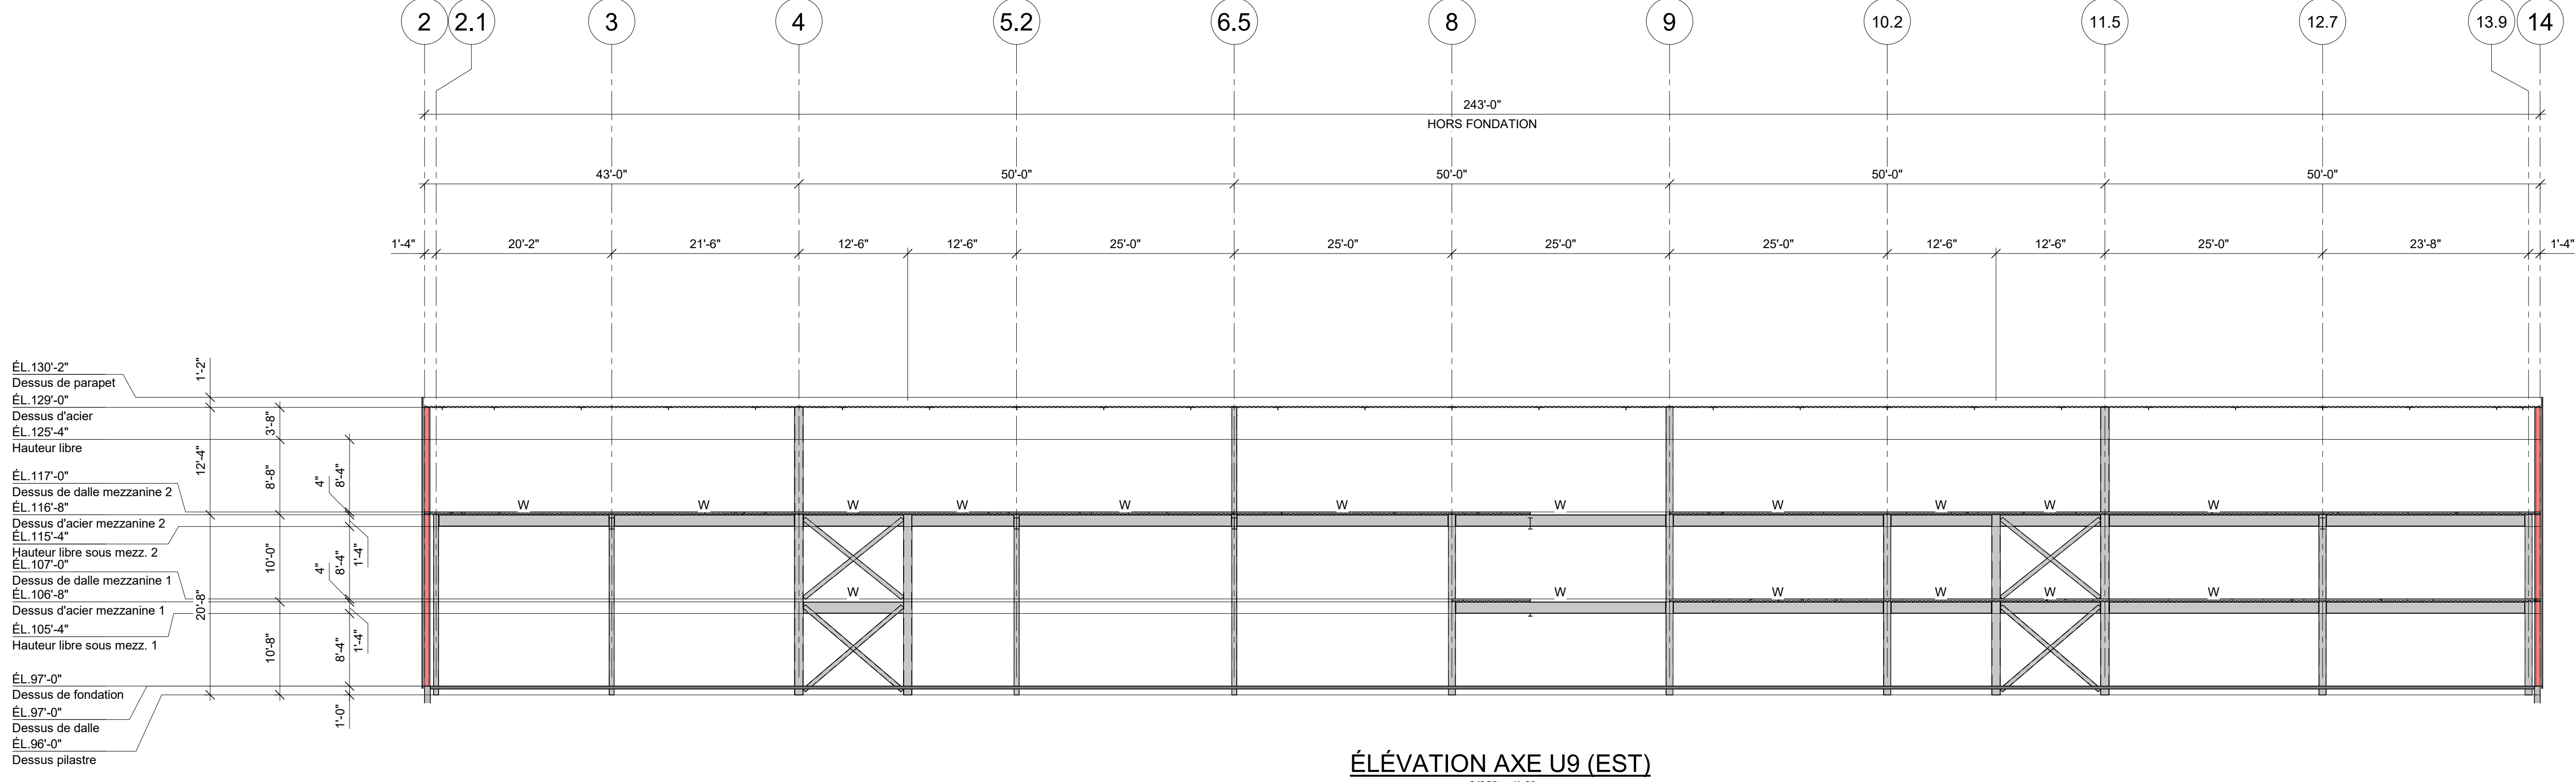
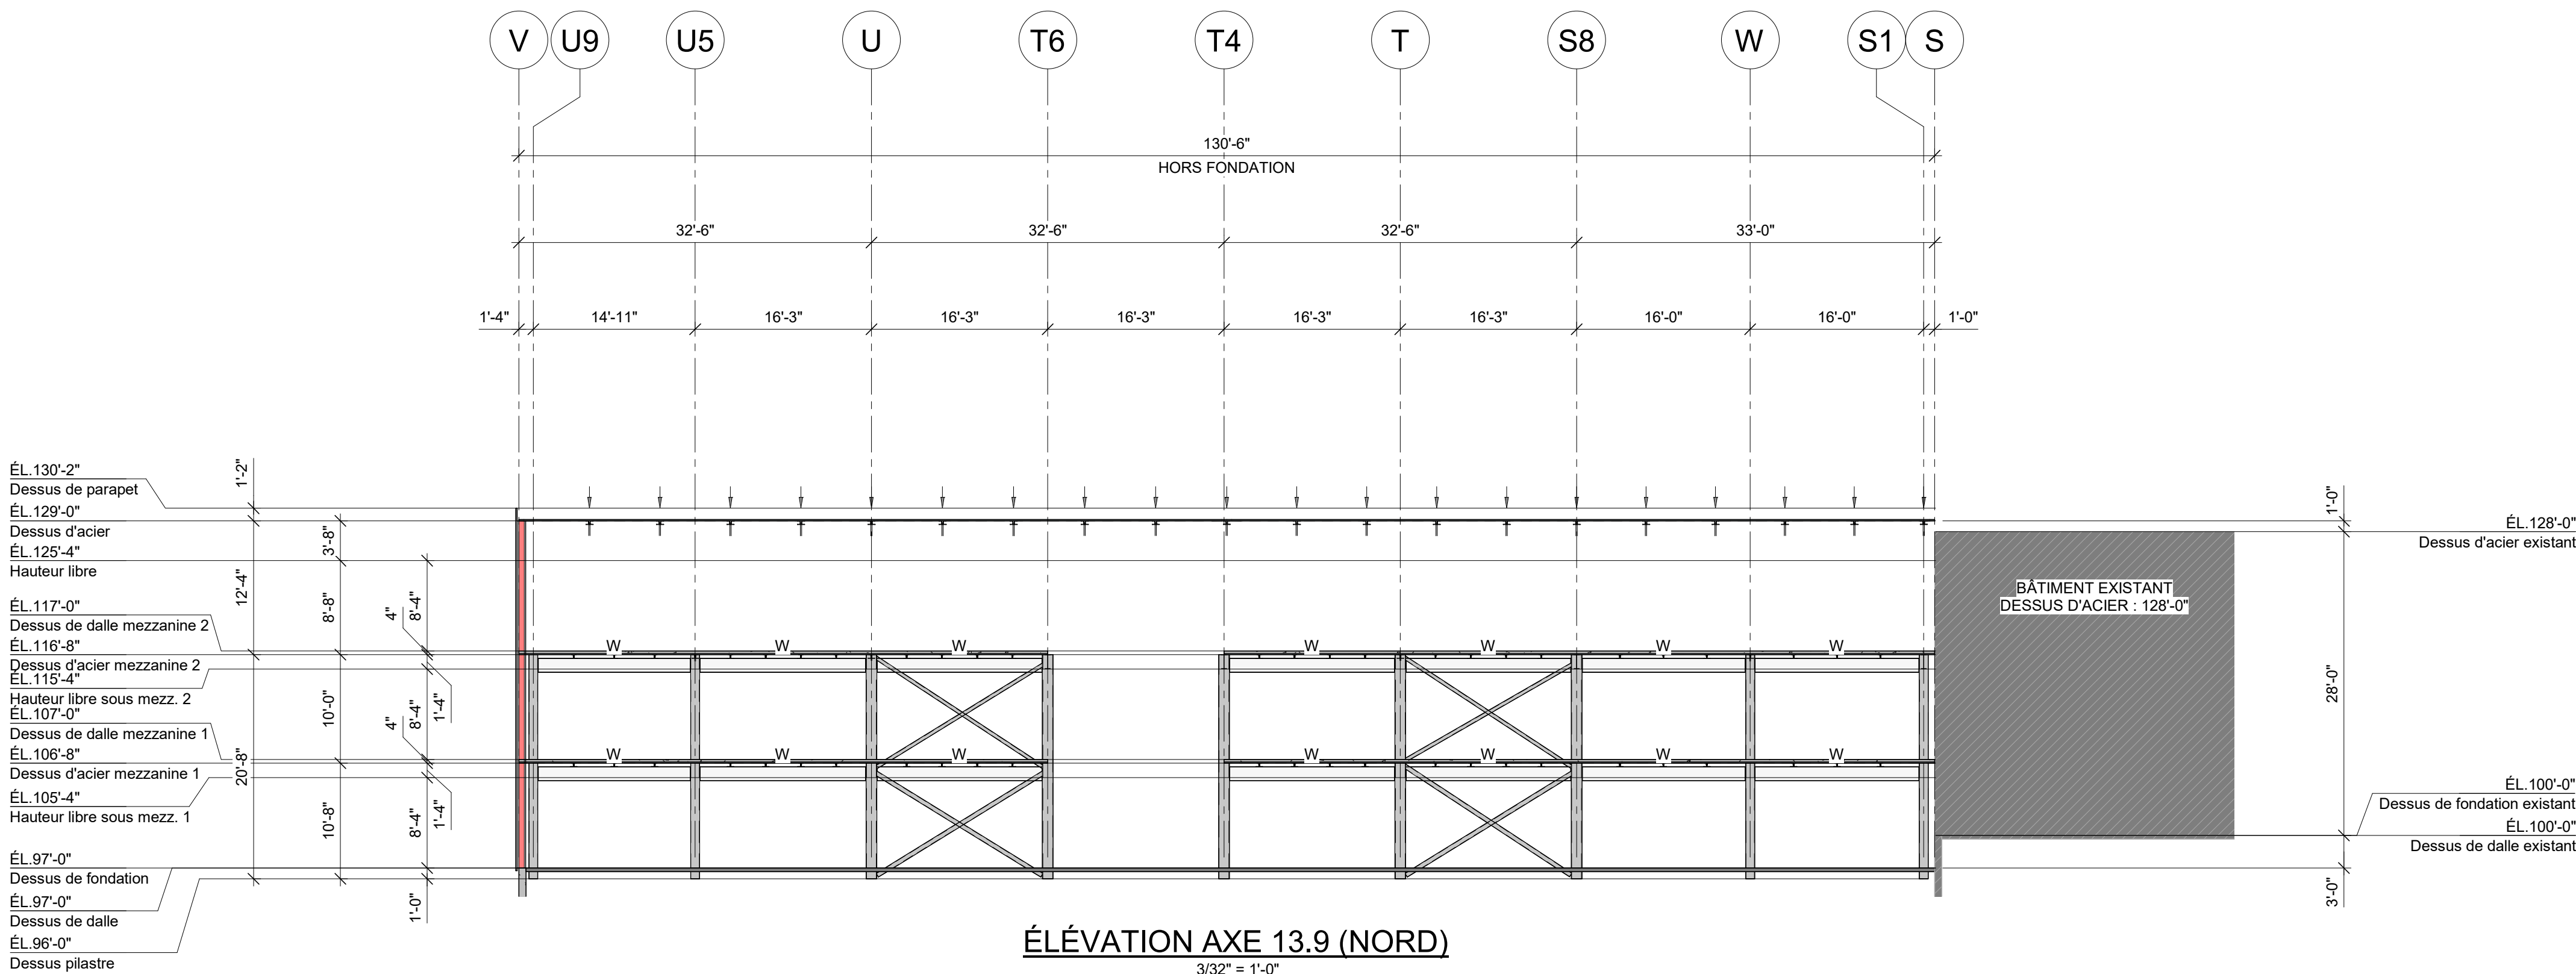


10/11/2025

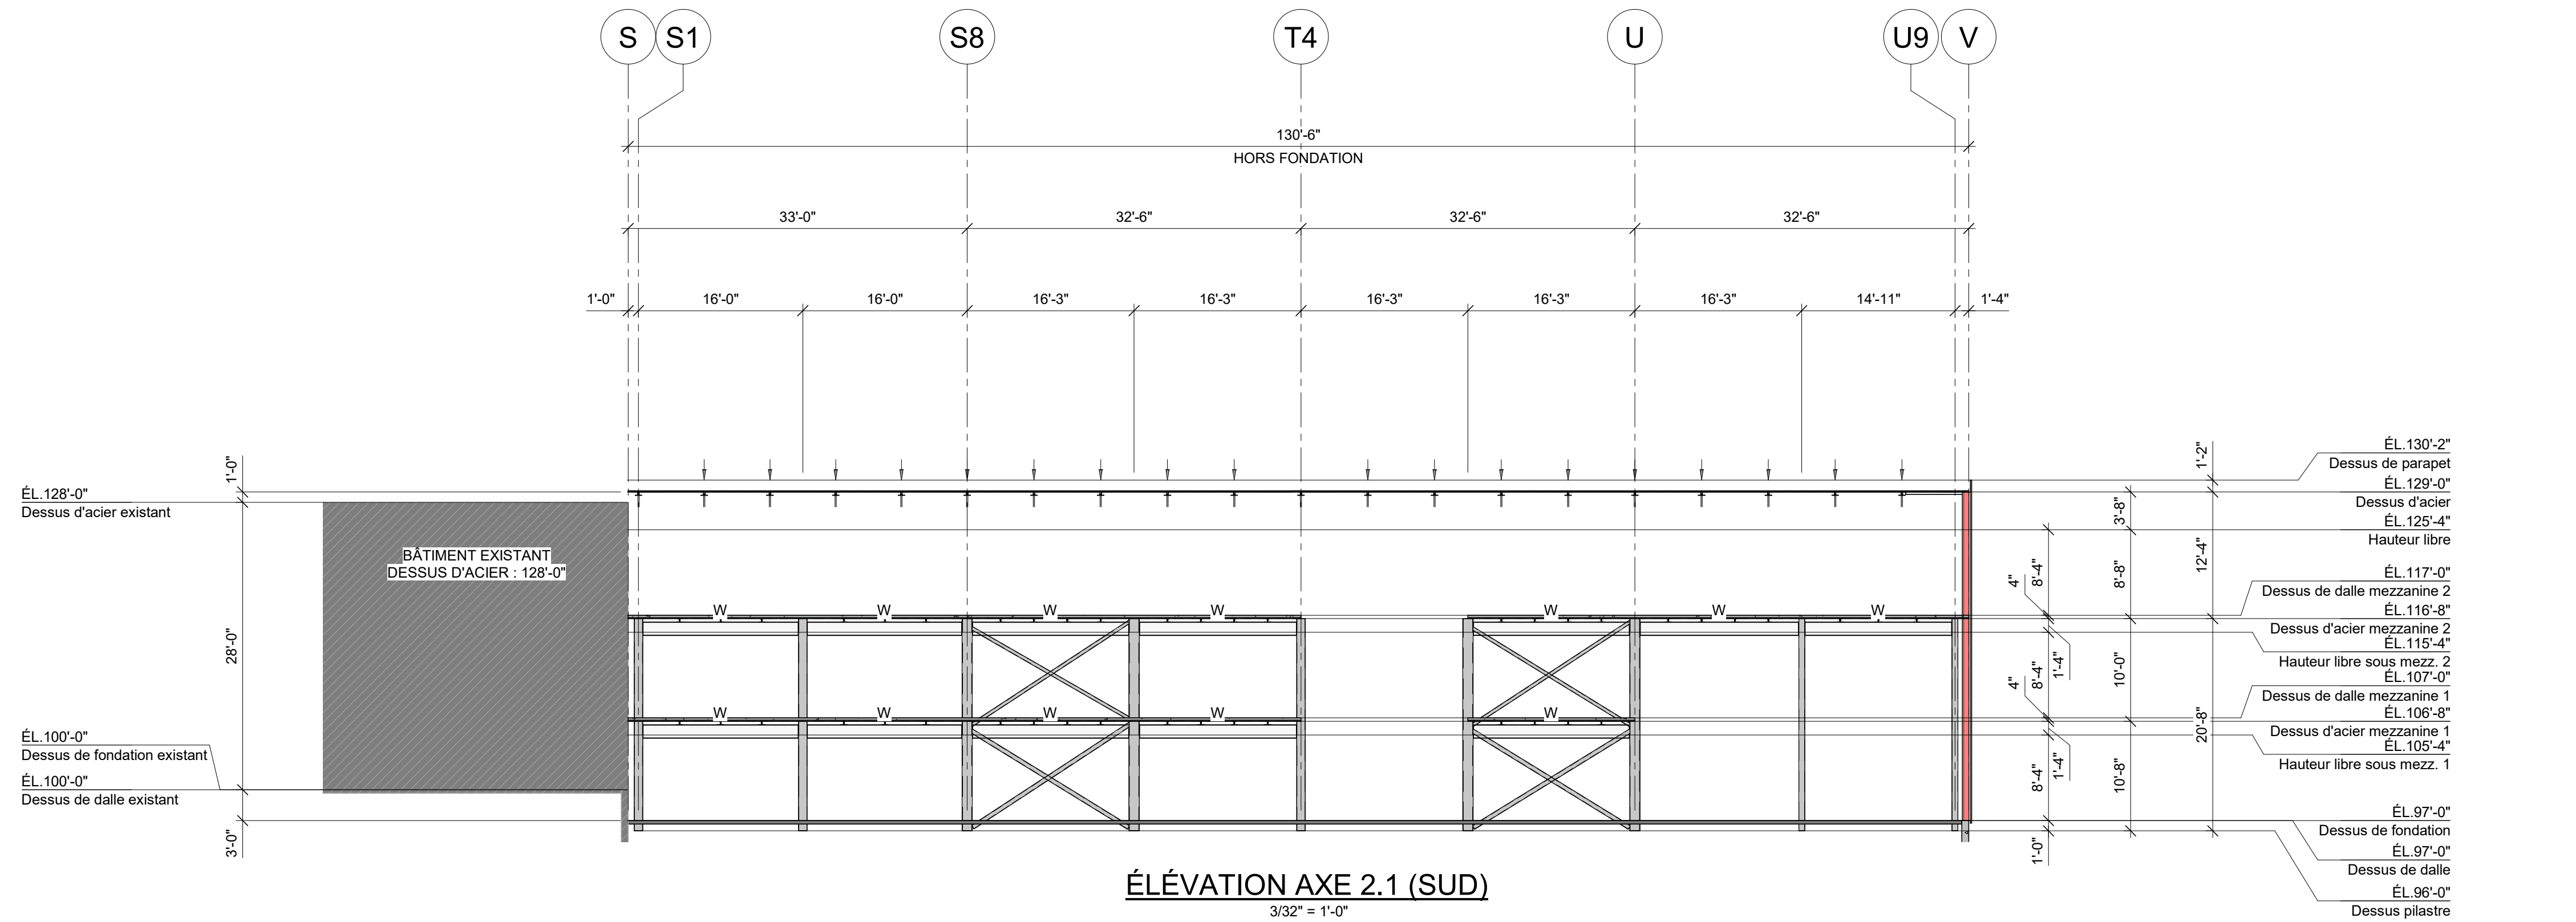

NOTE POUR LE CONTRACTEUR/ÉRECTEUR:
IL EST STRICTEMENT DÉFENDU DE MODIFIER, COPIER, REPRODUIRE OU DE DISTRIBUER CES DESSINS OU QUELQUES REPRÉSENTATIONS DE CES DESSINS PAR TOUTES SOURCES DE MÉDIA INCLUANT ÉLECTRONIQUEMENT, SANS L'APPROBATION ÉCRITE DE GROUPE CANAM INC.

PRÉLIMINAIRE
NE DOIT PAS SERVIR À LA
CONSTRUCTION

3	01/06/2025	R2	J.P.	
2	05/02/2025	R2	J.P.	
1	10/11/2025	R1	J.P.	
REVISION	DATE	DESCRIPTION	DESS	VER
DESSIN DE PROJET				

DESSIN	CONÇU PAR	INGÉNIEUR/OU PROJET	ÉCHELLE:
DESSINÉ PAR	J.P.		3/32" = 1'-0"
VÉRIFIÉ PAR	INGÉNIEURS CONSEILS / ARCHITECTES	DATE (mm/aa/aaaa)	03/11/2025

CLIENT: Gestion DMJ



11505, 1re Avenue, bureau 500, Saint-Georges Beaulac
Québec, Canada G5V 7X5
Téléphone : (418) 228-8031
Sans frais : (877) 459-8049
www.canam.com

PROJET

Entrepôt U-Haul Gatineau
Gatineau, Québec

TITRE
CROQUIS PRÉLIMINAIRE -
ÉLEVATIONS

NUMÉRO CONTRAT	NUMÉRO DESSIN	DIVISION	REVISION
P2025-177	EsMx502		3