


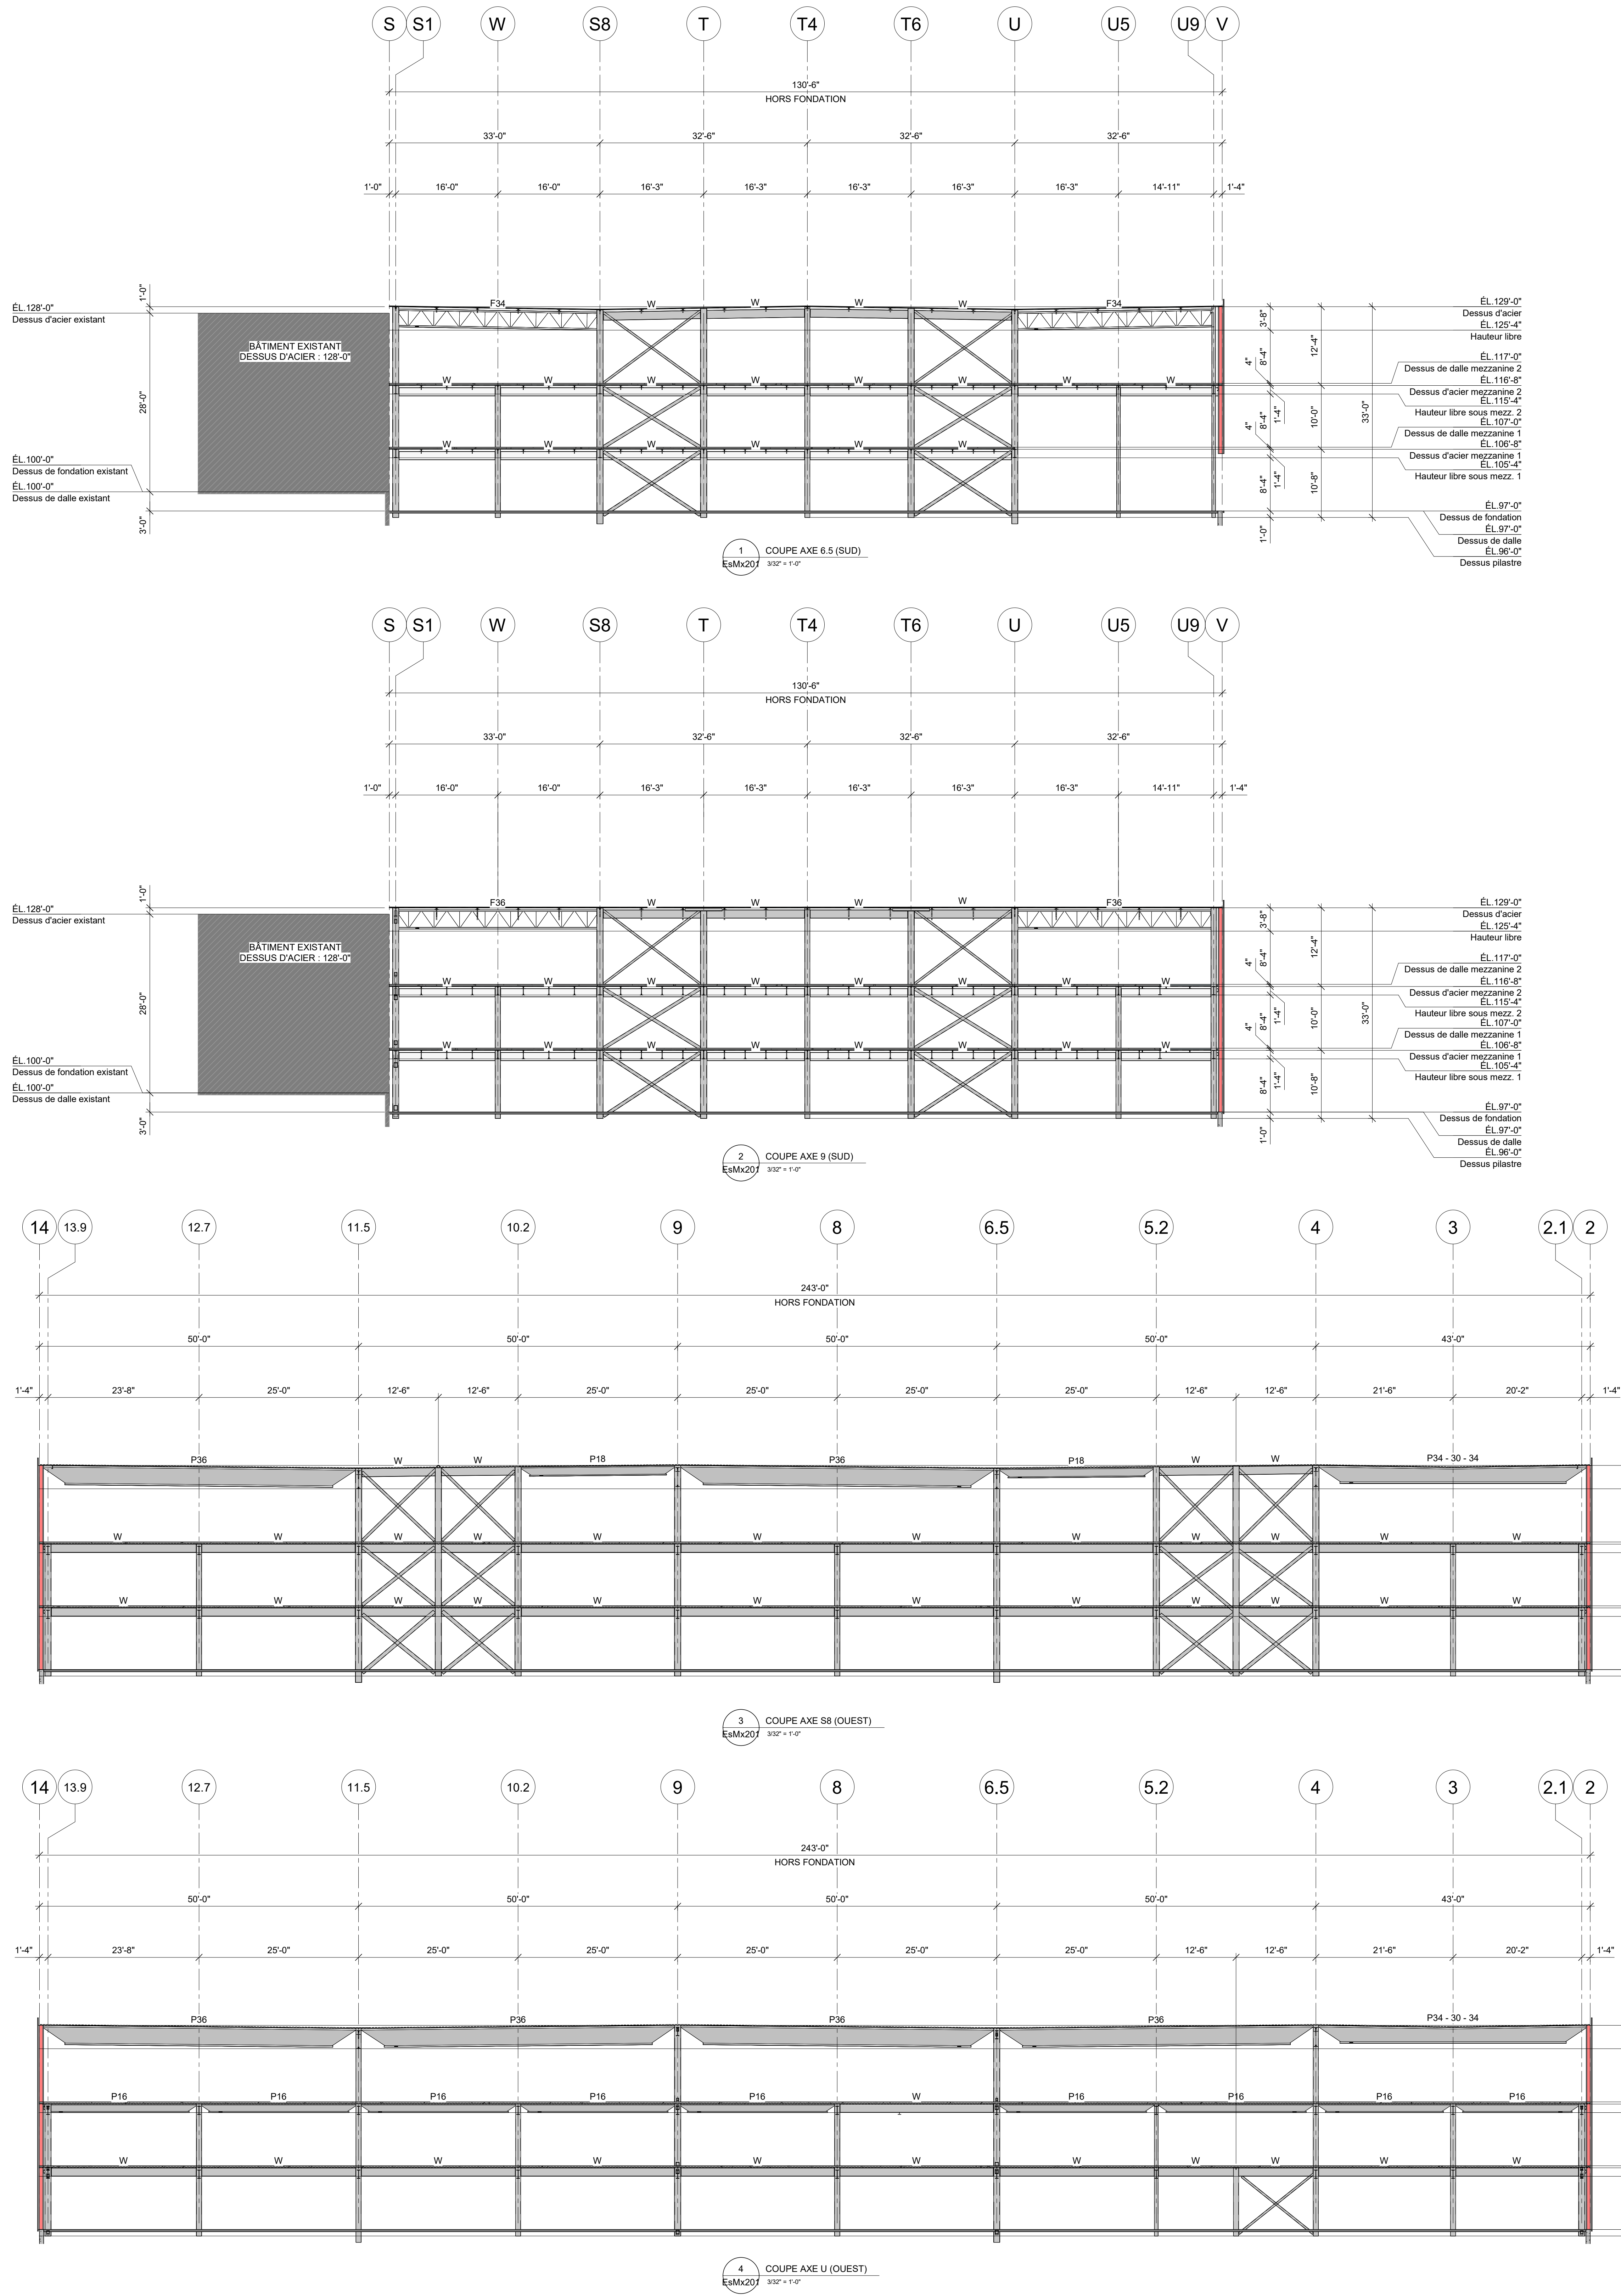

NOTE POUR LE CONTRACTEUR/ÉRECTEUR:
IL EST STRICTEMENT DÉFENDU DE MODIFIER, COPIER, REPRODUIRE OU DE DISTRIBUER CES DESSINS OU QUELQUES REPRÉSENTATIONS DE CES DESSINS, PAR TOUTES SOURCES DE MÉDIA INCLUANT ÉLECTRONIQUEMENT, SANS L'APPROBATION ÉCRITE DE GROUPE CANAM INC.

PRÉLIMINAIRE

NE DOIT PAS SERVIR À LA CONSTRUCTION

3	01/06/2025	R2	J.P.	
2	05/02/2025	R2	J.P.	
1	03/11/2025	R1	J.P.	

REVISION	DATE	DESCRIPTION	DESSIN	VER

DESSIN	CONÇU PAR	INGÉNIEUR OU PROJET	ÉCHELLE:
J.P.			3/32" = 1'-0"
VERIFIÉ PAR	INGÉNIEURS CONSEILS / ARCHITECTES	DATE (mm/aaaa)	
		03/11/2025	

CLIENT: Gestion DMJ



SCAUX PROFESSIONNEL

PROJET: Entrepôt U-Haul Gatineau
Gatineau, Québec

TITRE: CROQUIS PRÉLIMINAIRE - COUPES

NUMÉRO CONTRAT	NUMÉRO DESSIN	DIVISION	REVISION
P2025-177	EsMx503		3