
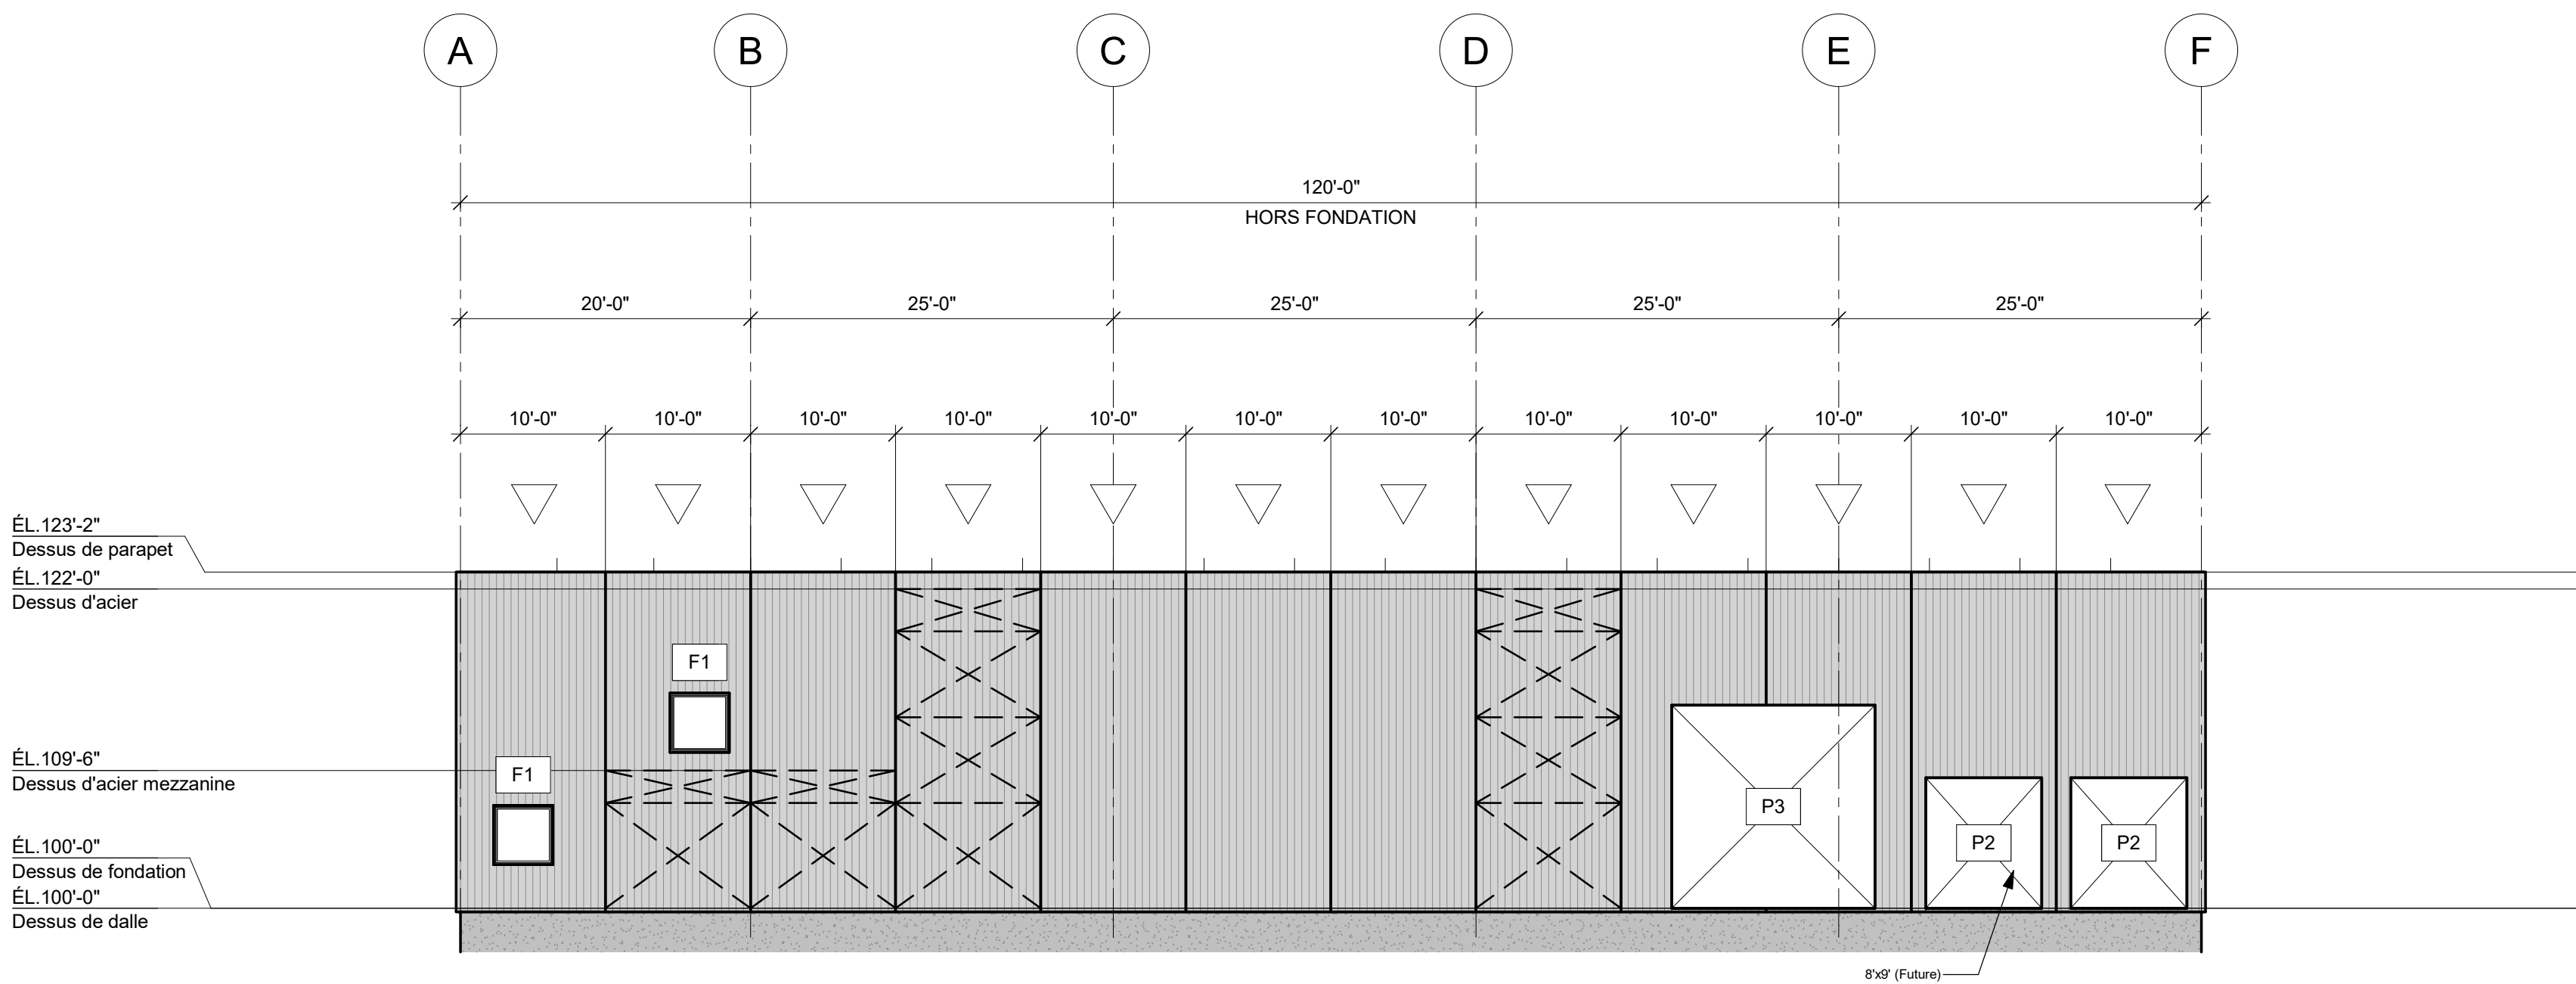


[illegible]

CÉDULE DES FENÊTRES						
Identifiant	Qté.	Installation	Description	Dimensions ext. cadre largeur X hauteur	Couleur du cadre	Remarques
F1	2		Fenêtre en aluminium fixe avec bris thermique et verre scellé + Low-E argon clair	4'-0" x 4'-0"	Cadre d'Aluminium (Blanc ext. et int.)	

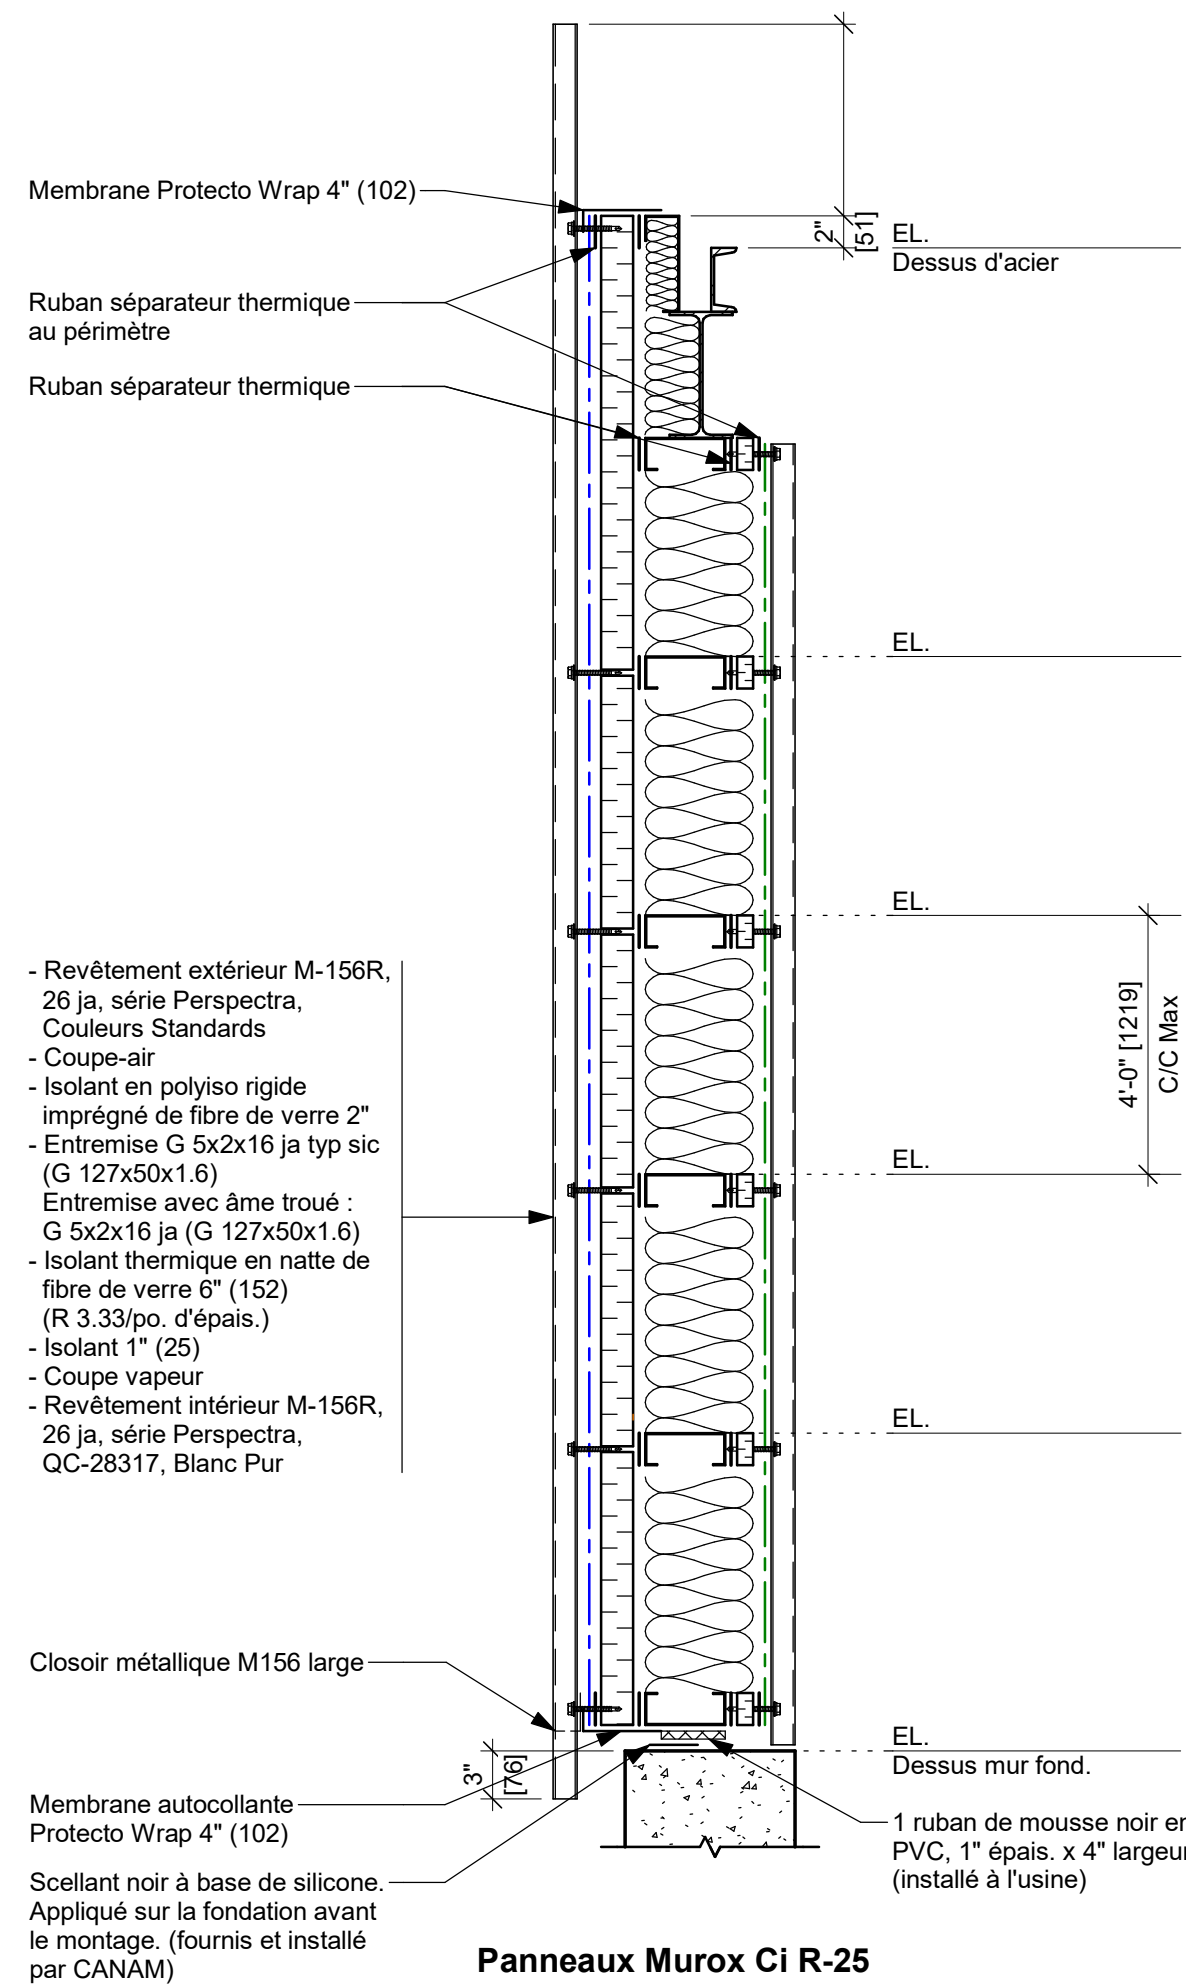

ÉLÉVATION AXE 5 (EST)
1" = 10'-0"