


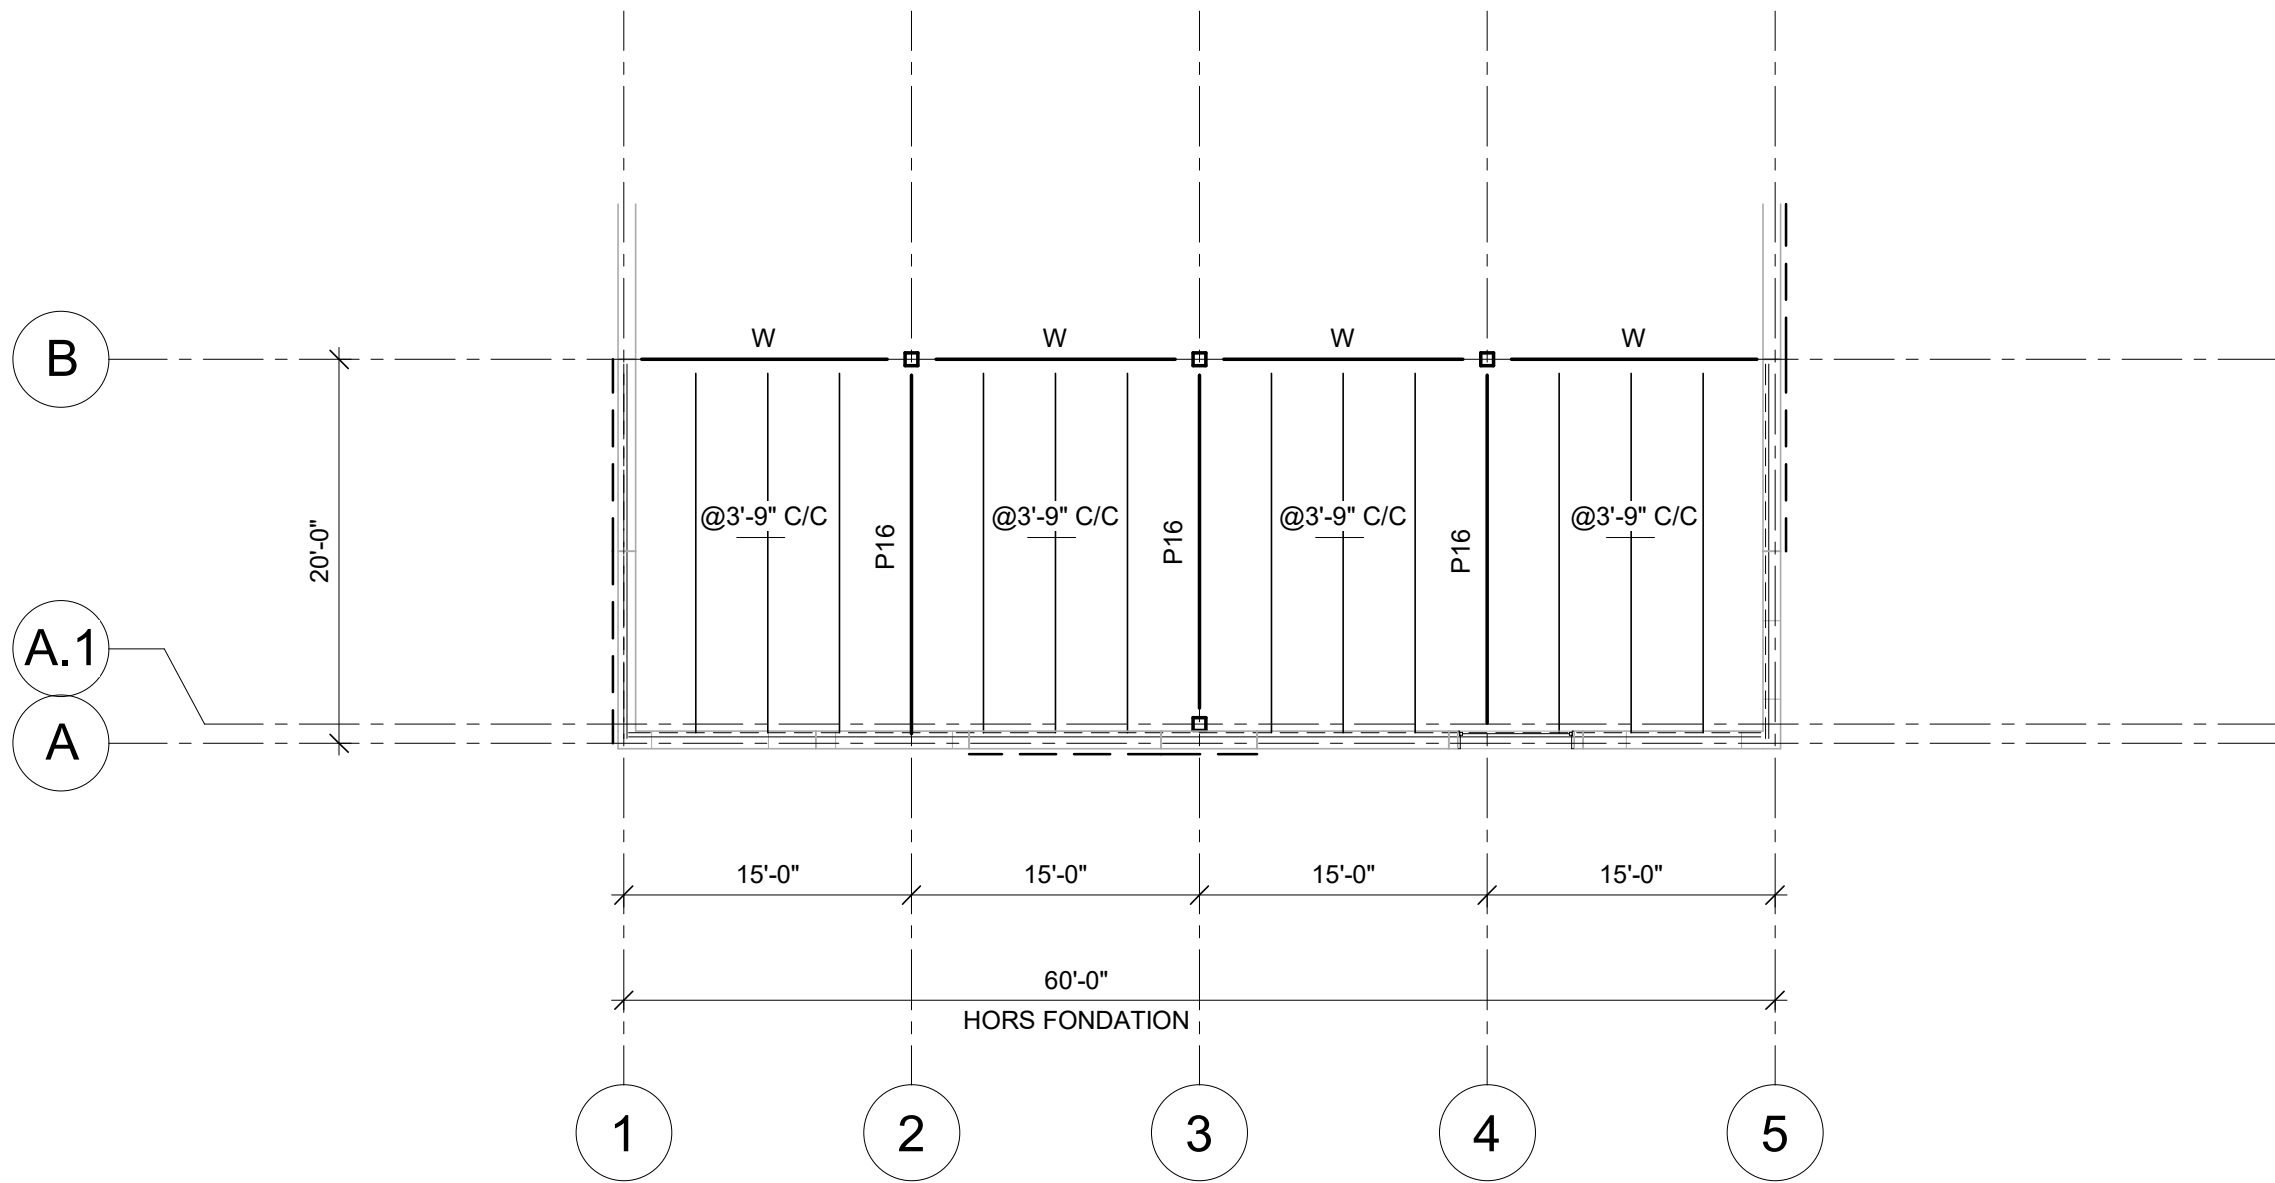

PLAN DE MEZZANINE
1" = 10'-0"

NOTE POUR LE CONTRACTEUR/ÉRECTEUR:
II EST STRICTEMENT DÉFENDU DE MODIFIER, COPIER, REPRODUIRE OU DE DISTRIBUER CES DESSINS OU QUELQUES REPRÉSENTATIONS DE CES DESSINS, PAR TOUTES SOURCES DE MÉDIA INCLUANT ÉLECTRONIQUEMENT, SANS L'APPROBATION ÉCRITE DE GROUPE CANAM INC.

MEZZANINE

HAUTEUR LIBRE SOUS MEZZ. : 8'-2"
DESSUS D'ACIER MEZZ. : 100'-0"
HAUTEUR LIBRE DESSUS MEZZ. : 8'-2"

MEZZANINE

C.M. : 70 psf
C.V. : 50 psf
Δ L/360


PRÉLIMINAIRE

NE DOIT PAS SERVIR À LA
CONSTRUCTION

REVISION	DATE	DESCRIPTION	DESS	VER.
GERANT DE PROJET				
		-		
		-		
		-		
		-		

DESSIN:			
DESSINE PAR AD	CONÇU PAR	INGÉNIEUR DU PROJET	ECHELLE: 1" = 10'-0"
VÉRIFIÉ PAR	INGÉNIEURS CONSEILS / ARCHITECTES		DATE (jj/mm/aaaa) : 18/11/2025

CLIENT:

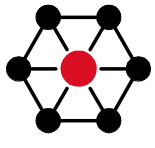**CANAM**

11505, 1re Avenue, bureau 500, Saint-Georges Beauce
Québec, Canada, G5Y 7X3
Téléphone : (418) 228-8031
Sans frais : (877) 499-6049
www.canam.com

SCEAU PROFESSIONNEL

PROJET

Saint-Gédéon , Québec

TITRE

CROQUIS PRÉLIMINAIRE - PLAN DE
MEZZANINE

NUMÉRO CONTRAT P2025-182	NUMÉRO DESSIN EsMx201	DIVISION	RÉVISION 
-----------------------------	--------------------------	----------	---

Initiales