


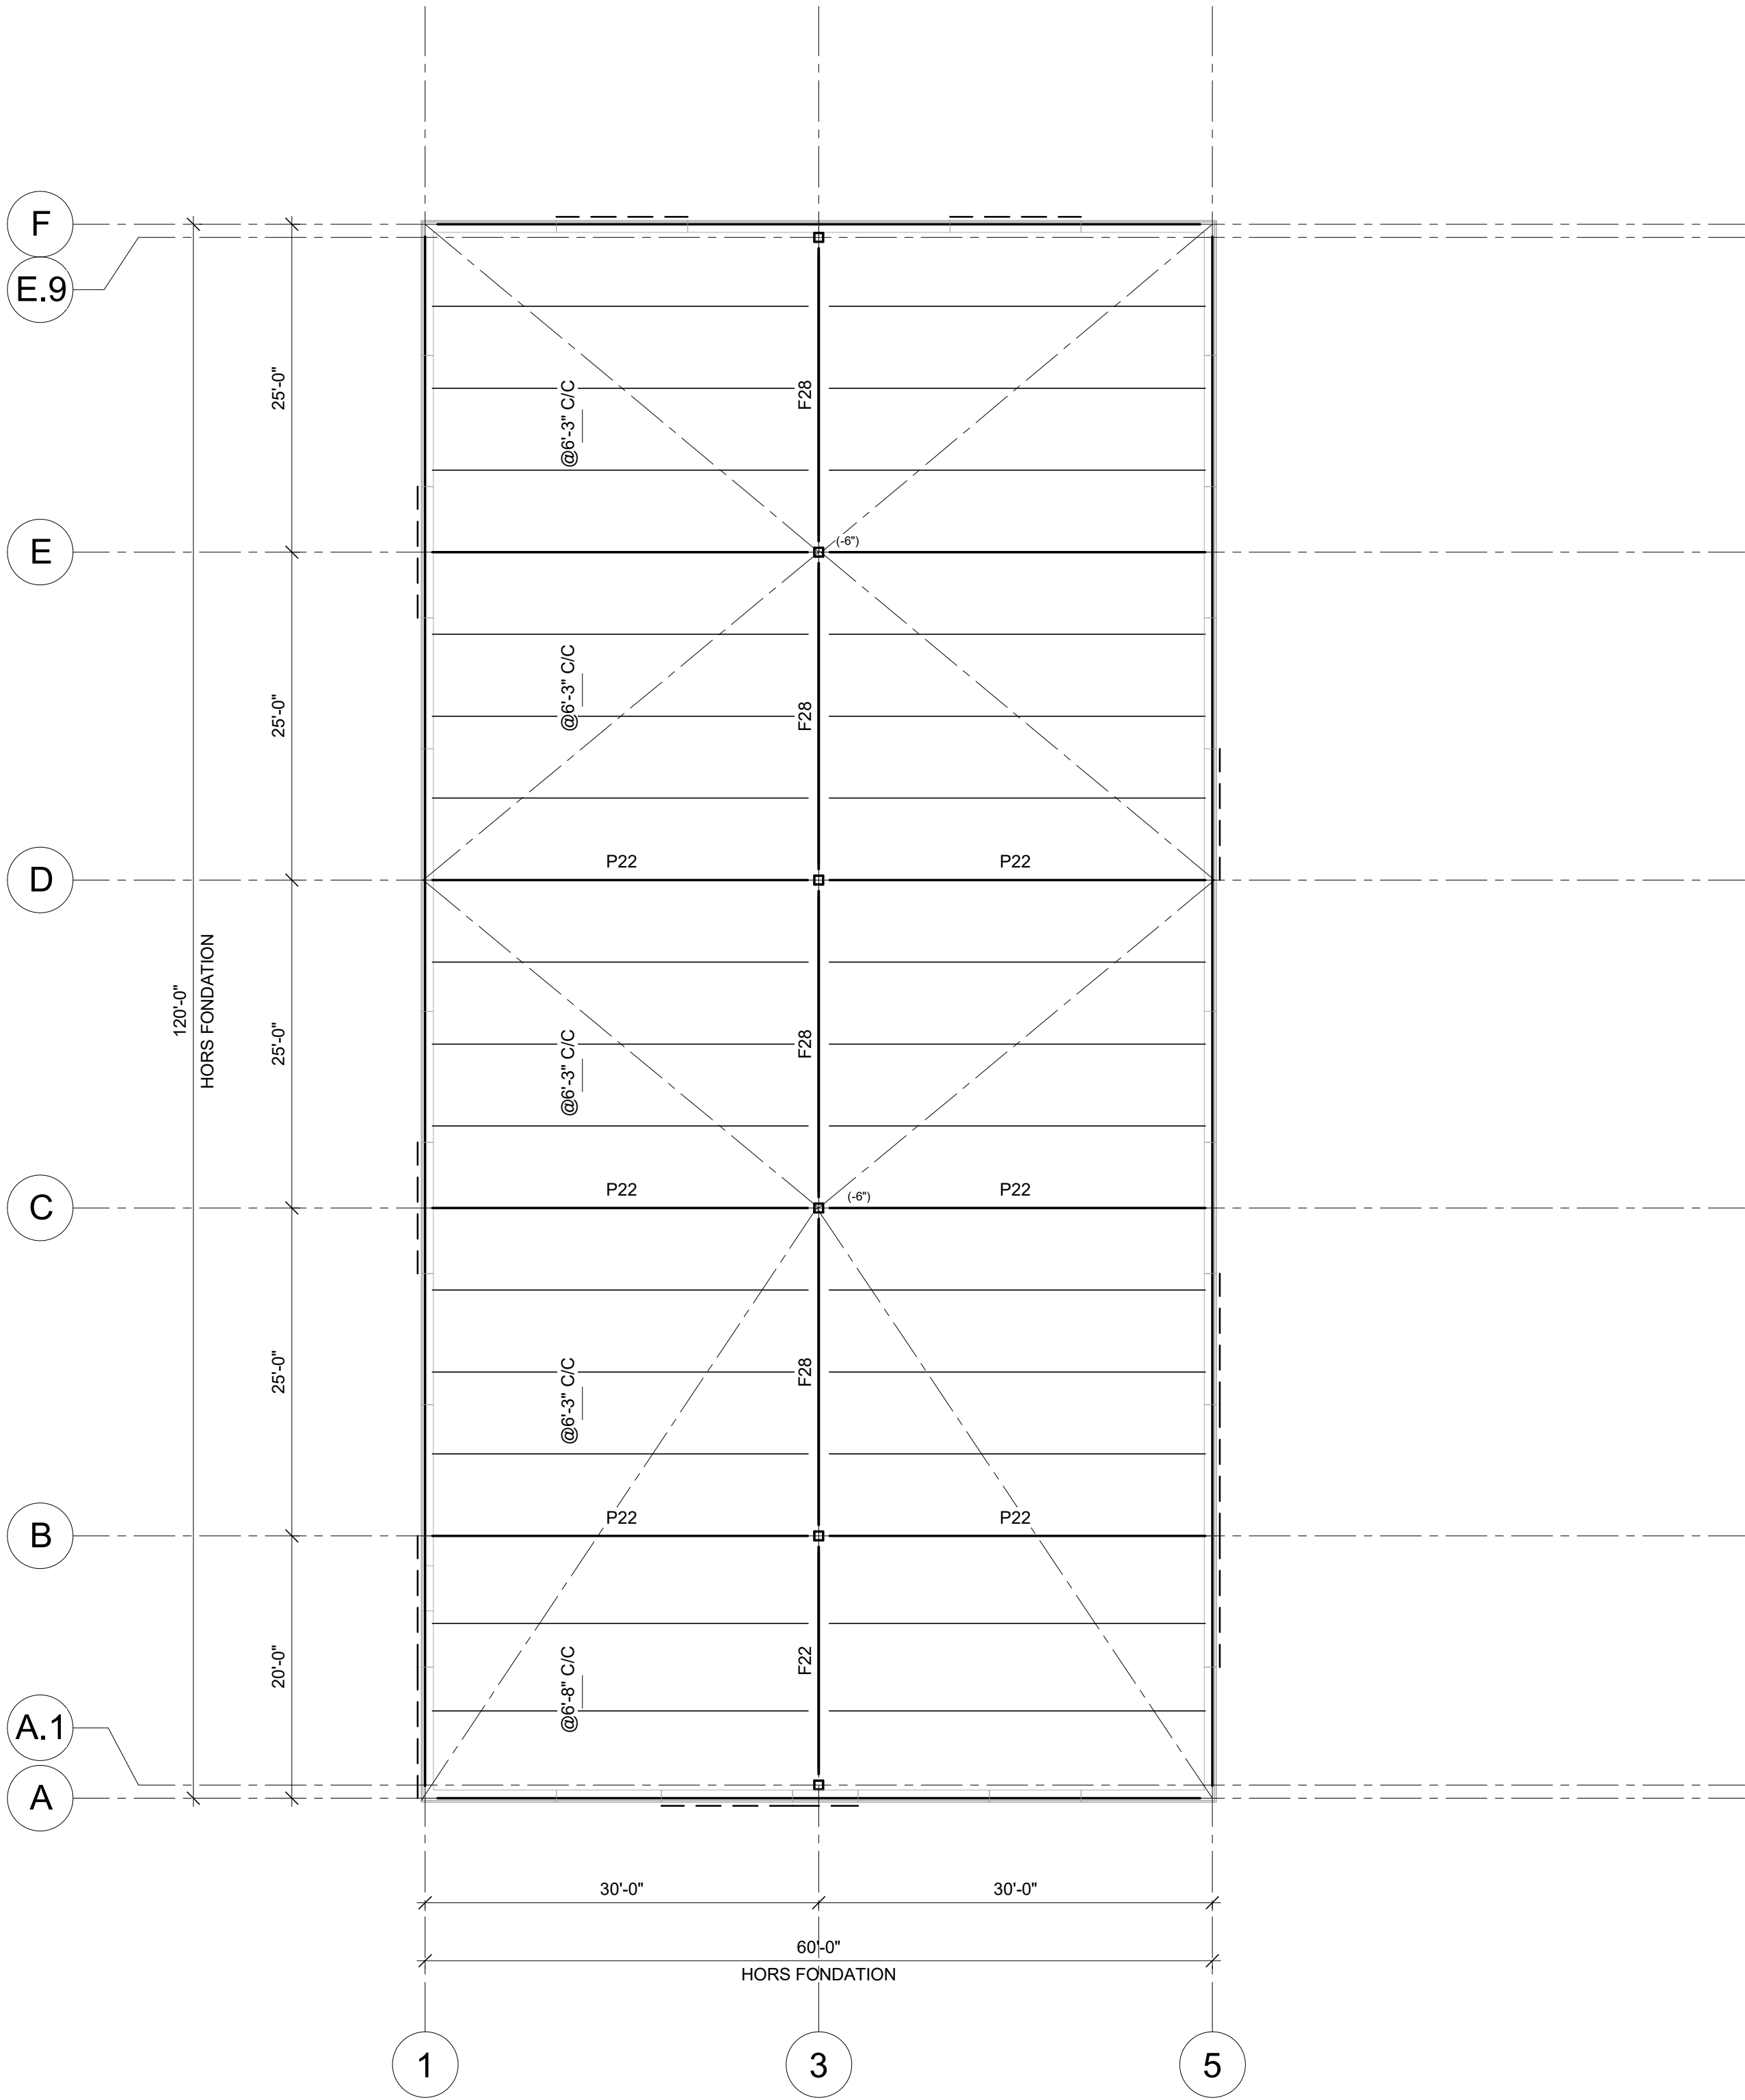

PLAN DE TOIT
1" = 10'-0"

CHARGES :


- Charge morte au toit (excluant charge collatérale): 18 lbs/pi²
- Charge collatérale : 5 lbs/pi² (incluant éclairage et/ou mécanique et gicleurs plus petits que 4" de diamètre) : 59.3 lbs/pi²
- Charge de neige au toit : 0lbs/pi²
- Charge vive au toit : 7.94 lbs/pi²
- Charge de vent q 1/50 : S_s = 58.49 lbs/pi²
- Charge de neige au sol : S_r = 12.53 lbs/pi²
- Catégorie de risque : normal
- Coefficient de surcharge de neige : C_b = 0.8
- : C_w = 1.0

- Code Applicable : Code National du Bâtiment du Canada
- Code du bâtiment du Québec, dernières éditions adoptées
- Code de Pratique Standard ICQA.

- Type de sol assumé : classe D

- NOTE :
1. Si toutefois la catégorie d'emplacement devient E ou F selon le rapport géotechnique, le concept structural préliminaire (localisation et géométrie des contreventements, etc.) devra être validé et coordonné par l'ingénieur de Canam.

DIAGRAMME DE SOULÈVEMENT BRUT (NON PONDÉRÉ)

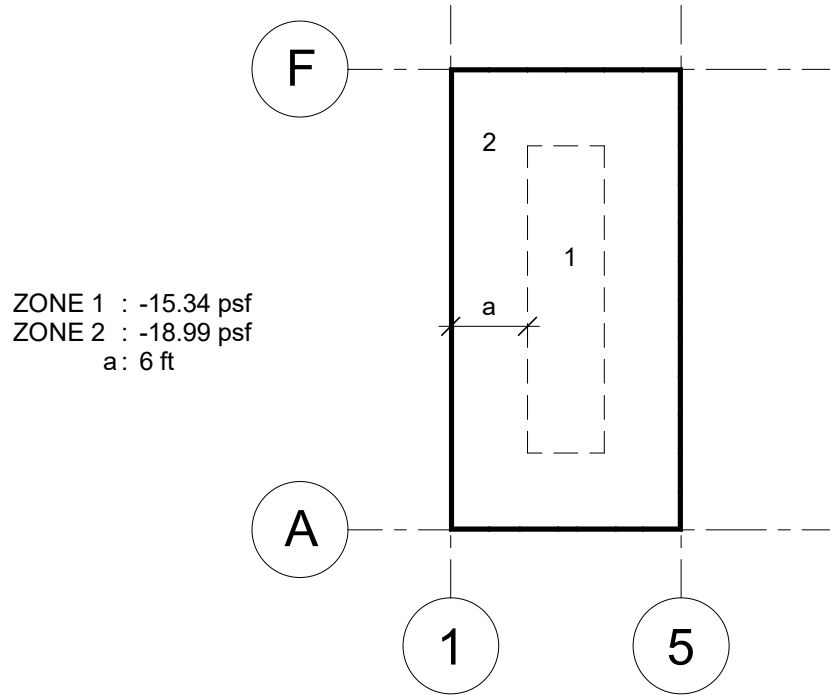

PRESSION POSITIVE DU VENT
(NON PONDÉRÉE): 8.77 psf

NOTE POUR LE CONTRACTEUR/ÉRECTEUR:

IL EST STRICTEMENT DÉFENDU DE MODIFIER, COPIER, REPRODUIRE OU DE DISTRIBUER CES DESSINS OU QUELQUES REPRÉSENTATIONS DE CES DESSINS, PAR TOUTES SOURCES DE MÉDIA INCLUANT ÉLECTRONIQUEMENT, SANS L'APPROBATION ÉCRITE DE GROUPE CANAM INC.

TOIT

DESSUS DE PILASTRE DDP : 98'-0"
DESSUS DE PILASTRE : 99'-0"
DESSUS DE LA DALLE : 100'-0"
DESSUS DE LA FONDATION : 100'-0"
HAUTEUR LIBRE : 18'-0"
DESSUS D'ACIER : 122'-0"
HAUTEUR DE PARAPET : 1'-2"

CHARGES

C.M. : 18 lbs/pi²
Coll. : 5 lbs/pi²
S_s : 58.49 lbs/pi²
S_r : 12.53 lbs/pi²
C_b x C_w : 0.8
C.V. au toit : 0lbs/pi²
I_s : 1.0
Charge de neige au toit : 59.3 lbs/pi²
I_w : 1.0
Vent q= 1/50 : lbs/pi²

Seisme (Sol de classe D assumé)

I_E : 1.0
S_s (0.2) : 0.2100
S_s (0.5) : 0.1430
S_s (1.0) : 0.0840
S_s (2.0) : 0.0440
S_s (5.0) : 0.0120
S_s (10.0) : 0.0050
PGA : 0.1300
PGV : 0.1280


PRÉLIMINAIRE

NE DOIT PAS SERVIR À LA
CONSTRUCTION

REVISION	DATE	DESCRIPTION	DESS	VER.
GERANT DE PROJET				
		-		
		-		
		-		
		-		

DESSIN:			
DESSINE PAR AD	CONÇU PAR	INGÉNIEUR DU PROJET	ECHELLE: Comme indiqué
VÉRIFIÉ PAR	INGÉNIEURS CONSEILS / ARCHITECTES		DATE (jj/mm/aaaa) : 18/11/2025

CLIENT:

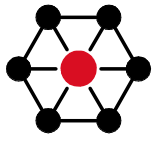**CANAM**


11505, 1re Avenue, bureau 500, Saint-Georges Beauce
Québec, Canada, G5Y 7X3
Téléphone : (418) 228-8031
Sans frais : (877) 499-6049
www.canam.com

SCEAU PROFESSIONNEL

PROJET

Saint-Gédéon , Québec

TITRE
CROQUIS PRÉLIMINAIRE - PLAN DE TOIT

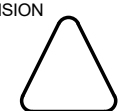NUMÉRO CONTRAT P2025-182	NUMÉRO DESSIN EsMx401	DIVISION	RÉVISION 
-----------------------------	--------------------------	----------	---

Initiales