




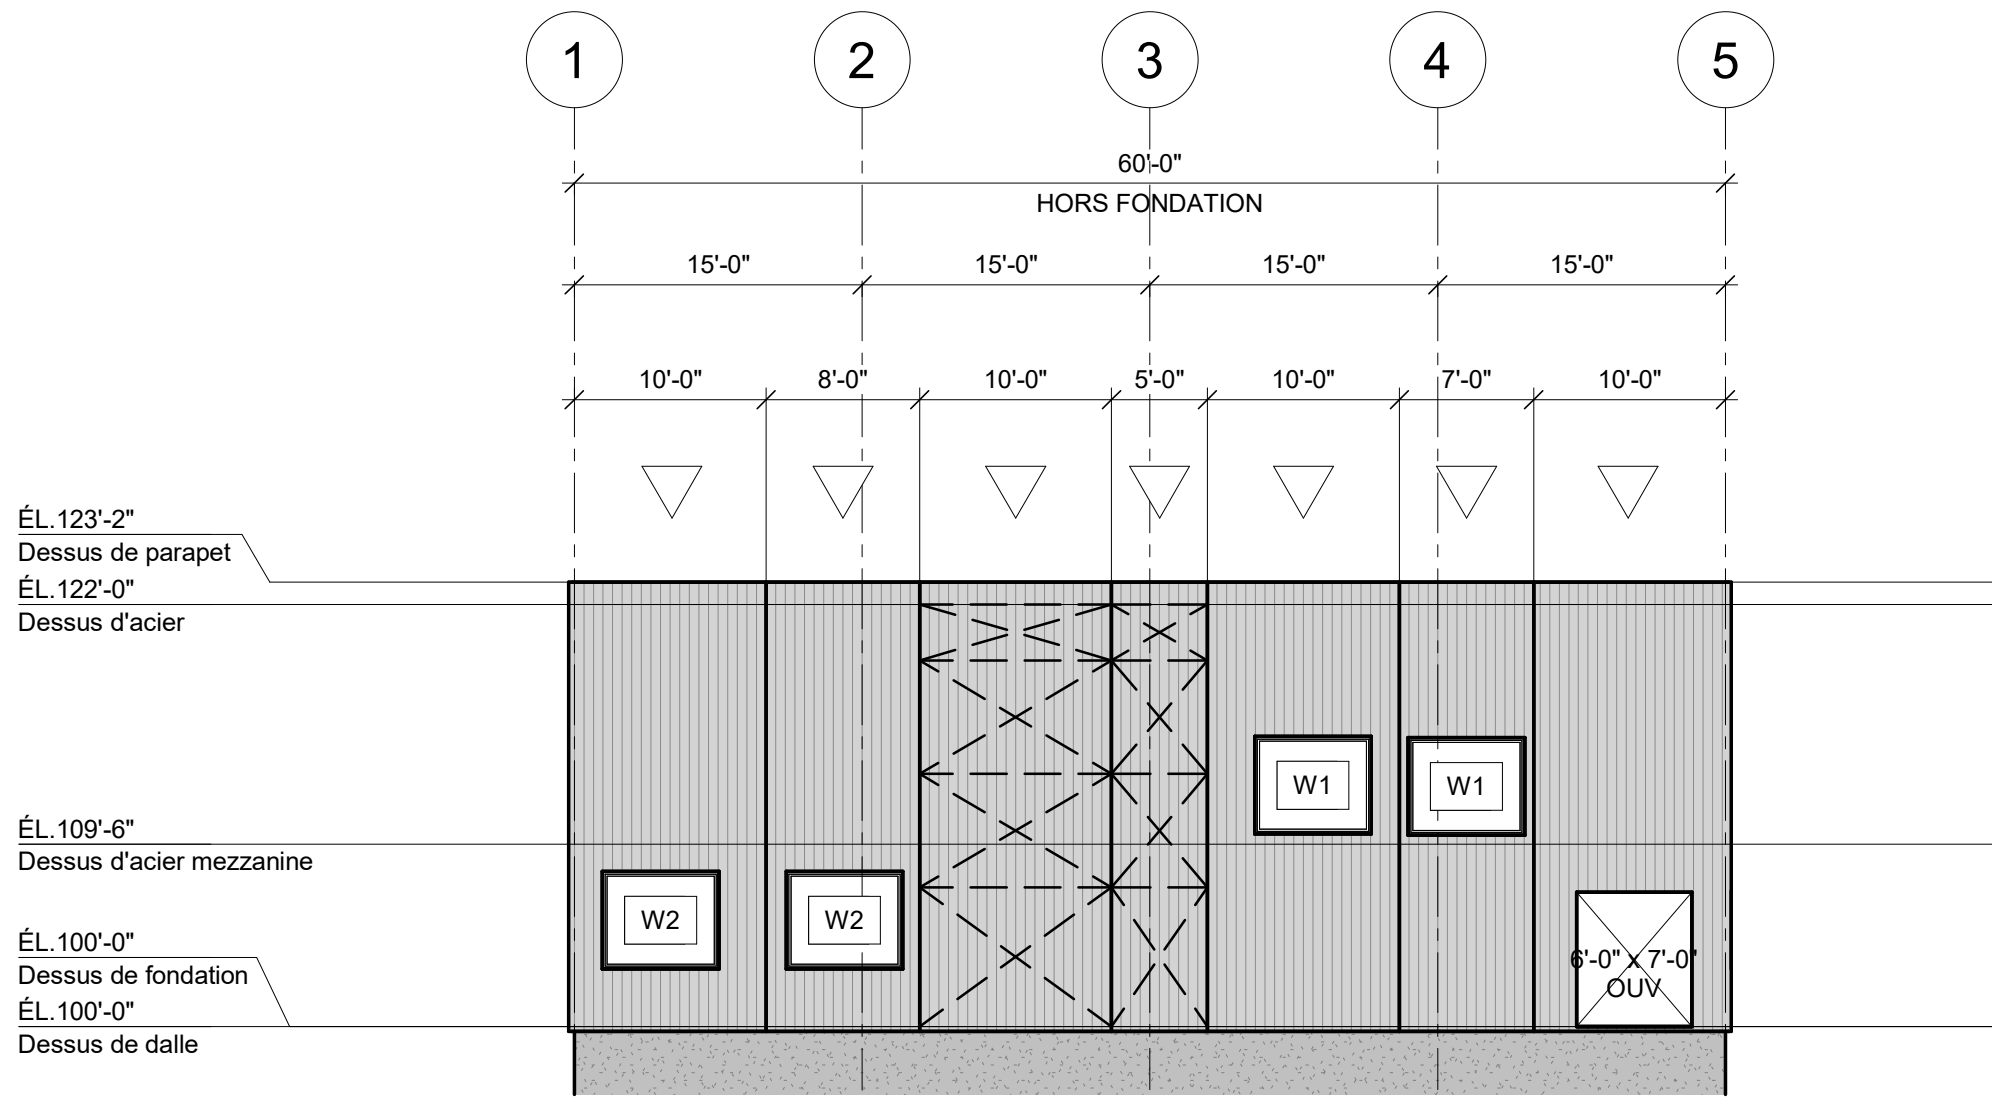

ÉLEVATION AXE A (SUD)
1" = 10'-0"

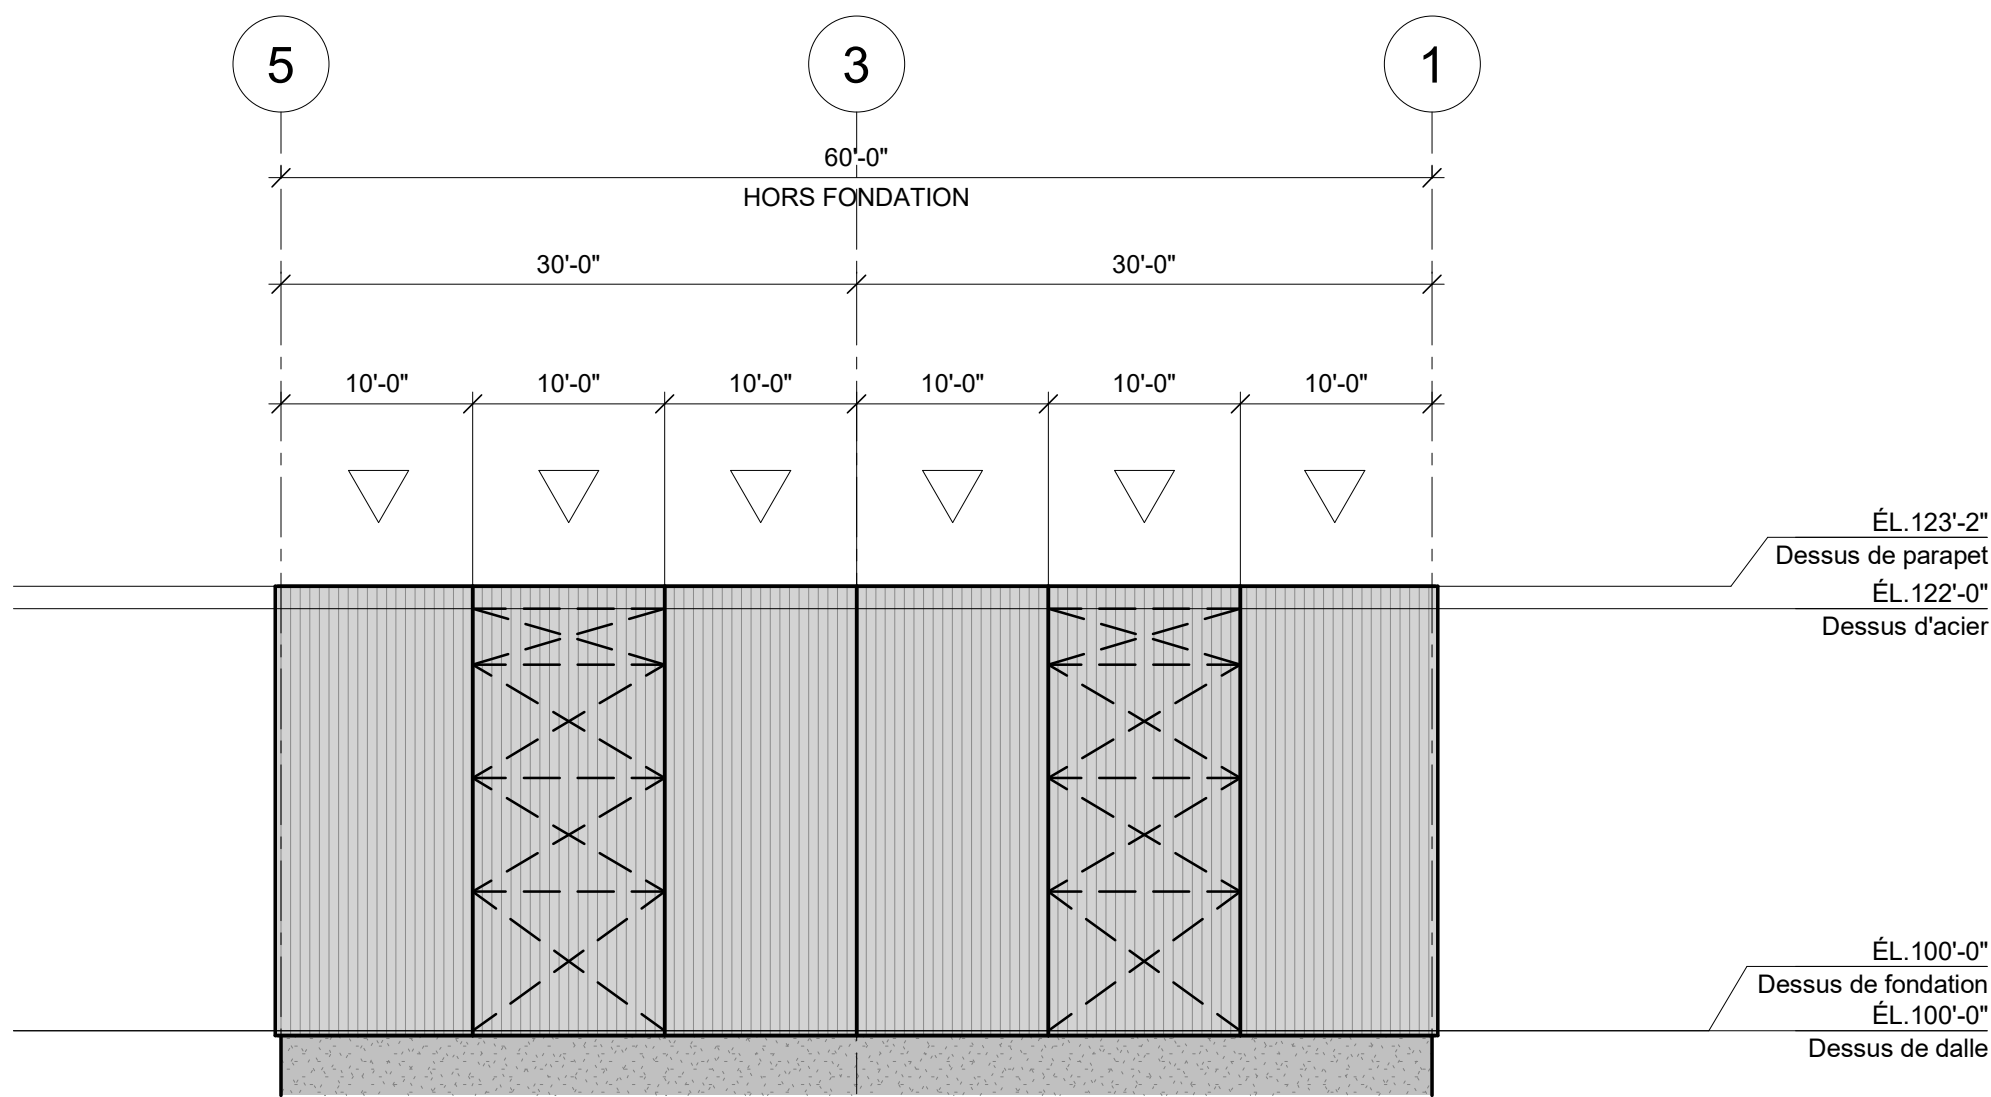

ÉLEVATION AXE F (NORD)
1" = 10'-0"

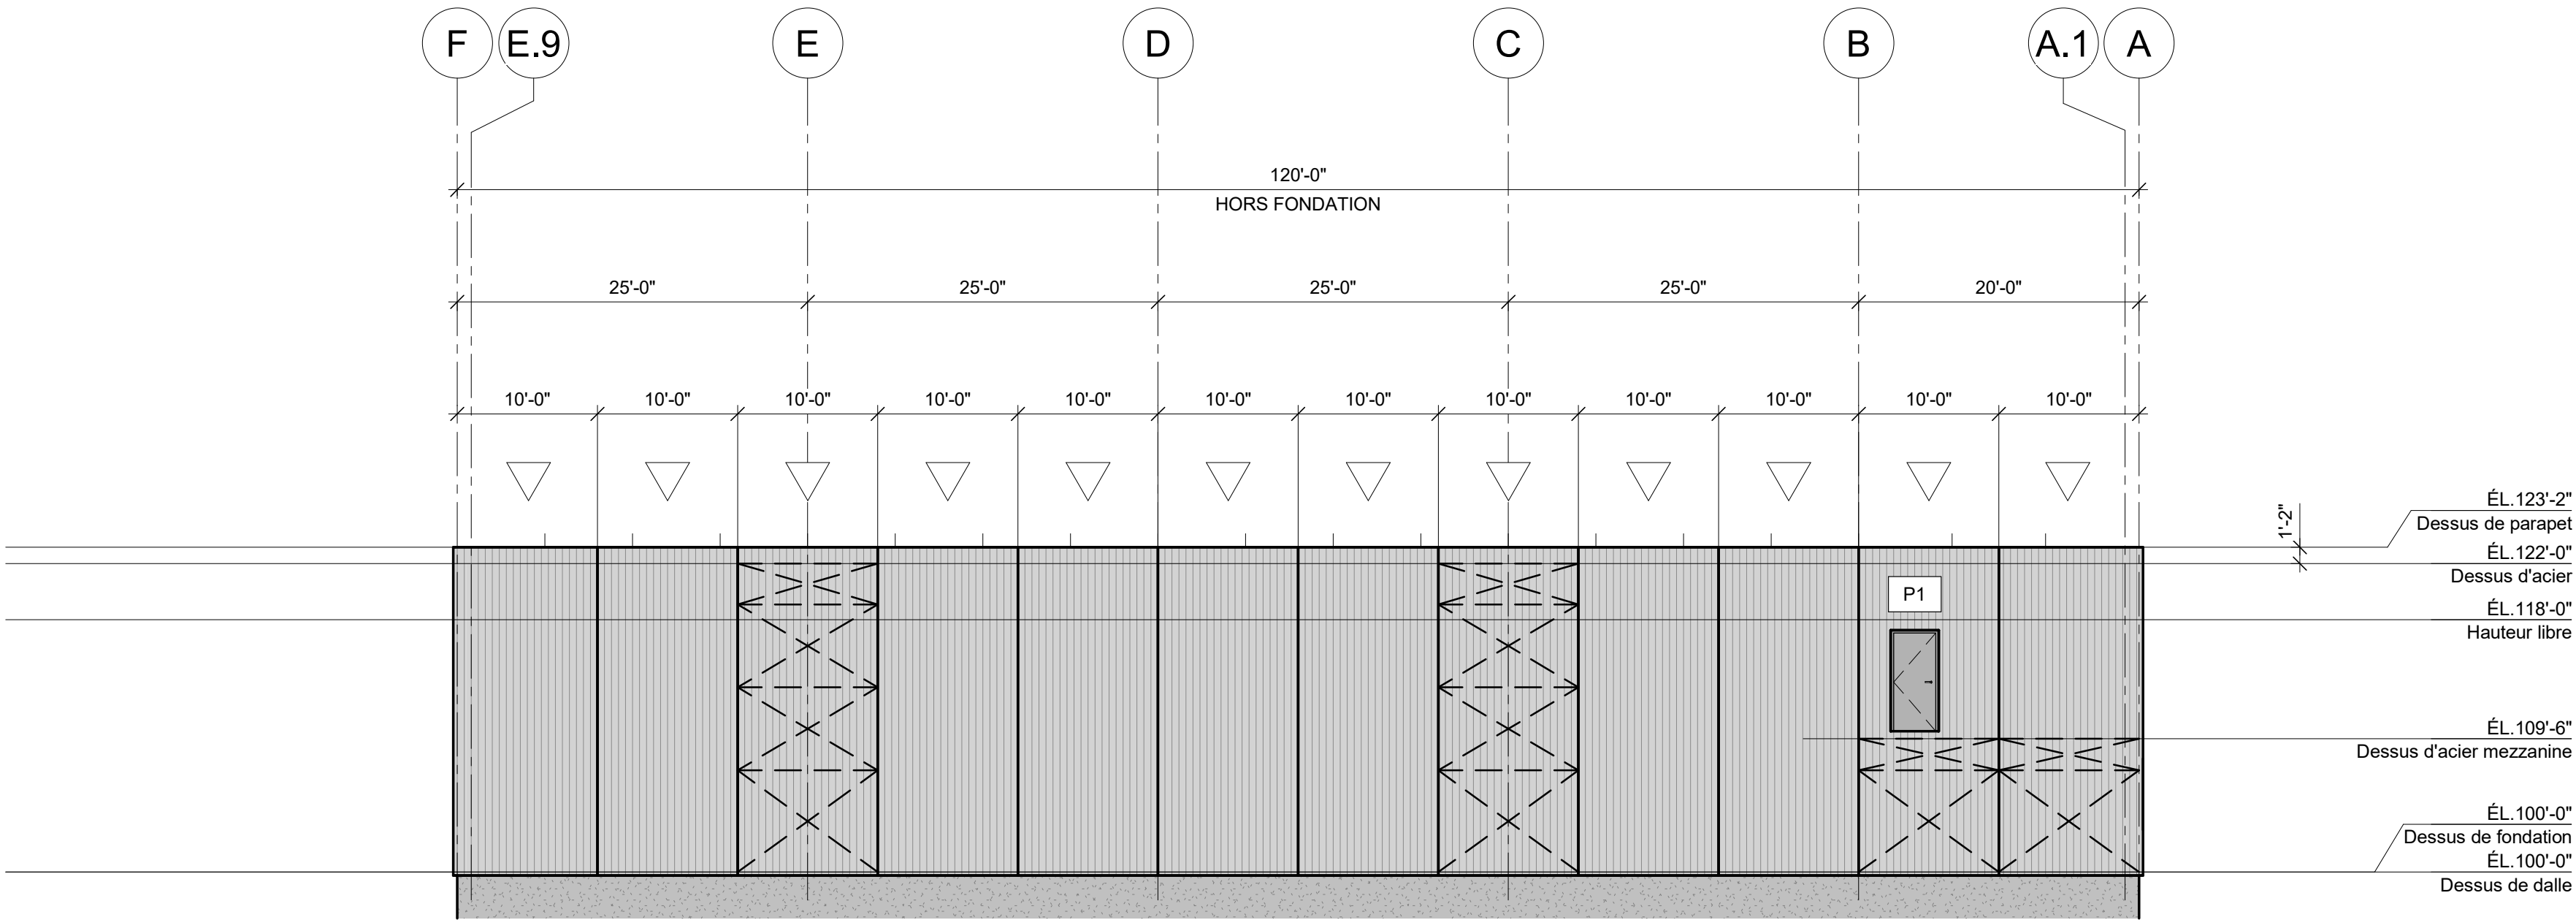

ÉLEVATION AXE 1 (OUEST)
1" = 10'-0"

NOTE POUR LE CONTRACTEUR/ÉRECTEUR:
IL EST STRICTEMENT DÉFENDU DE MODIFIER, COPIER, REPRODUIRE OU DE DISTRIBUER CES DESSINS OU QUELQUES REPRÉSENTATIONS DE CES DESSINS, PAR TOUTES SOURCES DE MÉDIA INCLUANT ÉLECTRONIQUEMENT, SANS L'APPROBATION ÉCRITE DE GROUPE CANAM INC.

PRÉLIMINAIRE
NE DOIT PAS SERVIR À LA
CONSTRUCTION

REVISION	DATE	DESCRIPTION	DESS	VER.
GERANT DE PROJET				
		-		
		-		
		-		
		-		
DESSIN:				
DESSINE PAR	CONÇU PAR	INGÉNIEUR DU PROJET	ECHELLE:	
AD			1" = 10'-0"	
VÉRIFIÉ PAR	INGÉNIEURS CONSEILS / ARCHITECTES		DATE (jj/mm/aaaa) :	
			18/11/2025	

CLIENT:



11505, 1re Avenue, bureau 500, Saint-Georges Beauce
Québec, Canada, G5Y 7X3
Téléphone : (418) 228-8031
Sans frais : (877) 499-6049
www.canam.com

SCEAU PROFESSIONNEL

PROJET

Saint-Gédéon , Québec

TITRE

CROQUIS PRÉLIMINAIRE -
ÉLÉVATIONS

NUMÉRO CONTRAT	NUMÉRO DESSIN	DIVISION	RÉVISION
P2025-182	EsMx501		

Initiales

