
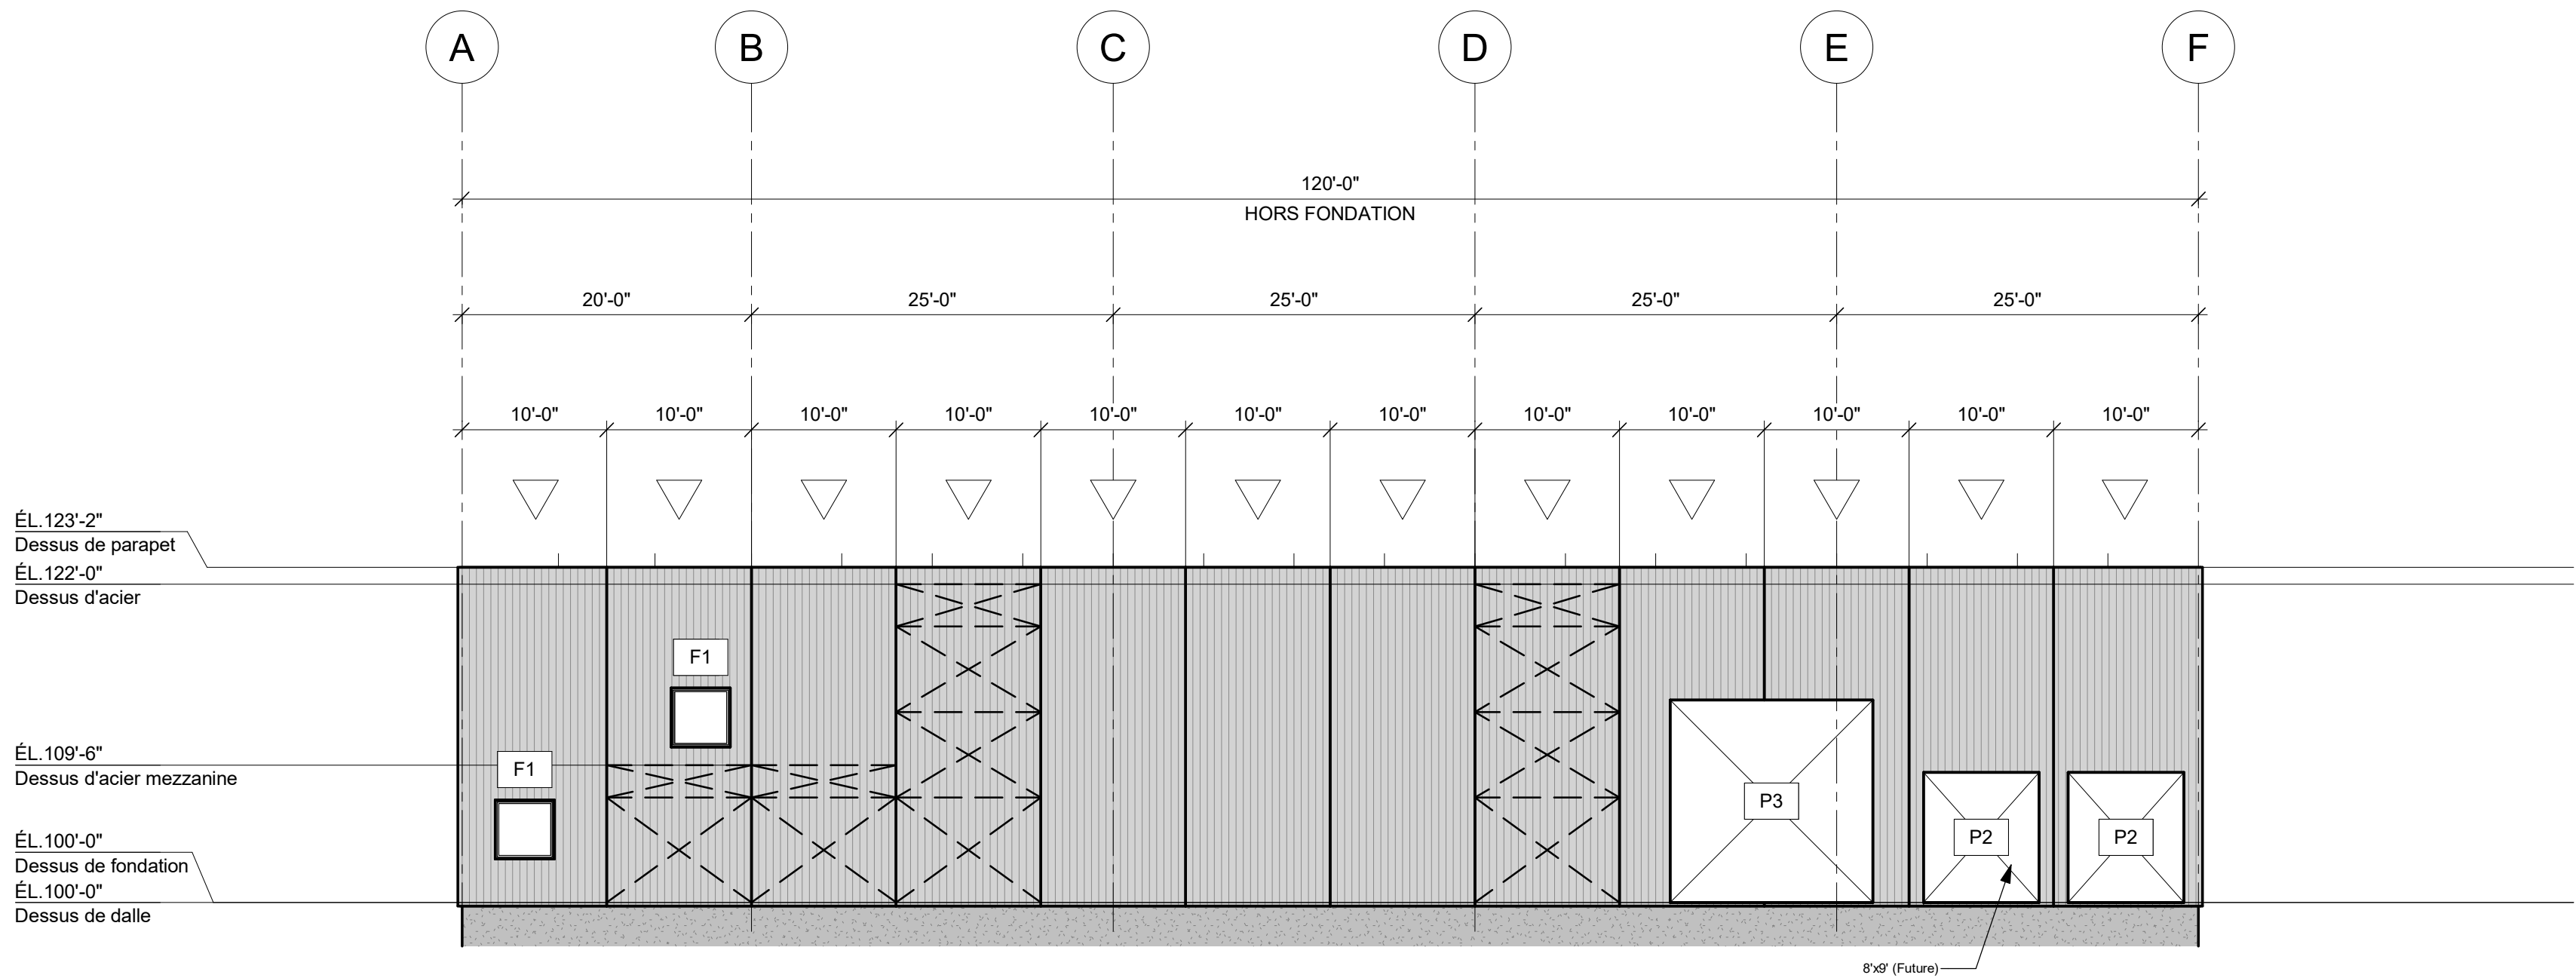


CÉDULE DES P.M. ET DES OUVERTURES			
Total	Type	Tag	Commentaires
1	6'-0" x 7'-0"	OUV	
Total général: 1			

[illegible]

CÉDULE DES FENÊTRES						
Identifiant	Qté.	Installation	Description	Dimensions ext. cadre largeur X hauteur	Couleur du cadre	Remarques
F1	2		Fenêtre en aluminium fixe avec bris thermique et verre scellé + Low-E argon clair	4'-0" x 4'-0"	Cadre d'Aluminium (Blanc ext. et int.)	

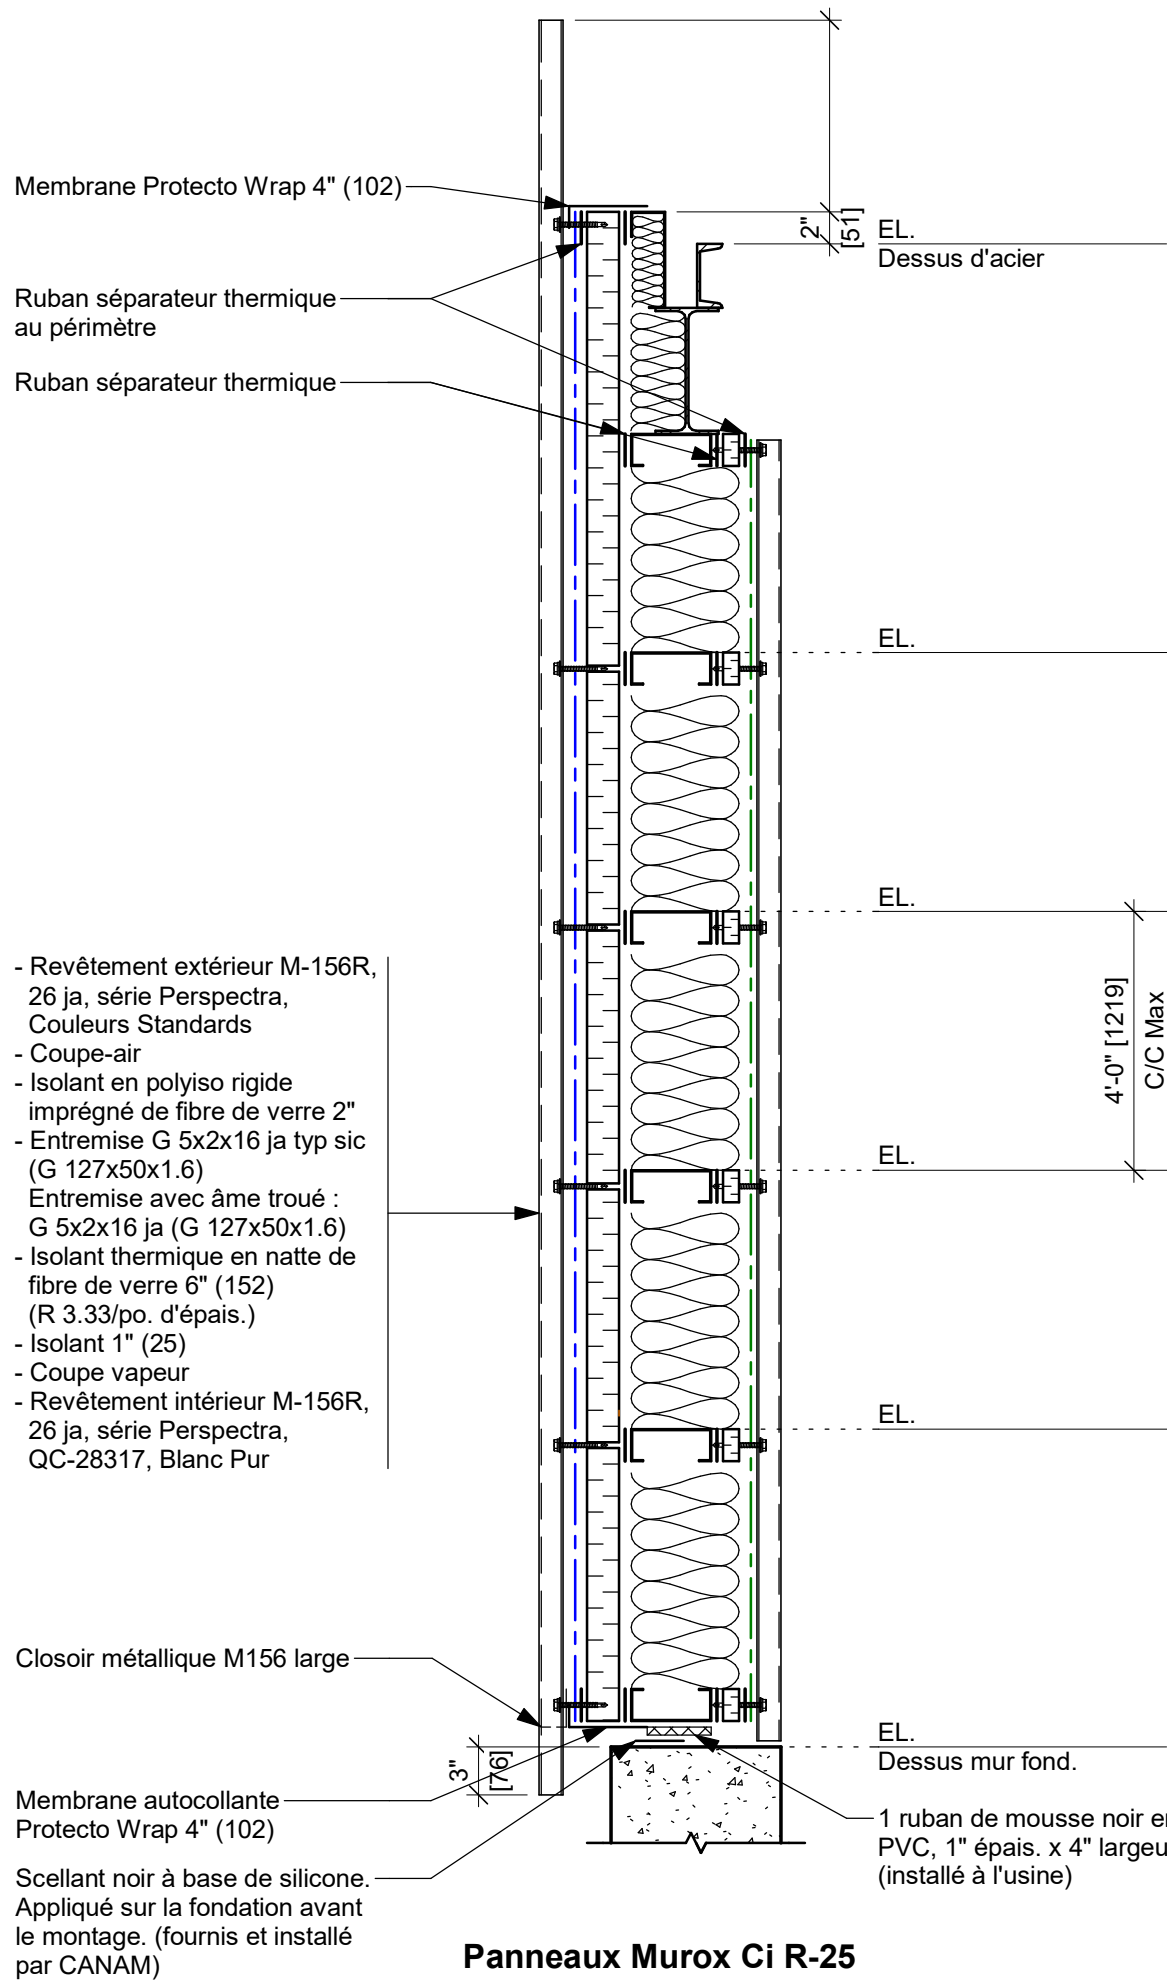

ÉLÉVATION AXE 5 (EST)
1" = 10'-0"

NOTE POUR LE CONTRACTEUR/ÉRECTEUR:

II EST STRICTEMENT DÉFENDU DE MODIFIER, COPIER, REPRODUIRE OU DE DISTRIBUER CES DESSINS OU QUELQUES REPRÉSENTATIONS DE CES DESSINS, PAR TOUTES SOURCES DE MÉDIA INCLUANT ÉLECTRONIQUEMENT, SANS L'APPROBATION ÉCRITE DE GROUPE CANAM INC.

PRÉLIMINAIRE

NE DOIT PAS SERVIR À LA
CONSTRUCTION

REVISION	DATE	DESCRIPTION	DESS.	VER.
GERANT DE PROJET				
		-		
		-		
		-		
		-		
		-		

DESSIN:			
DESSINÉ PAR	CONÇU PAR	INGÉNIEUR DU PROJET	ÉCHELLE:
INITIALE			Comme indiqué
VÉRIFIÉ PAR	INGÉNIEURS CONSEILS / ARCHITECTES		DATE (jj/mm/aaaa) :
			18/11/2025

CLIENT



SCEAU PROFESSIONNEL

PROJE

Saint-Gédéon , Québec

TITRE

CROQUIS PRÉLIMINAIRE -
ÉLEVATION, COUPE DE MUR ET
CÉDULE

NUMÉRO CONTRAT	NUMÉRO DESSIN	DIVISION	RÉVISION
P2025-182	EsMx502		

Initiales