


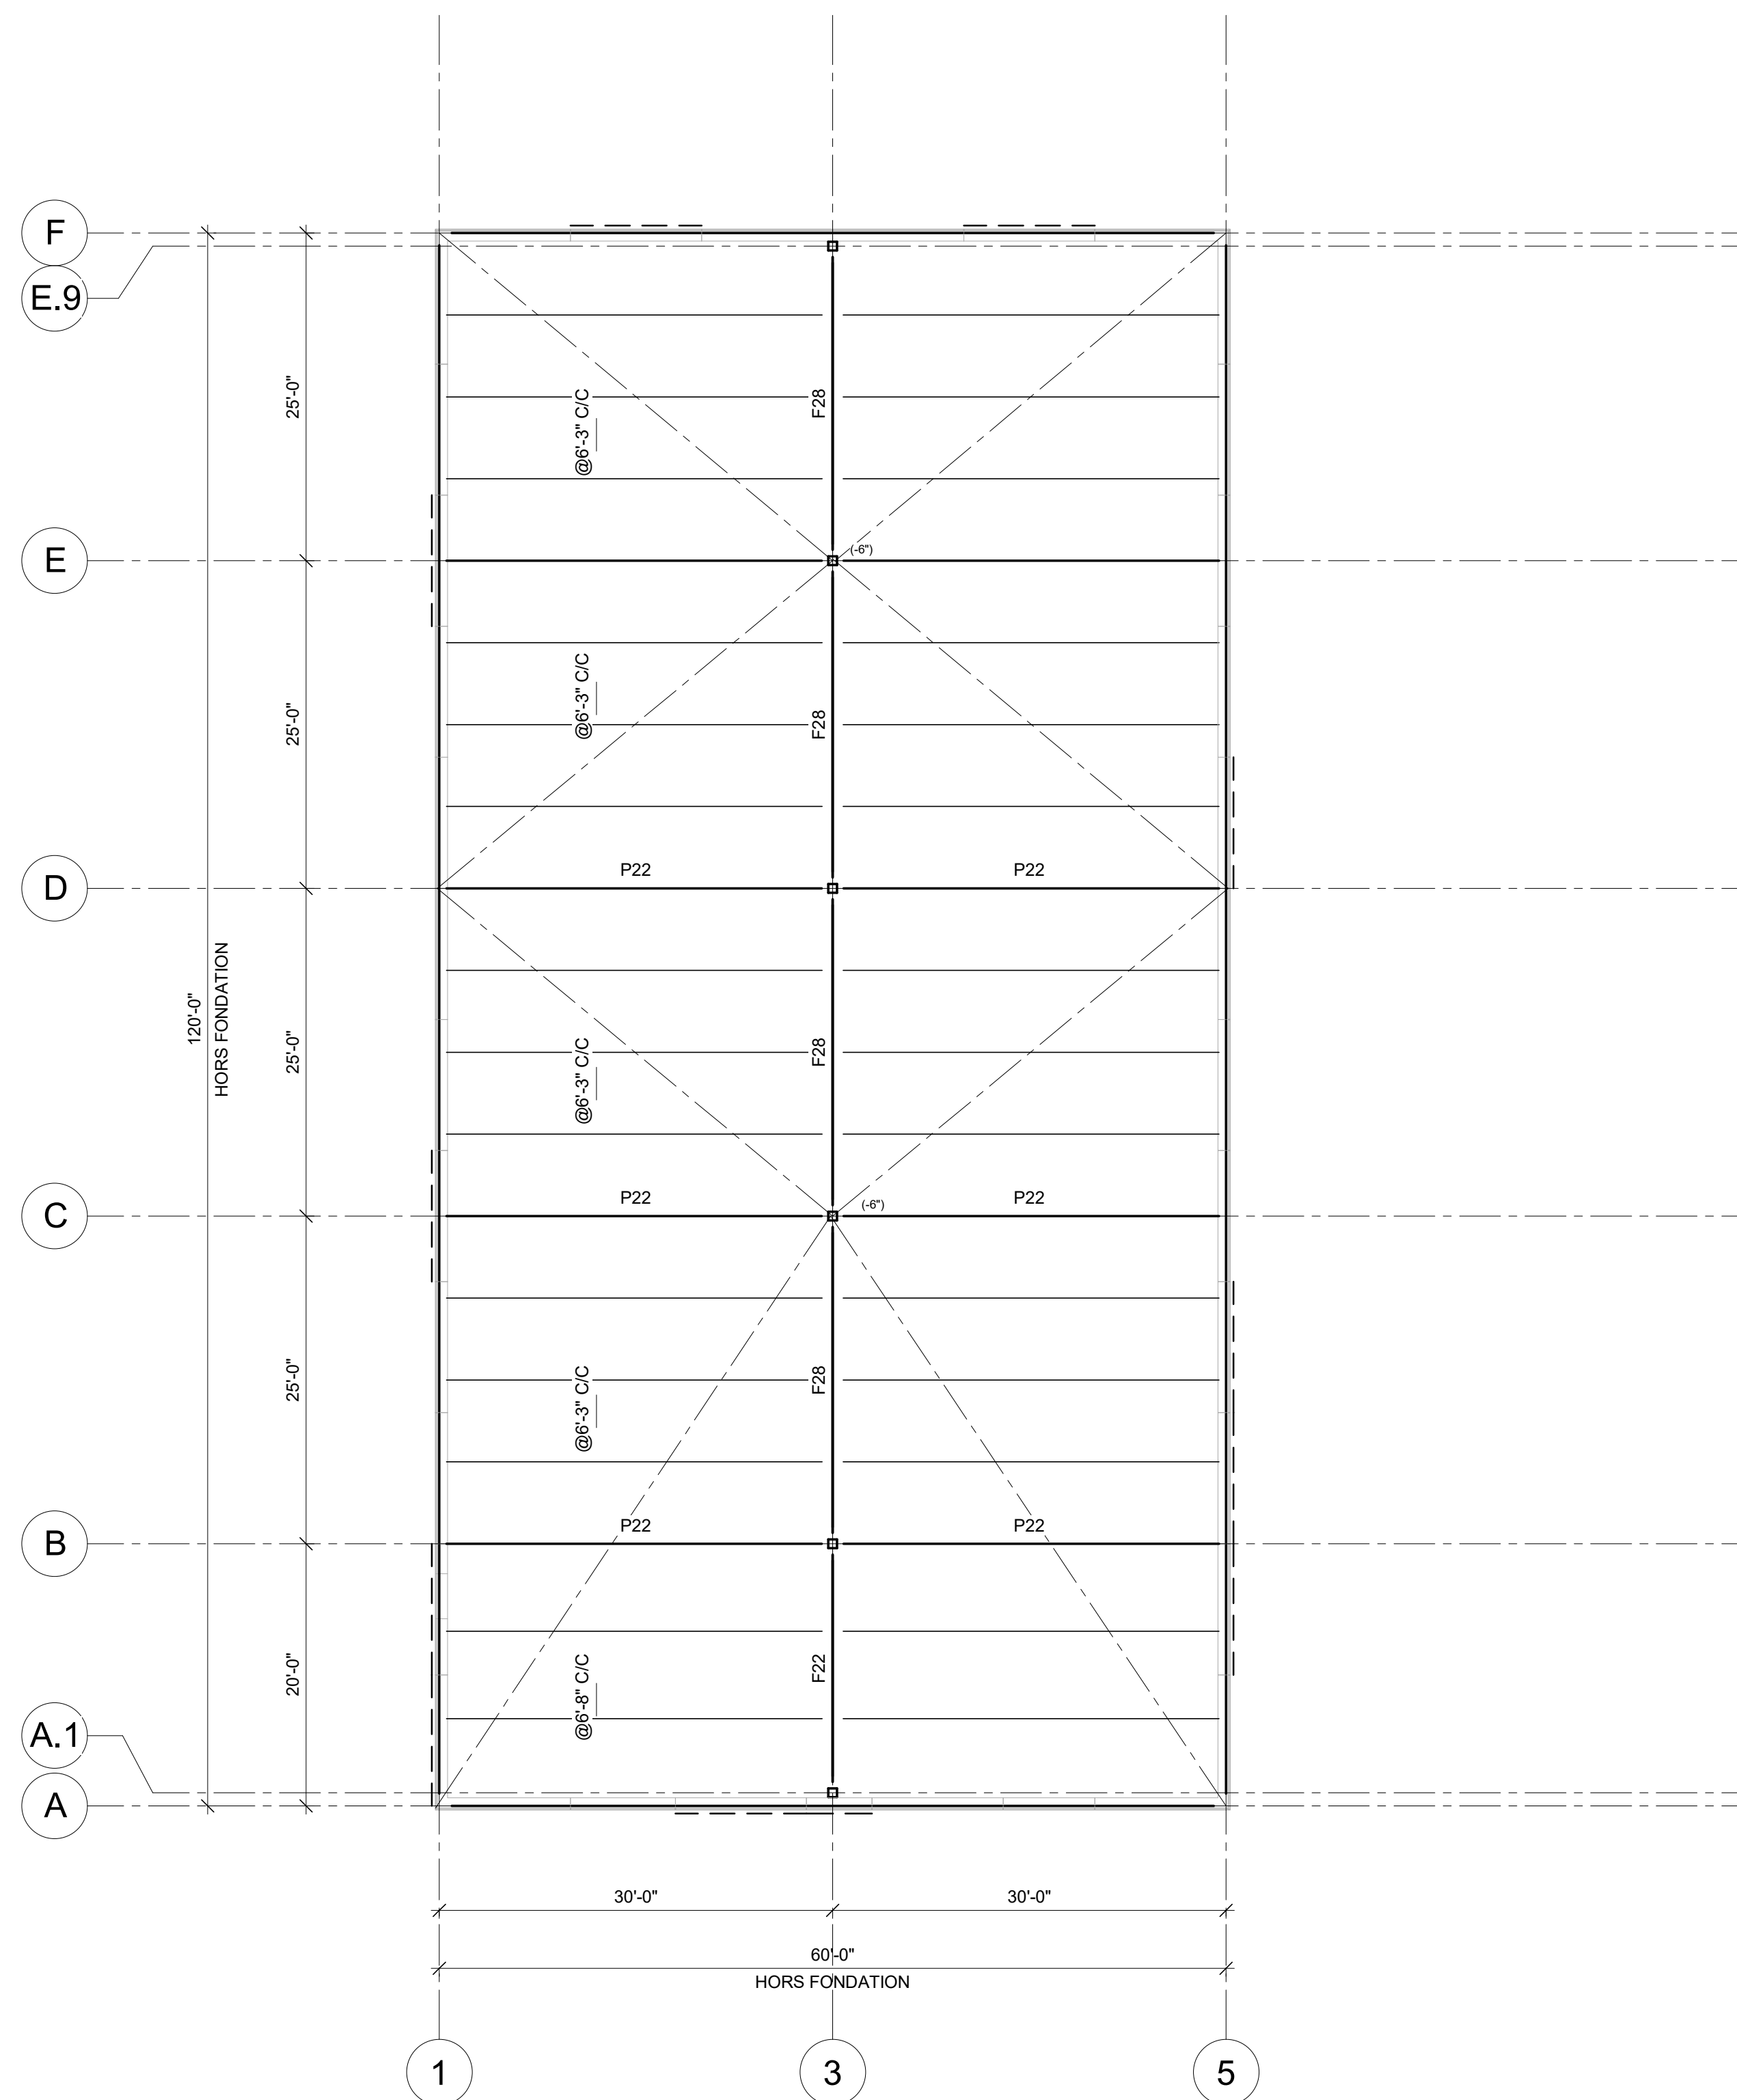

CHARGES :

- Charge morte au toit (excluant charge collatérale): 18 lbs/pi²
- Charge collatérale : 5 lbs/pi² (incluant éclairage et/ou mécanique et gicleurs plus petits que 4" de diamètre)
- Charge de neige au toit : 59.3 lbs/pi²
- Charge vive au toit : 0lbs/pi²
- Charge de vent q : 1/50 : 7.94 lbs/pi²
- Charge de neige au sol : S_w = 58.49 lbs/pi²
S_n = 12.53 lbs/pi²
- Catégorie de risque : normal
- Coefficient de surcharge de neige : C_b = 0.8
C_w = 1.0
- Code Applicable : Code National du Bâtiment du Canada
Code du bâtiment du Québec, dernières éditions adoptées
Code de Pratique Standard ICCA.
- Type de sol assumé : classe D
- NOTE :
 1. Si toutefois la catégorie d'emplacement devient E ou F selon le rapport géotechnique, le concept structural préliminaire (localisation et géométrie des contreventements, etc.) devra être validé et coordonné par l'ingénieur de Canam.

DIAGRAMME DE SOULÈVEMENT BRUT (NON PONDÉRÉ)

