



NORD POUR ÉRECTION SEULEMENT

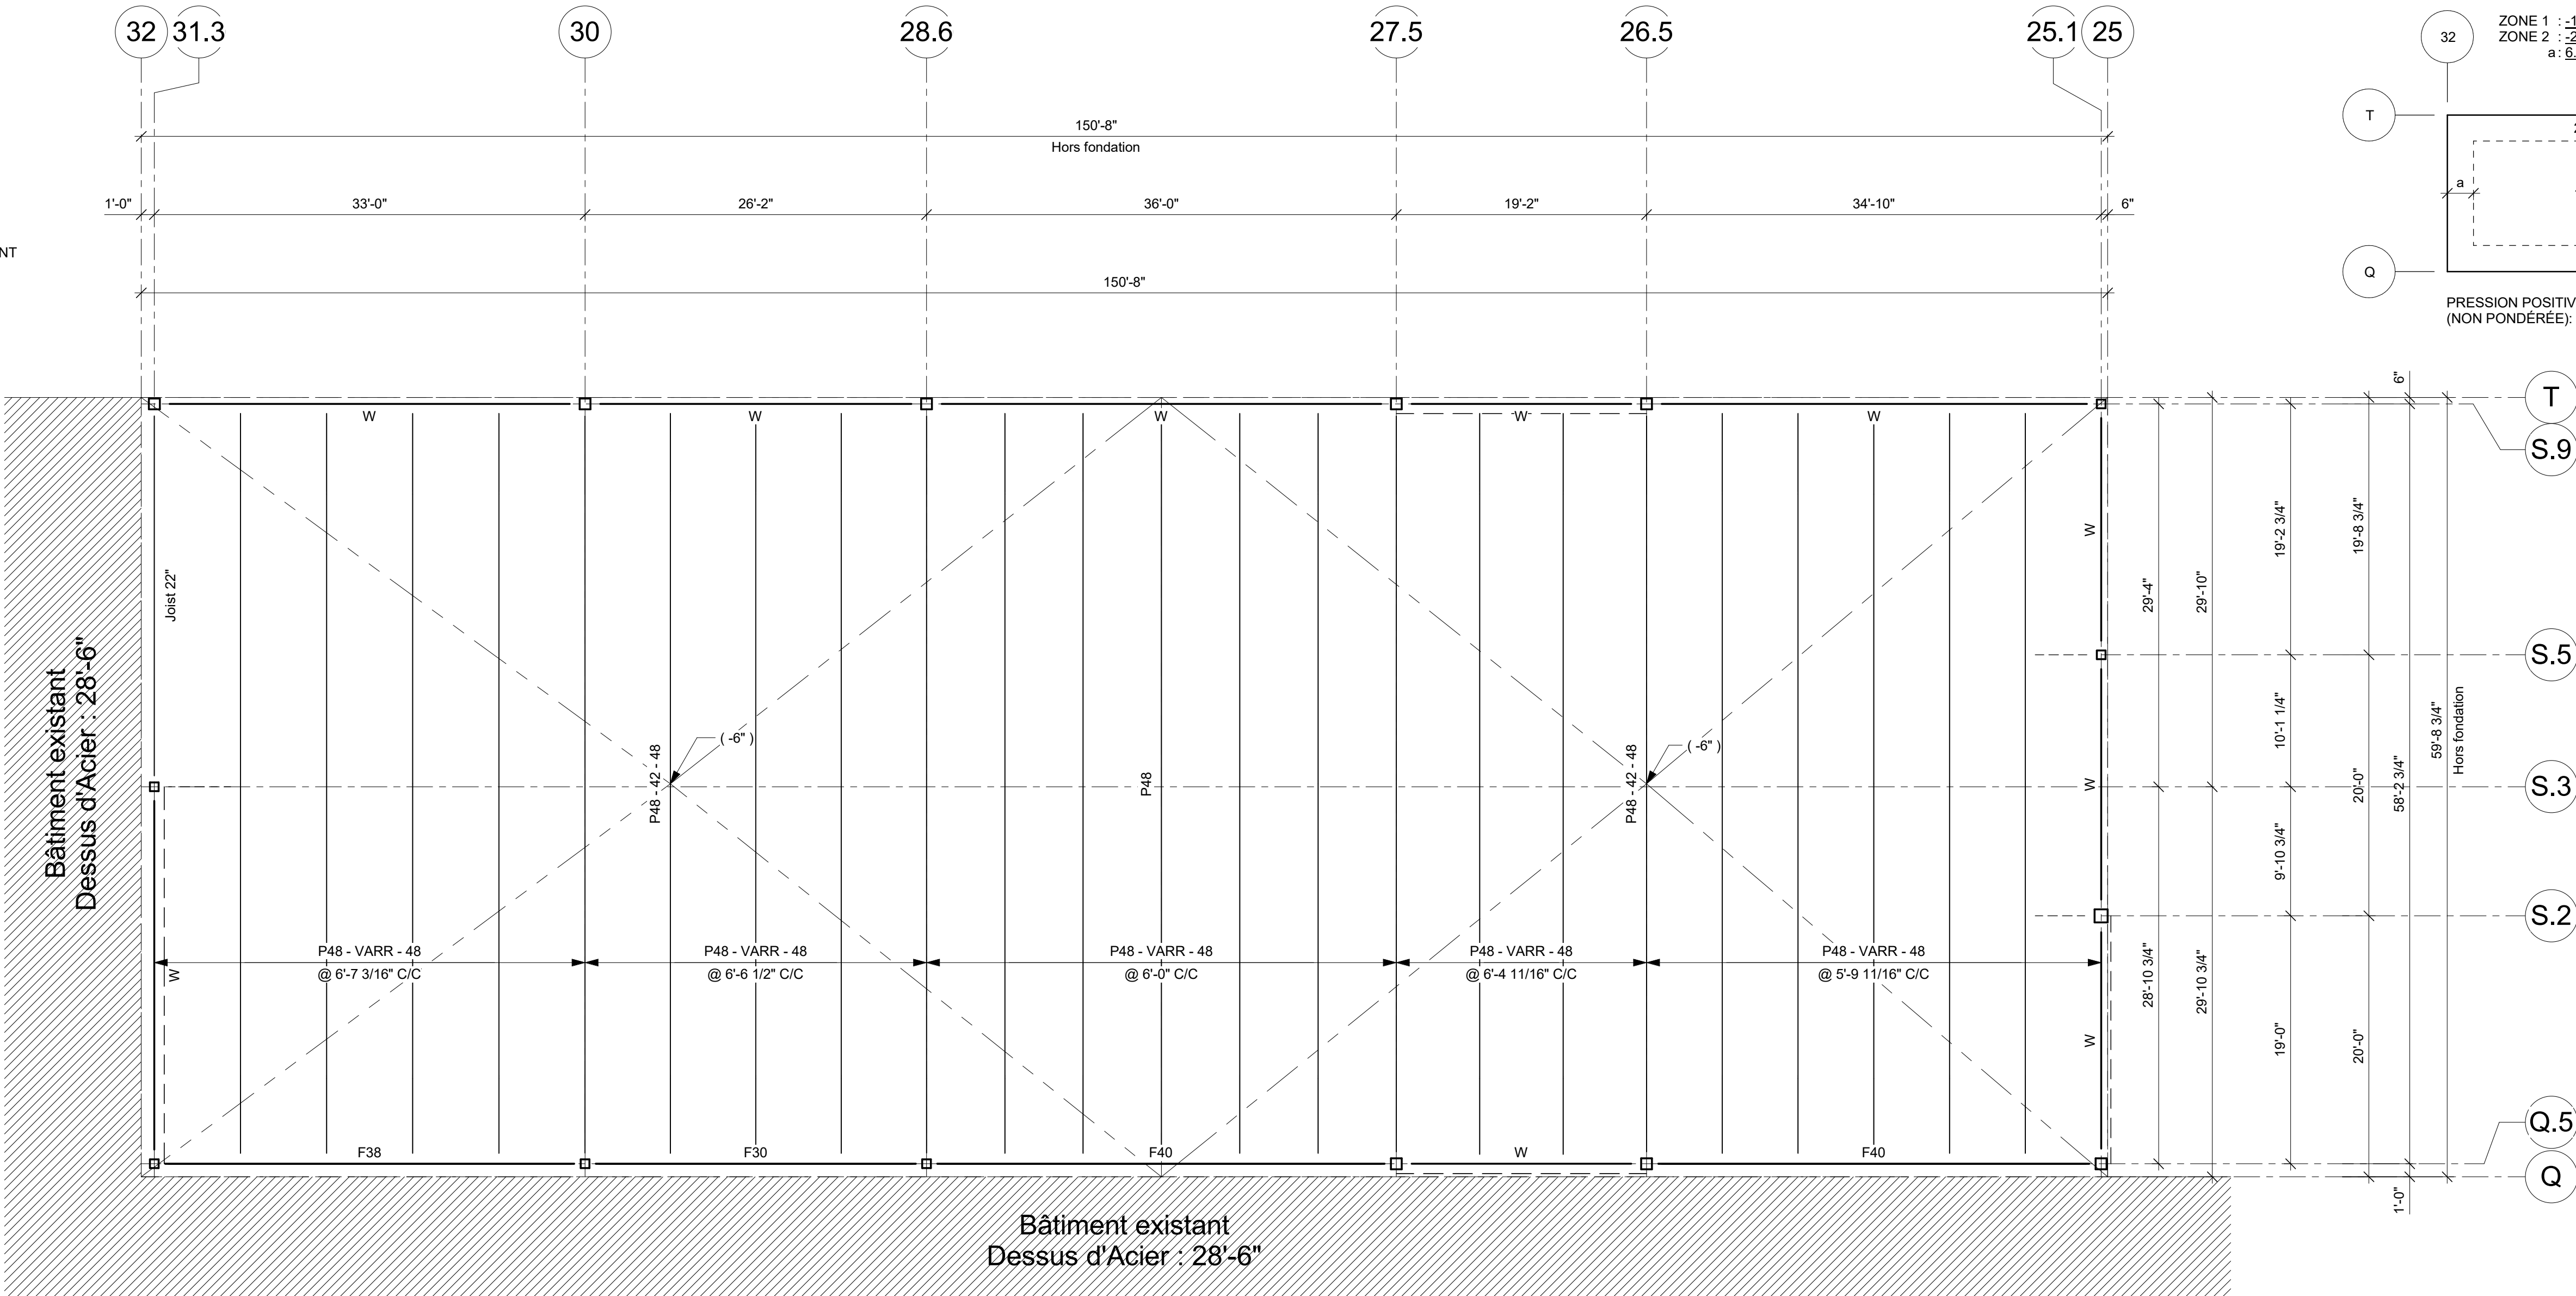

PLAN DE TOIT


1/8" = 1'-0"

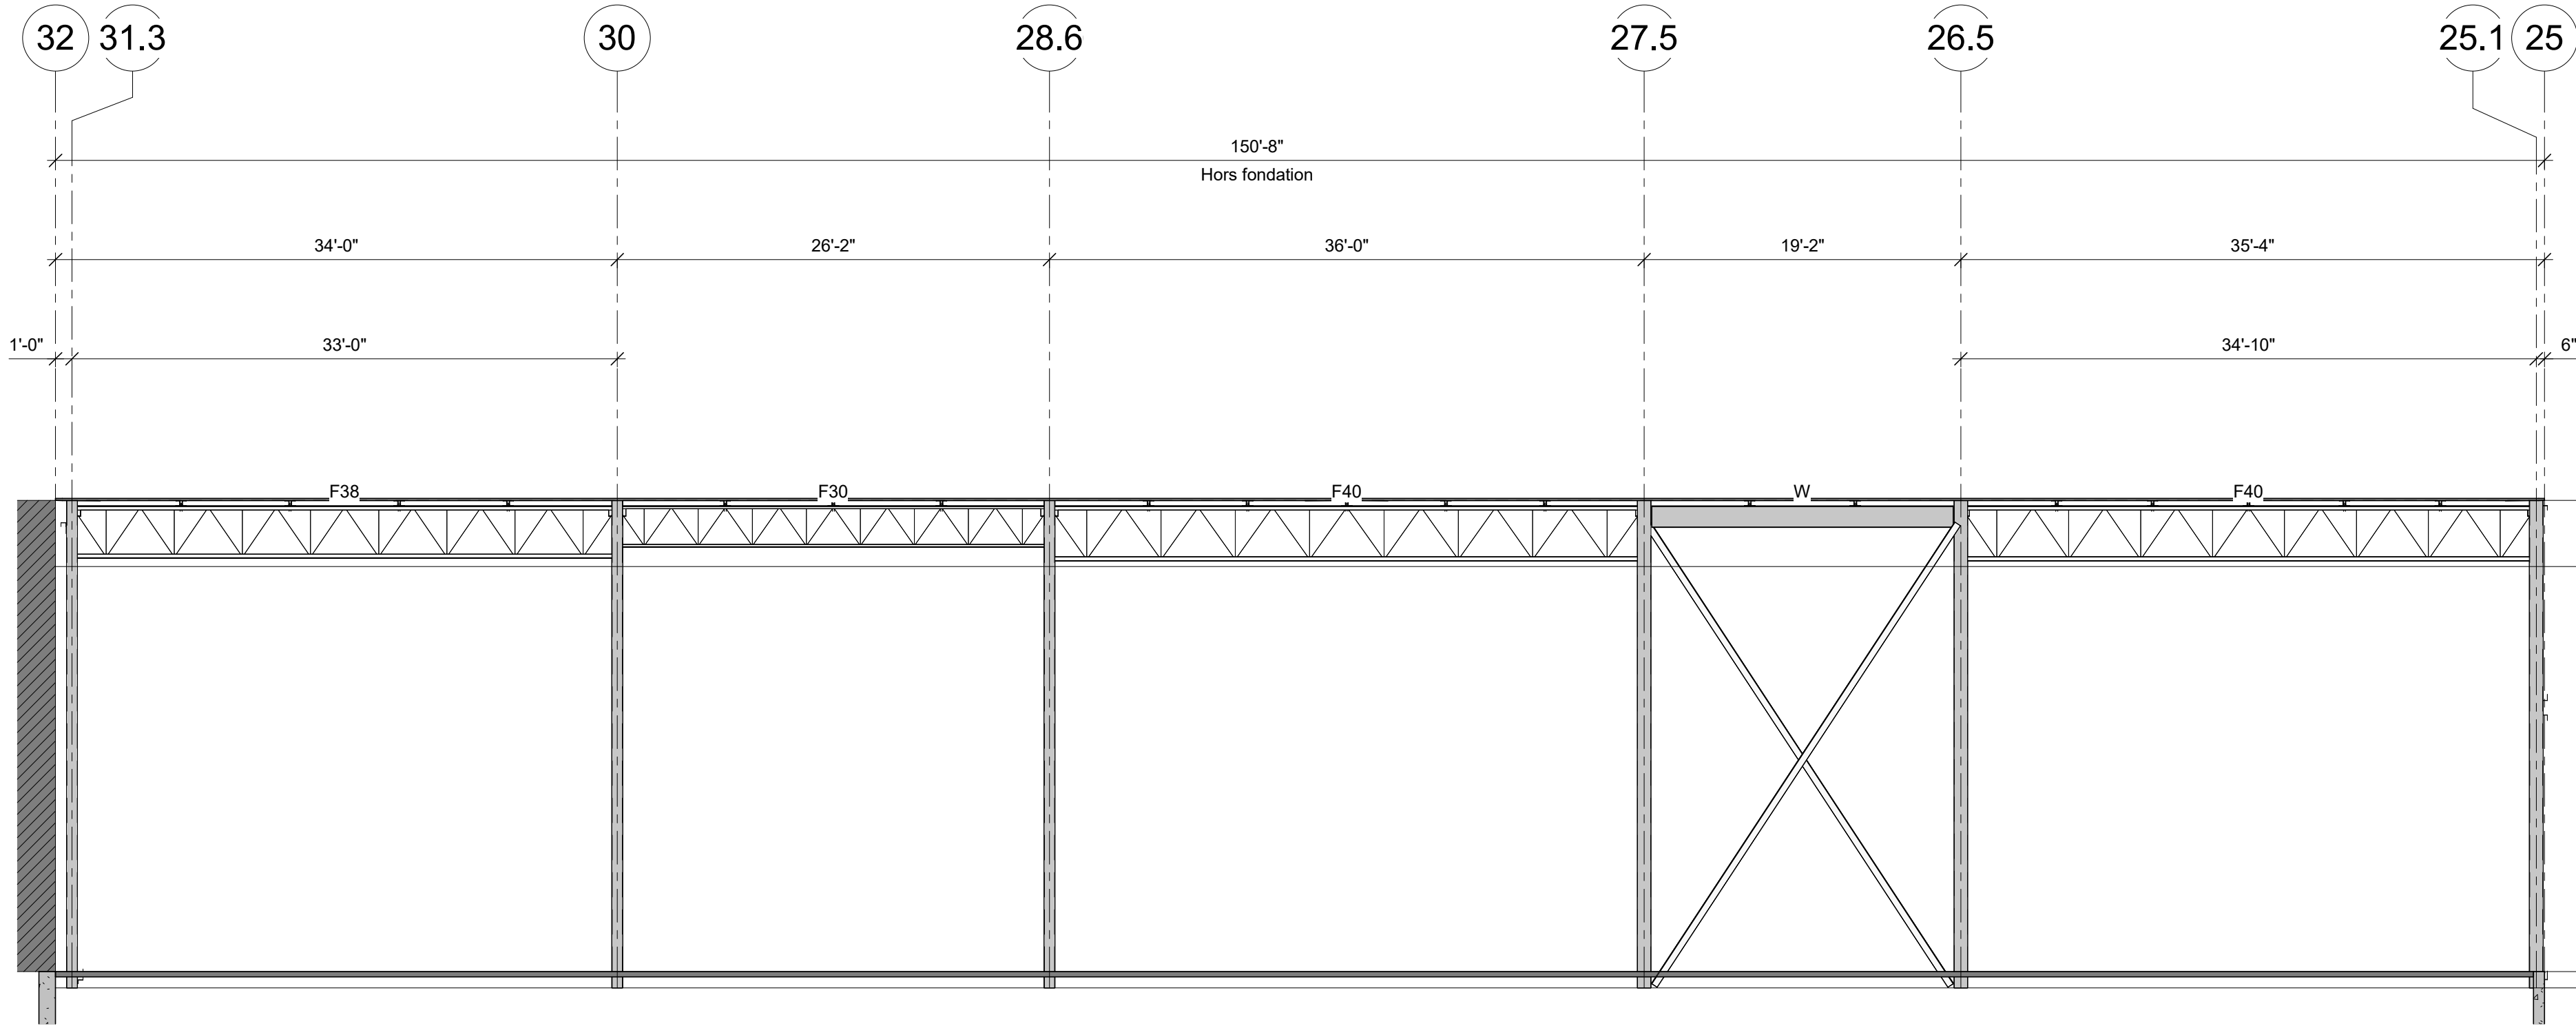

ELEVATION AXE Q.5 (SUD)

1/8" = 1'-0"

DIAGRAMME DE SOULÈVEMENT BRUT (NON PONDÉRÉ)

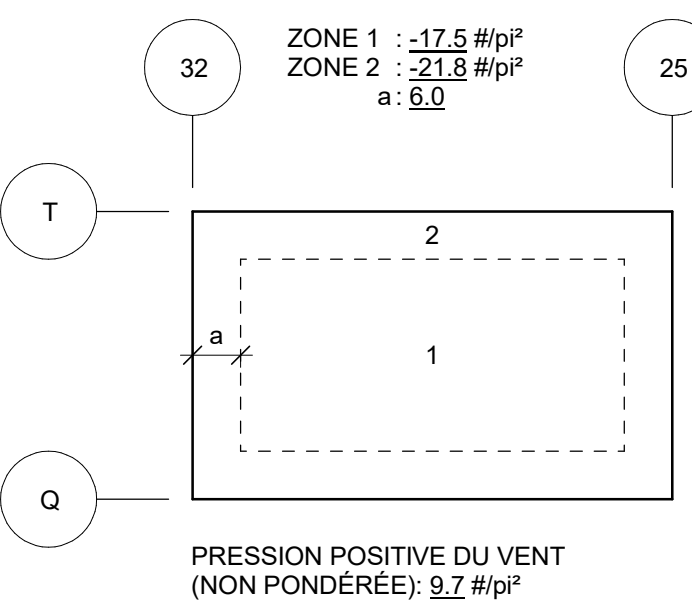

PRESSION POSITIVE DU VENT
(NON PONDÉRÉE): 9.7 #/pi²

S.9

S.5

S.3

S.2

Q.5

Q

CHARGES :

- Charge morte au toit (excluant charge collatérale): 28 lbs/pi²
- Charge collatérale : 4 lbs/pi² (incluant éclairage et/ou mécanique et gicleurs plus petits que 4" de diamètre)
- Charge de neige au toit : 57.1 lbs/pi²
- Charge vive au toit : 0 lbs/pi²
- Charge de vent q 1/50 : 8.77 lbs/pi²
- Charge de neige au sol : S_s = 0.8 lbs/pi²
- Catégorie de risque : normal
- Coefficient de surcharge de neige : C_b = 0.8

- Code Applicable : Code National du Bâtiment du Canada
- Code du bâtiment du Québec, dernières éditions adoptées
- Code de Pratique Standard ICCA.

- Type de sol assumé : classe D

- NOTE : 1. Si toutefois la catégorie d'emplacement devient E ou F selon le rapport géotechnique, le concept structural préliminaire (localisation et géométrie des contreventements, etc.) devra être validé et coordonné par l'ingénieur de Canam.

NOTE POUR LE CONTRACTEUR/ÉRECTEUR:

IL EST STRICTEMENT DÉFENDU DE MODIFIER, COPIER, REPRODUIRE OU DE DISTRIBUER CES DESSINS OU QUELQUES REPRÉSENTATIONS DE CES DESSINS, PAR TOUTES SOURCES DE MÉDIA INCLUANT ÉLECTRONIQUEMENT, SANS L'APPROBATION ÉCRITE DE GROUPE CANAM INC.

TOIT

DESSUS DE PILASTRE DDP : -2'-0"
DESSUS DE PILASTRE : -1'-0"
DESSUS DE LA DALLE : 0'-0"
DESSUS DE LA FONDATION : 0'-0"
HAUTEUR LIBRE : 24'-6"
DESSUS D'ACIER : 28'-6"

CHARGES

C.M. : 28.0 lbs/pi²
Coll. : 4.0 lbs/pi²
Ss : 54.3 lbs/pi²
Sr : 8.36 lbs/pi²
C_b x C_w : 0.90
C.V. au toit : 0 lbs/pi²
Is :
Charge de neige au toit : 57.1 lbs/pi²
I_w :
Vent q = 1/50 : 8.77 lbs/pi²

Seisme (Sol de classe D assumé)

I_e : 1.0
S_{as} (0.2) : 0.796
S_s (0.5) : 0.579
S_s (1.0) : 0.347
S_s (2.0) : 0.165
S_s (5.0) : 0.046
S_s (10.0) : 0.014
PGA : 0.480
PGV : 0.413

PRÉLIMINAIRE

NE DOIT PAS SERVIR À LA
CONSTRUCTION

1	2026/01/12	R1	J.P.	
REVISION	DATE	DESCRIPTION	DRAWN	CHECKED
GERANT DE PROJET				
		-		
		-		
		-		
		-		
		-		

DESSIN:			
DESSINE PAR	CONÇU PAR	INGÉNIEUR DU PROJET	ECHELLE:
S.L.			COMME INDiqué
VÉRIFIÉ PAR	INGÉNIEURS CONSEILS / ARCHITECTES		DATE:
			2025-12-12

CLIENT: 9307-9952 Québec Inc



11505, 1^{re} Avenue, bureau 500, Saint-Georges Beauce
Québec, Canada, G5Y 7X3
Téléphone: (418) 228-8031
Télécopieur: (418) 228-4489

SCEAU PROFESSIONNEL

PROJET

Agrandissement Phase 2 Annexe
LAVAL, QUÉBEC

TITRE

CROQUIS PRÉLIMINAIRE - PLAN DE
TOIT ET ELEVATION

NUMÉRO CONTRAT P2025-196	NUMÉRO DESSIN 3 de 4	DIVISION	REVISION 1
-----------------------------	-------------------------	----------	---------------