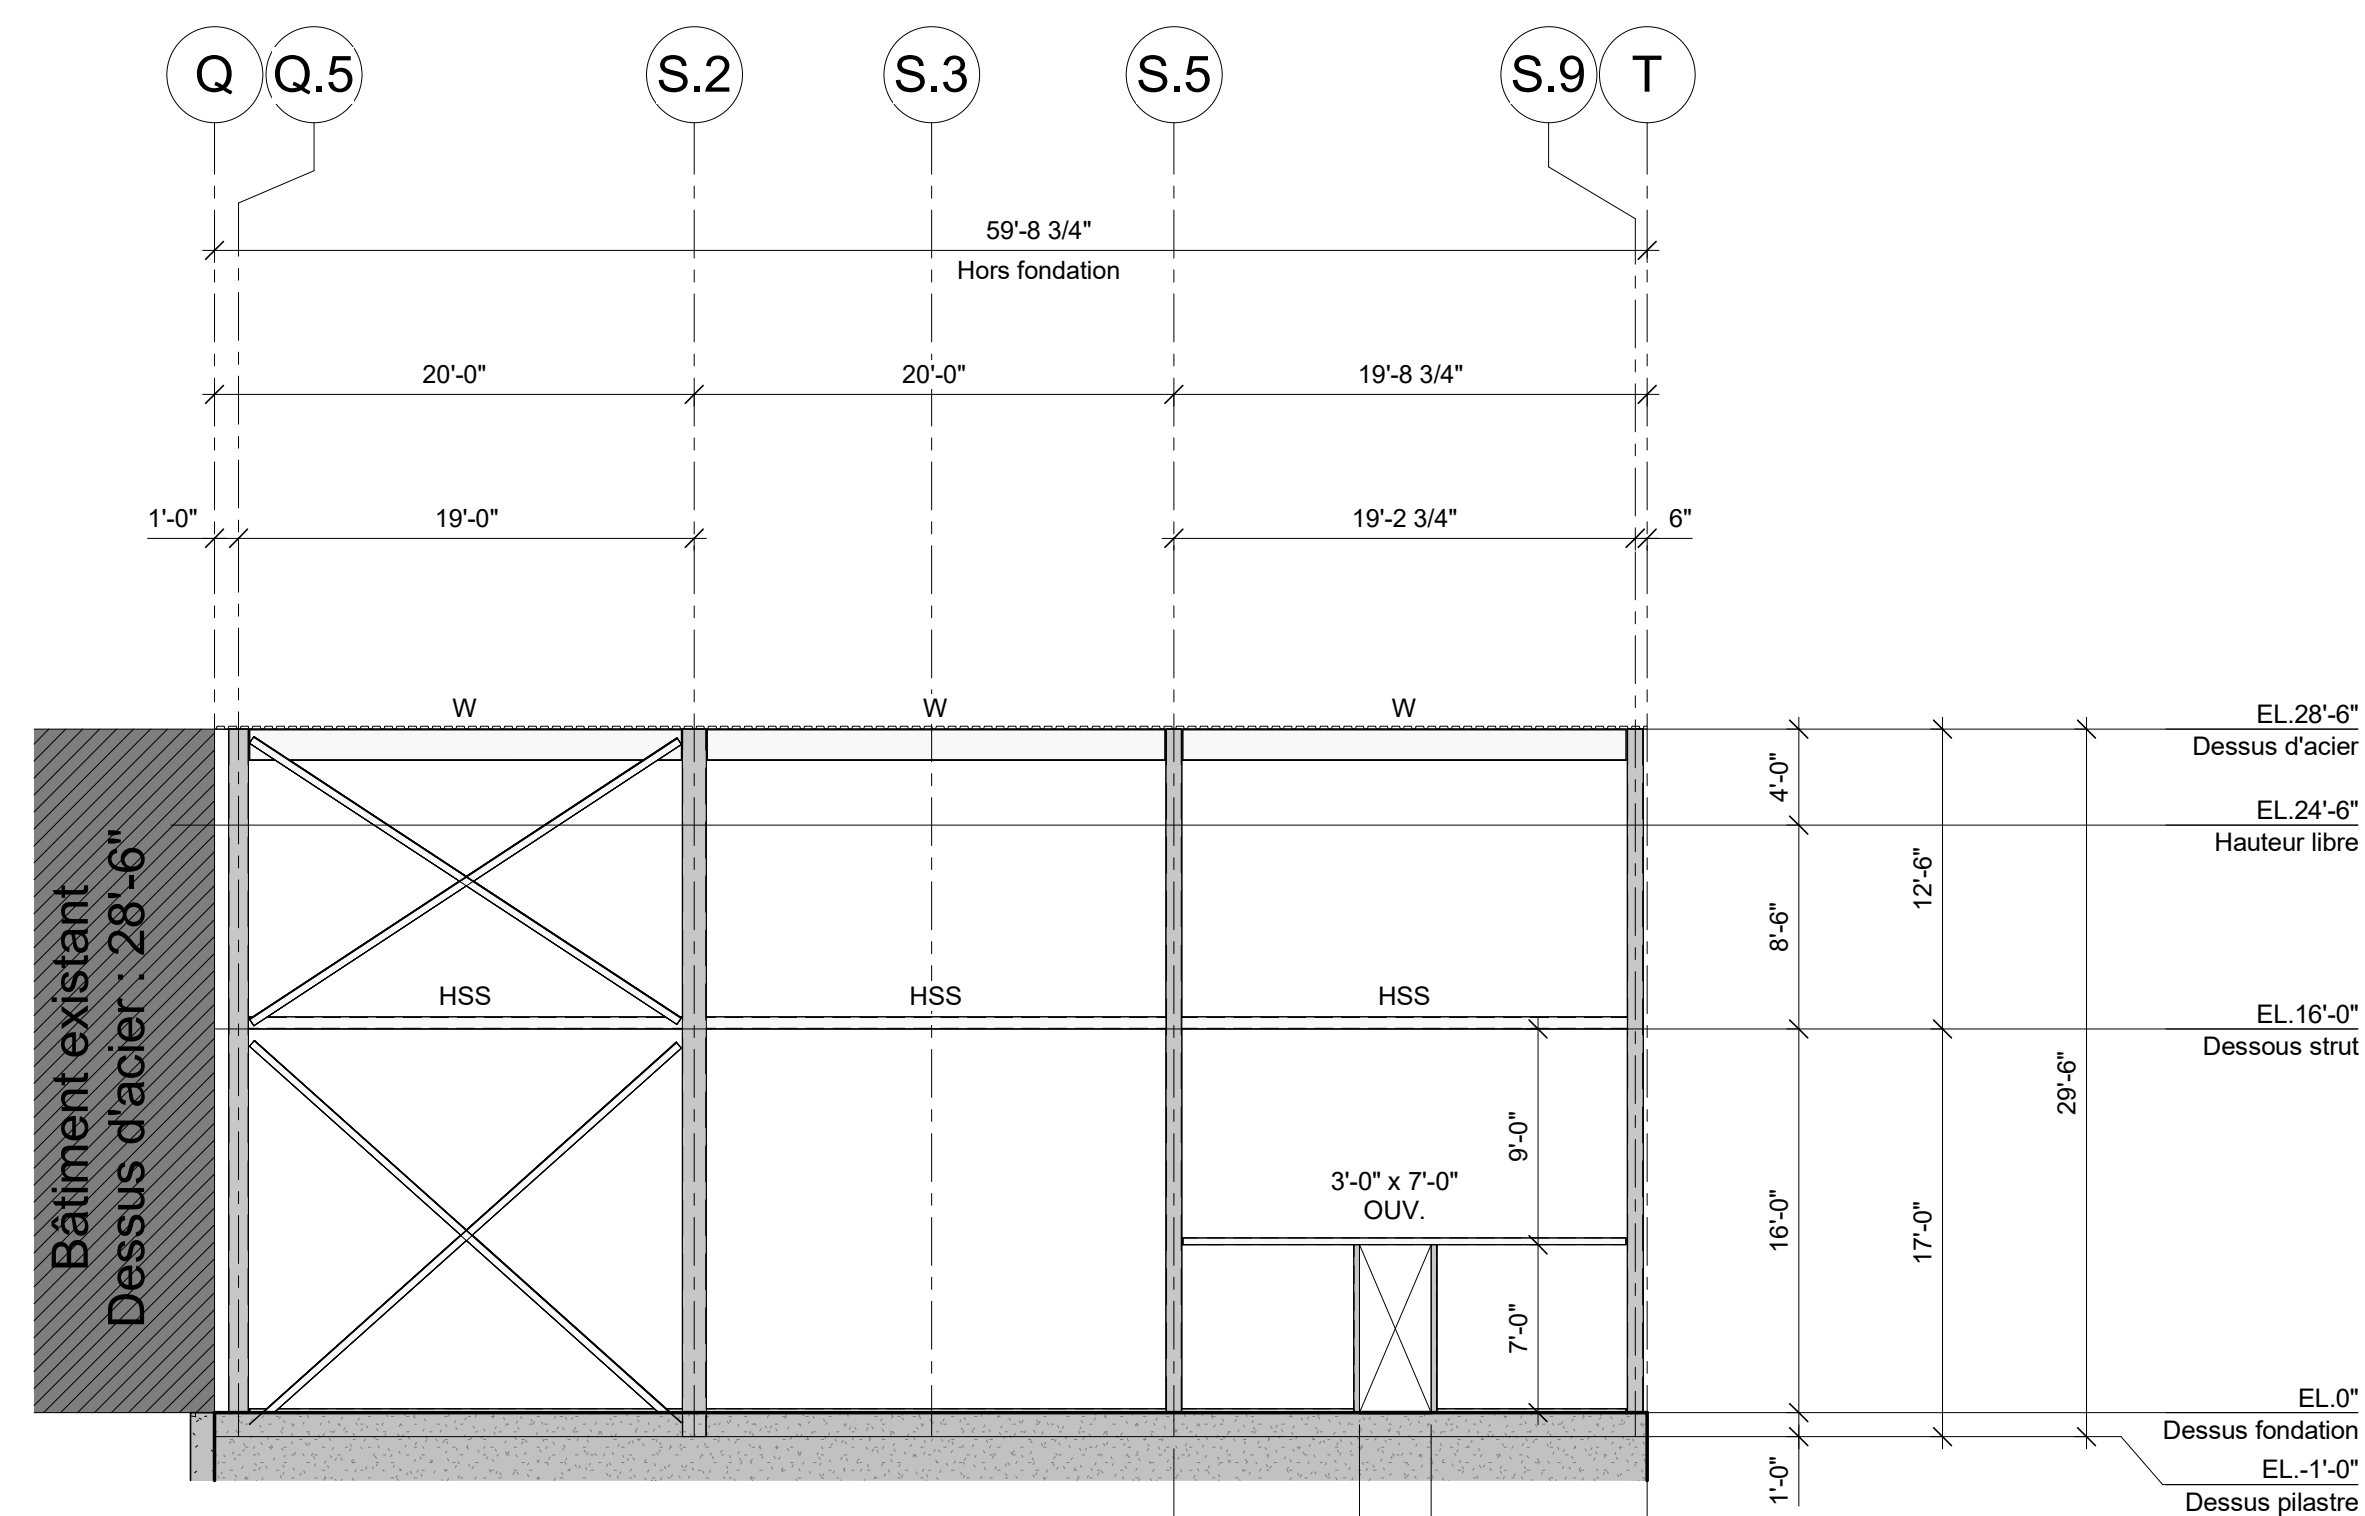
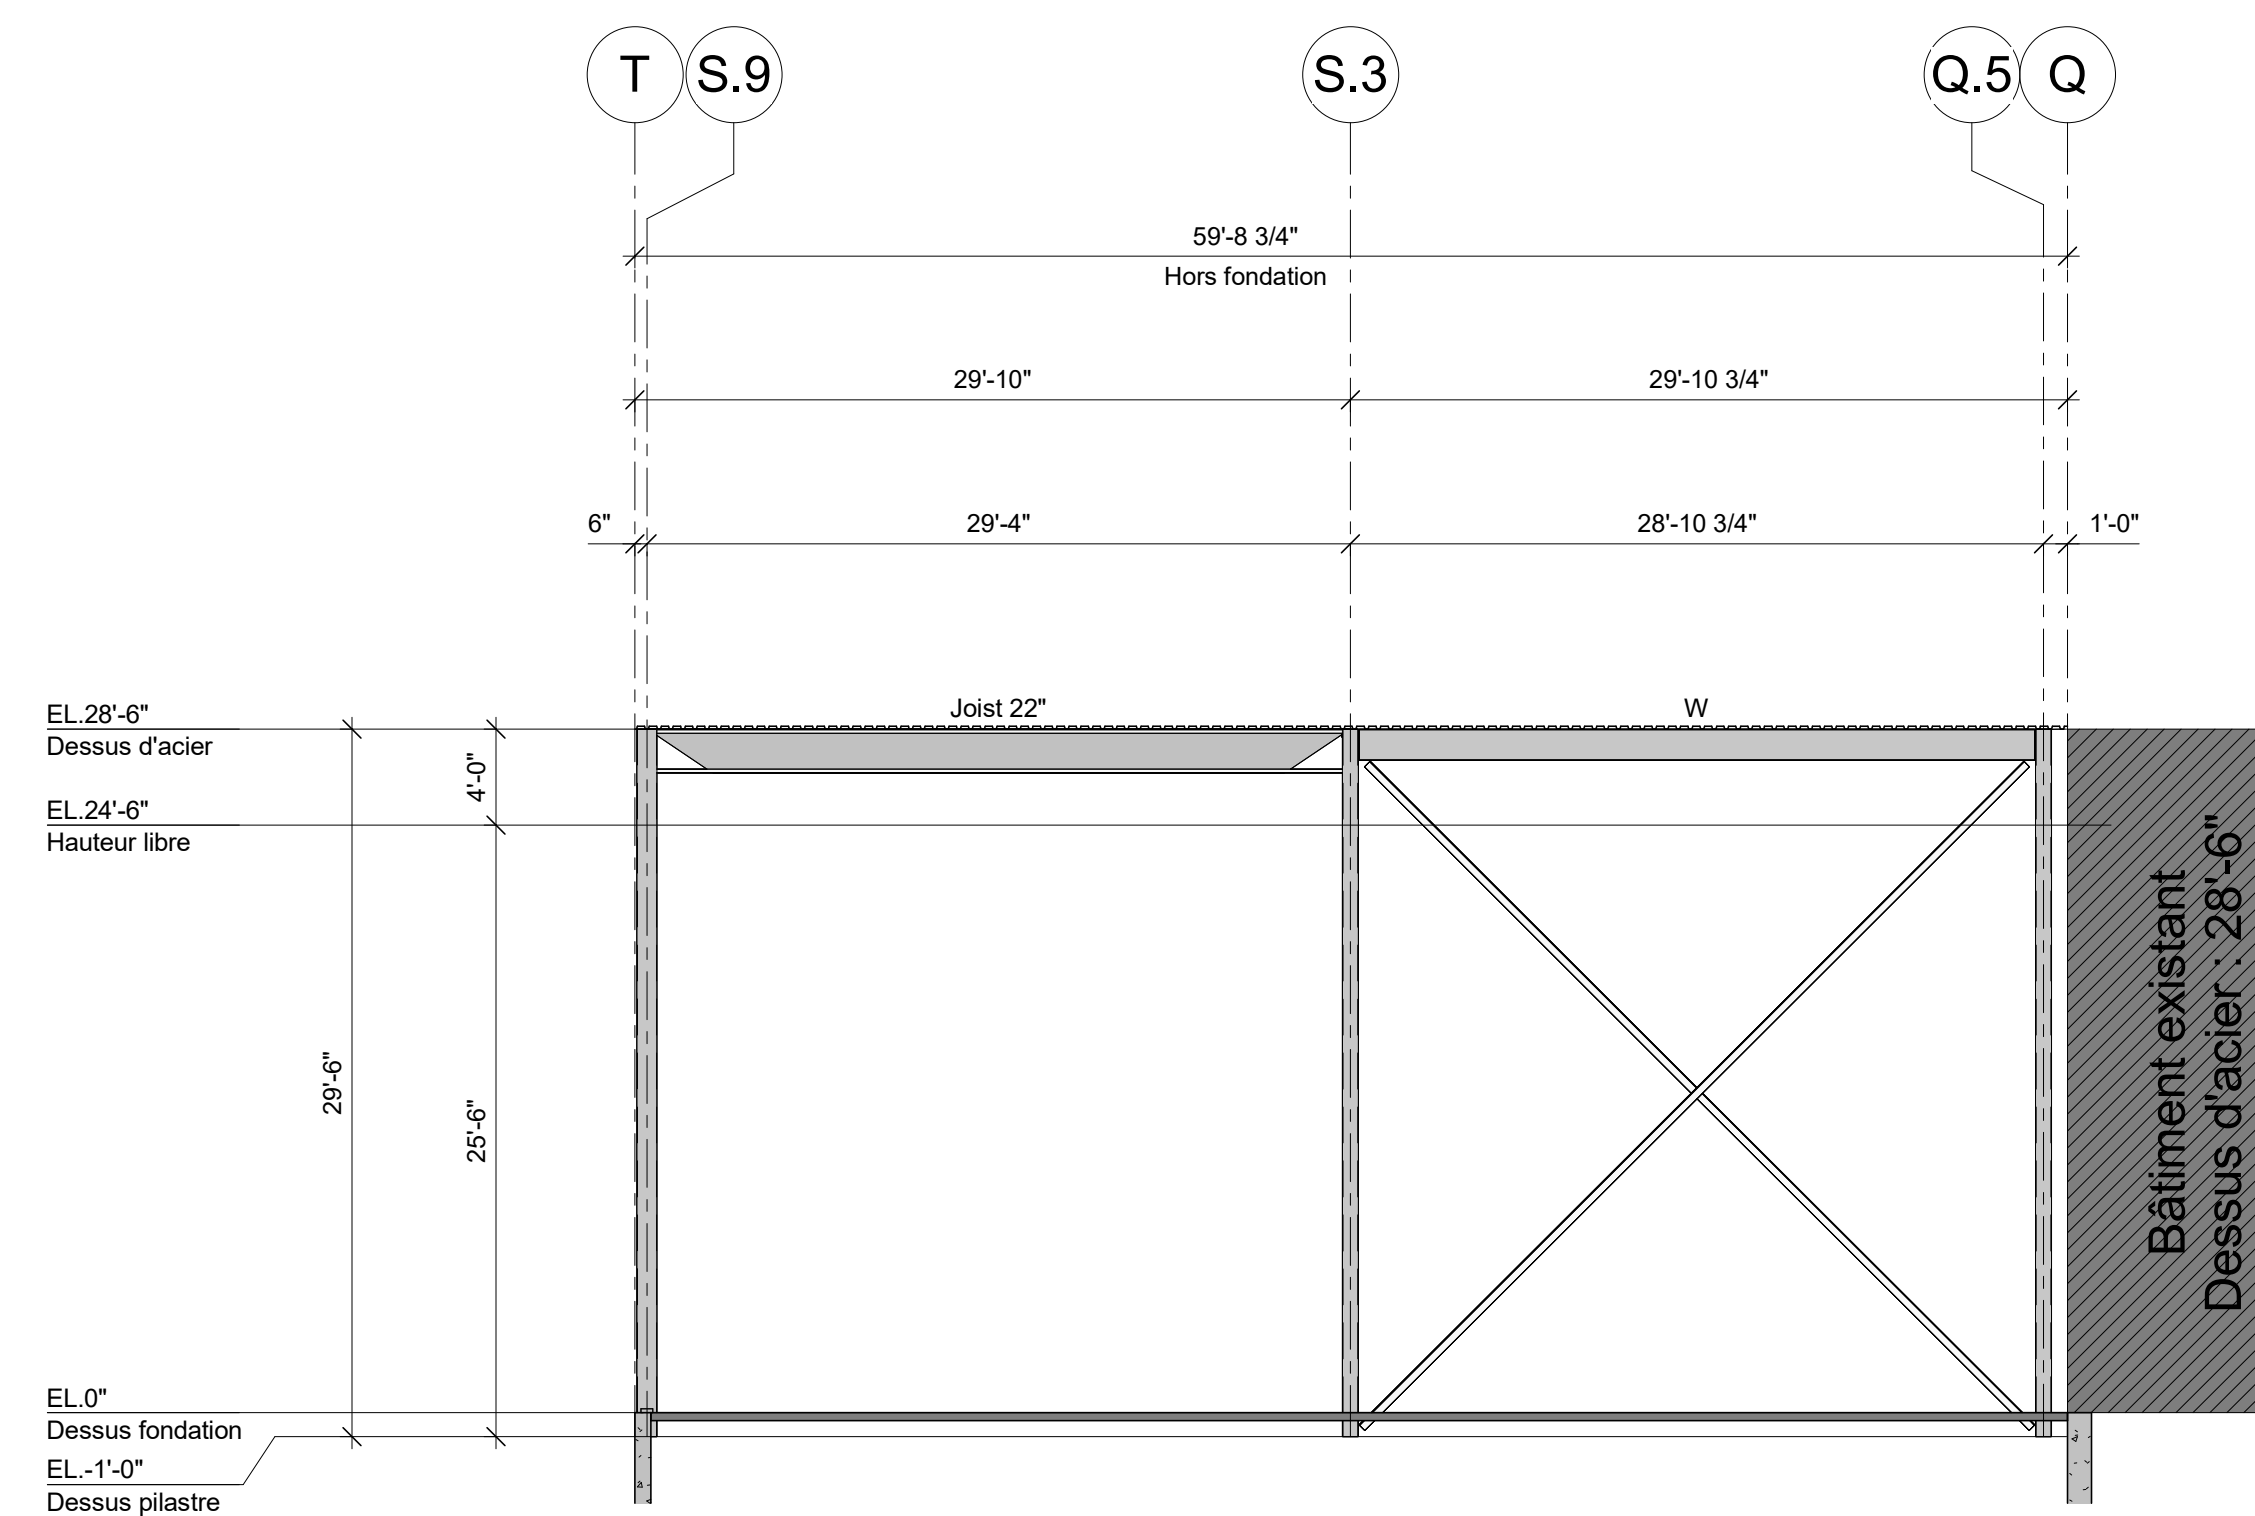
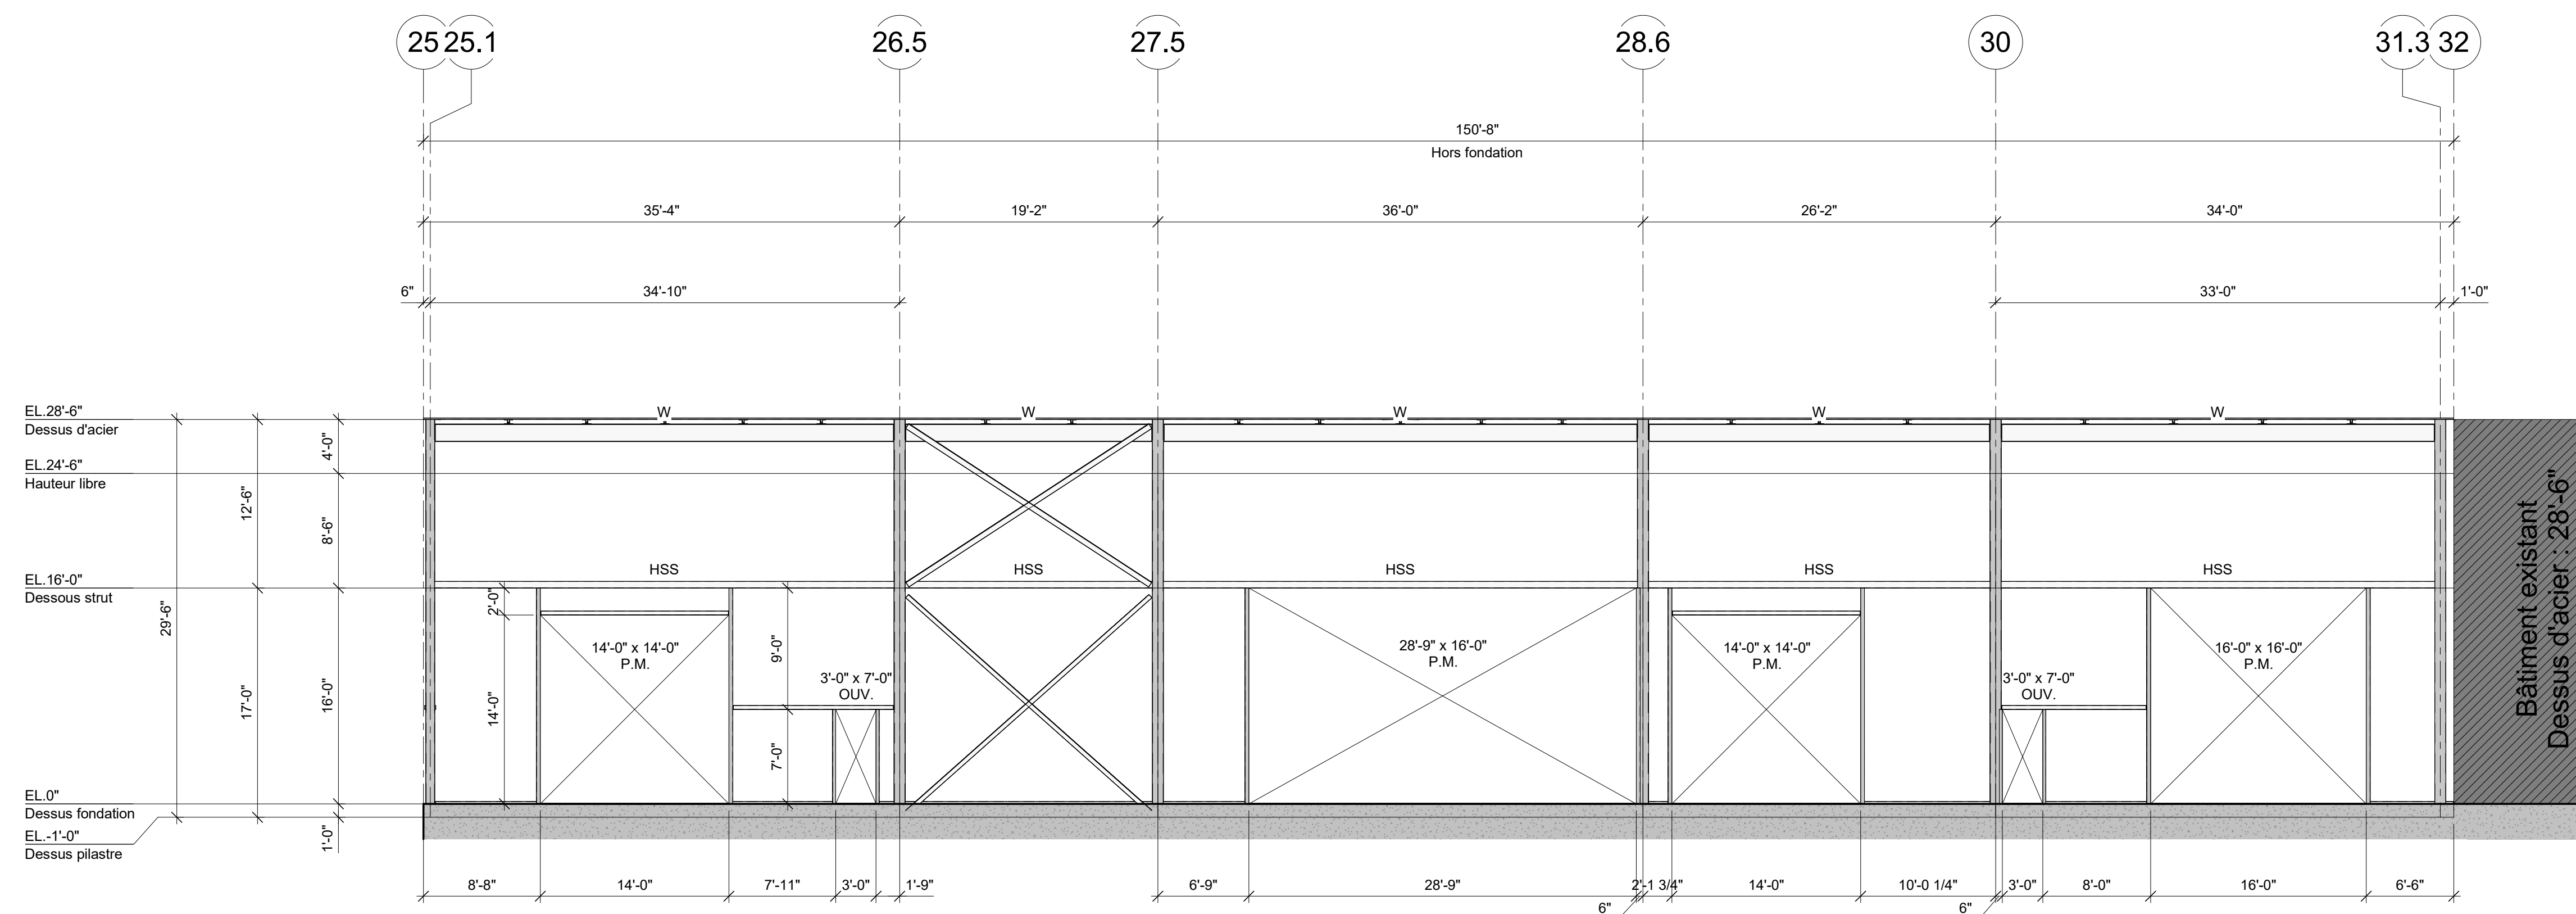


ELEVATION AXE 25 (EST)
$$1/8'' = 1'-0''$$


ELEVATION AXE 31.3 (OUEST)

$$1/8'' = 1'-0''$$


ELEVATION AXE T (NORD)

$1/8'' = 1'-0''$

NOTE POUR LE CONTRACTEUR/ÉRECTEUR:

IL EST STRICTEMENT DÉFENDU DE MODIFIER, COPIER, REPRODUIRE
OU DE DISTRIBUER CES DESSINS OU QUELQUES REPRÉSENTATIONS
DE CES DESSINS, PAR TOUTES SOURCES DE MÉDIA INCLUANT
ÉLECTRONIQUEMENT, SANS L'APPROBATION ÉCRITE DE GROUPE
CANAM INC.

PRÉLIMINAIRE

NE DOIT PAS SERVIR À LA
CONSTRUCTION

1	2026/01/12	R1	J.P.	
REVISION	DATE	DESCRIPTION	DRAWN	CHECKED

GÉRANT DE PROJET	-
	-
	-
	-
	-

DESSIN:

DESSINÉ PAR S.L.	CONÇU PAR	INGÉNIEUR DU PROJET	ÉCHELLE: COMME INDIQUÉ
VÉRIFIÉ PAR	INGÉNIEURS CONSEILS / ARCHITECTES		DATE: 2025-12-12

CLIENT: 9307-9952 Québec Inc



11505, 1^{re} Avenue, bureau 500, Saint-Georges Beauce
Québec, Canada, G5Y 7X3
Téléphone: (418) 228-8031
Télécopieur: (418) 226-4489

SCEAU PROFESSIONNEL

PROJET	
--------	--

Agrandissement Phase 2 Annexe
LAVAL, QUÉBEC

TITRE	
-------	--

CROQUIS PRÉLIMINAIRE - ÉLÉVATIONS

NUMÉRO CONTRAT P2025-196	NUMÉRO DESSIN	DIVISION	RÉVISION A
-----------------------------	---------------	----------	---------------