



NORD POUR ÉRECTION SEULEMENT

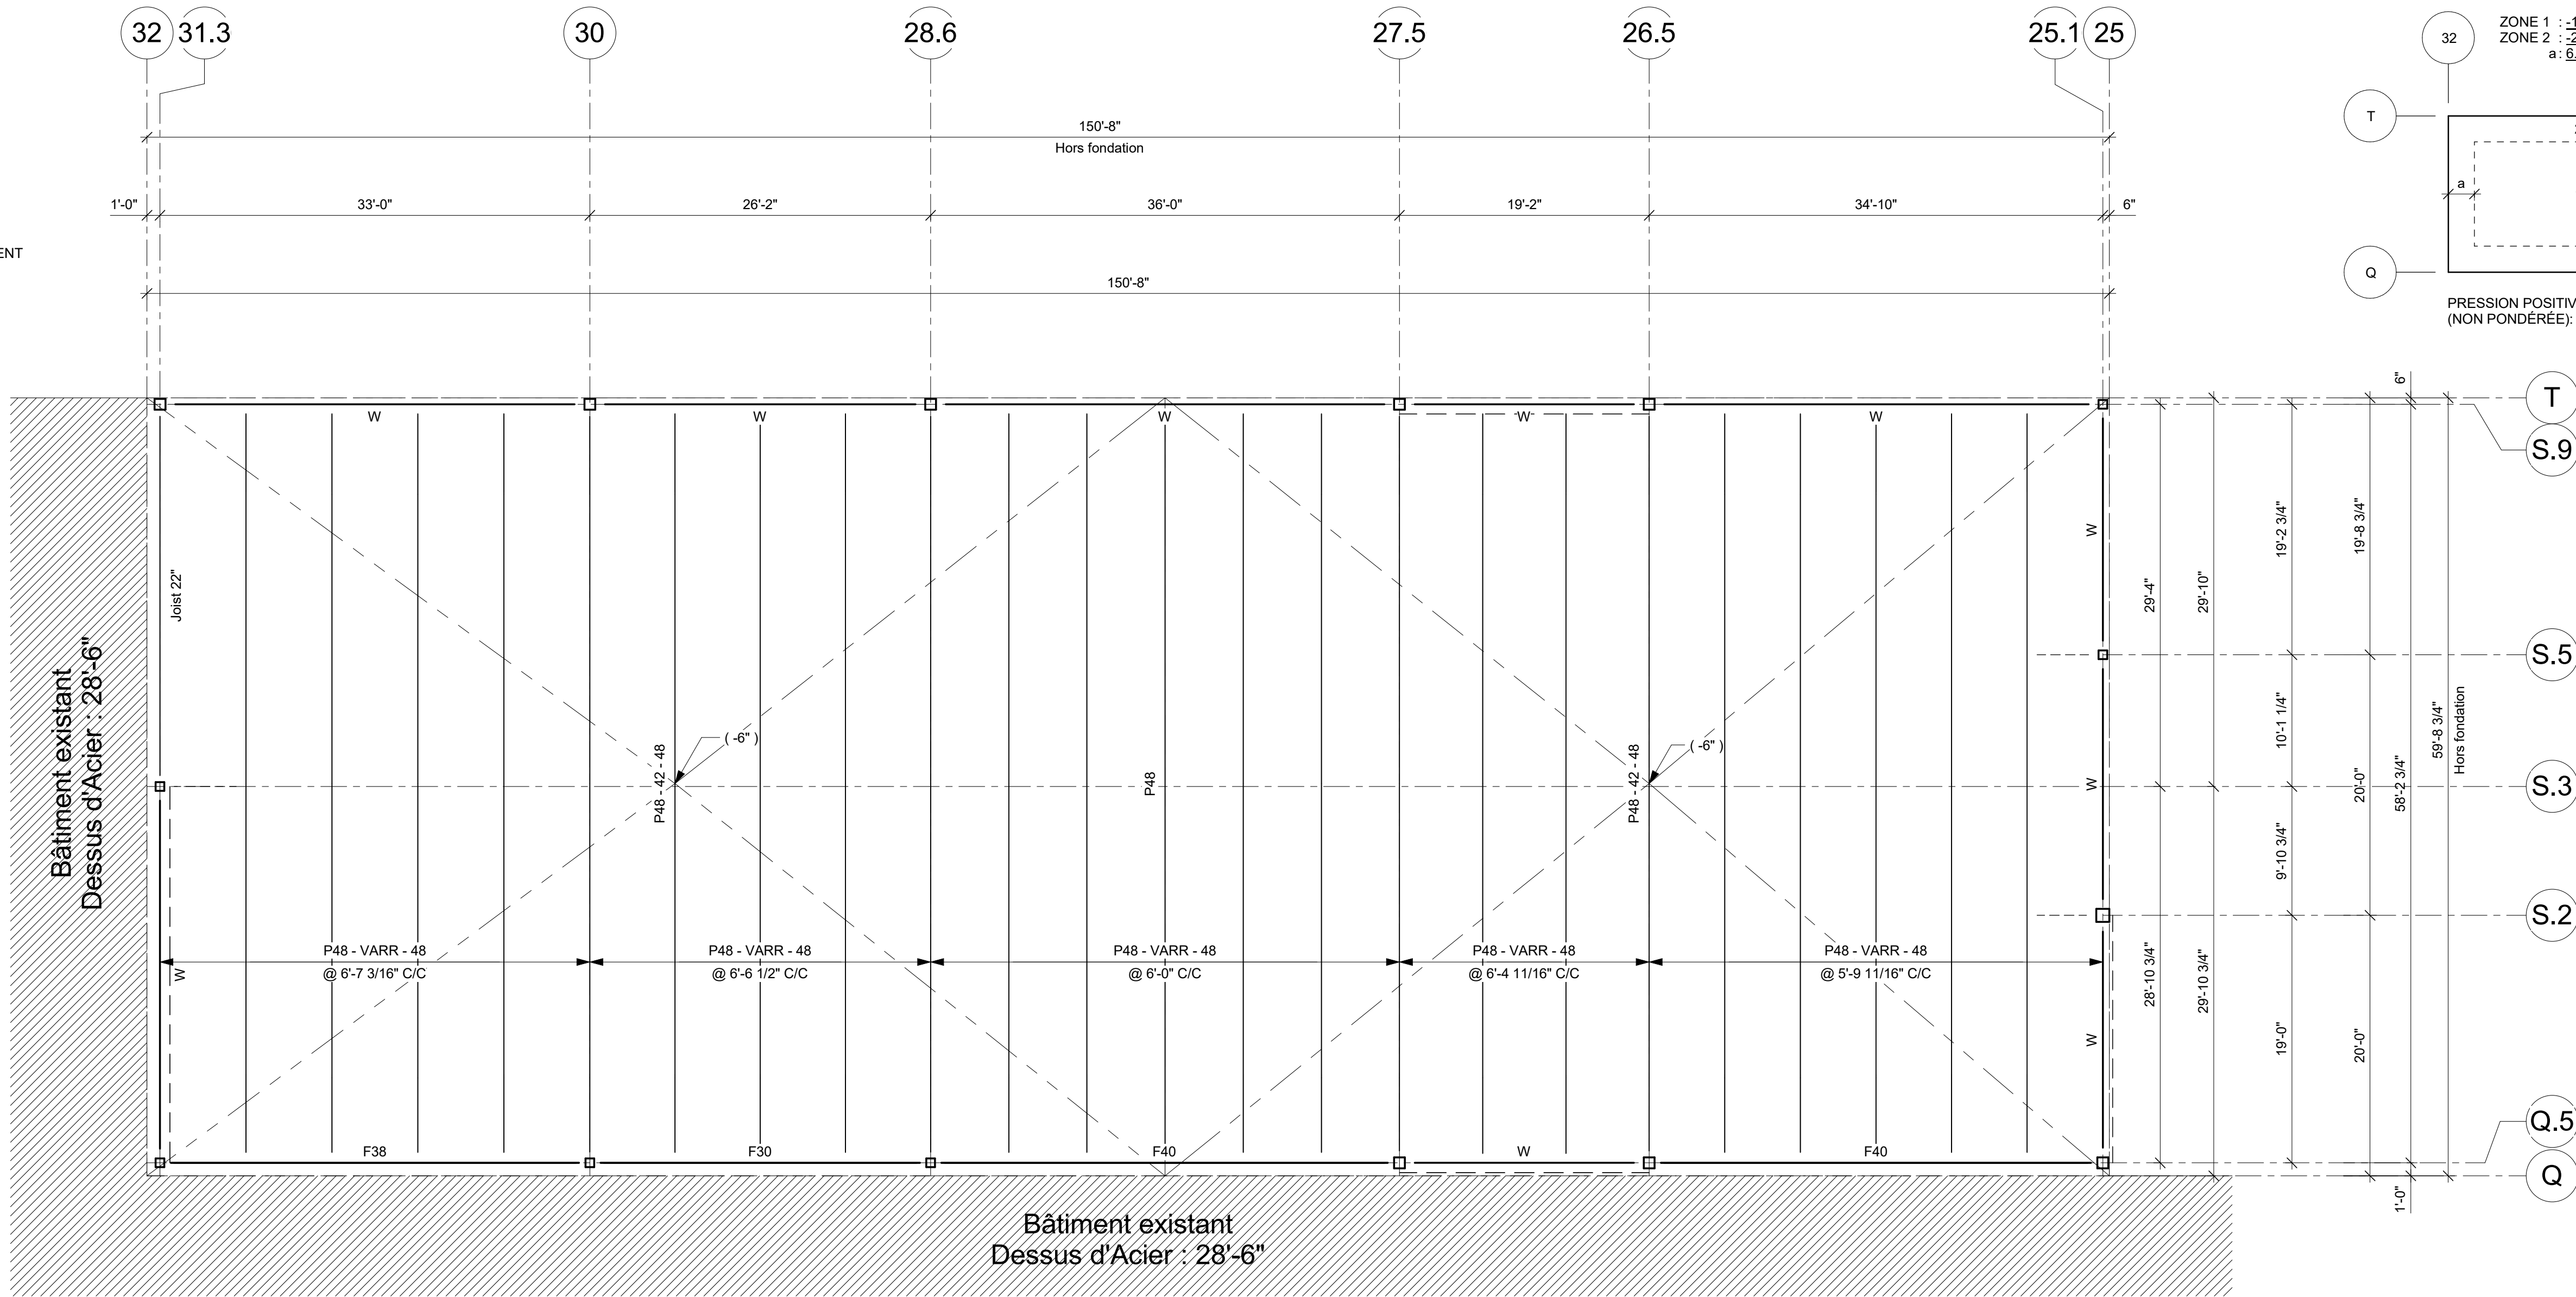

PLAN DE TOIT

1/8" = 1'-0"

DIAGRAMME DE SOULÈVEMENT BRUT (NON PONDÉRÉ)

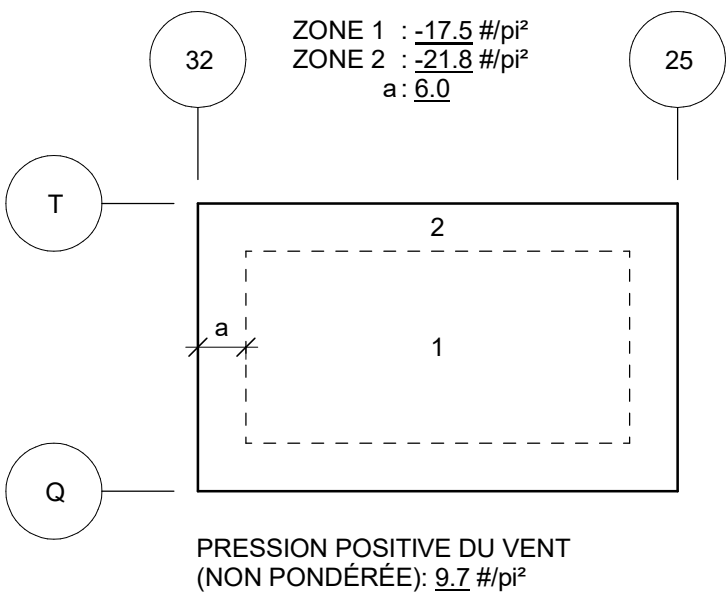


CHARGES :

- Charge morte au toit (excluant charge collatérale): 28 lbs/pi²
- Charge collatérale : 4 lbs/pi² (incluant éclairage et/ou mécanique et gicleurs plus petits que 4" de diamètre)
- Charge de neige au toit : 57.1 lbs/pi²
- Charge vive au toit : 0 lbs/pi²
- Charge de vent q 1/50 : 8.77 lbs/pi²
- Charge de neige au sol : S_s = 0.8 lbs/pi²
- Catégorie de risque : normal
- Coefficient de surcharge de neige : C_b = 0.8
- Coefficient de surcharge de neige : C_w = 1.0

• Code Applicable : Code National du Bâtiment du Canada
Code du bâtiment du Québec, dernières éditions adoptées
Code de Pratique Standard ICCA.

• Type de sol assumé : classe D

• NOTE :
1. Si toutefois la catégorie d'emplacement devient E ou F selon le rapport géotechnique, le concept structural préliminaire (localisation et géométrie des contreventements, etc.) devra être validé et coordonné par l'ingénieur de Canam.

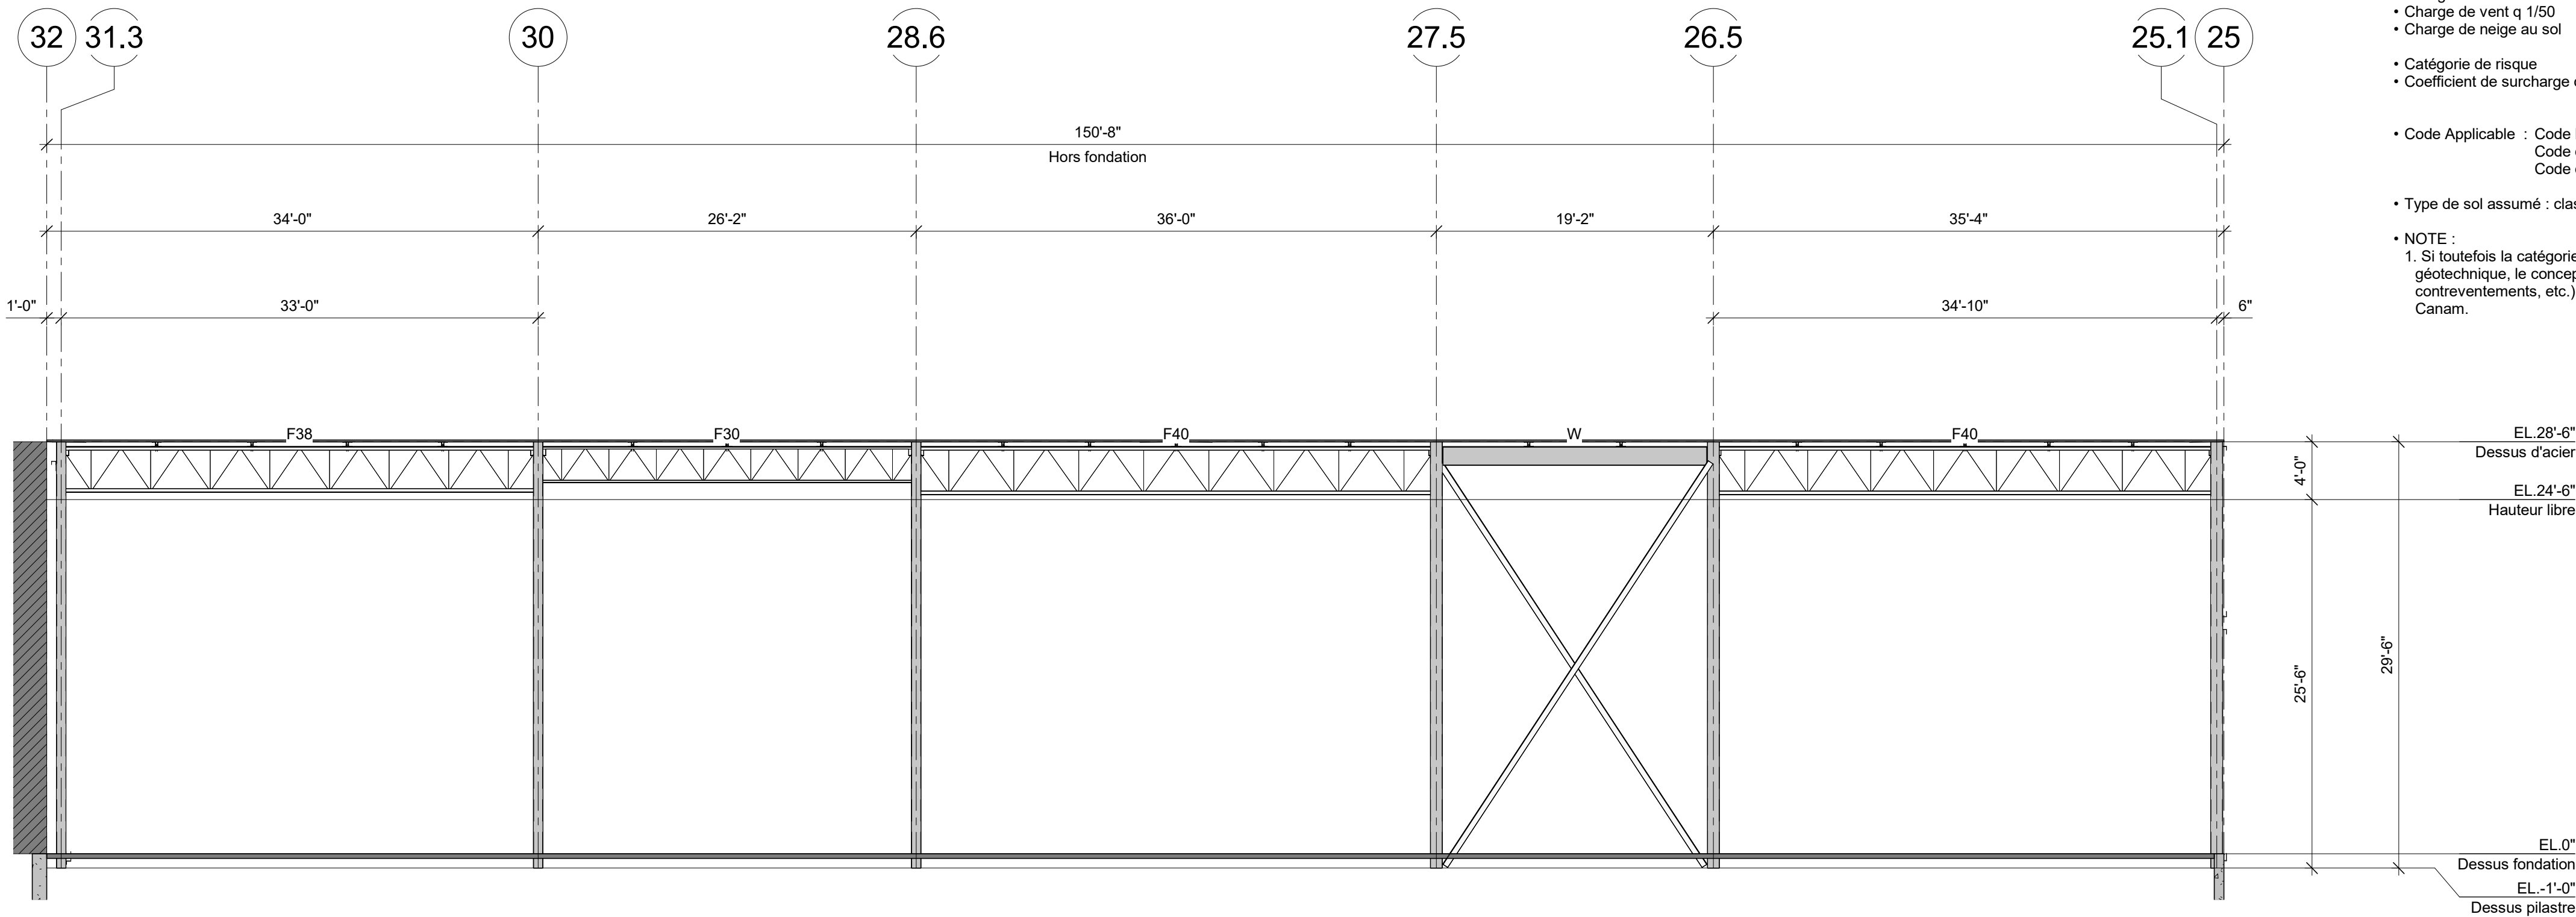

ELEVATION AXE Q.5 (SUD)

1/8" = 1'-0"

EL 28'-6"
Dessus d'acier
EL 24'-6"
Hauteur libre
EL 0"
Dessus fondation
EL -1'-0"
Dessus pilastre