

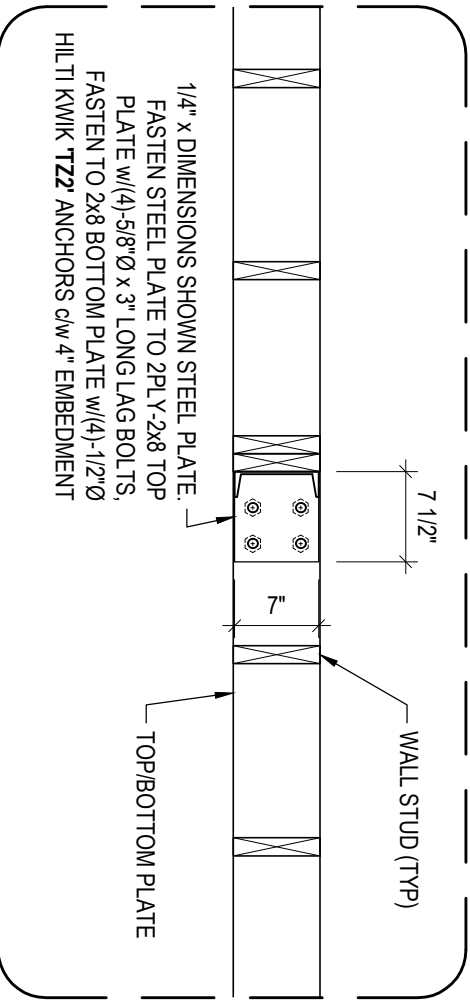
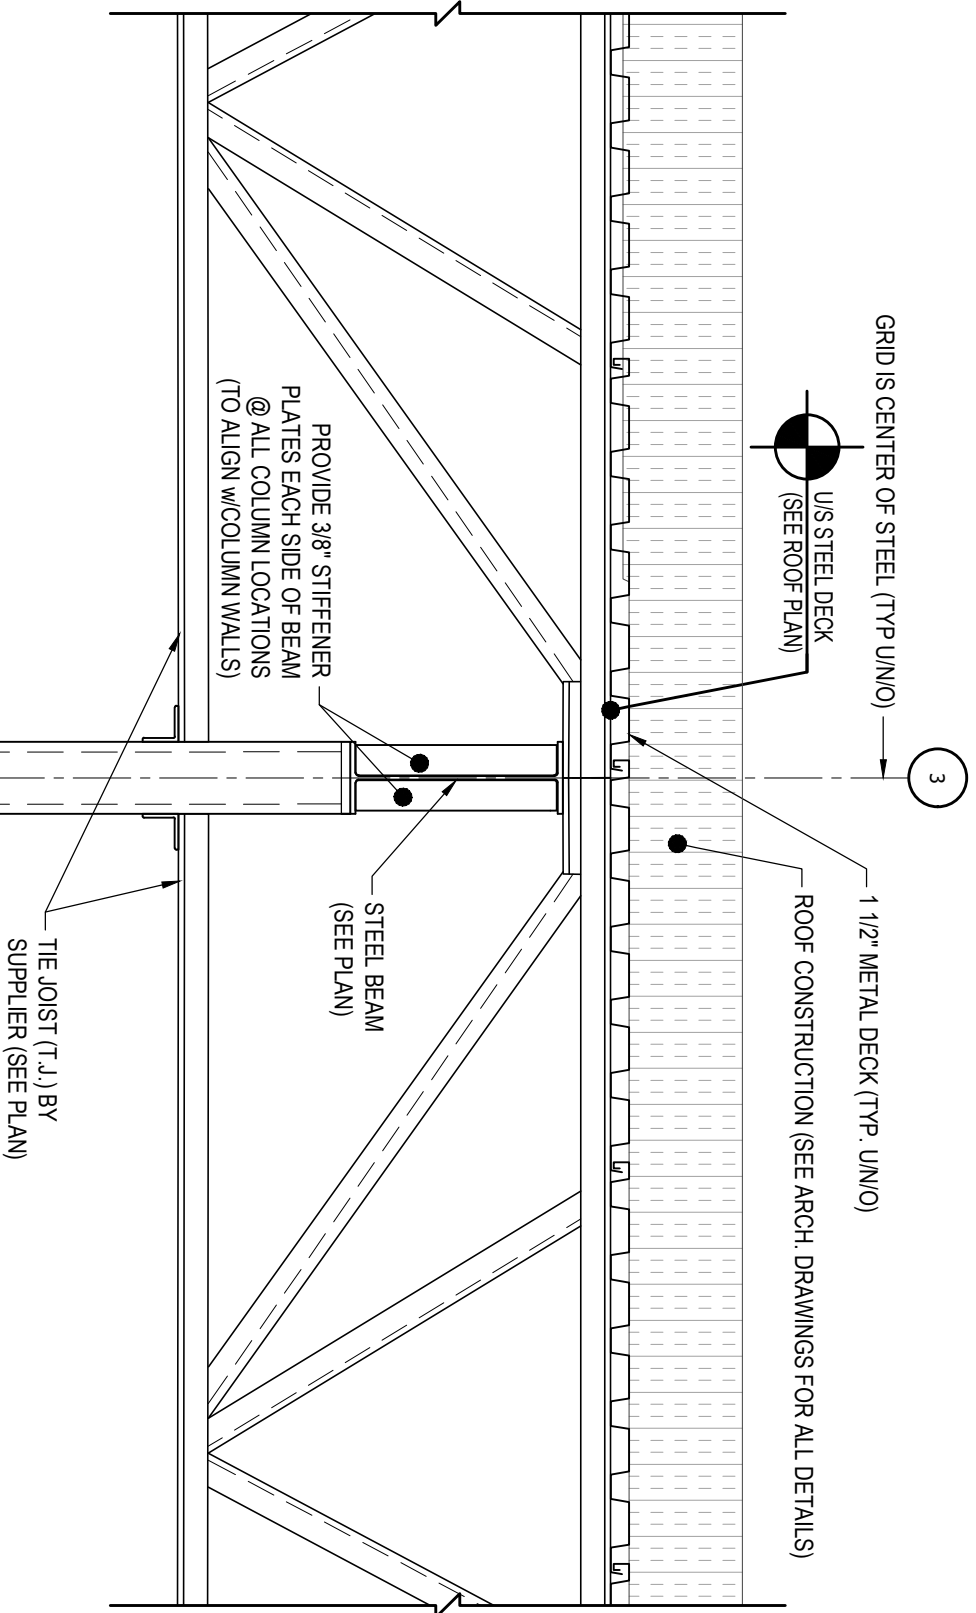


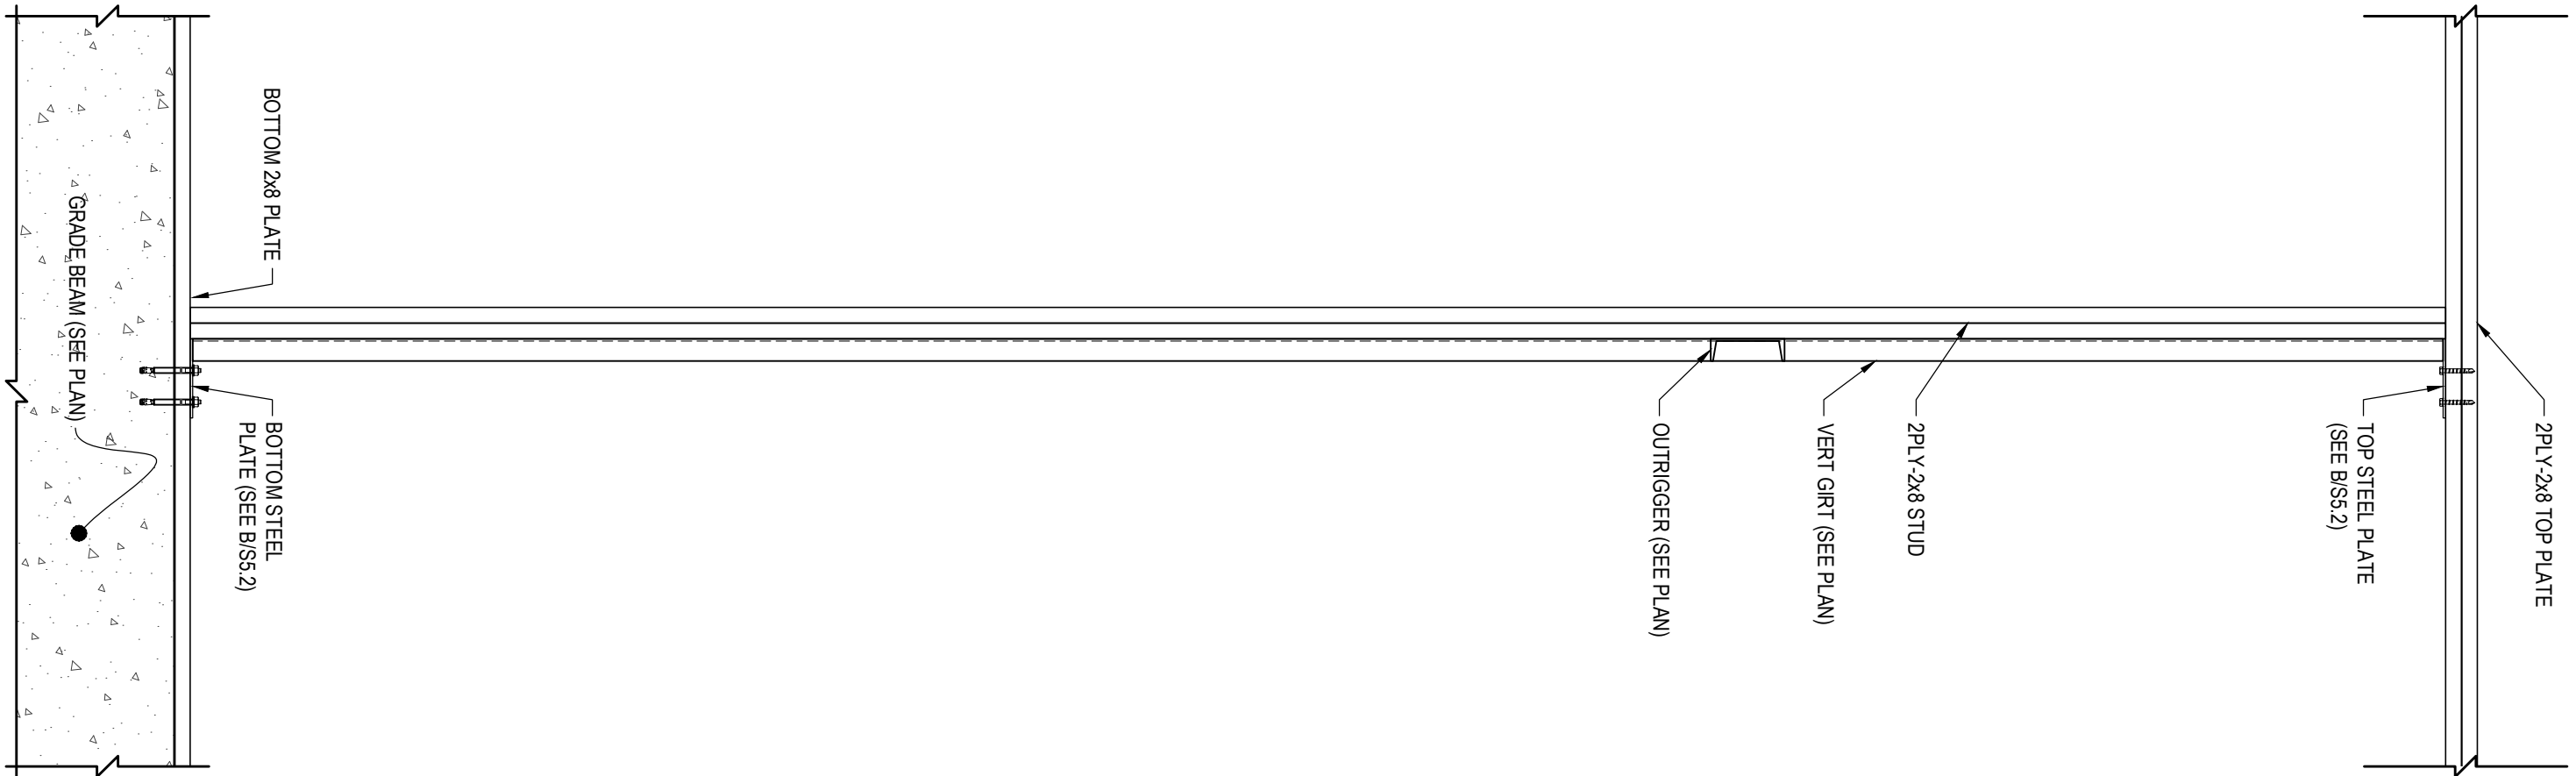

B
S5.2
DETAIL
SCALE : 3/4"=1'-0"

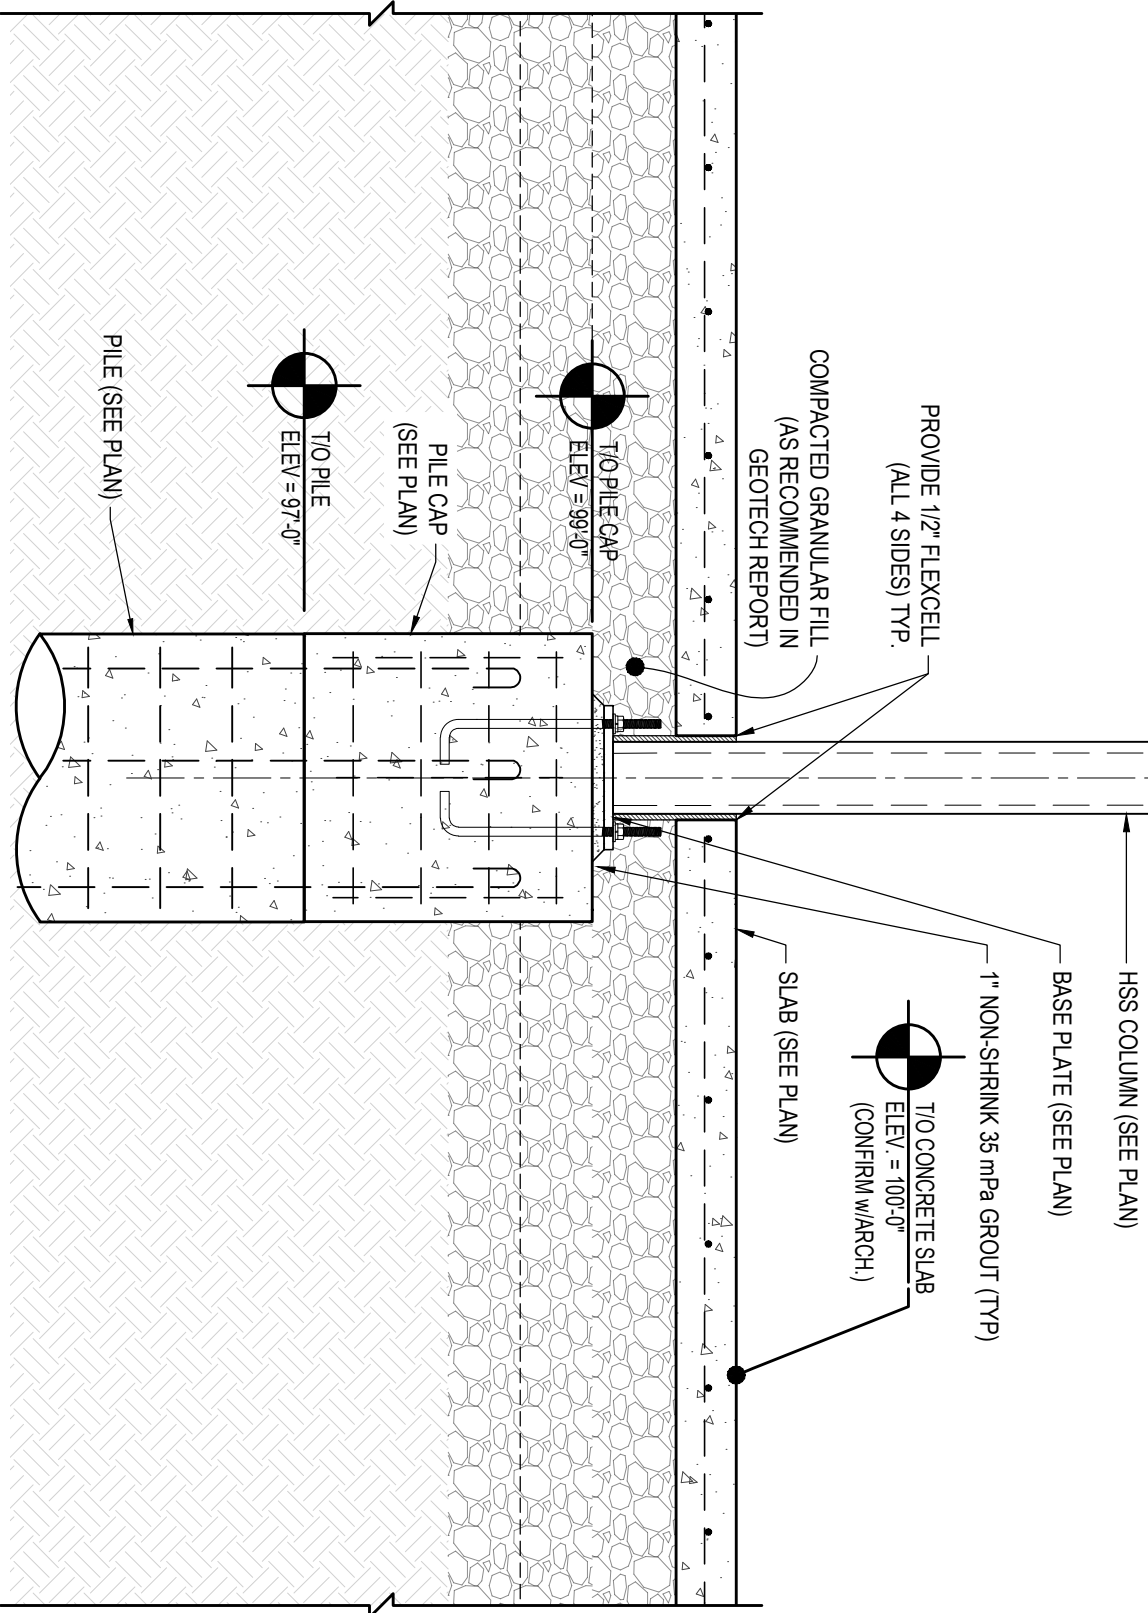

2
S5.2
SECTION
SCALE : 3/4"=1'-0"