

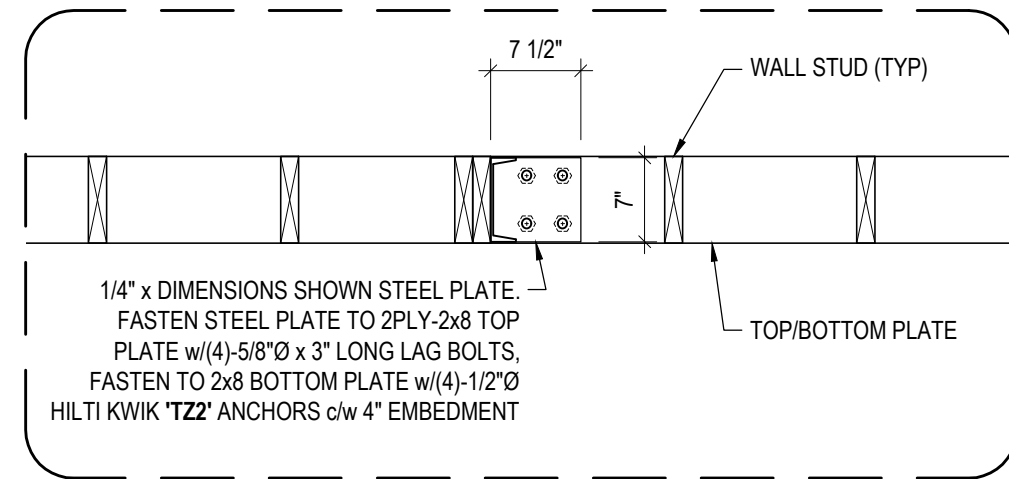


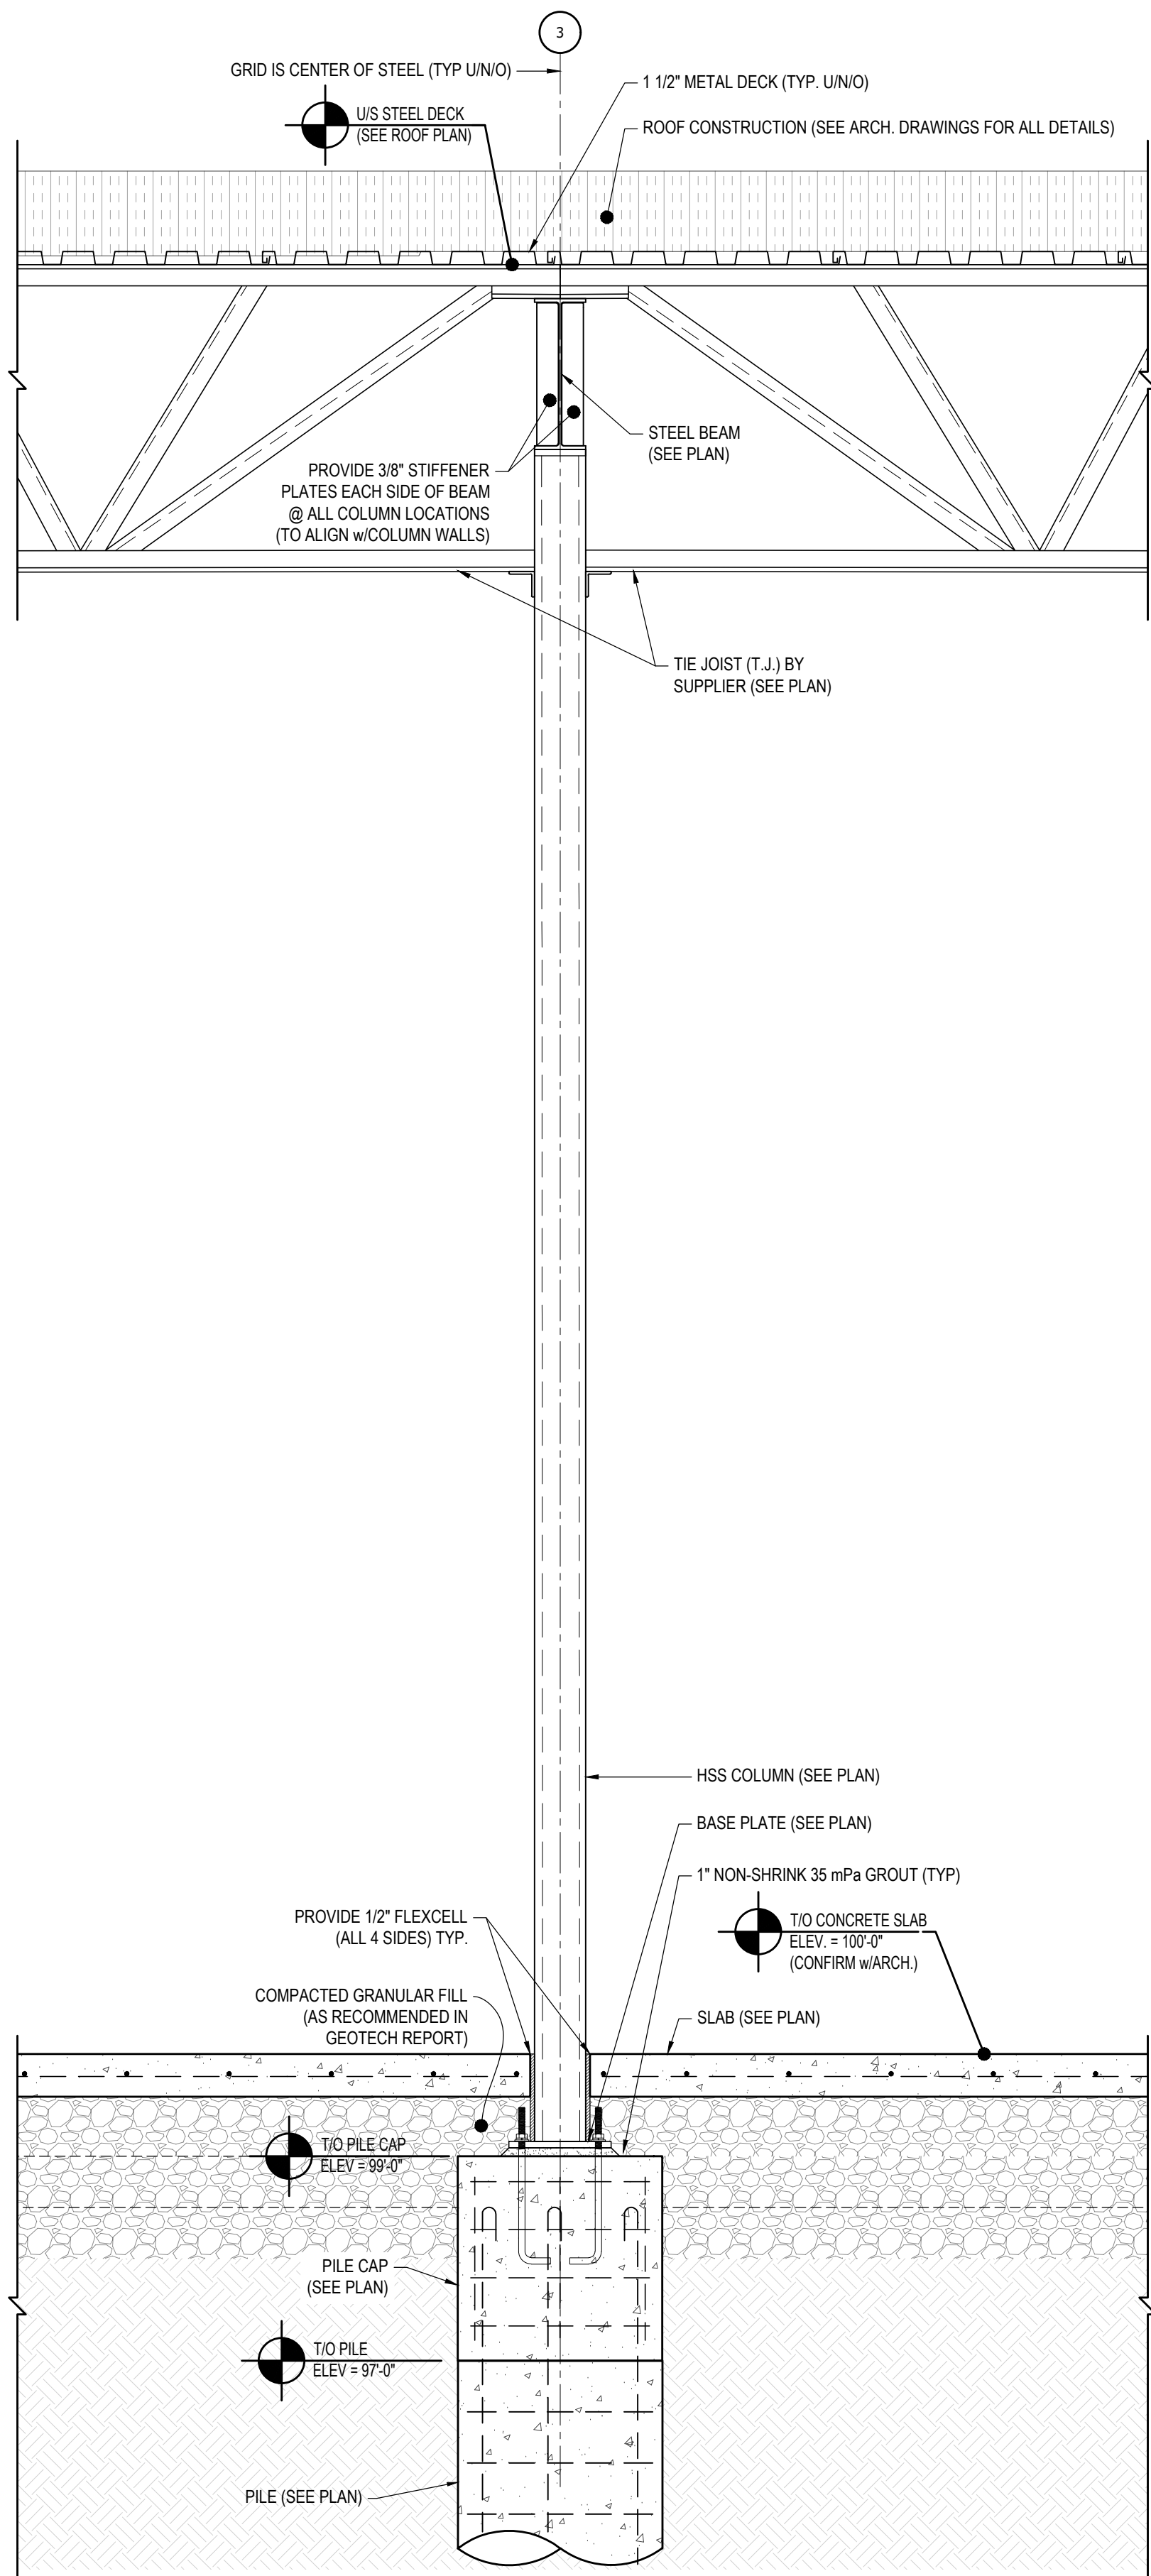

B
S5.2
DETAIL
SCALE : 3/4"=1'-0"

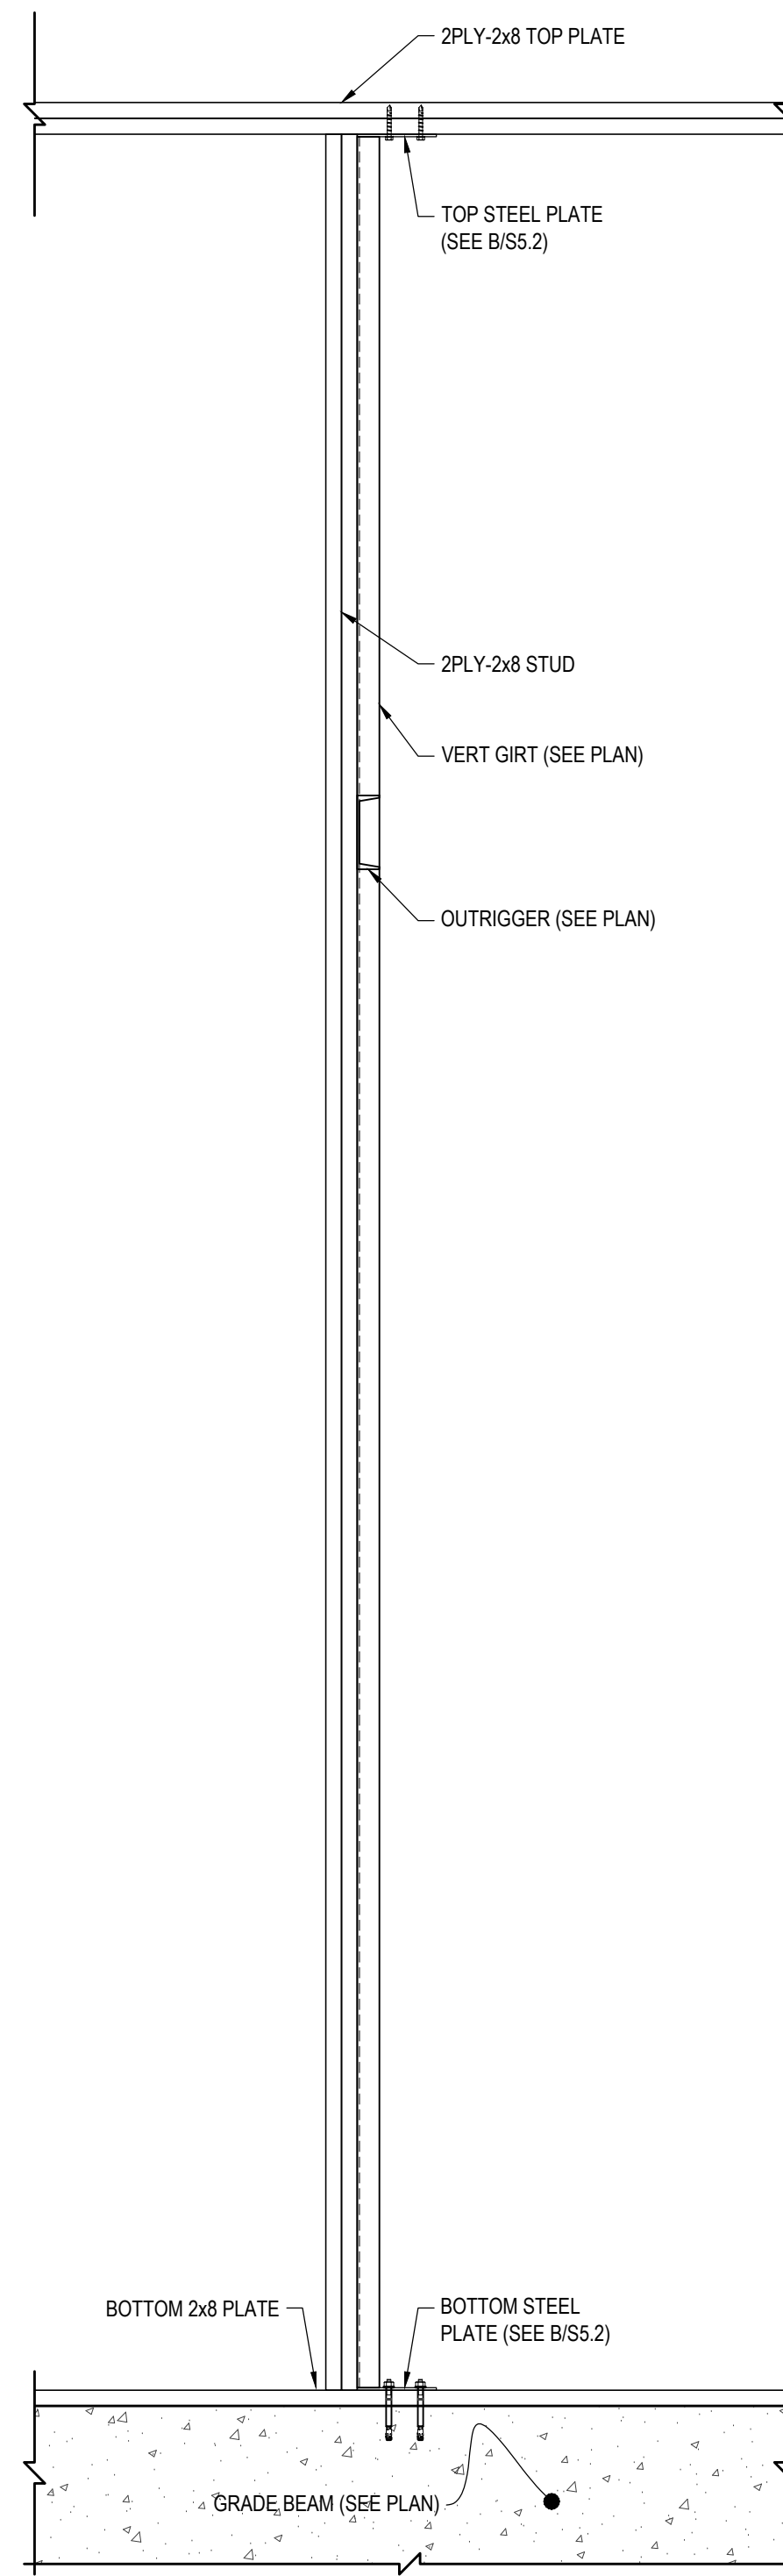

2
S5.2
SECTION
SCALE : 3/4"=1'-0"

NOT FOR CONSTRUCTION



Professional Engineering Services
1050 St. Mary's Road, Winnipeg, Manitoba R2M 3S9
Telephone: (204) 255 7251 Fax: (204) 257 7239
Website: www.beachrocke.ca

ARCCADD
ARCHITECTURE INC

109-340 Waterfront Drive, R3B 0M3 • Winnipeg, Canada
p. 204.772.6011 • f. 204.772.2043 • www.arccadd.com

Client: GS HOMES

Project: SELKIRK CRU
287 MAIN STREET
SELKIRK, MANITOBA

Drawing: SECTIONS

Issued For:
99% REVIEW

Issued Date:
05-DEC-2025

Revision Description:
N/A

Revision Date:
N/A

Project:
25-1346-CG-223

Scale:
AS NOTED

S5.2