


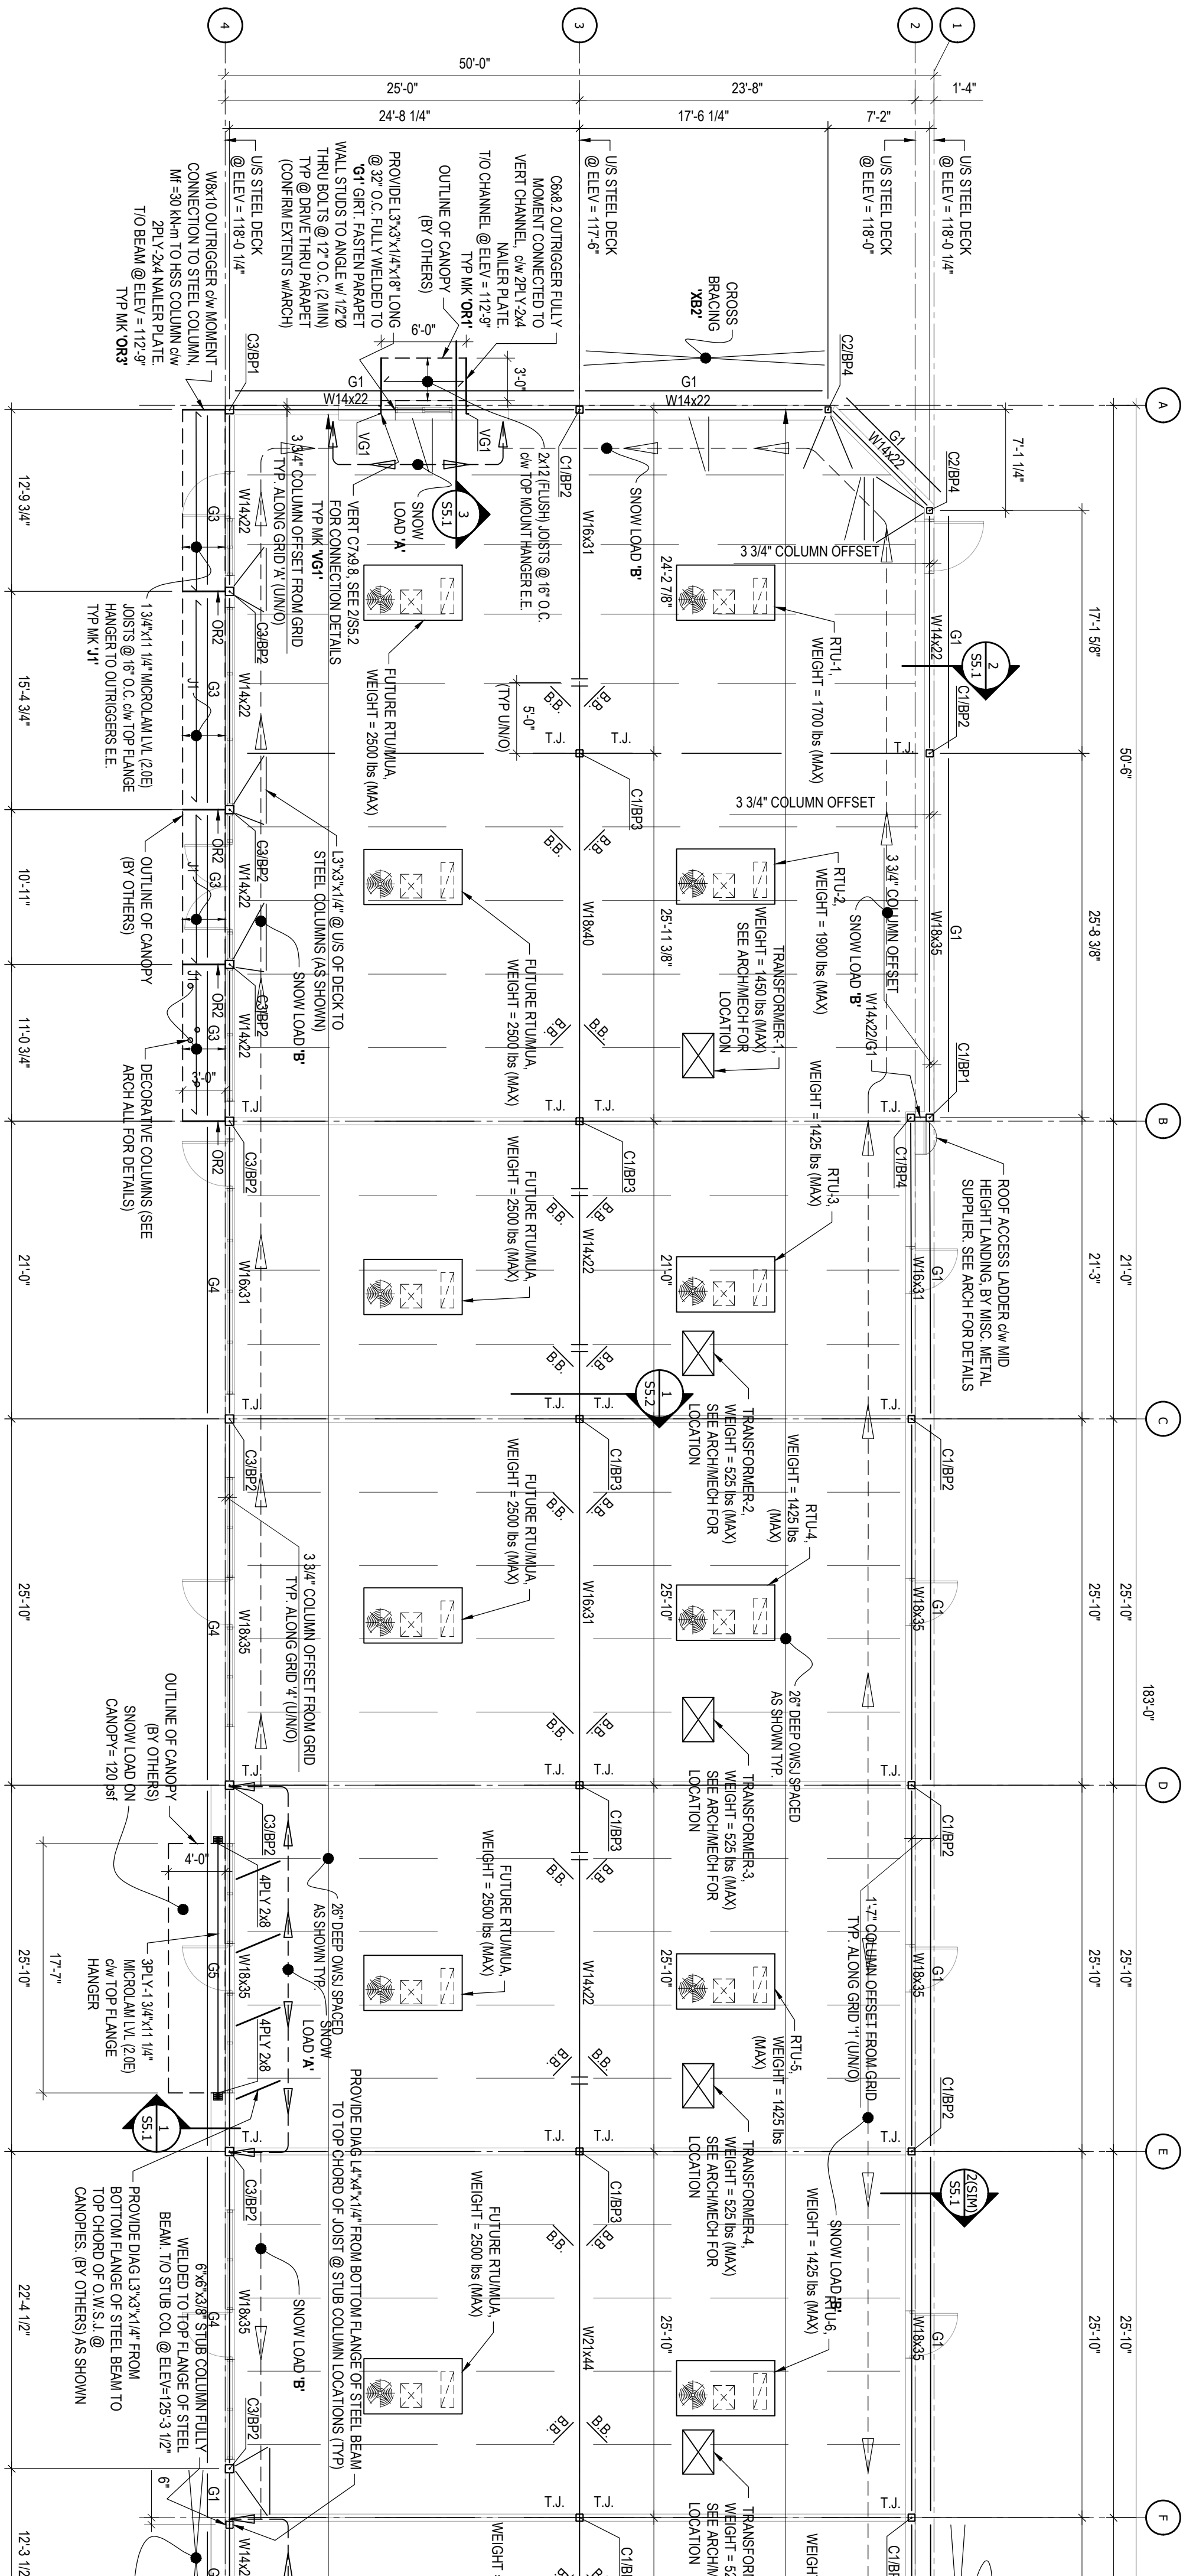

1 ROOF FRAMING PLAN

SCALE : 1/8"=1'-0"

ROOF DESIGN NOTES:


- T/O STEEL @ ELEVATION = (SEE PLAN)
- SNOW LOAD = 17.2 ksf (80 psf) UNIFORM
- DESIGN WIND LOAD = 130 psf (9.0 psf)
- DESIGN WIND LOAD = 130 psf (9.0 psf)
- GROUND CENTRE OF STEEL UNIFORM
- PROVIDE 4"x4"x3/8" ANGLES AROUND ALL DECK OPENINGS TYP
- CONTRACTOR IS RESPONSIBLE FOR CONFIRMING AND PROVIDING MECHANICAL UNIT WEIGHTS AND LOCATIONS TO JOIST SUPPLIER PRIOR TO FABRICATION
- ROOF DECKING TO BE DESIGNED FOR SNOW BUILD UP AROUND MECHANICAL UNITS
- ALL EXPOSED STEEL TO BE GALVANIZED
- SNOW BUILD UP TO BE IN ACCORDANCE WITH 2020 NATIONAL BUILDING CODE OF CANADA, CURRENT EDITION
- PROVIDE 0.8x8.2 BELOW ALL RTU CURBS
- PROVIDE 1.3x3.3x8 BELOW ALL CONDENSERS AND EXHAUST FANS

ROOF NOTES:
STEEL DECK SUPPLIER TO ENSURE ALL DECK GAUGE IS SIZED APPROPRIATELY FOR SPACING OF SUPPORTS AND LOADS SHOWN ON THE ROOF FRAMING PLAN.

ROOF FRAMING PLAN NOTES:

- CONFIRM ALL DIMENSIONS W/ARCH DWGS PRIOR TO CONSTRUCTION
- ALL DIMENSIONS ARE TAKEN FROM GRIDS (TYP UNIFORM)
- CONFIRM ALL STEEL ELEVATIONS W/ARCH DWGS PRIOR TO CONSTRUCTION
- STEEL IS ON FACE OF GRIDS (TYP UNIFORM)

BUILT-UP-SNOW LOAD SCHEDULE

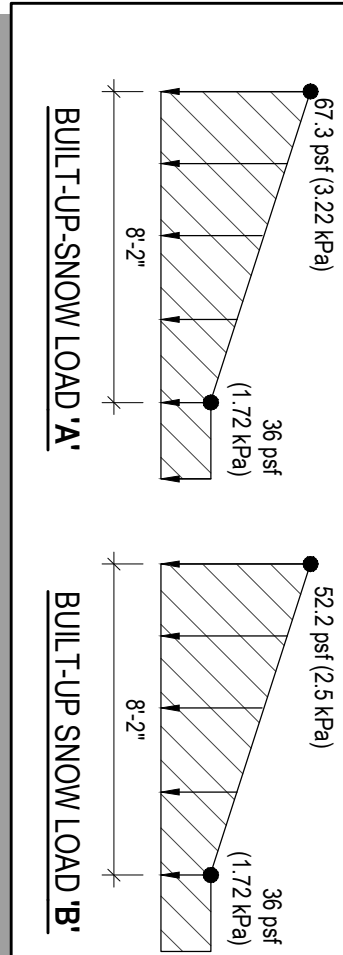

CROSS BRACING SCHED		
MARK	DESCRIPTION	TOP FACTOR HORIZONTAL
2B1	HSS 5"x5"x1/4"	40 kN
2B2	HSS 7"x7"x5/16"	115 kN
2B3	HSS 7"x7"x1/2"	115 kN

GIRT SCHEDULE

MARK	DESCRIPTION
91	HSS 5"x5"x1/4" T/O GIRT @ ELEVATION = 123.3 1/16"
92	HSS 5"x5"x1/4" T/O GIRT @ ELEVATION = 123.3 1/16"
93	HSS 5"x5"x1/4" T/O GIRT @ ELEVATION = 123.3 1/16"
94	HSS 5"x5"x1/4" T/O GIRT @ ELEVATION = 123.3 1/16"
95	HSS 5"x5"x1/4" T/O GIRT @ ELEVATION = 123.3 1/16"


- GIRT NOTES:**
- CONFIRM ALL ELEVATIONS W/ARCH. DRAWINGS PRIOR TO CONSTRUCTION
 - PROVIDE 3/4"x3/4" RODS @ MID SPAN ALL GIRTS @ OUTSIDE FACE OF BEAM (TYP)
 - DESIGN GIRT TO COLUMN CONNECTION FOR T/O = 25 kN (MN)

WOOD LINTEL SCHEDULE

R.O. SIZE	DESCRIPTION
0" TO 4" 0"	2P LVL 2x8 @ W 2x8 SIL. PLATE @ W 1" JACK. HANGING EACH SIDE OF R.O.
4" TO 8" 0"	2P LVL 2x8 @ W 2x8 SIL. PLATE @ W 1" JACK. 2x4 HANGING EACH SIDE OF R.O.

A BOTTOM BRACE 'B' DETAIL

SCALE : 3/4"=1'-0"

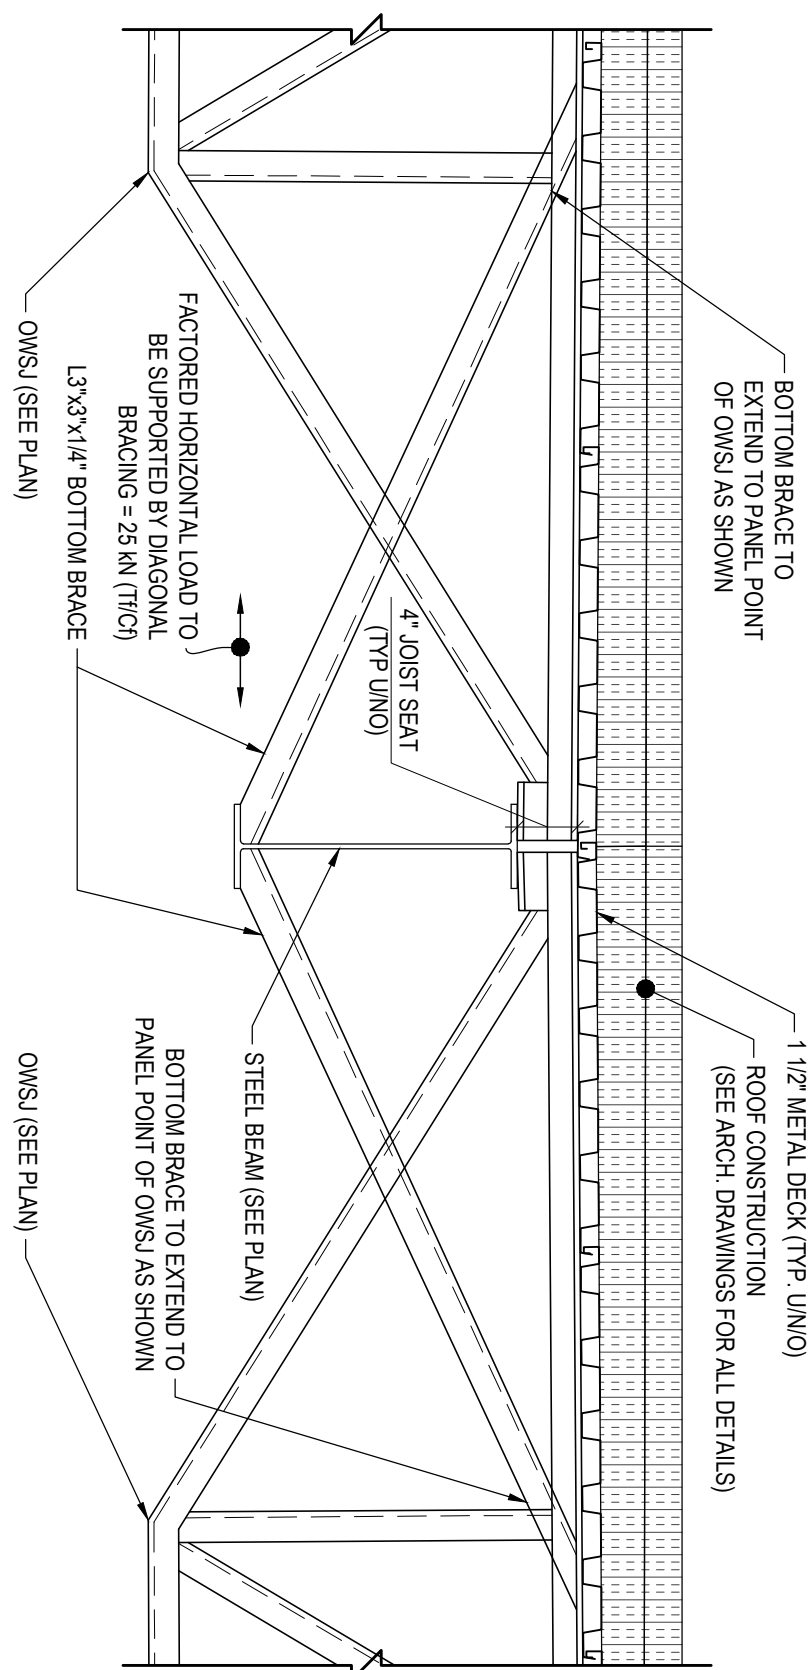

1 1/2" METAL DECK (TYP UNIFORM)
(SEE ARCH. DRAWINGS FOR ALL DETAILS)

STEEL BEAM (SEE PLAN)

FACTORED HORIZONTAL LOAD TO BE SUPPORTED BY DIAGONAL BRACING = 25 kN (TYP UNIFORM)

OWS (SEE PLAN)