



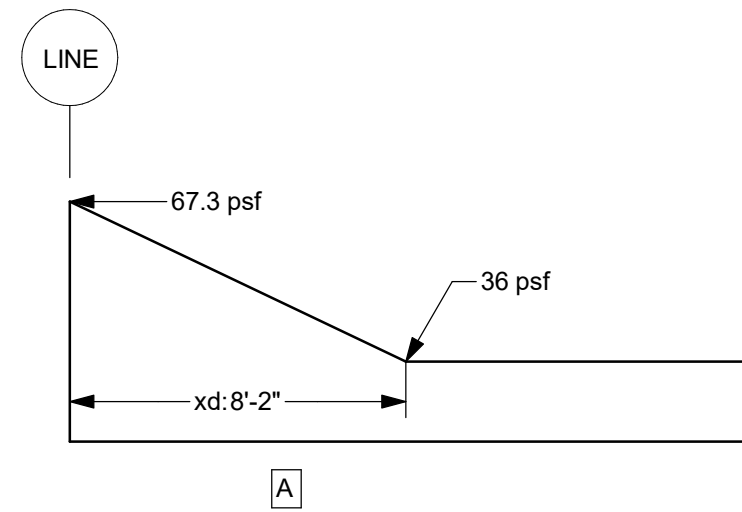



SNOW LOAD ACCUMULATION

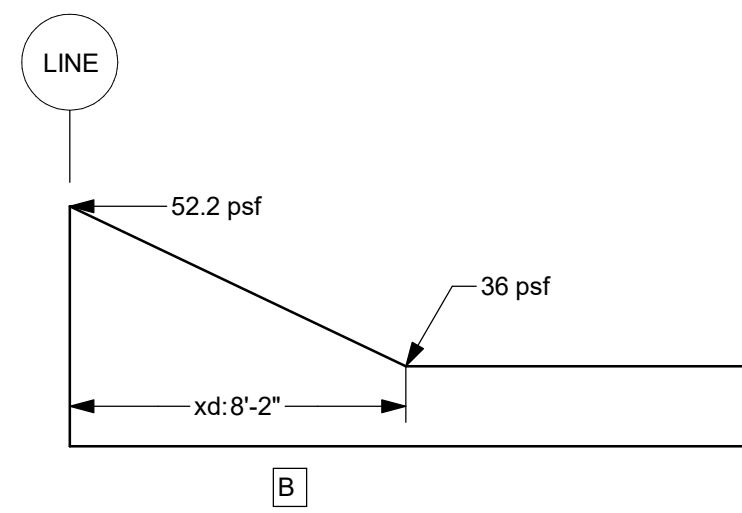

SNOW LOAD ACCUMULATION




RAIN LOAD + ADDITIONNAL LIVE LOAD

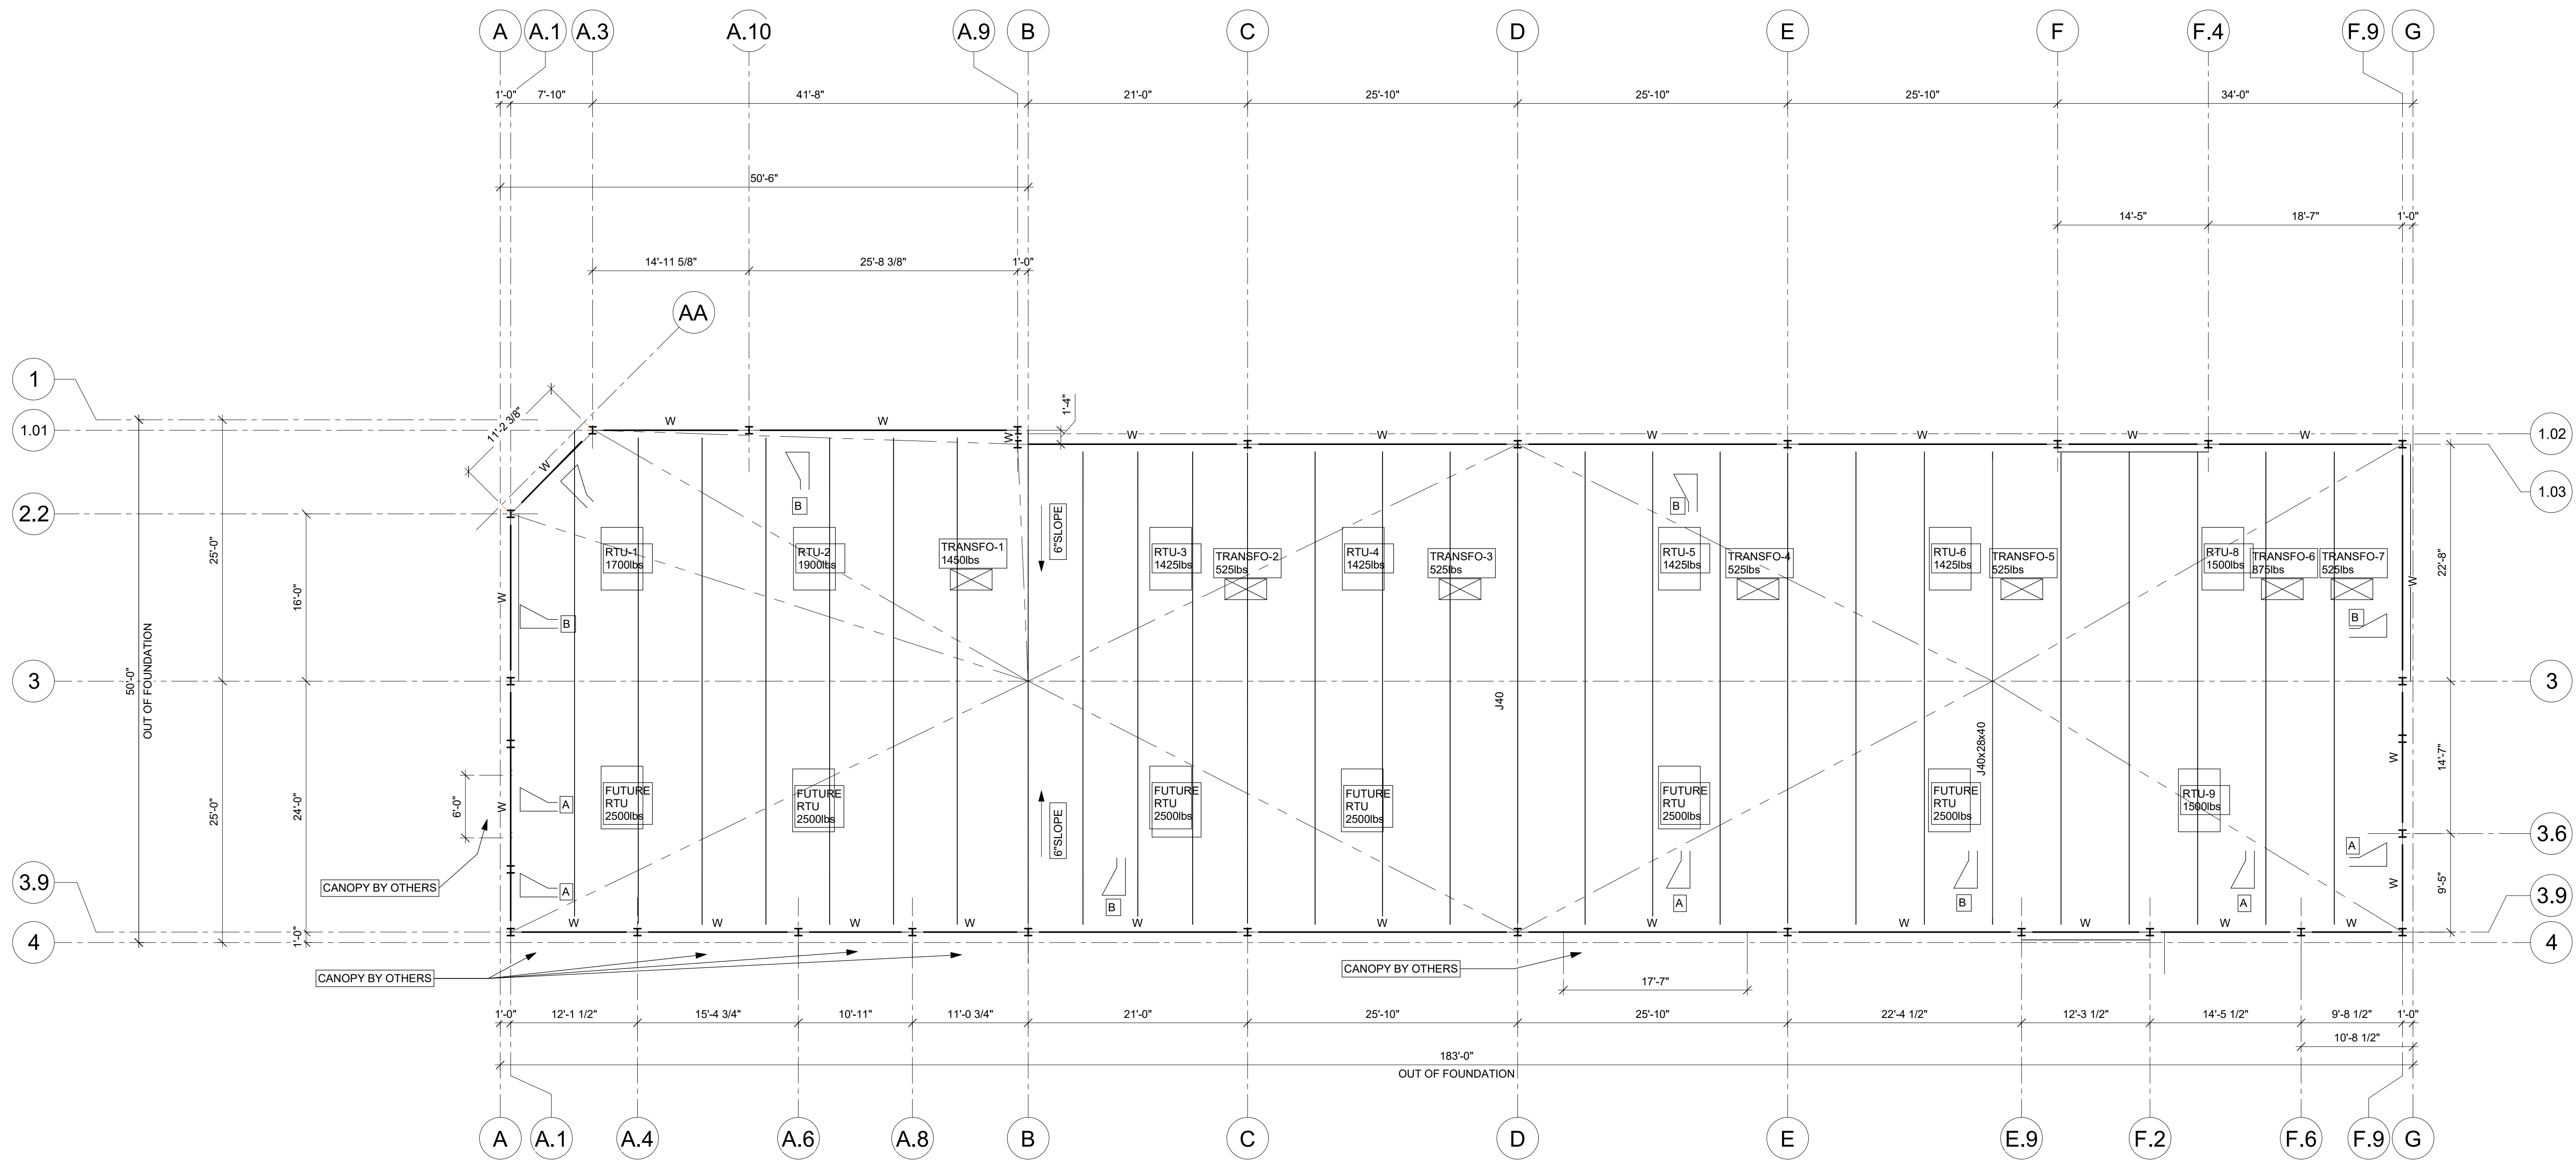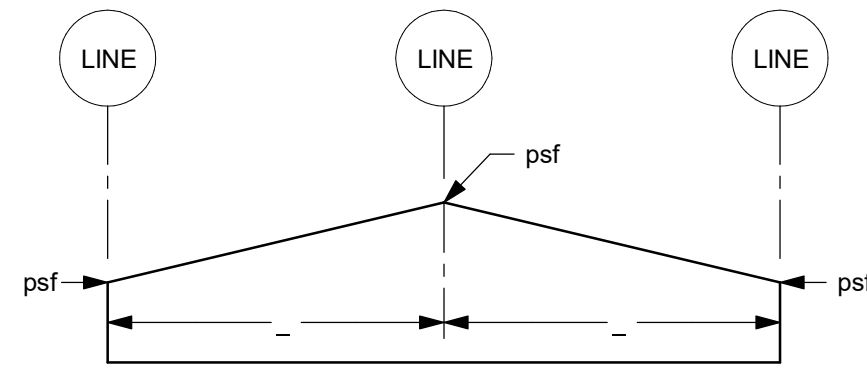

ROOF PLAN
1/8" = 1'-0"

GROSS UPLIFT DIAGRAM (UNFACTORED):

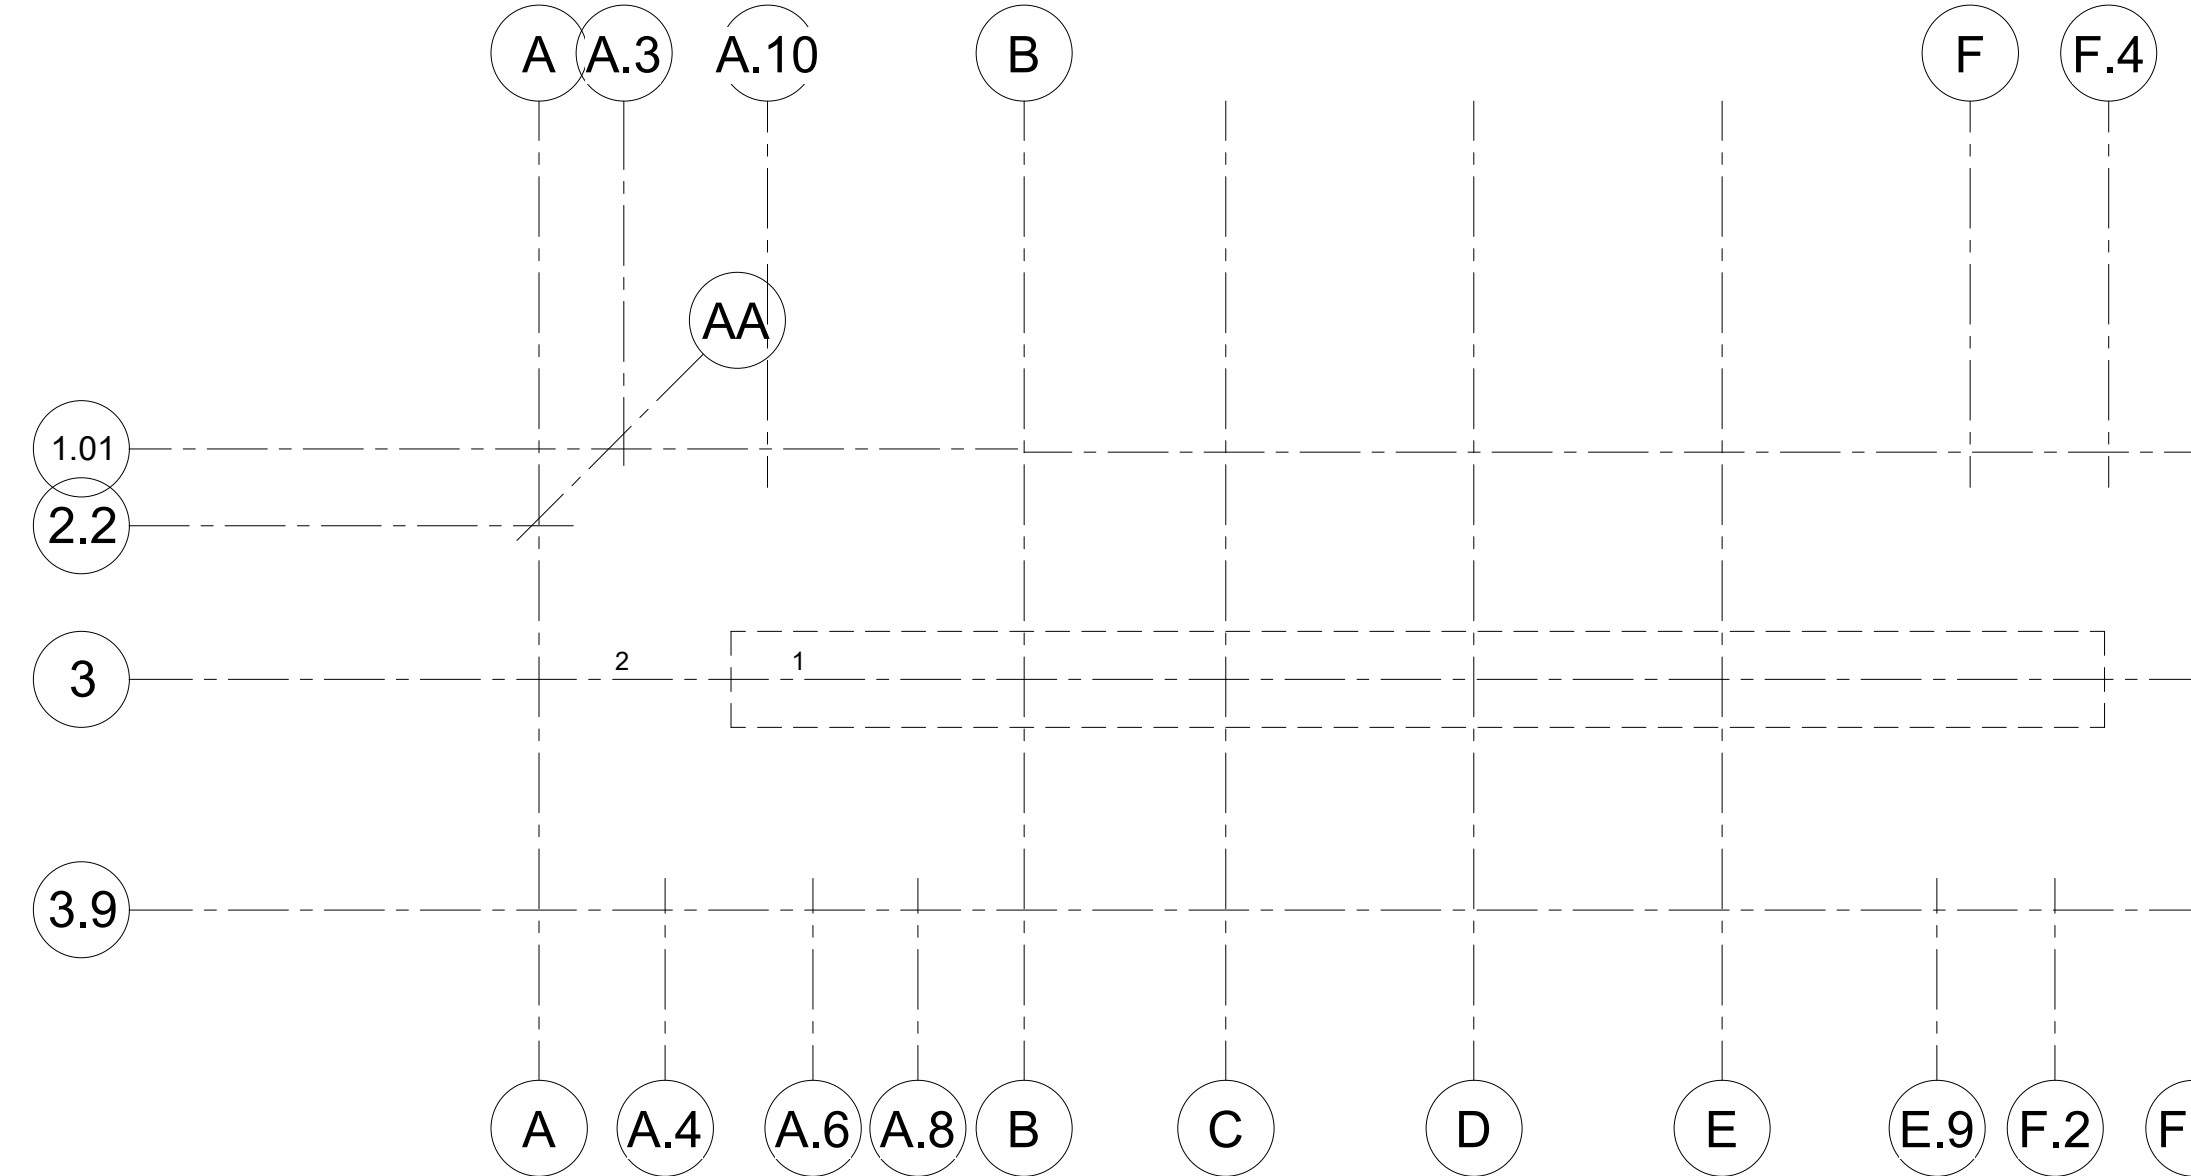

ZONE 1 : -17.77 psf
ZONE 2 : -22psf
a : 5'-0"

POSITIVE WIND PRESSURE
(UNFACTORED): 10.15 psf