


| DOOR SCHEDULE |      |              
|---------------|------|--------------|------------------|---------------|------------|--------|--------|---------------------------------------|-------------------------------------|-----------------------|-------------------------------------|----------------------------------|----------------------------|-----------|----------------------------|-------------|-----------------|--------------|----------|---------|
| Identity      | Qty. | Door 18 ga.  |                  |               | Glass      |        |        |                                       | Hardware                            |                       |                                     |                                  |                            |           |                            |             |                 |              |          | Remarks |
|               |      | Installation | Insulation (R12) | Dimensions    | Swing side | Width  | Height | Steel frame 16 ga. with thermal break | (3) Hinges non-rising removable pin | Door lock & latch set | Panic bar without outside trim 22EO | Panic bar with outside trim 23OL | Surface bolt inactive door | Threshold | Astragal for inactive door | Door closer | Door chain stop | Weatherstrip | Head cap |         |
| D1            | 9    |              |                  | 3'-0" x 7'-0" |            | 1'-10" | 1'-6"  |                                       |                                     |                       |                                     |                                  |                            |           |                            |             |                 |              |          |         |

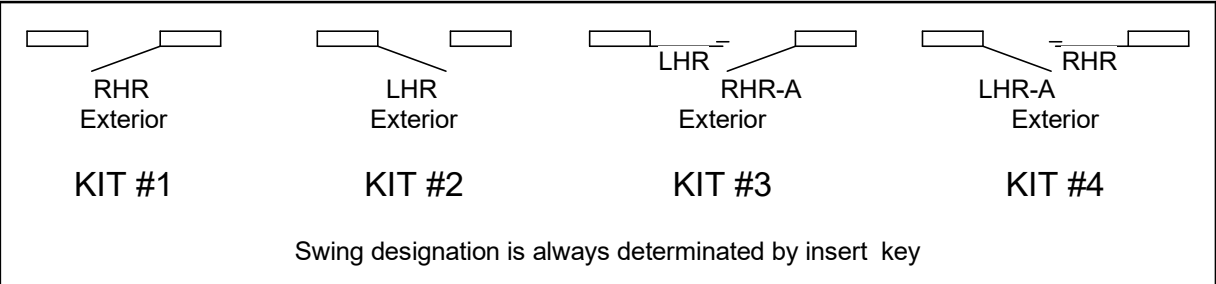


Supplier's standard hardware:


- Hinges: Stanley F88179 4.5" x 4"
- Exit device: Von Duprin 22 x 689 with outside trim 23OL
- Permanent cylinder: Schlage 20001C 626
- Door closure: LCN 1261 689
- Head and jamb seal: Unique 1650
- Bottom seal: Unique D54
- Threshold: See the remarks in "Door schedule"

| O/H & OPENING SCHEDULE |                 |     |         |
|------------------------|-----------------|-----|---------|
| Total                  | Type            | Tag | Remarks |
| 2                      | 10'-0" x 10'-0" | O/H |         |
| 2                      | 16'-0" x 16'-0" | O/H |         |
| 3                      | 18'-0" x 18'-0" | O/H |         |
| Total général: 7       |                 |     |         |


| WINDOW SCHEDULE |      |              |                                                                               |                           |
|-----------------|------|--------------|-------------------------------------------------------------------------------|---------------------------|
| Identity        | Qty. | Installation | Description                                                                   | Remarks                   |
| W1              | 5    |              | Fixed aluminum window with thermal break and sealed glass + Low-E argon clear | Aluminum Frame (no color) |
| W2              | 9    |              | Fixed aluminum window with thermal break and sealed glass + Low-E argon clear | Aluminum Frame (no color) |

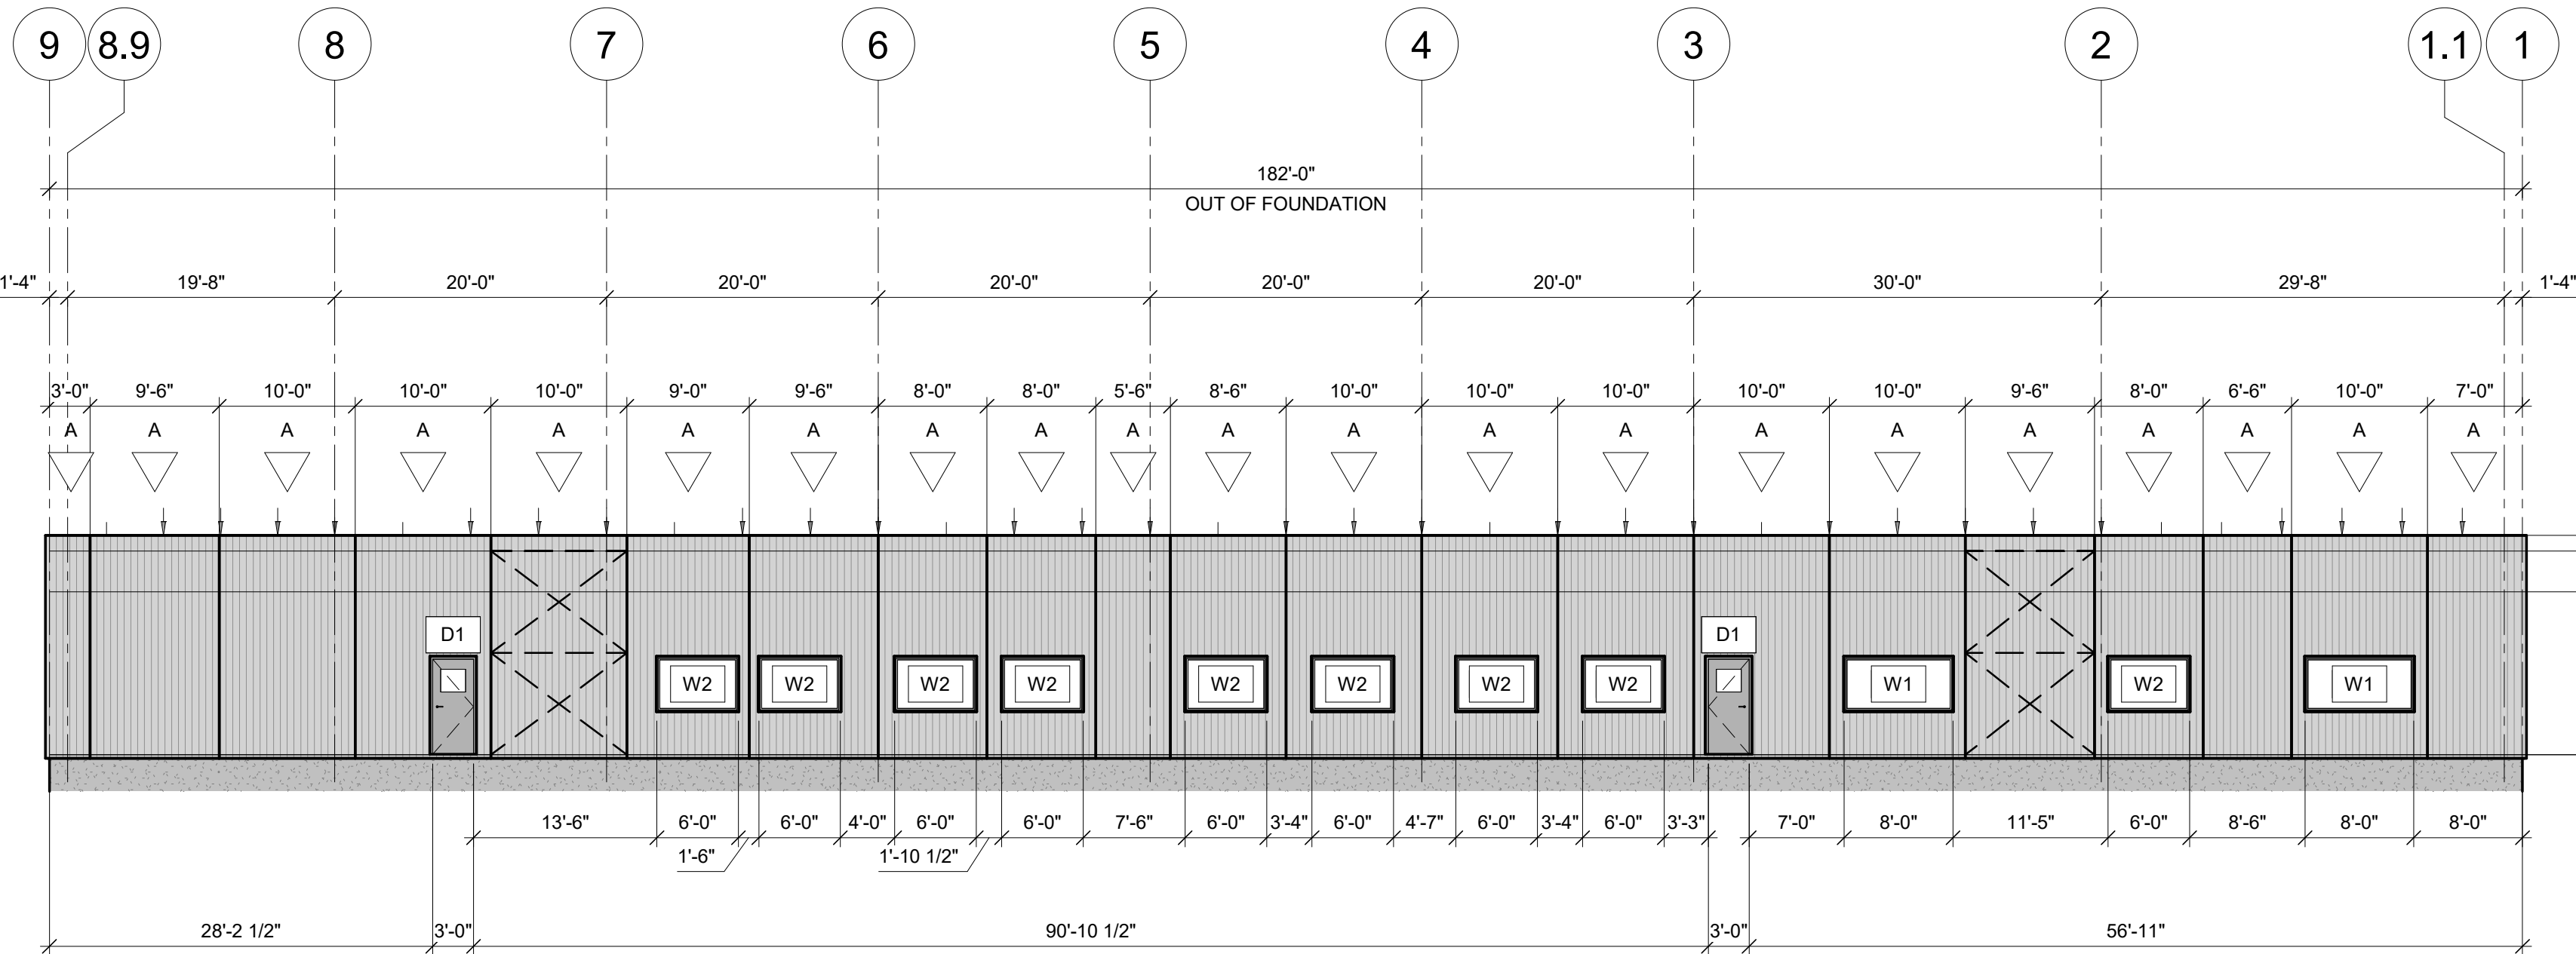


ELEVATION LINE A (WEST)  
3/32" = 1'-0"

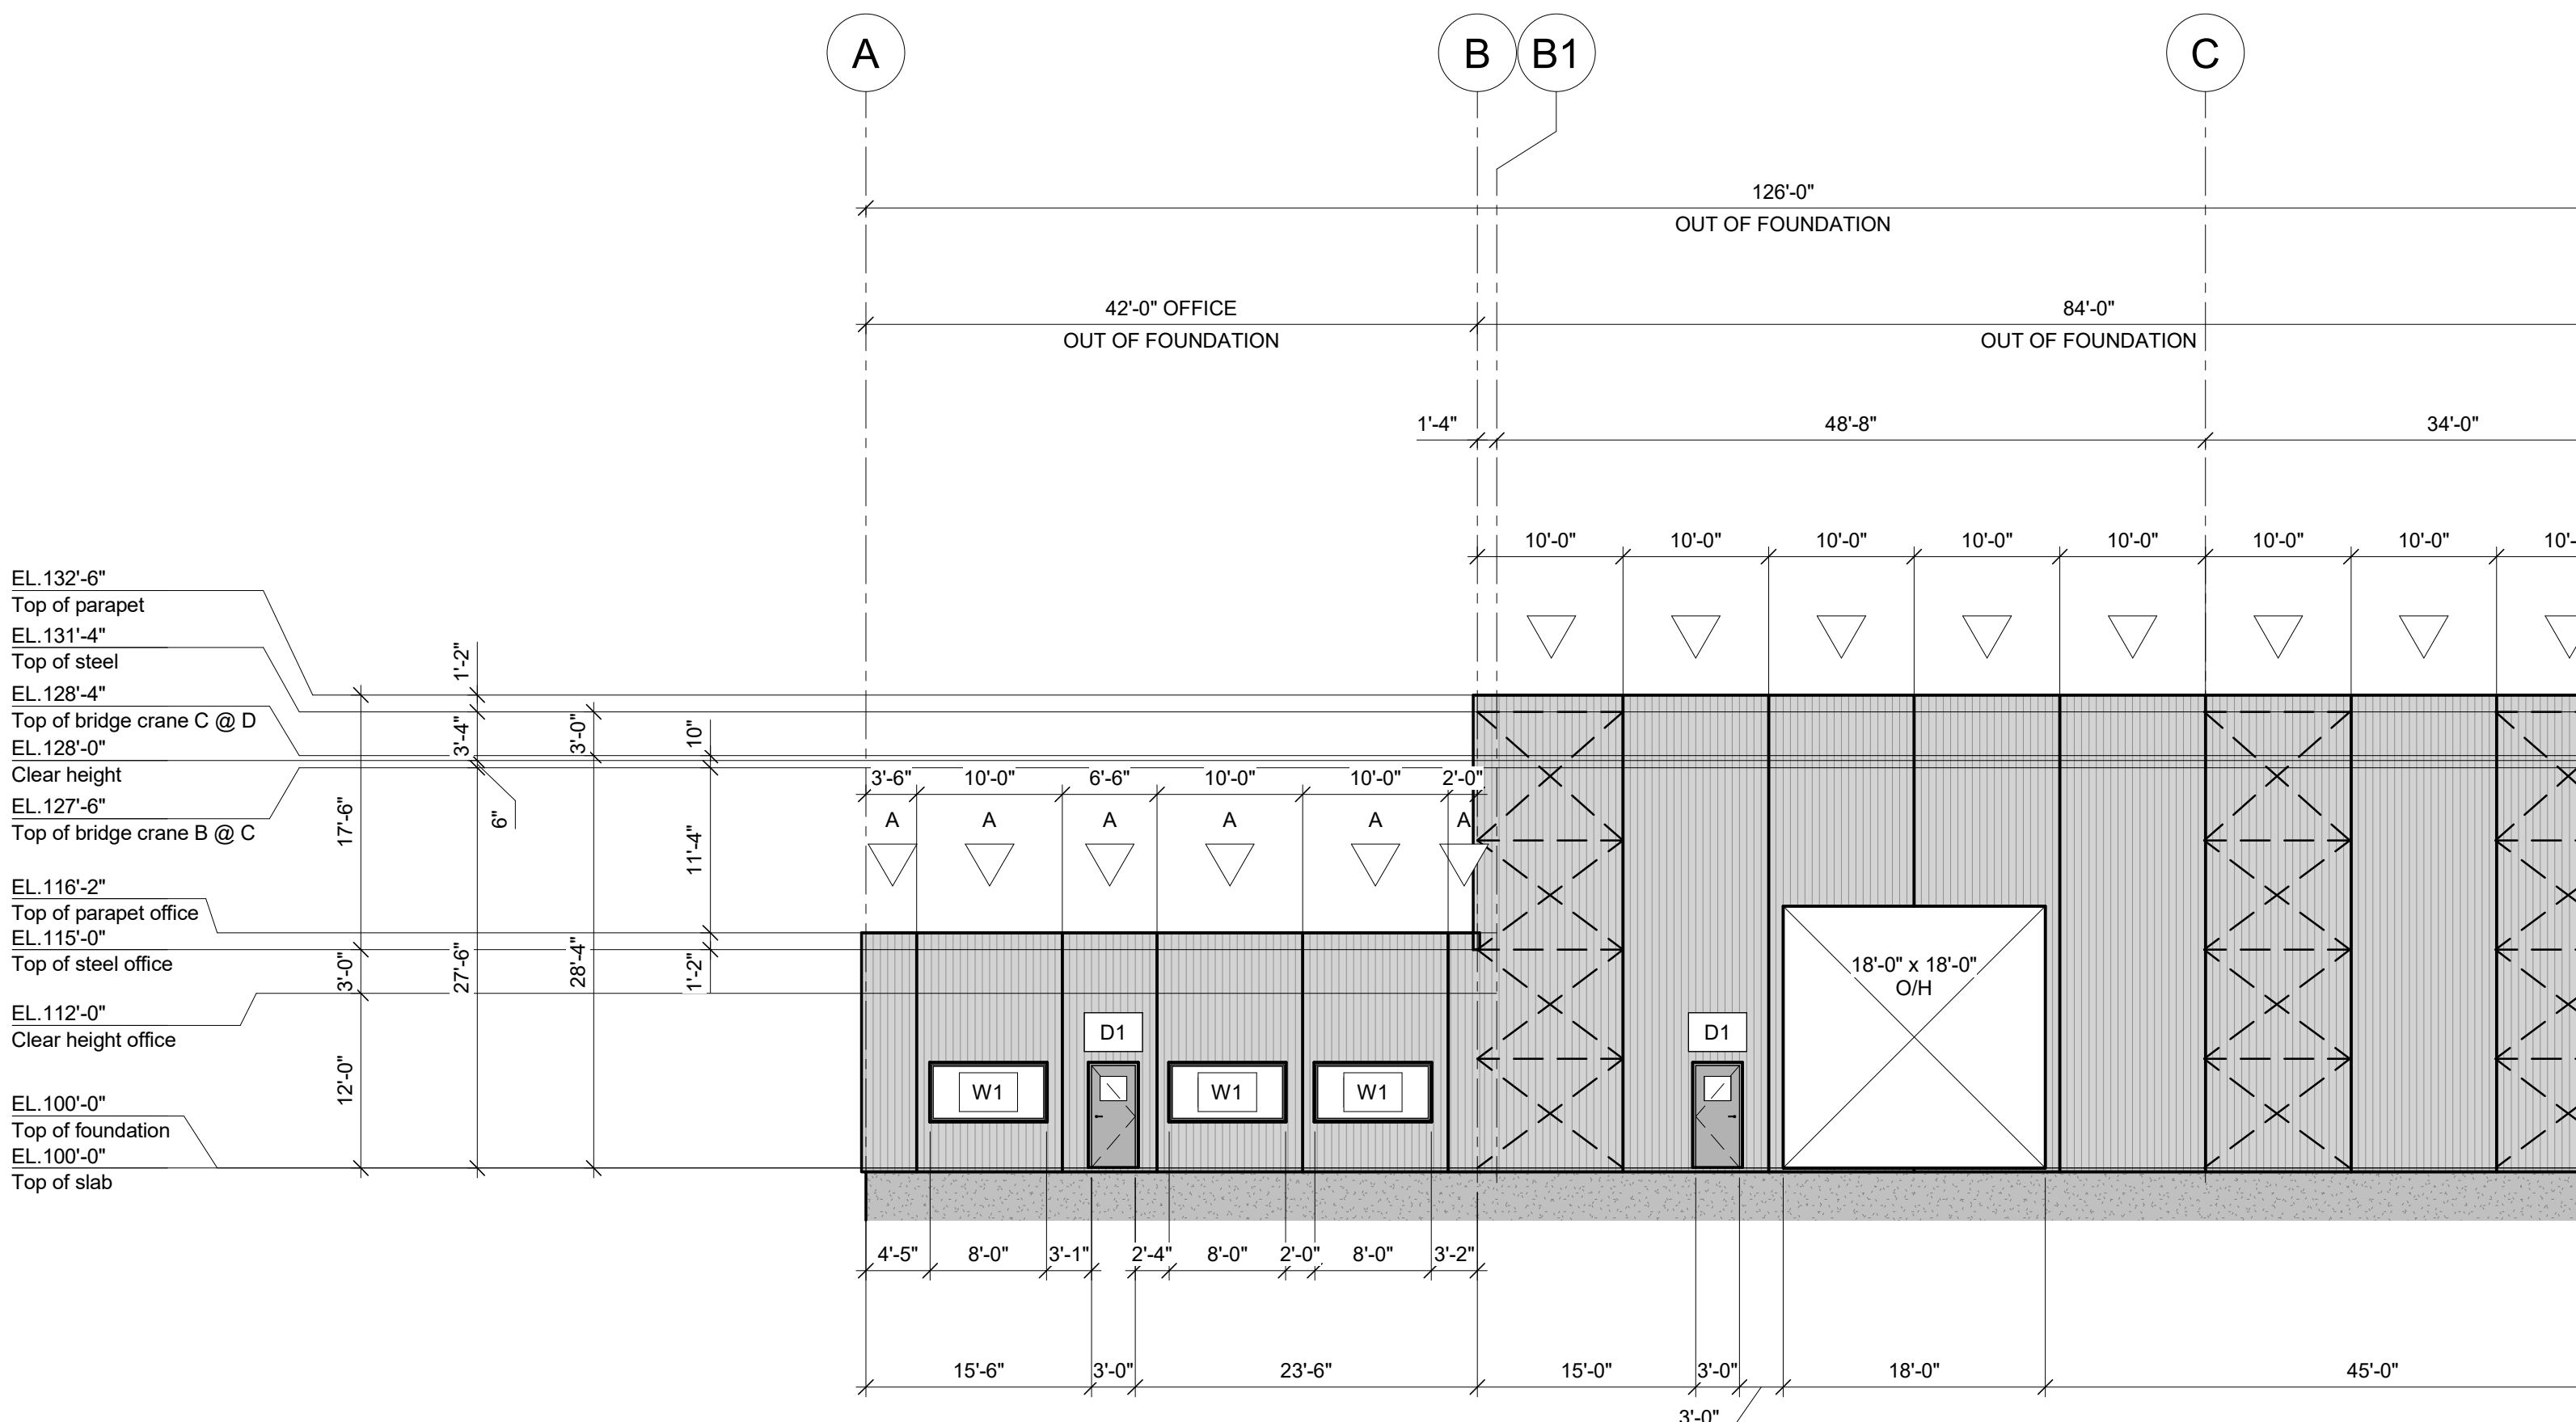


ELEVATION LINE 1 (SOUTH)  
3/32" = 1'-0"

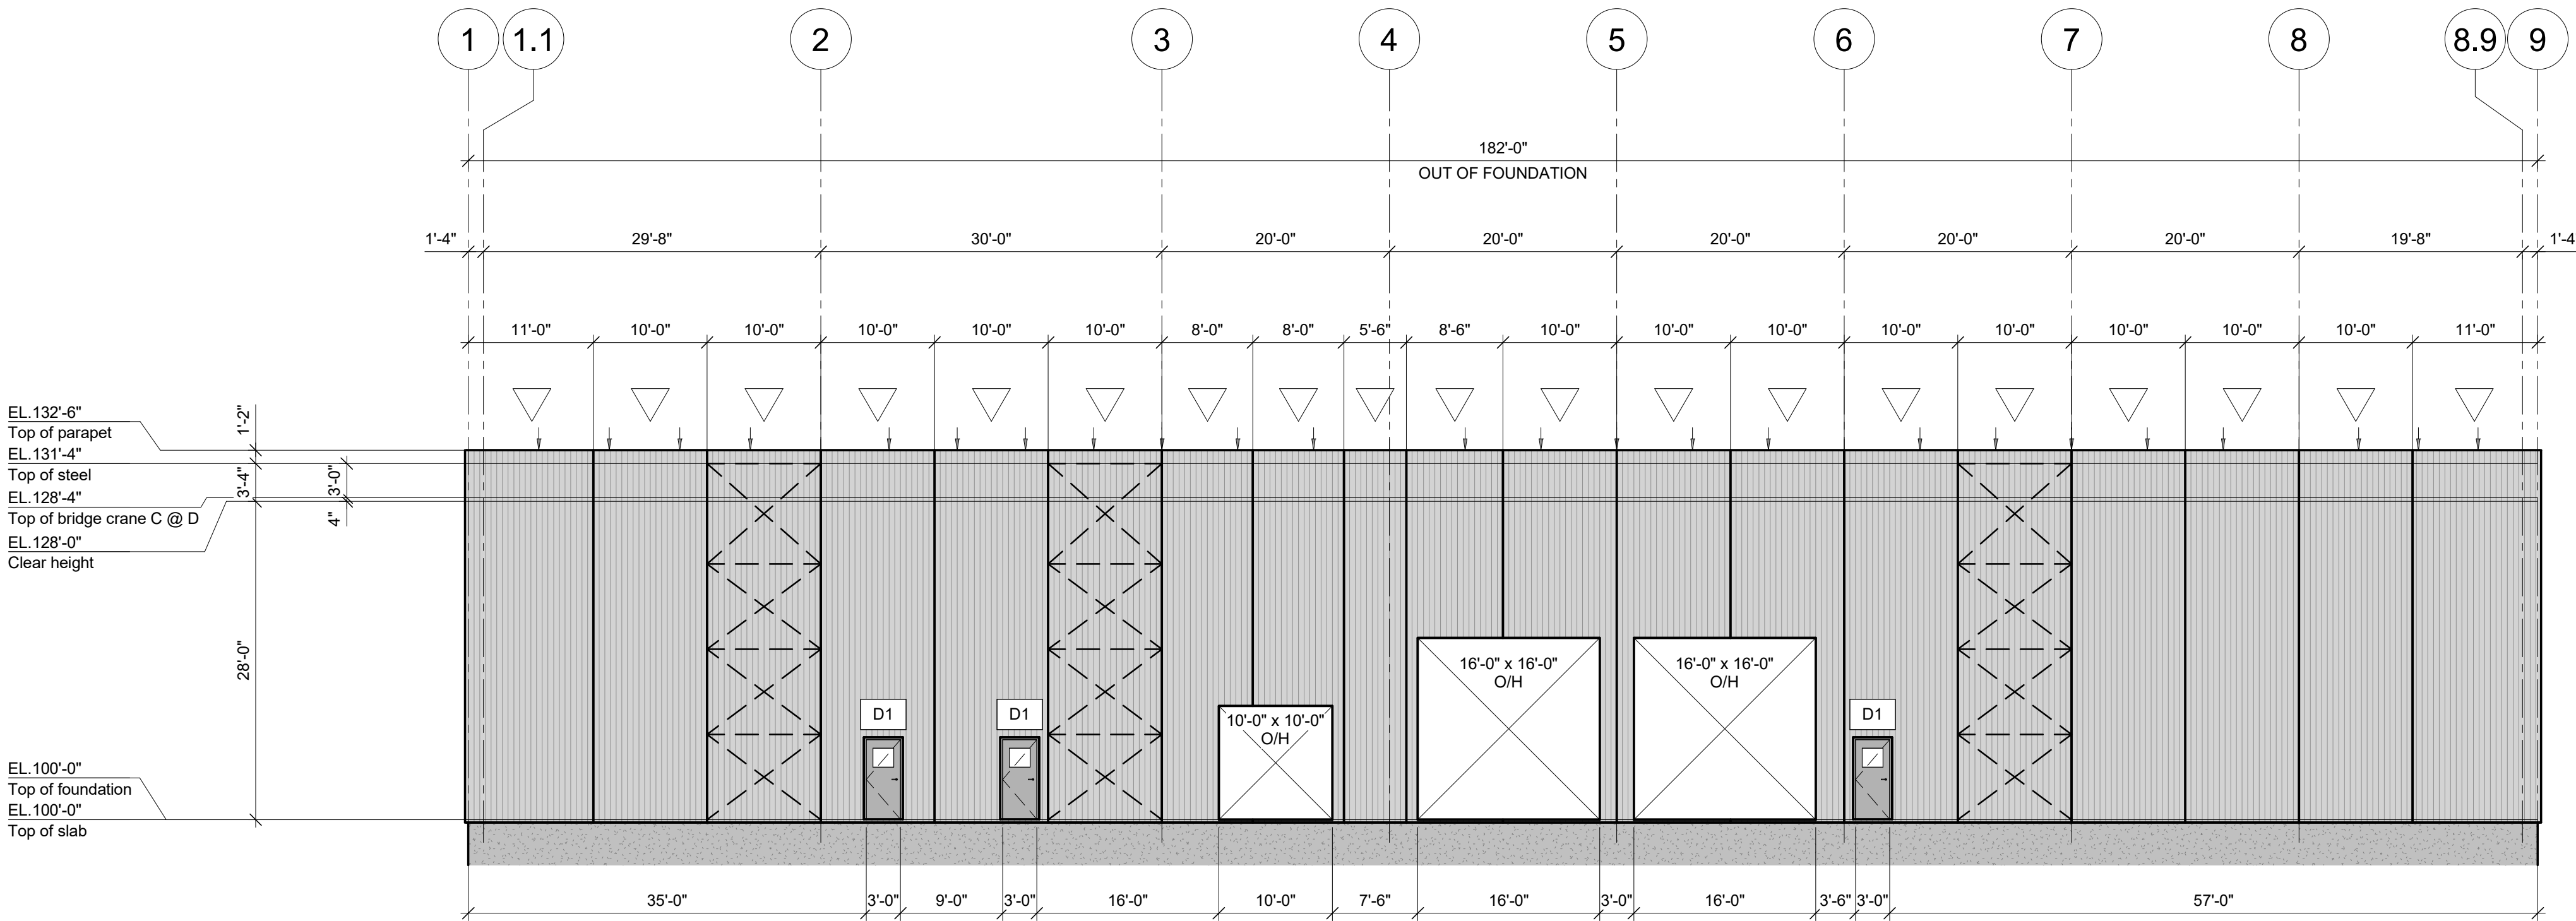


ELEVATION LINE D (EAST)  
3/32" = 1'-0"

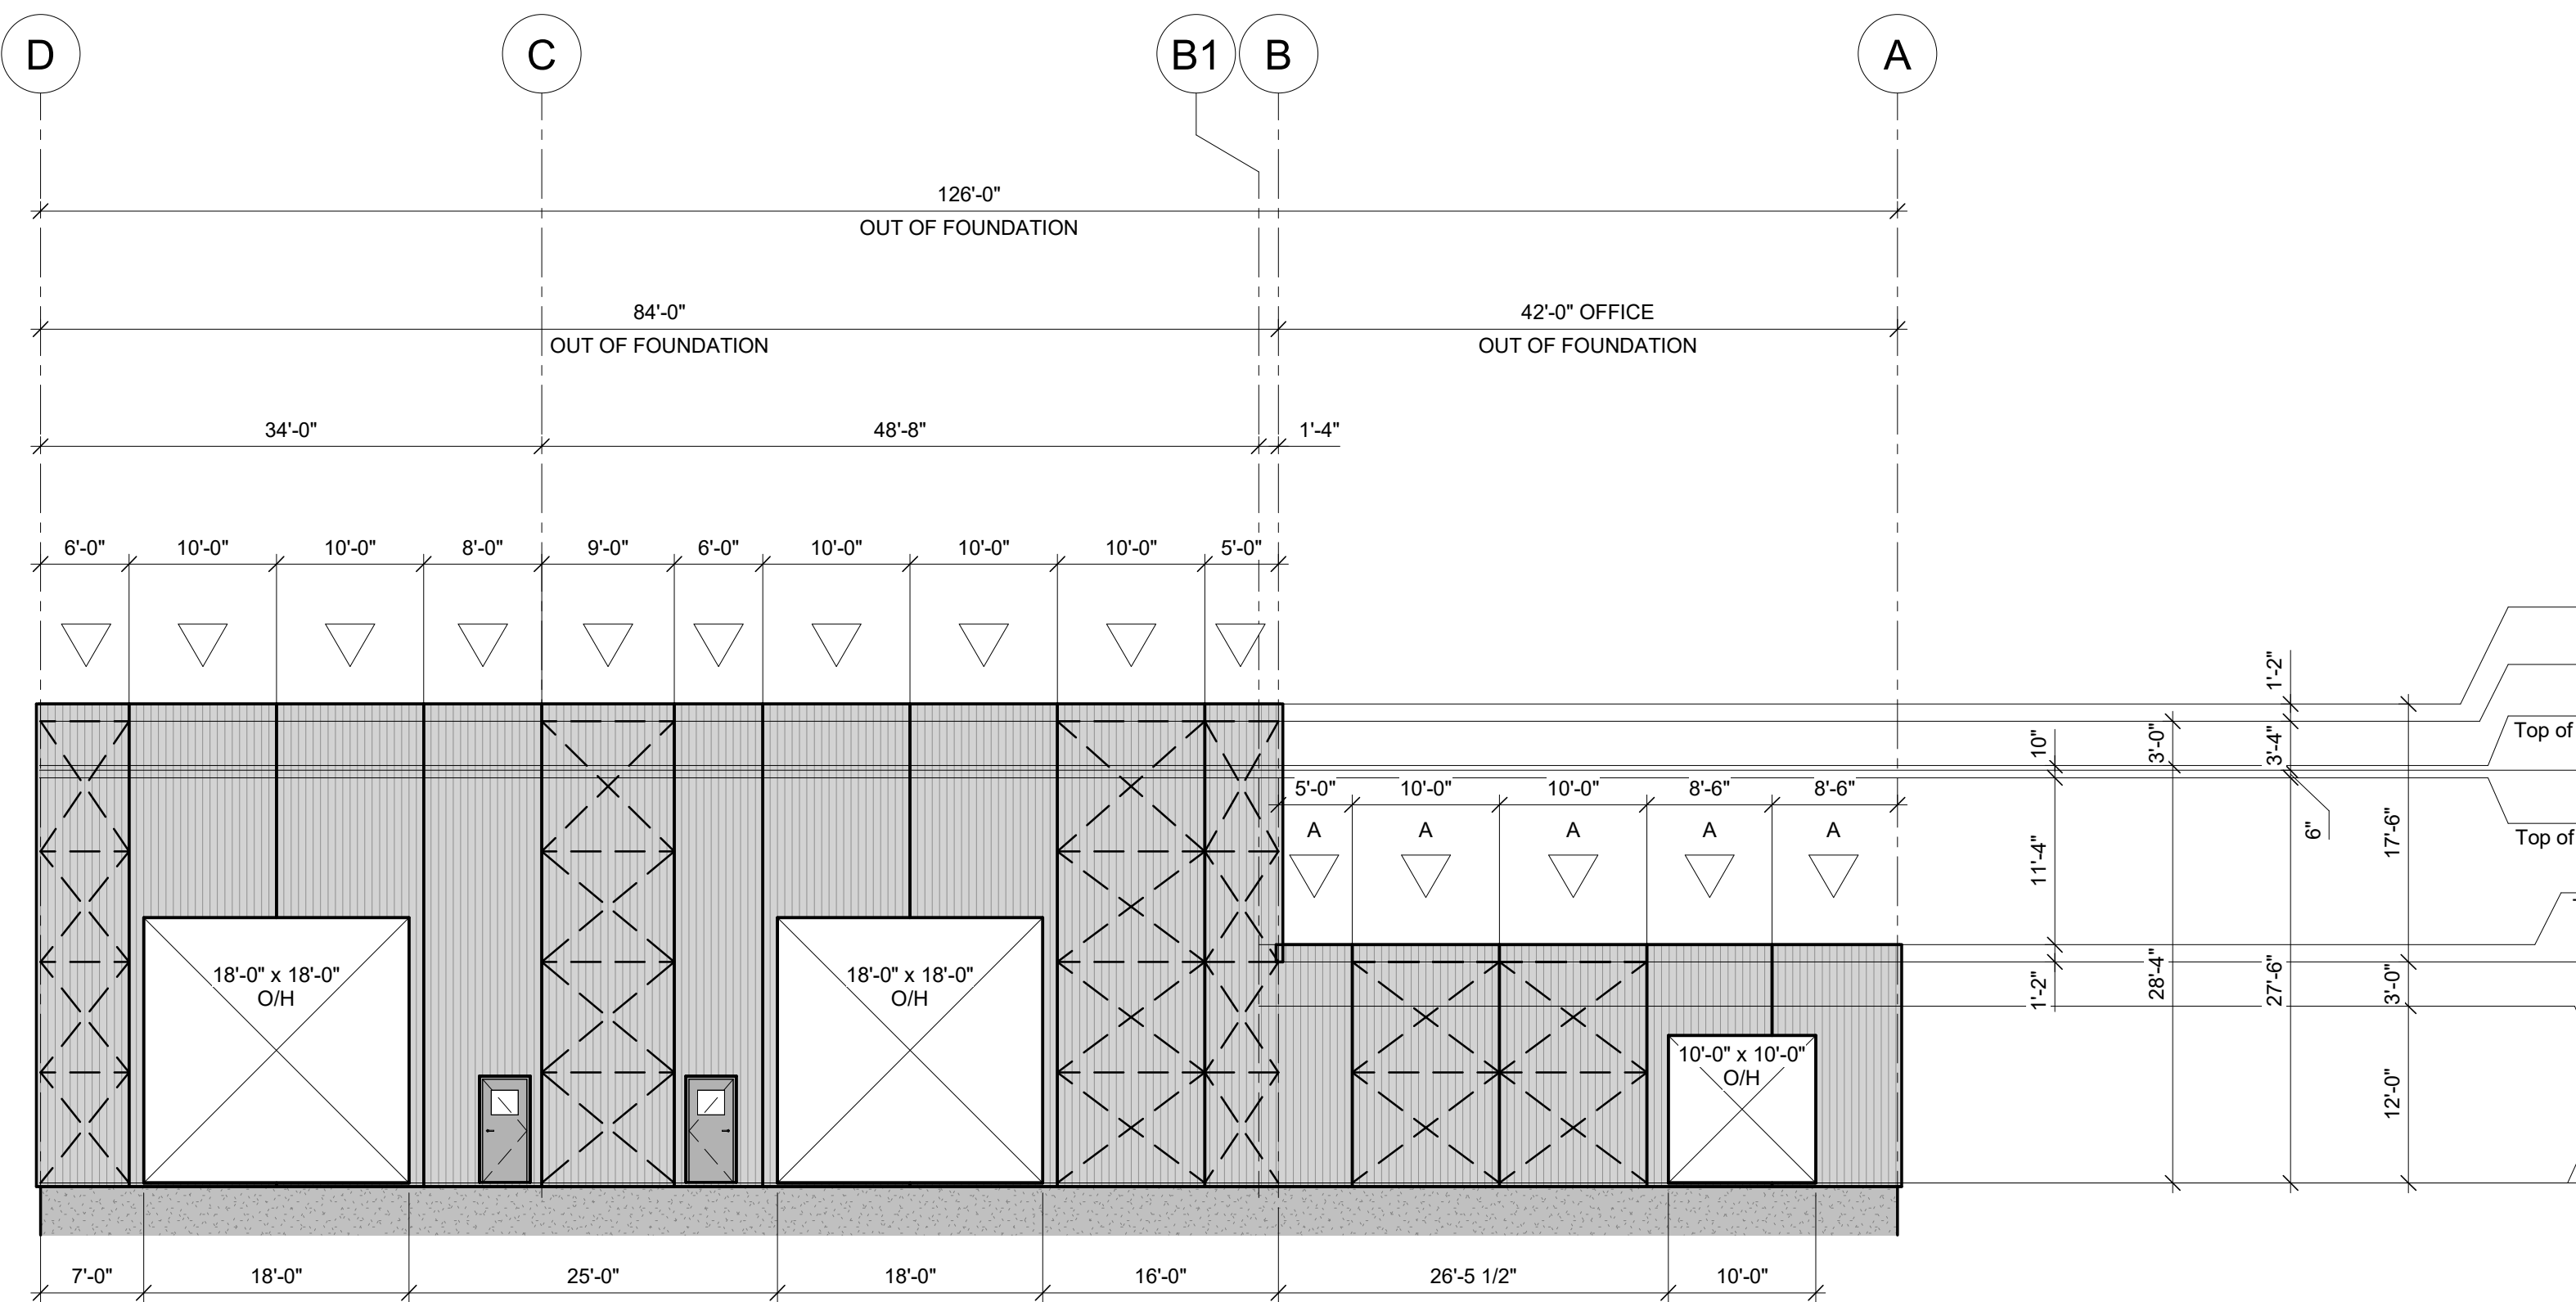


ELEVATION LINE 9 (NORTH)  
3/32" = 1'-0"

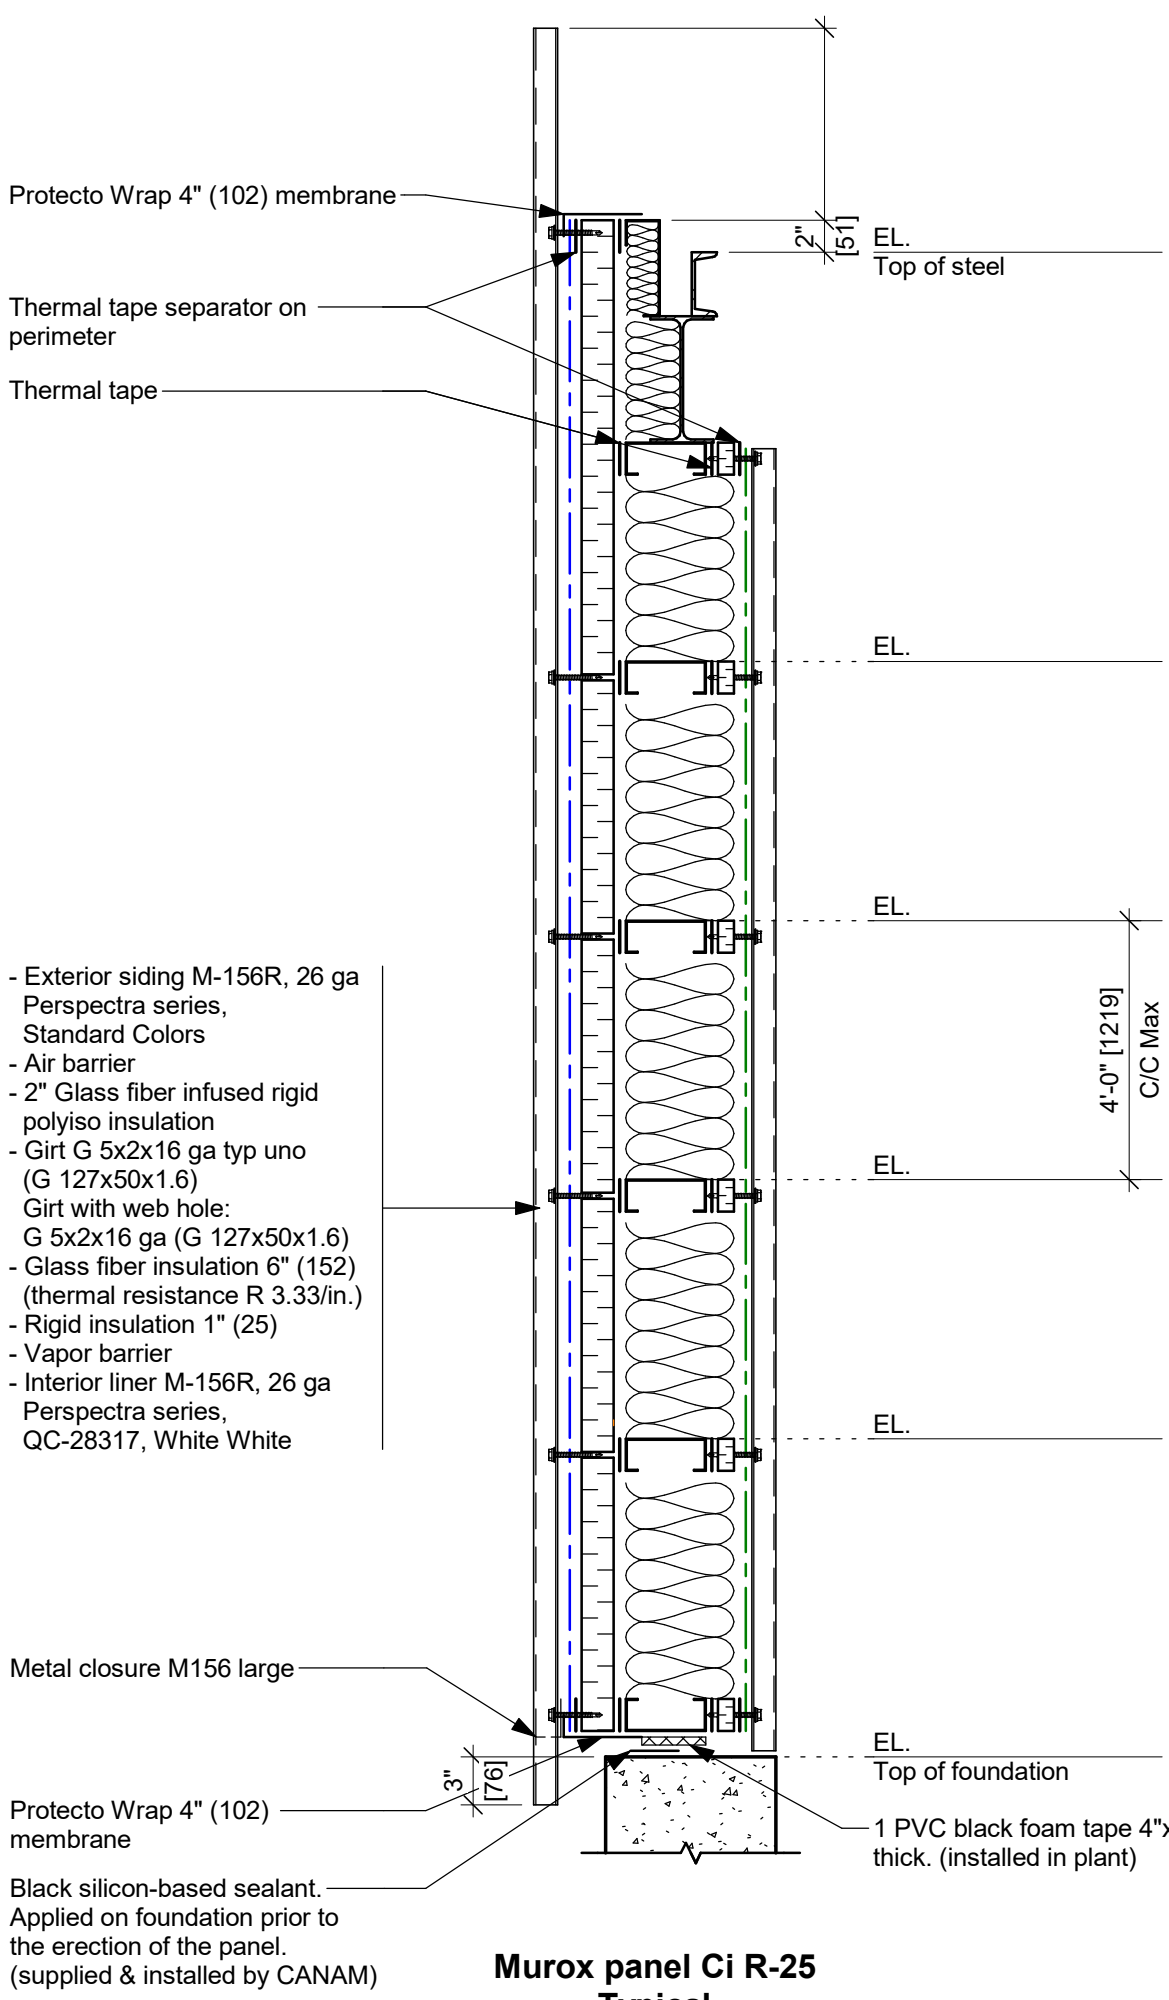

Murox panel CI R-25  
Typical

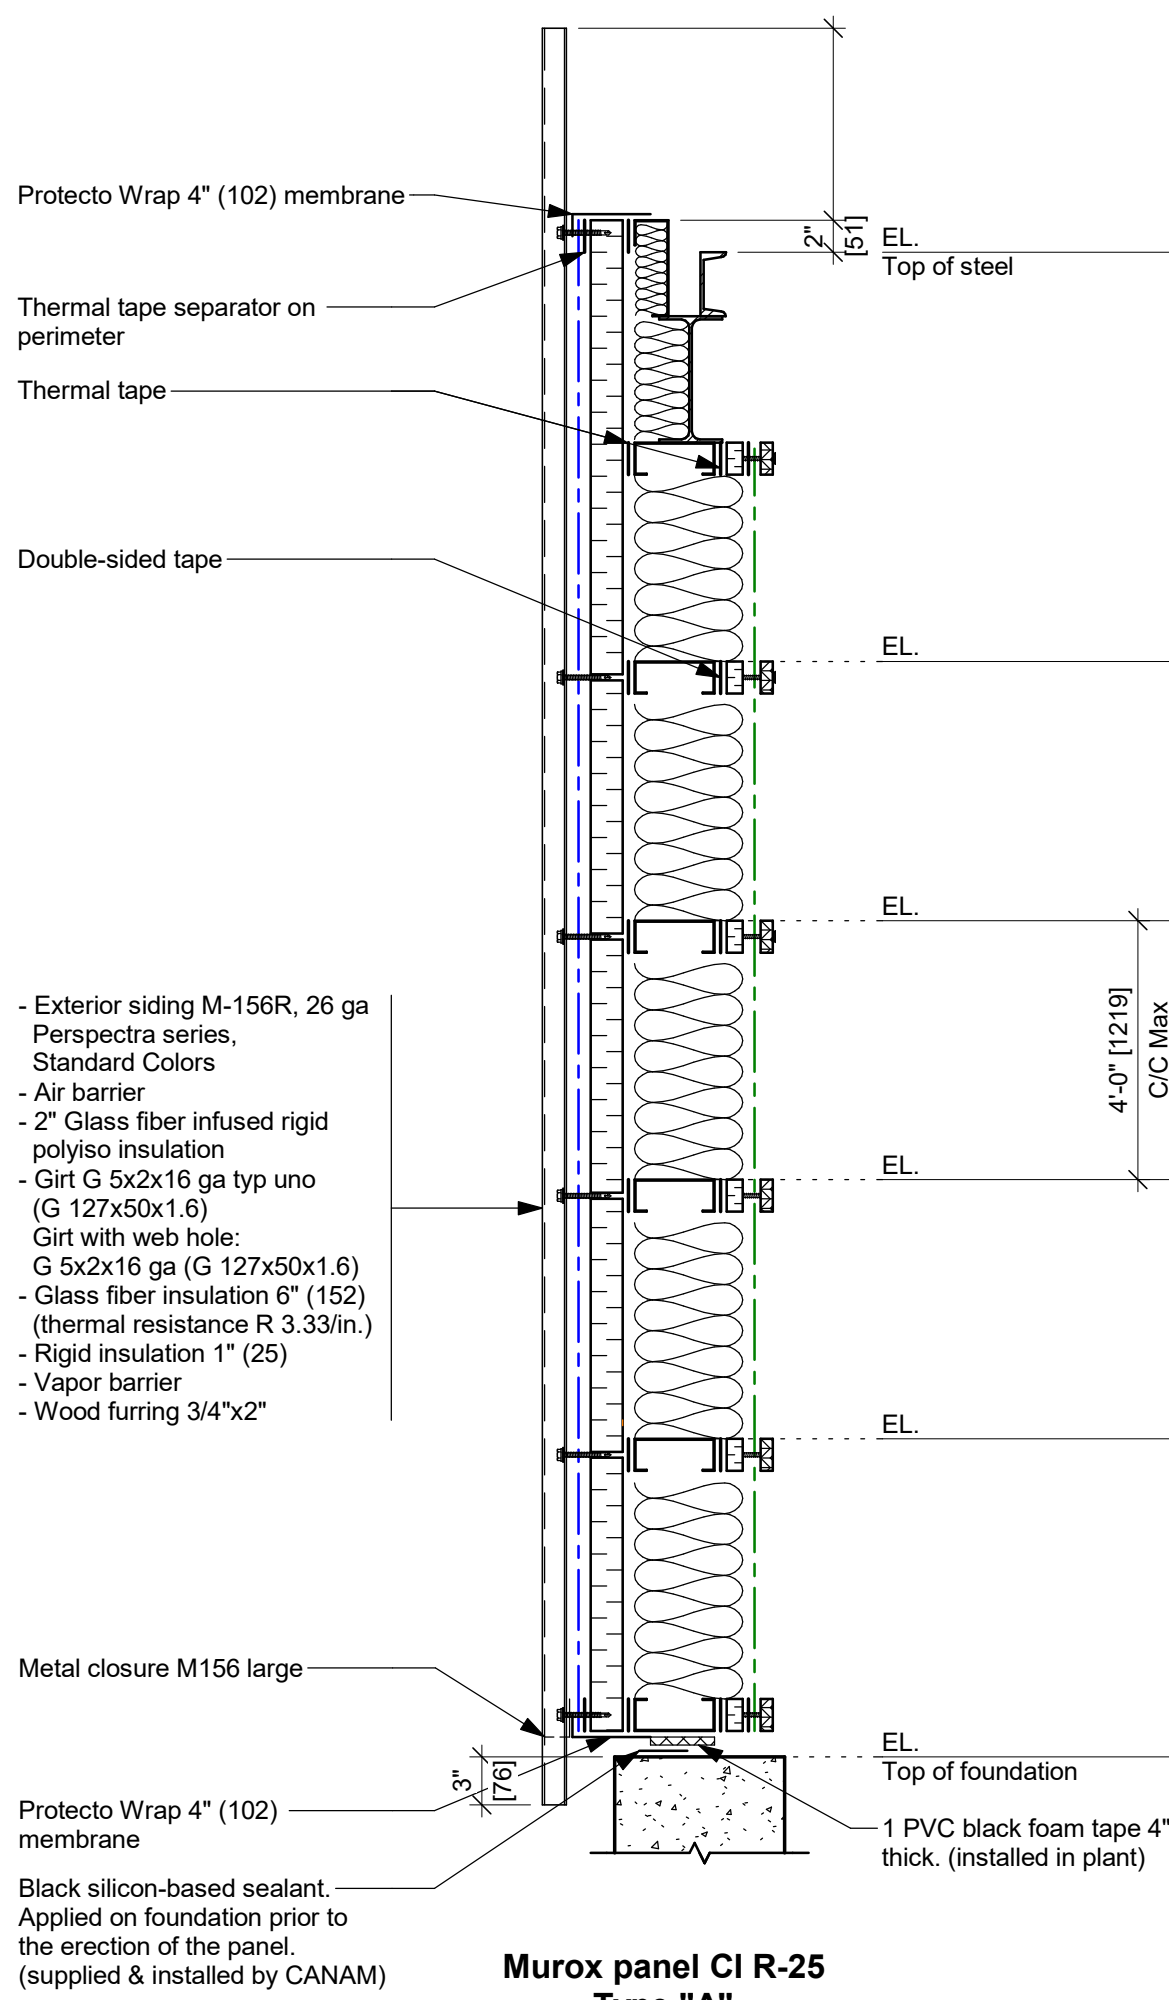

Murox panel CI R-25  
Type "A"

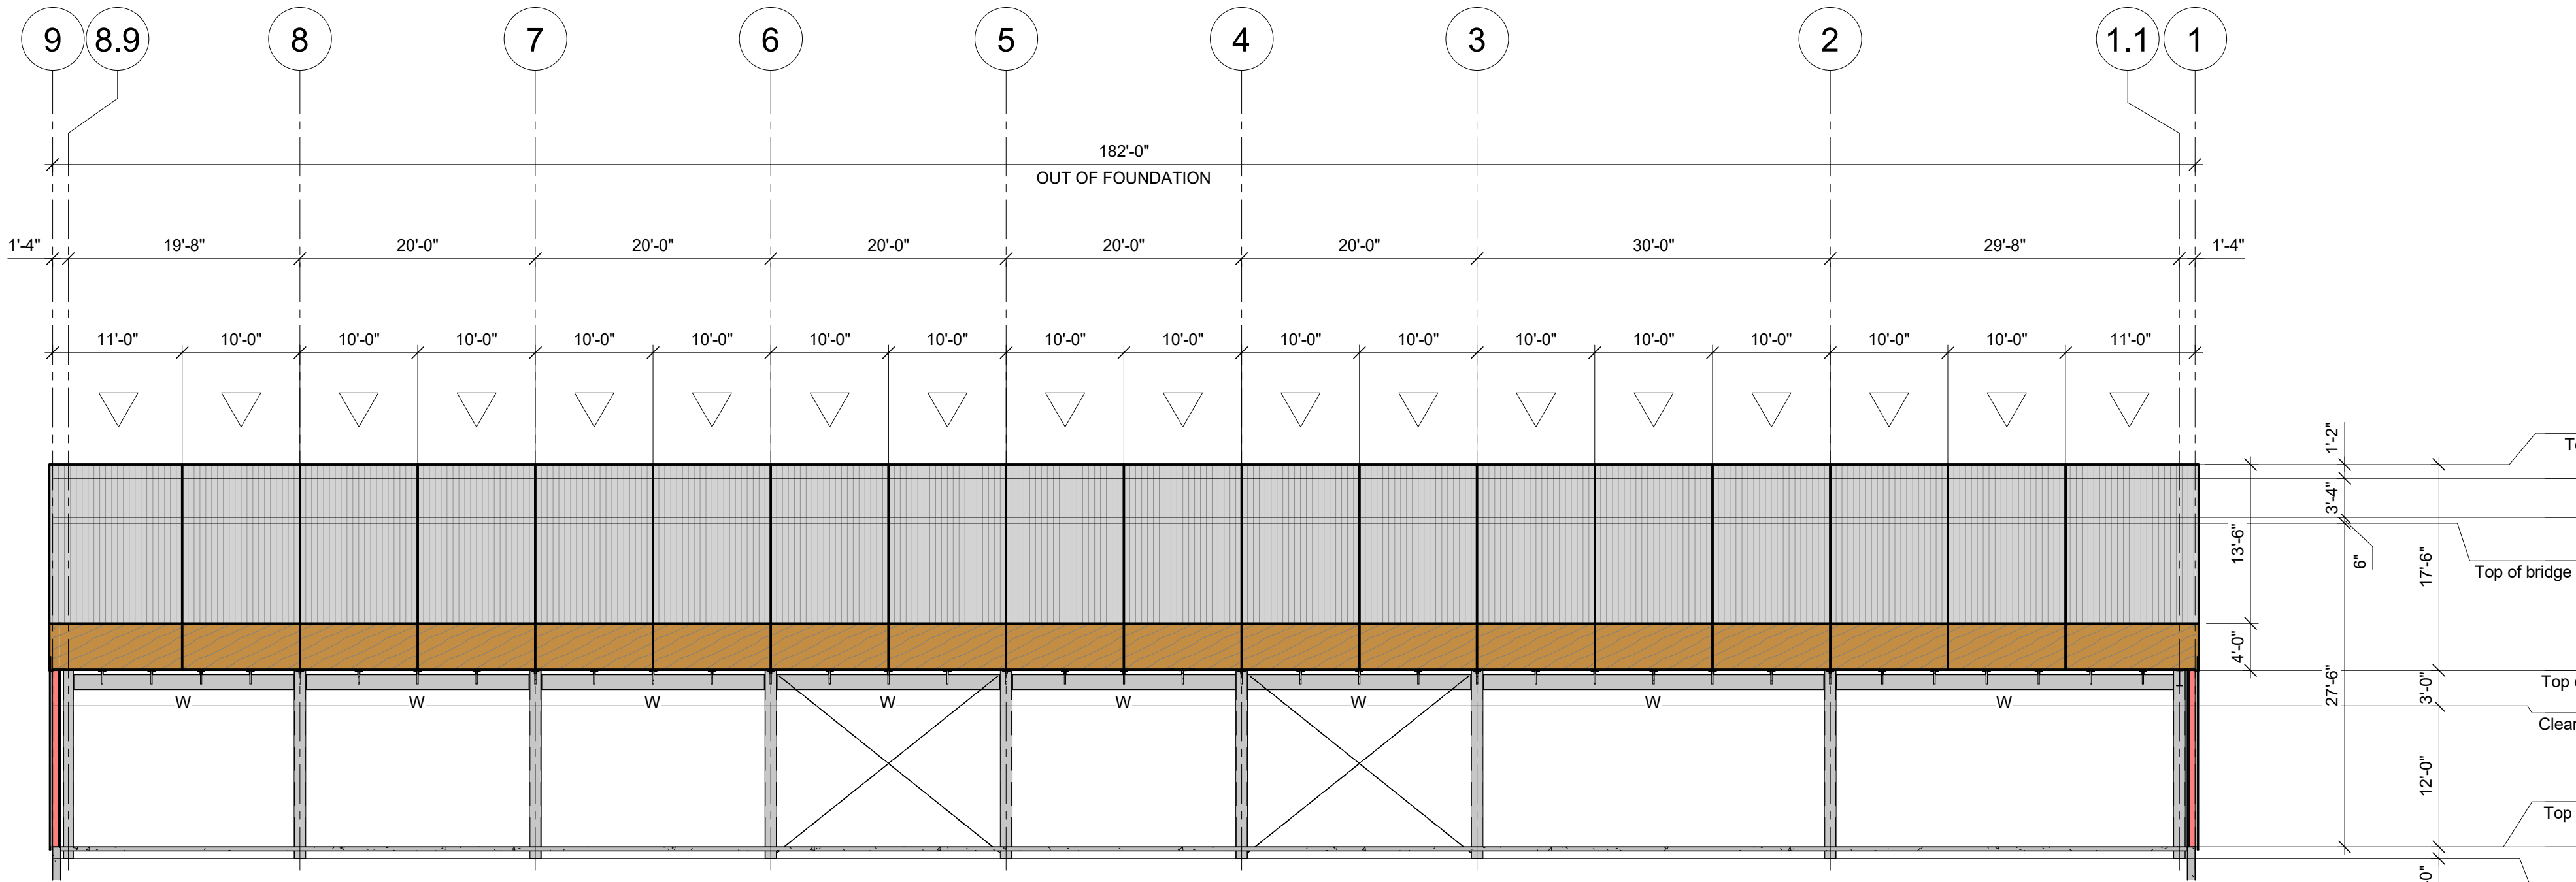

ELEVATION LINE B (WEST)  
3/32" = 1'-0"