

P2026-001 - BMG Shop



NOTE : ALL SERVICE LOADS ARE EXPRESSED IN Kips, TYP. U.N.

End of table															
JIB CRANES LOADS															
		VERTICAL LOADS				BRACINGS									C
col.		D	S	C	W	E		C			W				
ans						H(N/S)	H(E/W)	V.	H(N/S)	H(E/W)	V.	H(N/S)	H(E/W)	V.	H(E/W)
B.1	1.1	25.0	85.0	98.0	10.0										
B.1	2	45.0	130.0	74.0	17.0										#4 #28
B.1	3	37.0	105.0	70.0	15.0	#50		#62	#9		#14	#12		#16	#4 #28
B.1	4.5 & 6	30.0	85.0	67.0	12.0	#50		#62	#9		#14	#12		#16	#4 #28
B.1	7&8	30.0	85.0	67.0	12.0										#4 #28
B.1	8.9	24.0		44.0	7.0										
C	1.1	20.0	35.0	84.0	8.0										#4 #28
C	2	20.0	70.0	103.0	16.0										#4 #28
C	3	30.0	60.0	108.0	12.0										#4 #28
C	4 to 8	25.0	45.0	97.0	10.0										#4 #28
C	8.9	15.0	25.0	67.0	7.0										
1.1	(2 col. Added each side of the office door)	2.0	6.0	1.0		#20	#88					#6	#30		

P2026-001 - BMG Shop



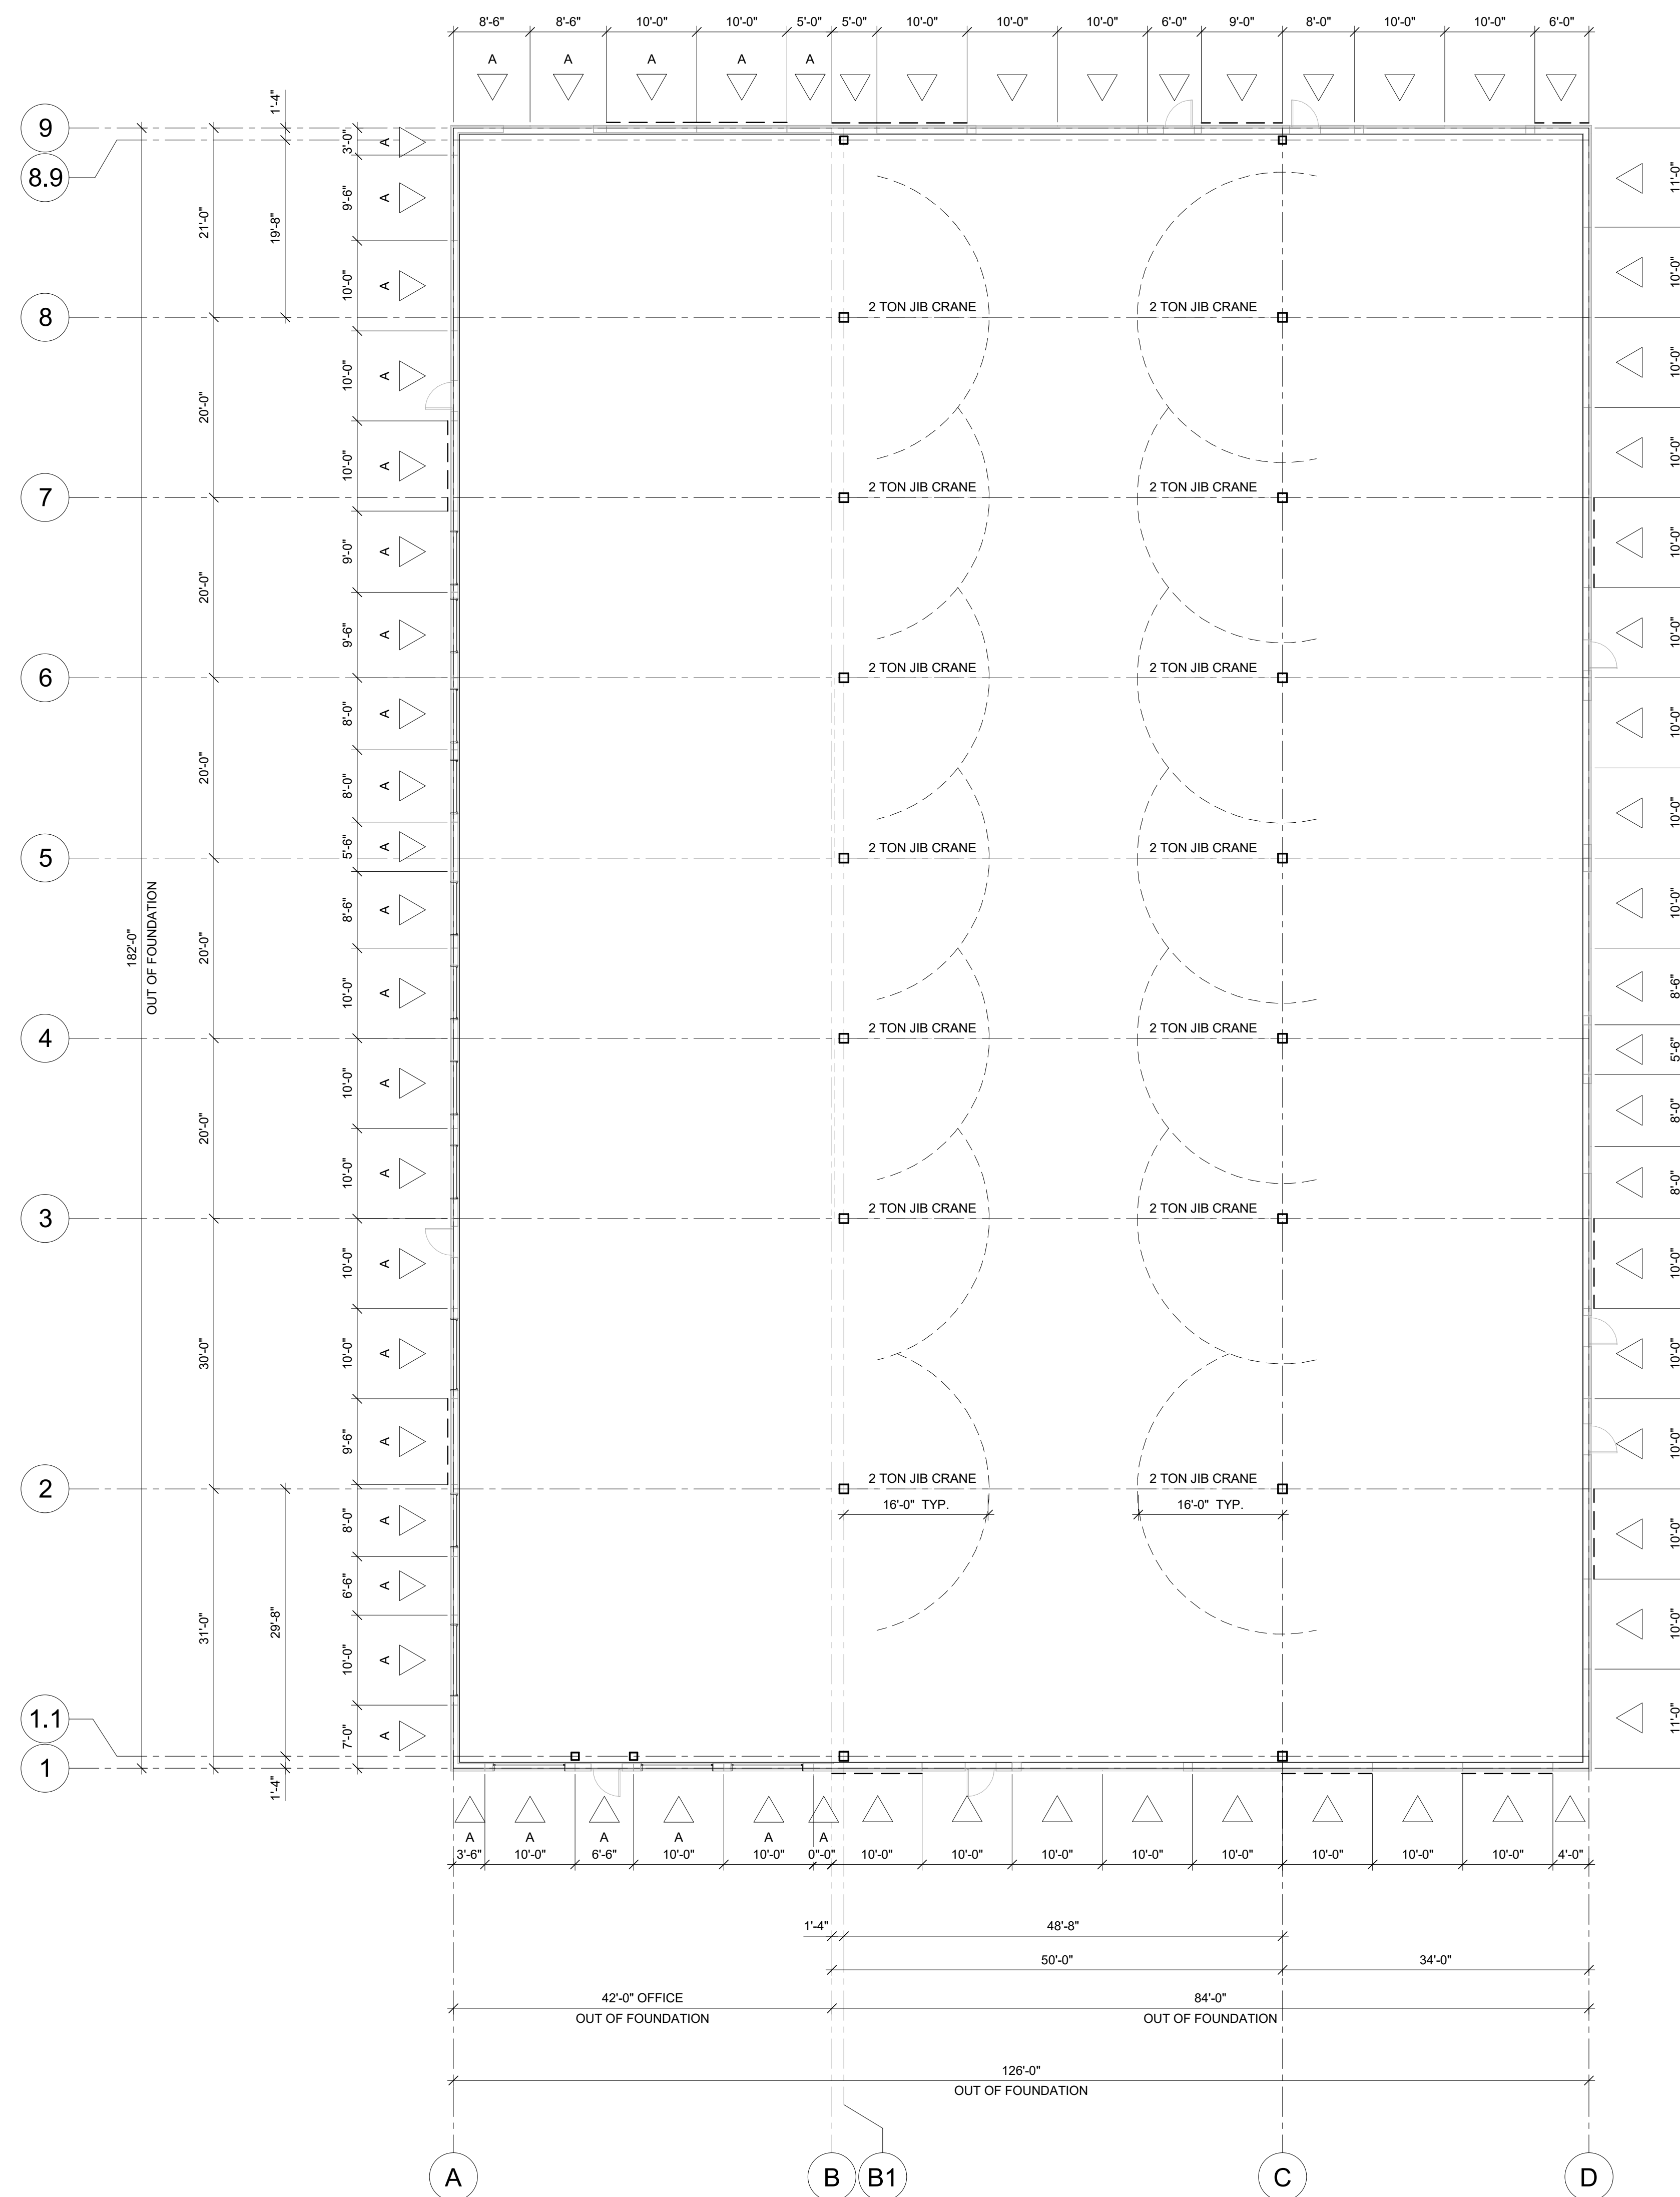
NOTE : ALL SERVICE LOADS ARE EXPRESSED IN Kips, TYP. U.N.

[illegible]

P2026-001 - BMG Shop



NOTE : ALL SERVICE LOADS ARE EXPRESSED IN Kips, TYP. U.N.

[illegible]

ANCHOR PLAN
3/32" = 1'-0"

NOTE:

All columns on line B & C will be designed to support a 2 ton jib crane, with a span of 16'-0", with the bracket attached to the columns at 6'-0"

CONTRACTOR/ERECTOR NOTE:

IT IS PROHIBITED TO MODIFY, COPY, REPRODUCE OR OTHERWISE
DISTRIBUTE THIS DRAWING OR ANY REPRESENTATION OF THIS
DRAWING, OR ANY MEDIA, INCLUDING ELECTRONIC, WITHOUT THE
PRIOR WRITTEN APPROVAL OF CANAM GROUP INC.

PRELIMINARY

NOT TO BE USED FOR CONSTRUCTION

REVISION	DATE	DESCRIPTION	DESS.	VER.
----------	------	-------------	-------	------

PROJECT MANAGER	-
	-
	-
	-
	-

DRAFTING:

DRAWN	DESIGNED	PROJECT ENGINEER	SCALE:
-------	----------	------------------	--------

INITIALE			$3/32^* = 1'-0^*$
----------	--	--	-------------------

CHECKED	CONSULTING ENGINEERS / ARCHITECTS	DATE (yyyy/mm/dd) :
---------	-----------------------------------	---------------------

		2028/01/09
--	--	------------



11505, 1re Avenue, bureau 500, Saint-Georges Beauce
Quebec, Canada, G5Y 7X3
Phone : (418) 228-8031
Toll free : (877) 499-6049
www.canam.com

PROFESSIONAL SEAL

PROJECT	
---------	--

BMG Shop
Chelmsford, Ontario

DRAWING TITLE

PRELIMINARY SKETCH - ANCHOR PLAN

Initials

CONTRACT NUMBER 00000-000	DRAWING NUMBER	DIVISION	REVISION 0
------------------------------	----------------	----------	---------------

EsM γ 101	Δ
------------------	----------