

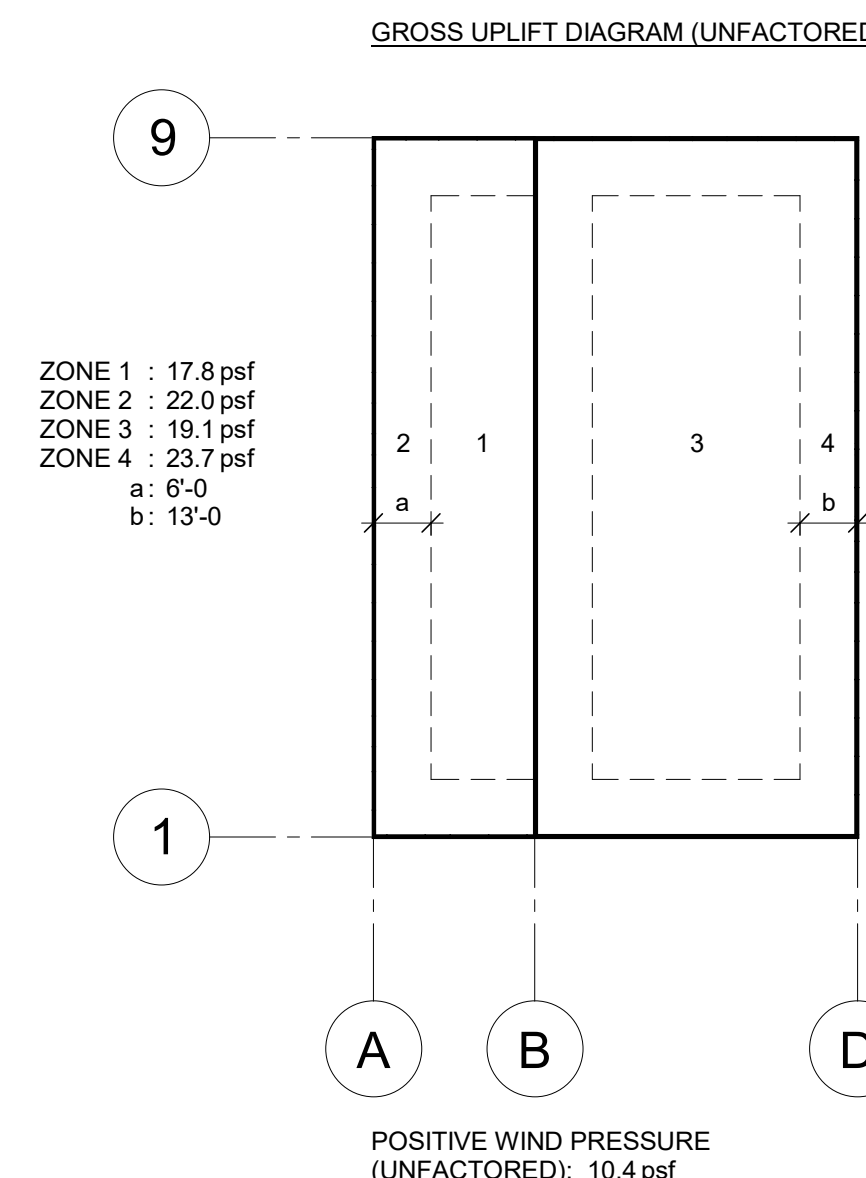
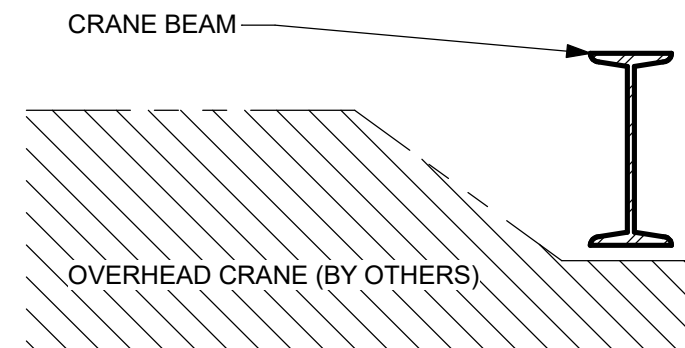
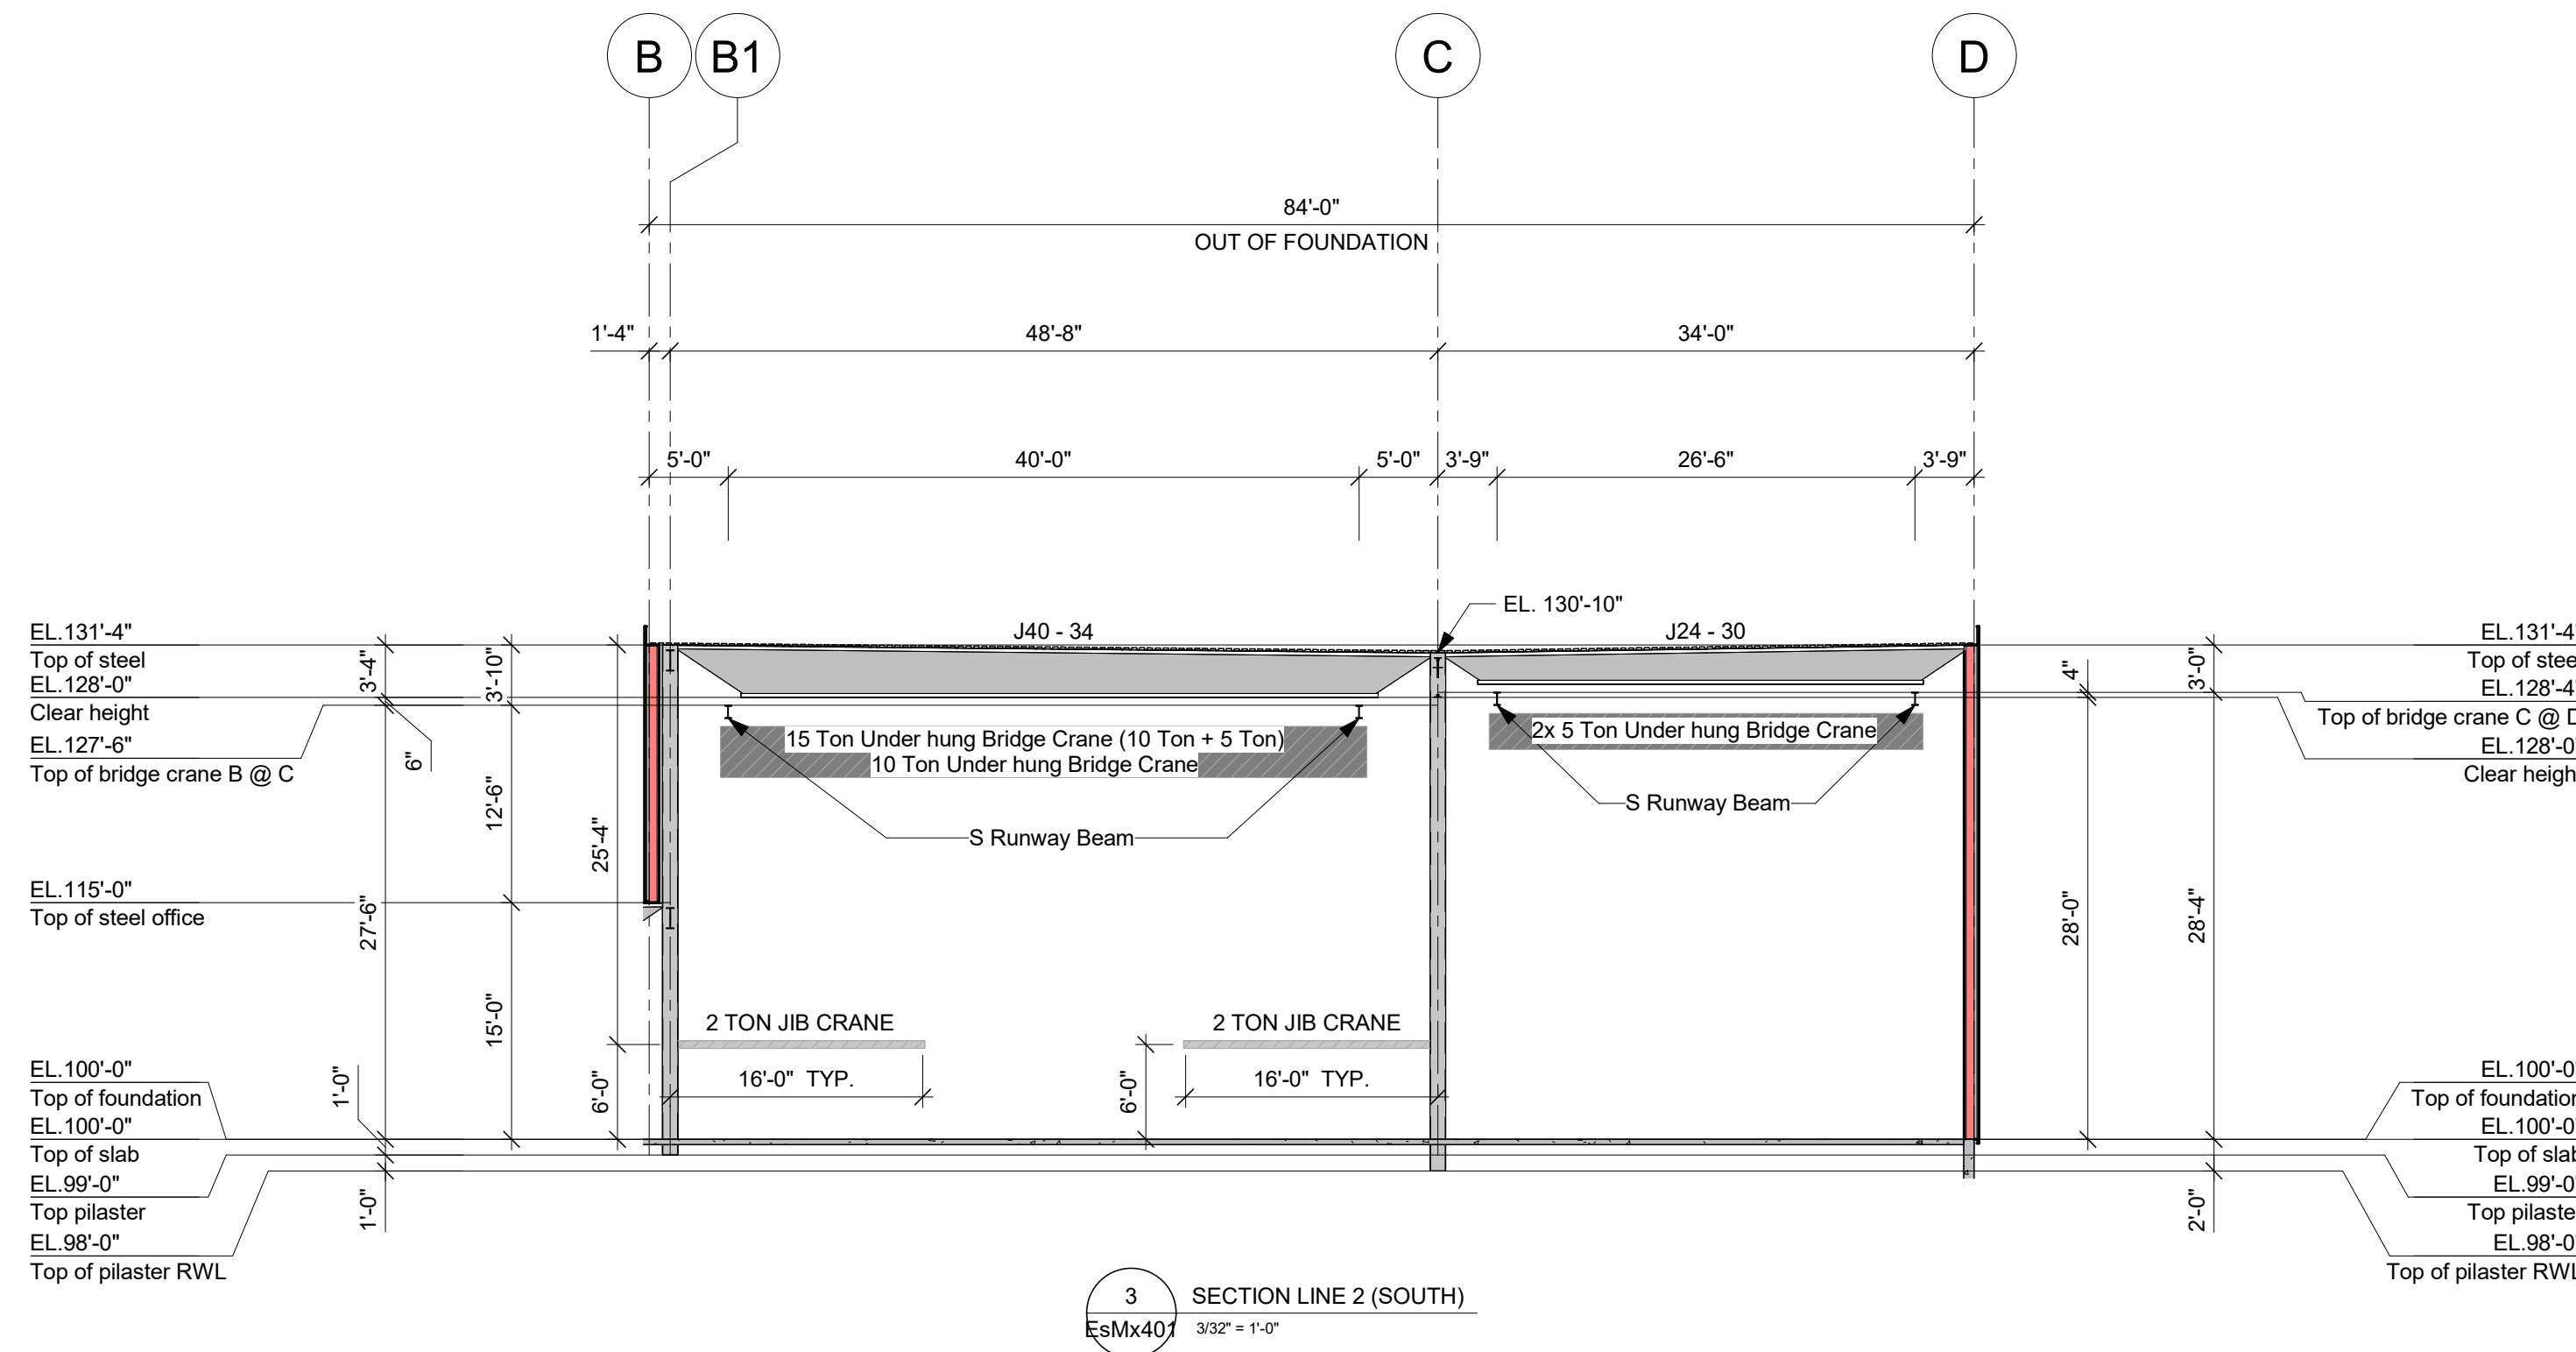


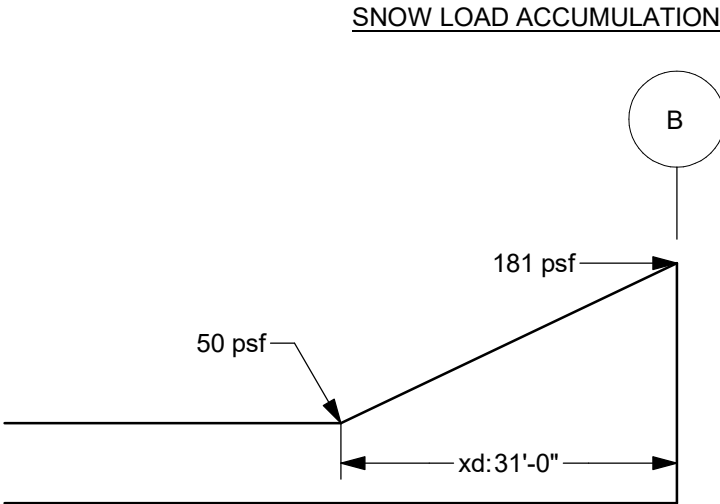

ERECTOR NORTH

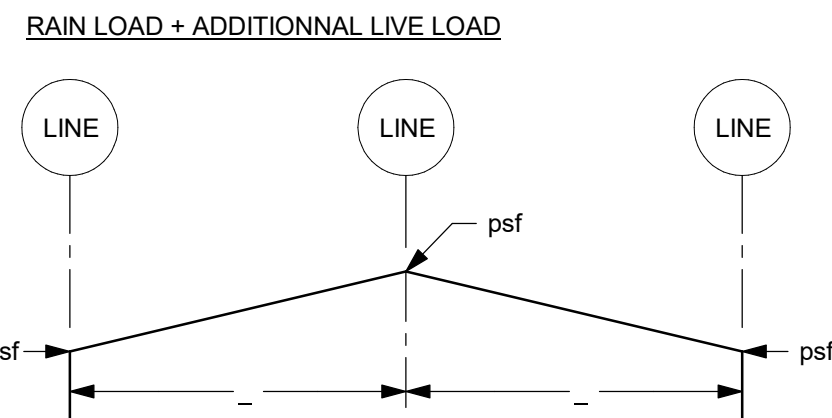


CONTRACTOR/RECTOR NOTE:
IT IS PROHIBITED TO MODIFY, COPY, REPRODUCE OR OTHERWISE DISTRIBUTE THIS DRAWING OR ANY REPRESENTATION OF THIS DRAWING, OR ANY MEDIA, INCLUDING ELECTRONIC, WITHOUT THE PRIOR WRITTEN APPROVAL OF CANAM GROUP INC.

ROOF
TOP OF PLASTER RWL : 98'-0"
TOP OF PLASTER : 99'-0"
TOP OF SLAB : 100'-0"
TOP OF FOUNDATION : 100'-0"
CLEAR HEIGHT : 28'-0"
TOP OF STEEL : 131'-4"
PARAPET HEIGHT : 1'-2"
TOP OF PARAPET : 132'-4"

ROOF OFFICE
TOP OF PLASTER RWL : 98'-0"
TOP OF PLASTER : 99'-0"
TOP OF SLAB : 100'-0"
TOP OF FOUNDATION : 100'-0"
CLEAR HEIGHT : 12'-0"
TOP OF STEEL : 119'-0"
PARAPET HEIGHT : 1'-2"
TOP OF PARAPET : 119'-2"


LOADS
D.L. : 18.0 psf
C.O.L. : 5.0 psf
Ss : 52.23 psf
Sr : 8.36 psf
Cb + Cw : 0.8
Roof L.L. : 0.0 psf
Lr : 1.0
Roof snow load : 50.1 psf
W : 1.0
Wind q : 1/50 : 9.4 psf
Seismic (Site class: E (Assumed))
Is : 1.0
Ss (0.2) : 0.250
Ss (0.5) : 0.254
Ss (1.0) : 0.175
Ss (2.0) : 0.0844
Ss (5.0) : 0.0221
Ss (10.0) : 0.0068
PCA : 0.145
PGV : 0.176

LOADINGS:
• Roof dead load excluding collateral load : 18.0 psf
• Collateral load : 5.0 psf (includes lighting and/or mechanical and sprinklers for
• Roof snow load : 50.1 psf
• Wind load q 1/50 : 9.4 psf
• Roof live load : 0.0 psf
• Ground snow load : Ss = 52.23 psf
• Risk Category : Ss = 8.36 psf
• Snow load factors : Cb = 0.8
• Cw = 1.0
• Code Applicable : National building Code of Canada
Ontario Building Code, latest adopted editions
Code of Standard Practice CISC.
• Assumed soil site class: E
• NOTE:
1. E, however, the seismic site class is determined to be E or F according to the geotechnical report, the preliminary structural concept (location and geometry of bracings, etc.) must be validated and coordinated by a Canam's engineer.

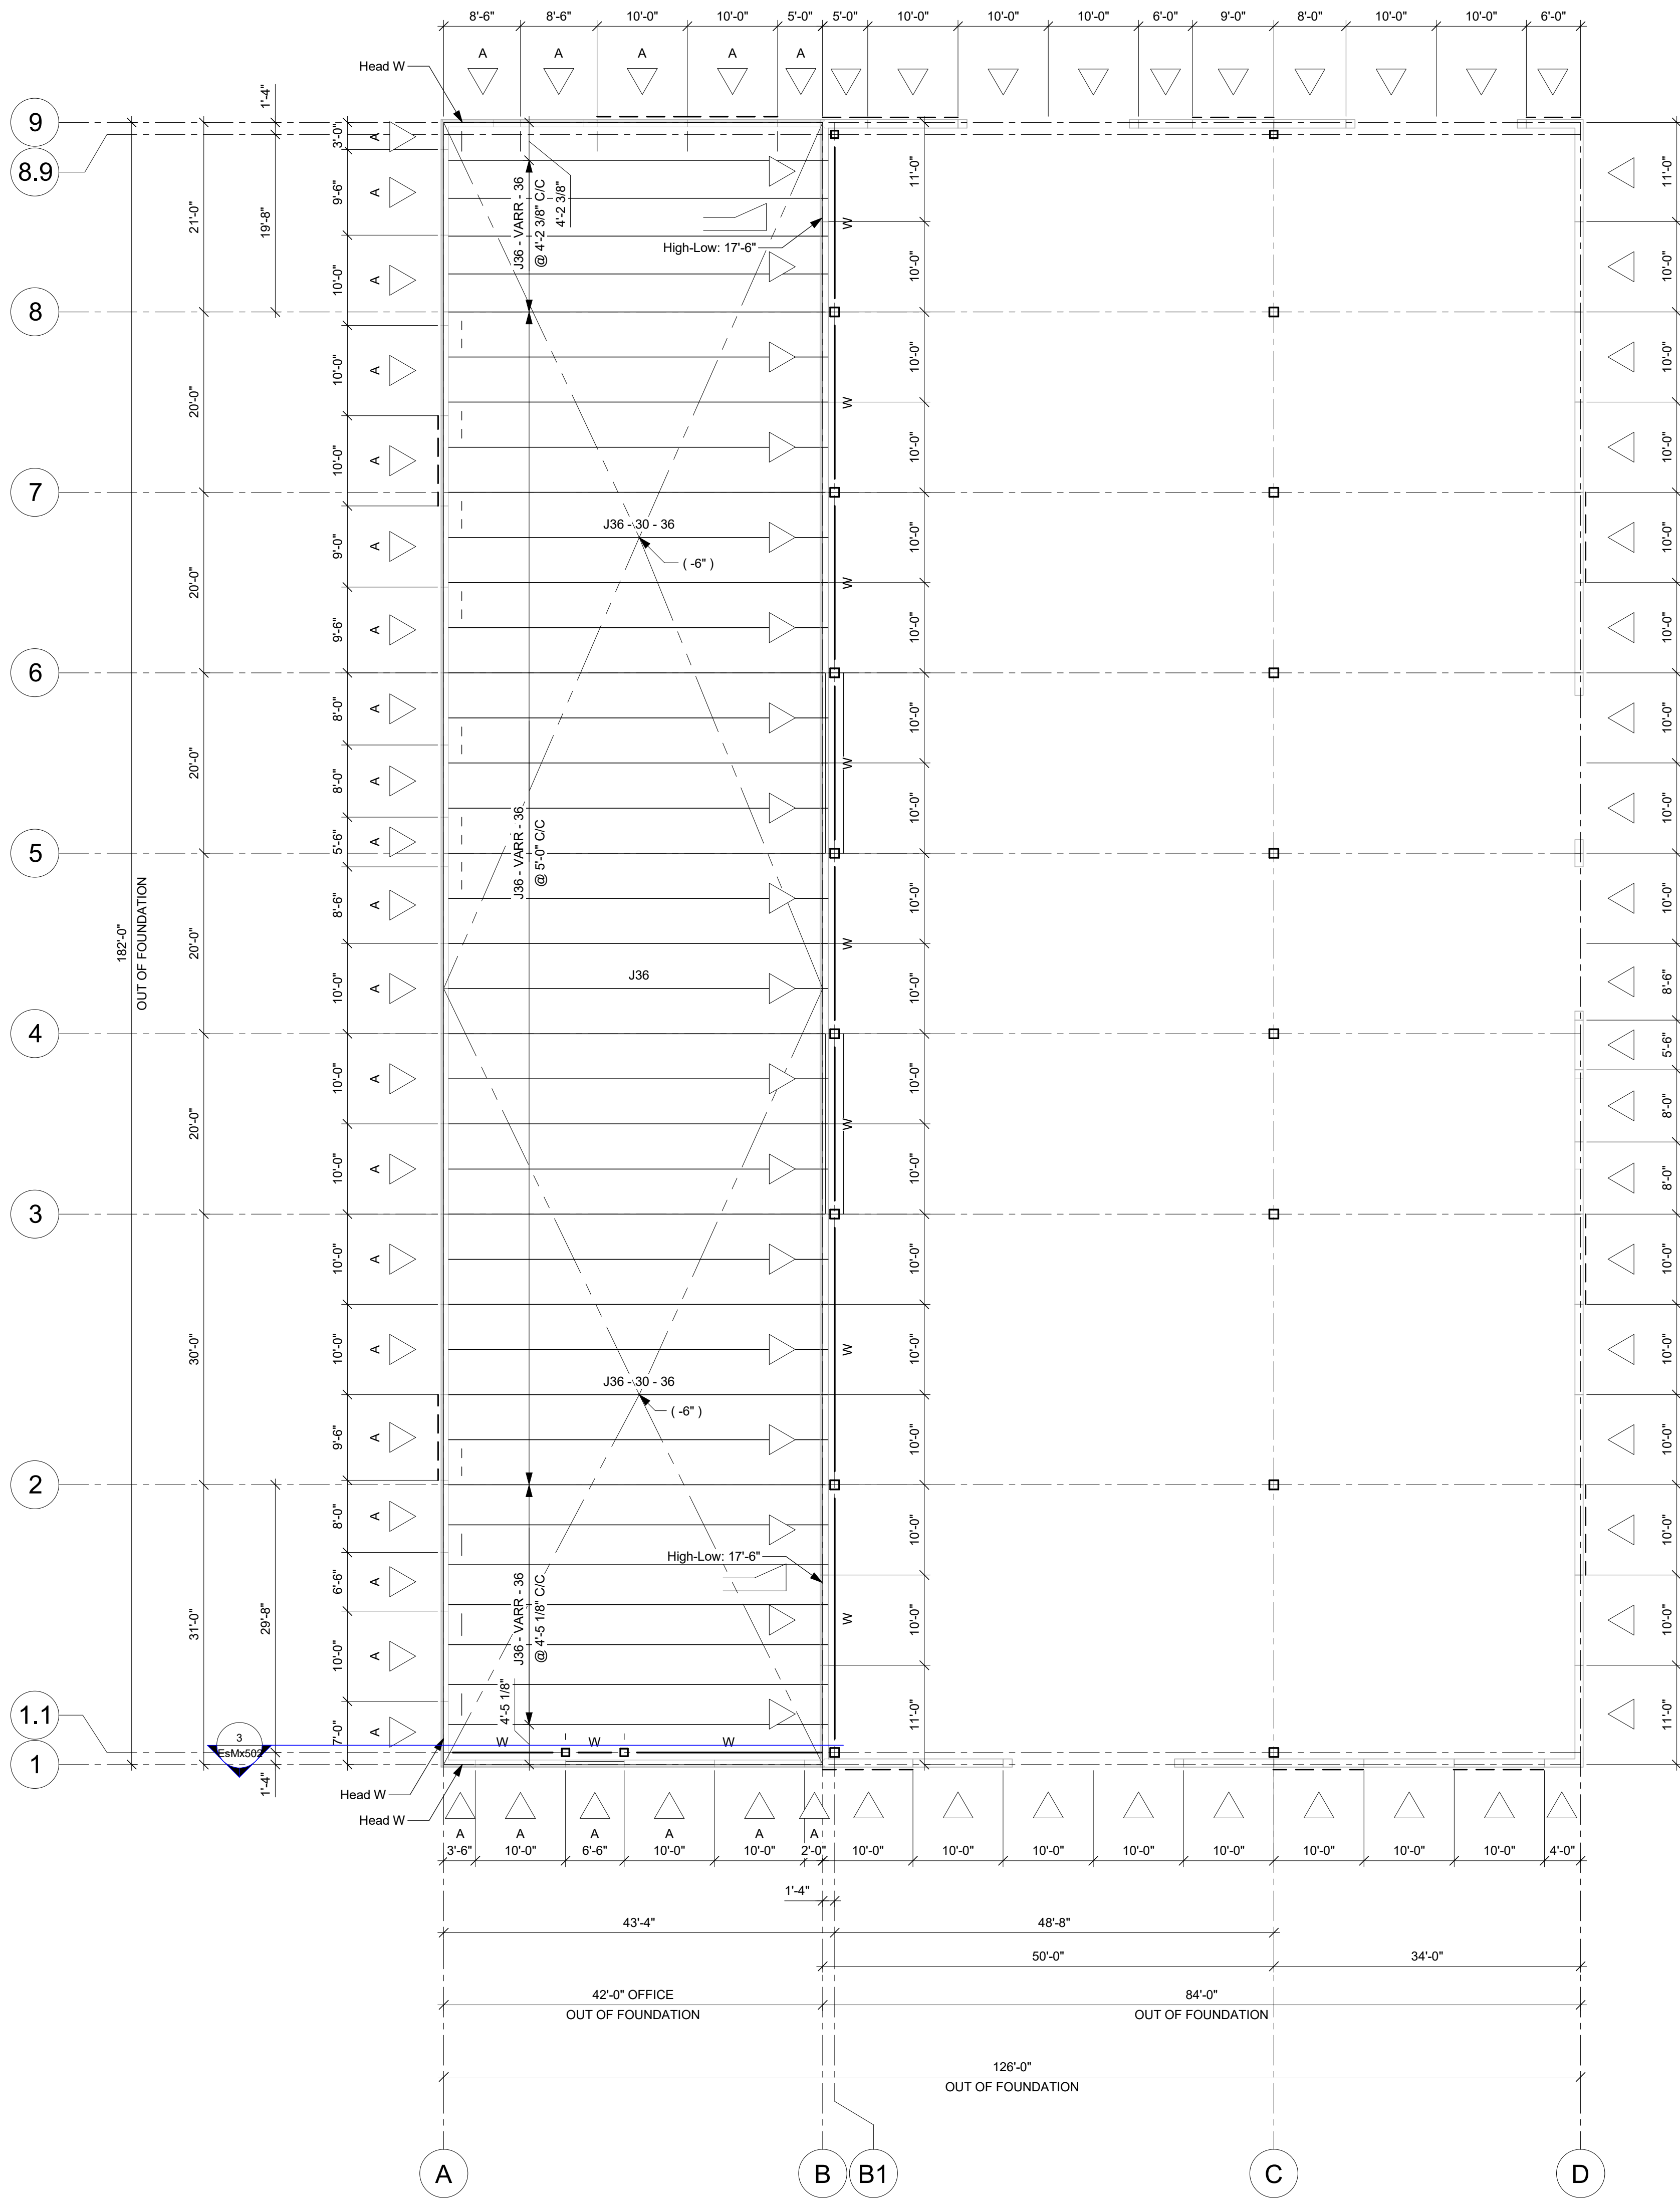

CRANE BEAM LOADS				
CAPACITY	CRANE WEIGHT	HOIST	MAX. WHEEL LOAD	WHEELS SPACING
5 Ton	2788 lb	900 lb	8.40 kip	6'-6 3/4"
5 Ton	2788 lb	900 lb	8.40 kip	6'-6 3/4"
10 Ton	9361 lb	1400 lb	17.70 kip	7'-8 1/2"
15 Ton (10 + 5)	9813 lb	2280 lb	18.30 kip	8'-2 3/8"

NOTE:
• The 10 ton and 5 ton cranes if the 15 ton cannot be used at the same time.
• No distance limitation between cranes.

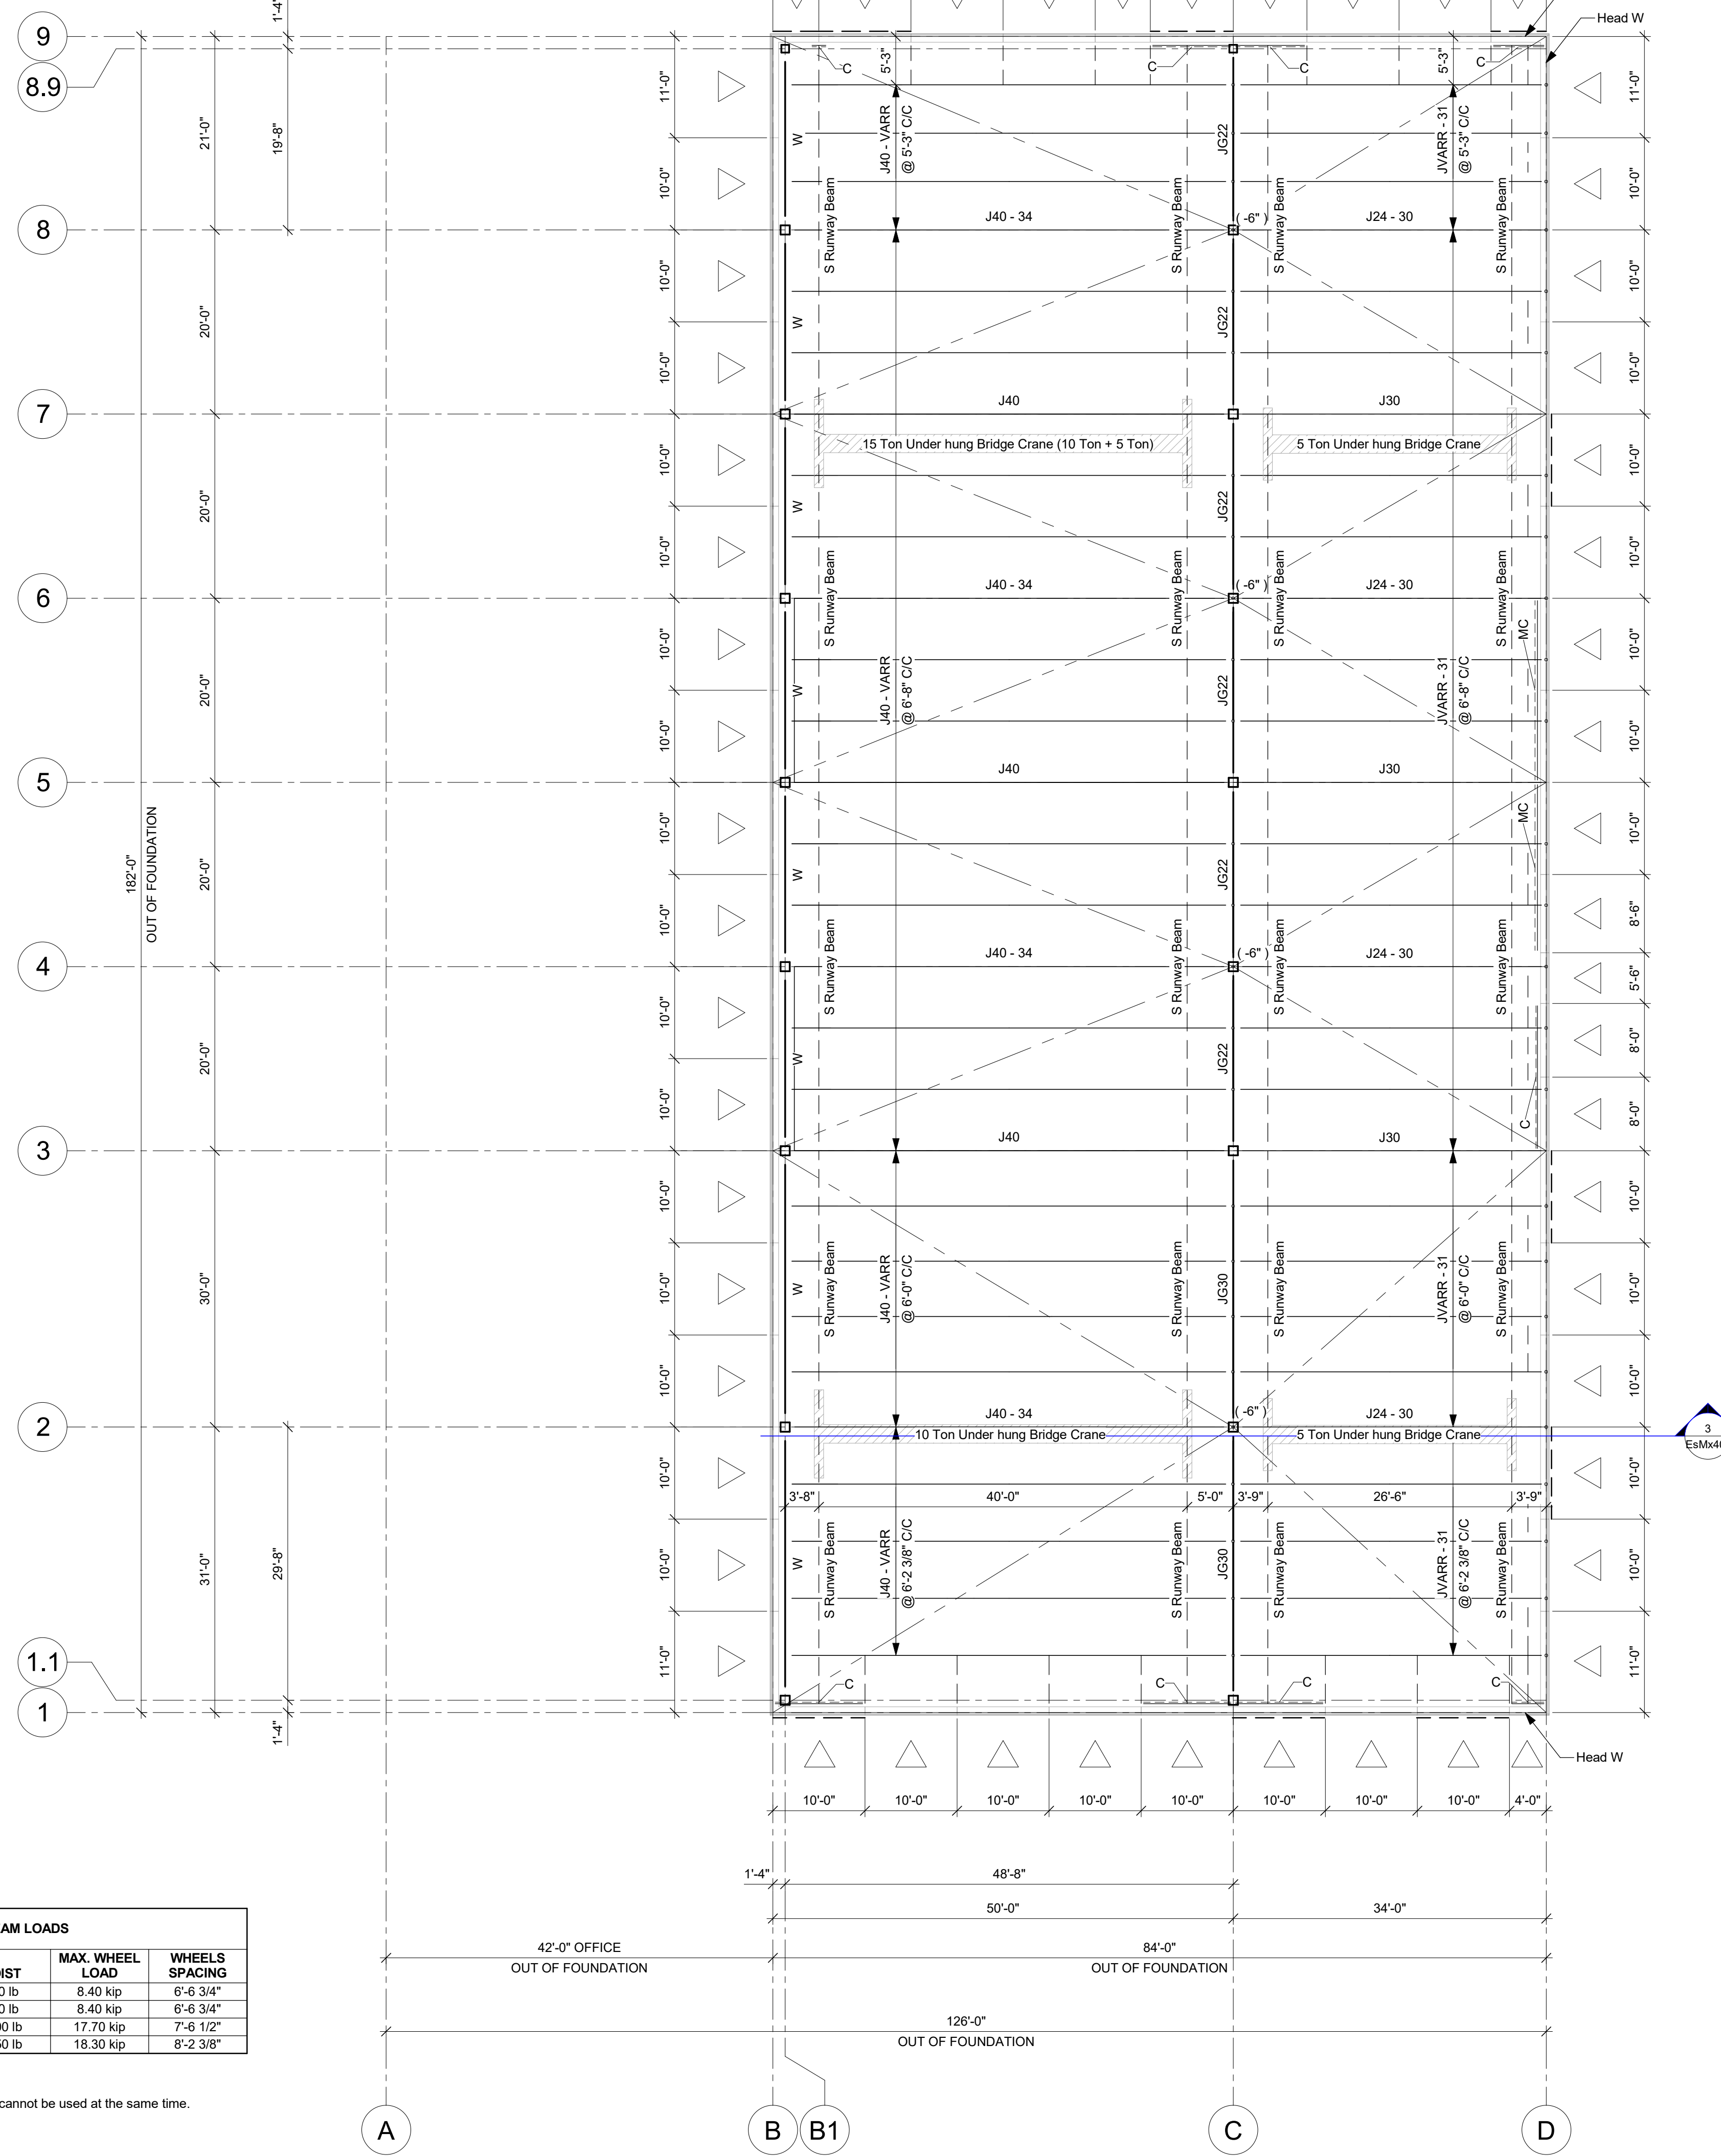

PRELIMINARY
NOT TO BE USED FOR CONSTRUCTION

REVISION	DATE	DESCRIPTION	USER	VER
1				
2				
PROFESSIONAL SEAL
PROJECT
BGM Shop
Chelmsford, Ontario

CONTRACT NUMBER: P2026-001
DRAWING NUMBER: EsMx401
DIVISION: 1
REVISION: 1

PRELIMINARY SKETCH - ROOF PLAN

Initials