



DOOR SCHEDULE																					
Identity	Qty	Installation	Door 18 ga.		Glass		Hardware								Remarks						
			Insulation (R12)	Dimensions 3'-0" x 7'-0"	Swing side	Width 1'-10"	Height 1'-8"	Steel frame 16 ga with thermal break	(3) Hinges non-rising removable pin	Door lock & latch set	Panic bar without outside trim 22EO	Panic bar with outside trim 23OL	Surface bolt inactive door	Threshold		Astragal for inactive door	Door closer	Door chain stop	Weatherstrip	Head cap	
D1																					

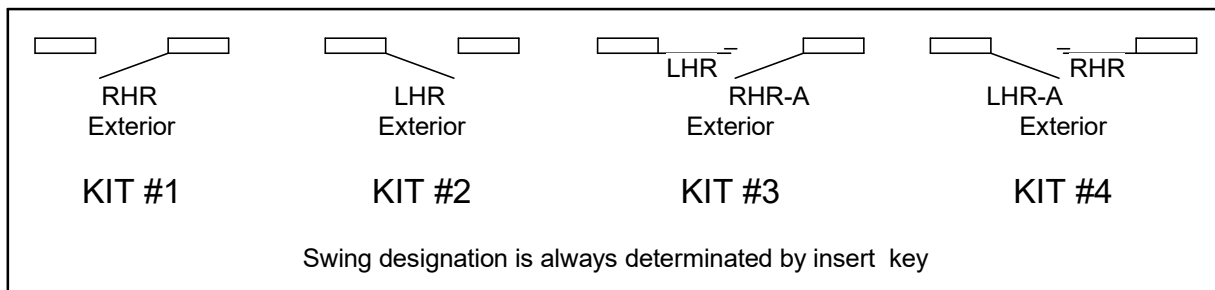

Supplier's standard hardware:
- Hinges: Stanley FB8179 4.5" x 4"
- Exit device: Von Duprin 22 x 689 with outside trim 23OL
- Permanent cylinder: Schlage 2000IC 626
- Door closure: LCN 1201 689
- Head and jamb seal: Unique 1650
- Bottom seal: Unique DS4
- Threshold: See the remarks in "Door schedule"


OH & OPENING SCHEDULE			
Total	Type	Tag	Remarks
2	10'-0" x 10'-0"	O/H	
2	16'-0" x 16'-0"	O/H	
3	16'-0" x 16'-0"	O/H	
Total general: 7			

WINDOW SCHEDULE				
Identity	Qty.	Installation	Description	Remarks
W1	5		Fixed aluminum window with thermal break and sealed glass + Low-E argon clear	Aluminum Frame (no color)
W2	9		Fixed aluminum window with thermal break and sealed glass + Low-E argon clear	Aluminum Frame (no color)

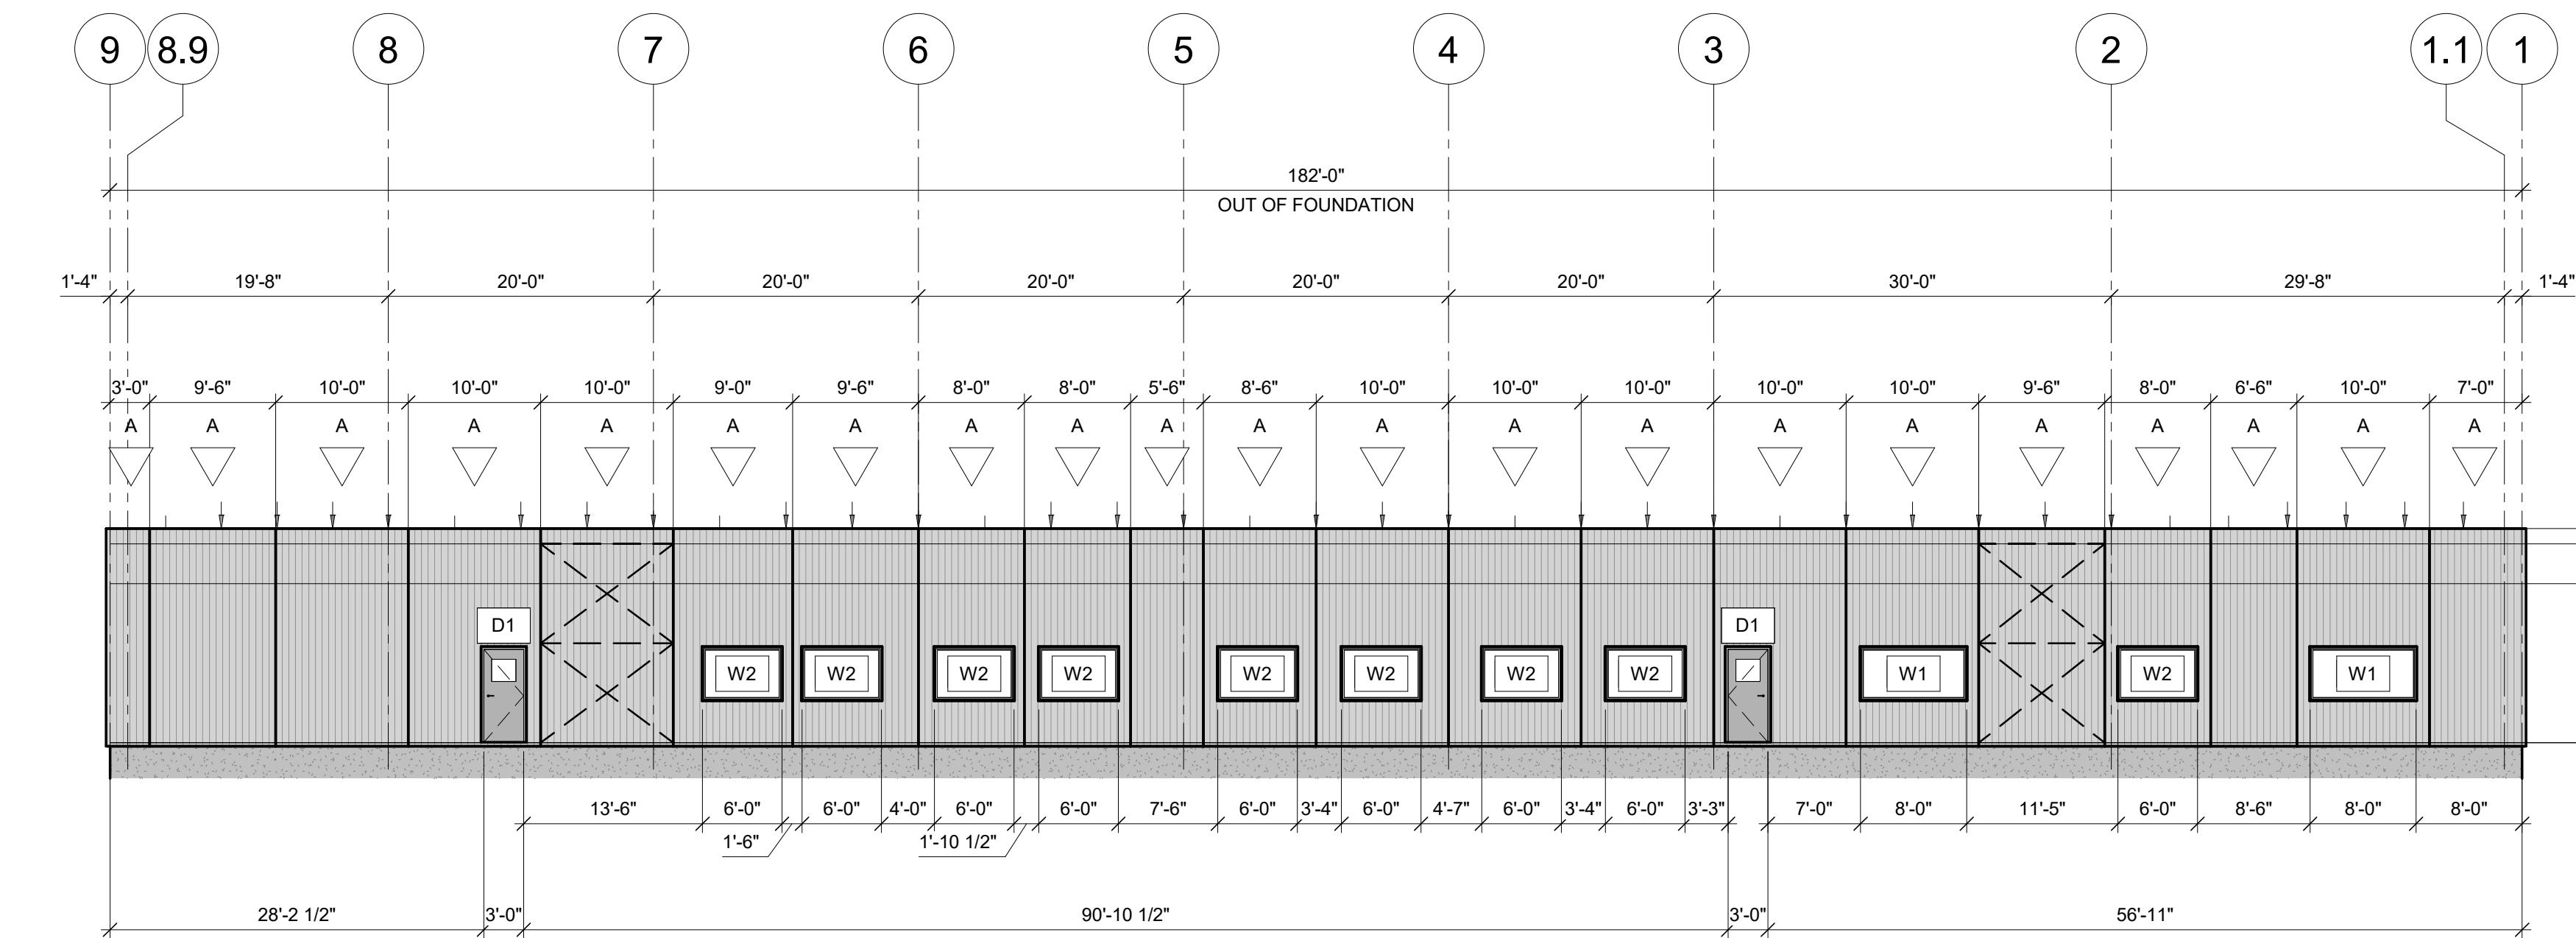


ELEVATION LINE A (WEST)

3/32" = 1'-0"

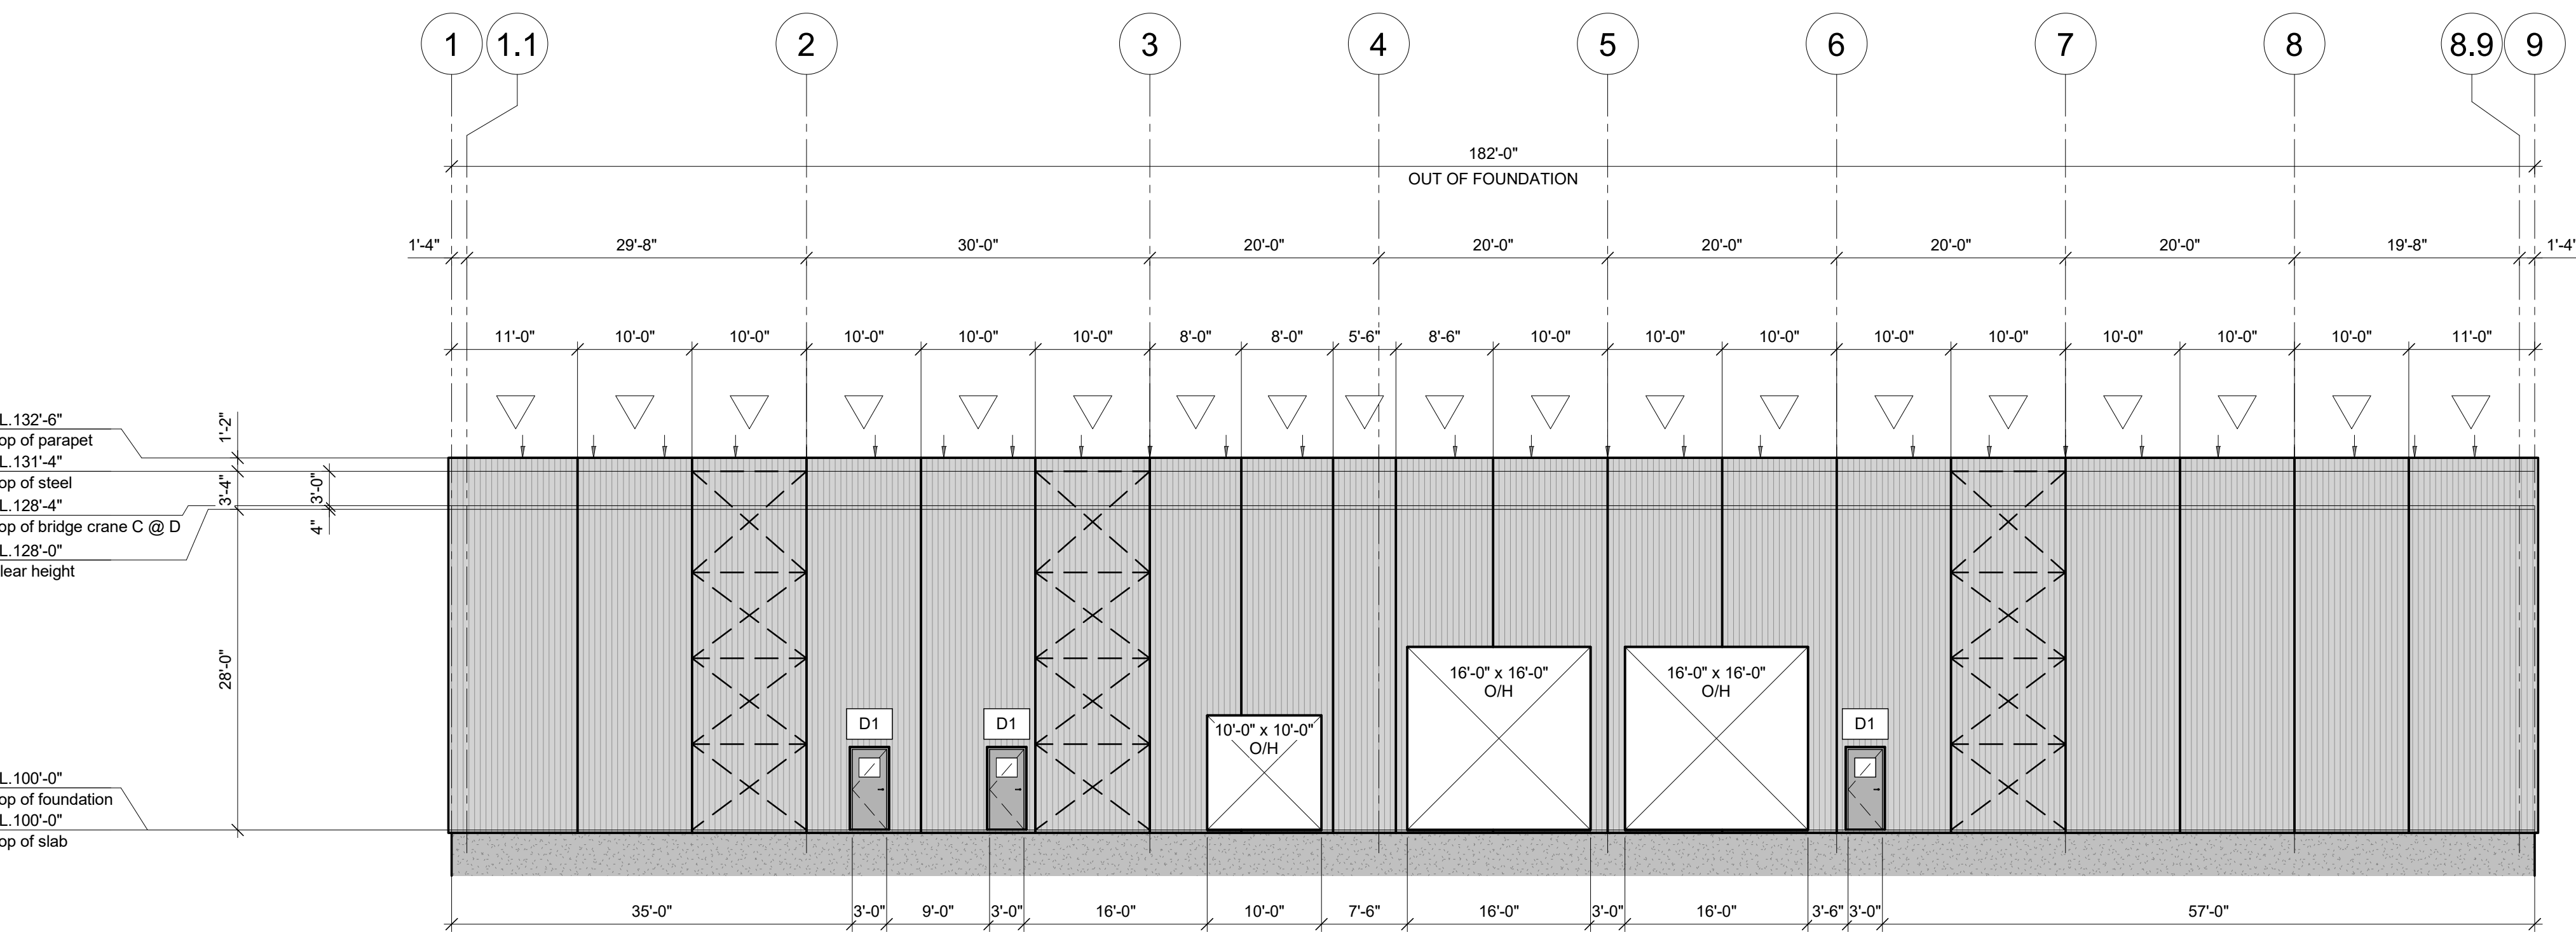


ELEVATION LINE D (EAST)


3/32" = 1'-0"

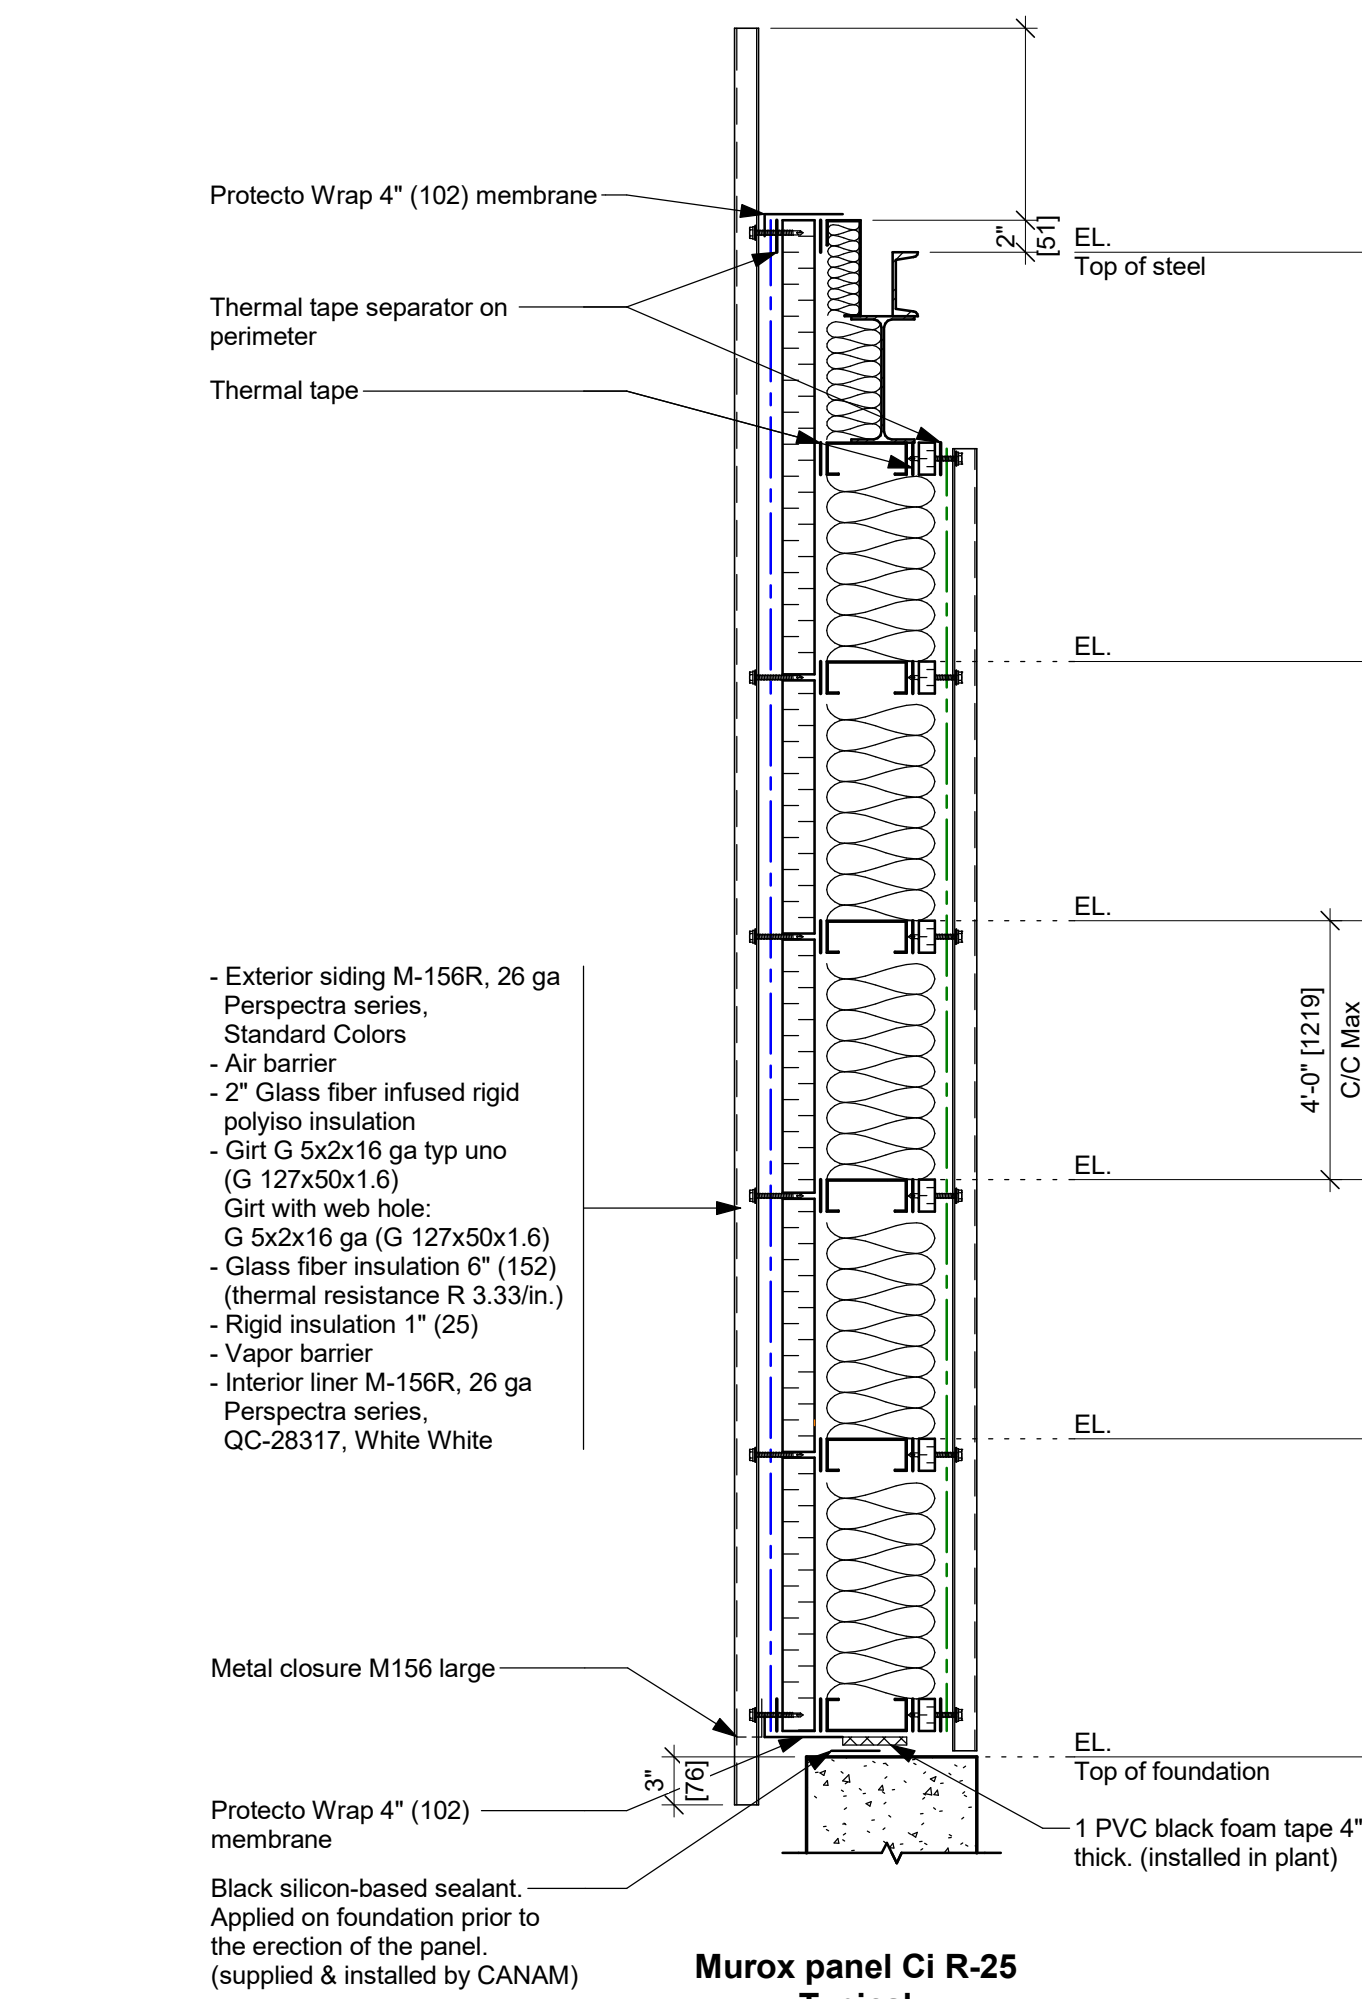

Murox panel CI R-25
Typical

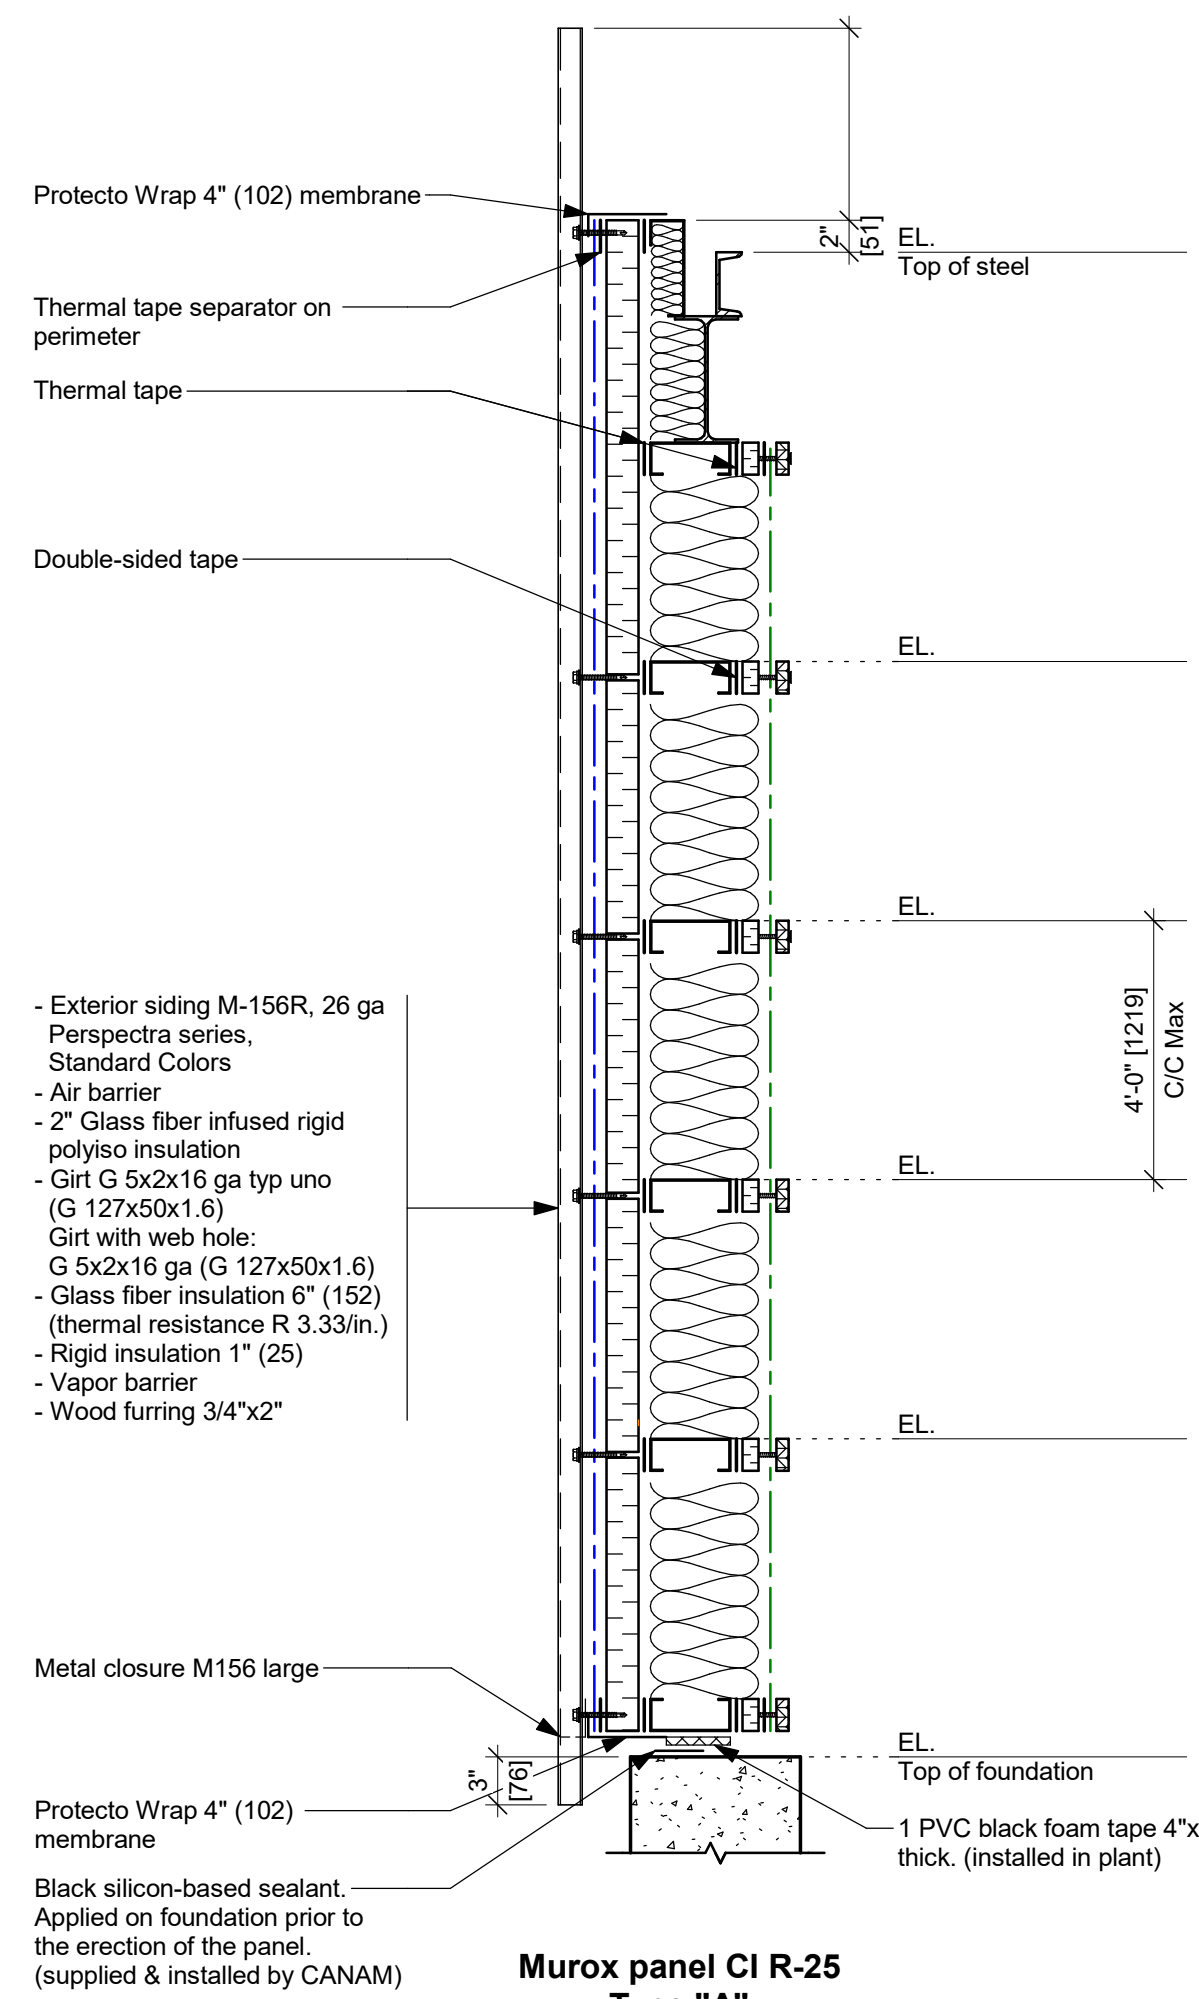


Murox panel CI R-25
Type "A"

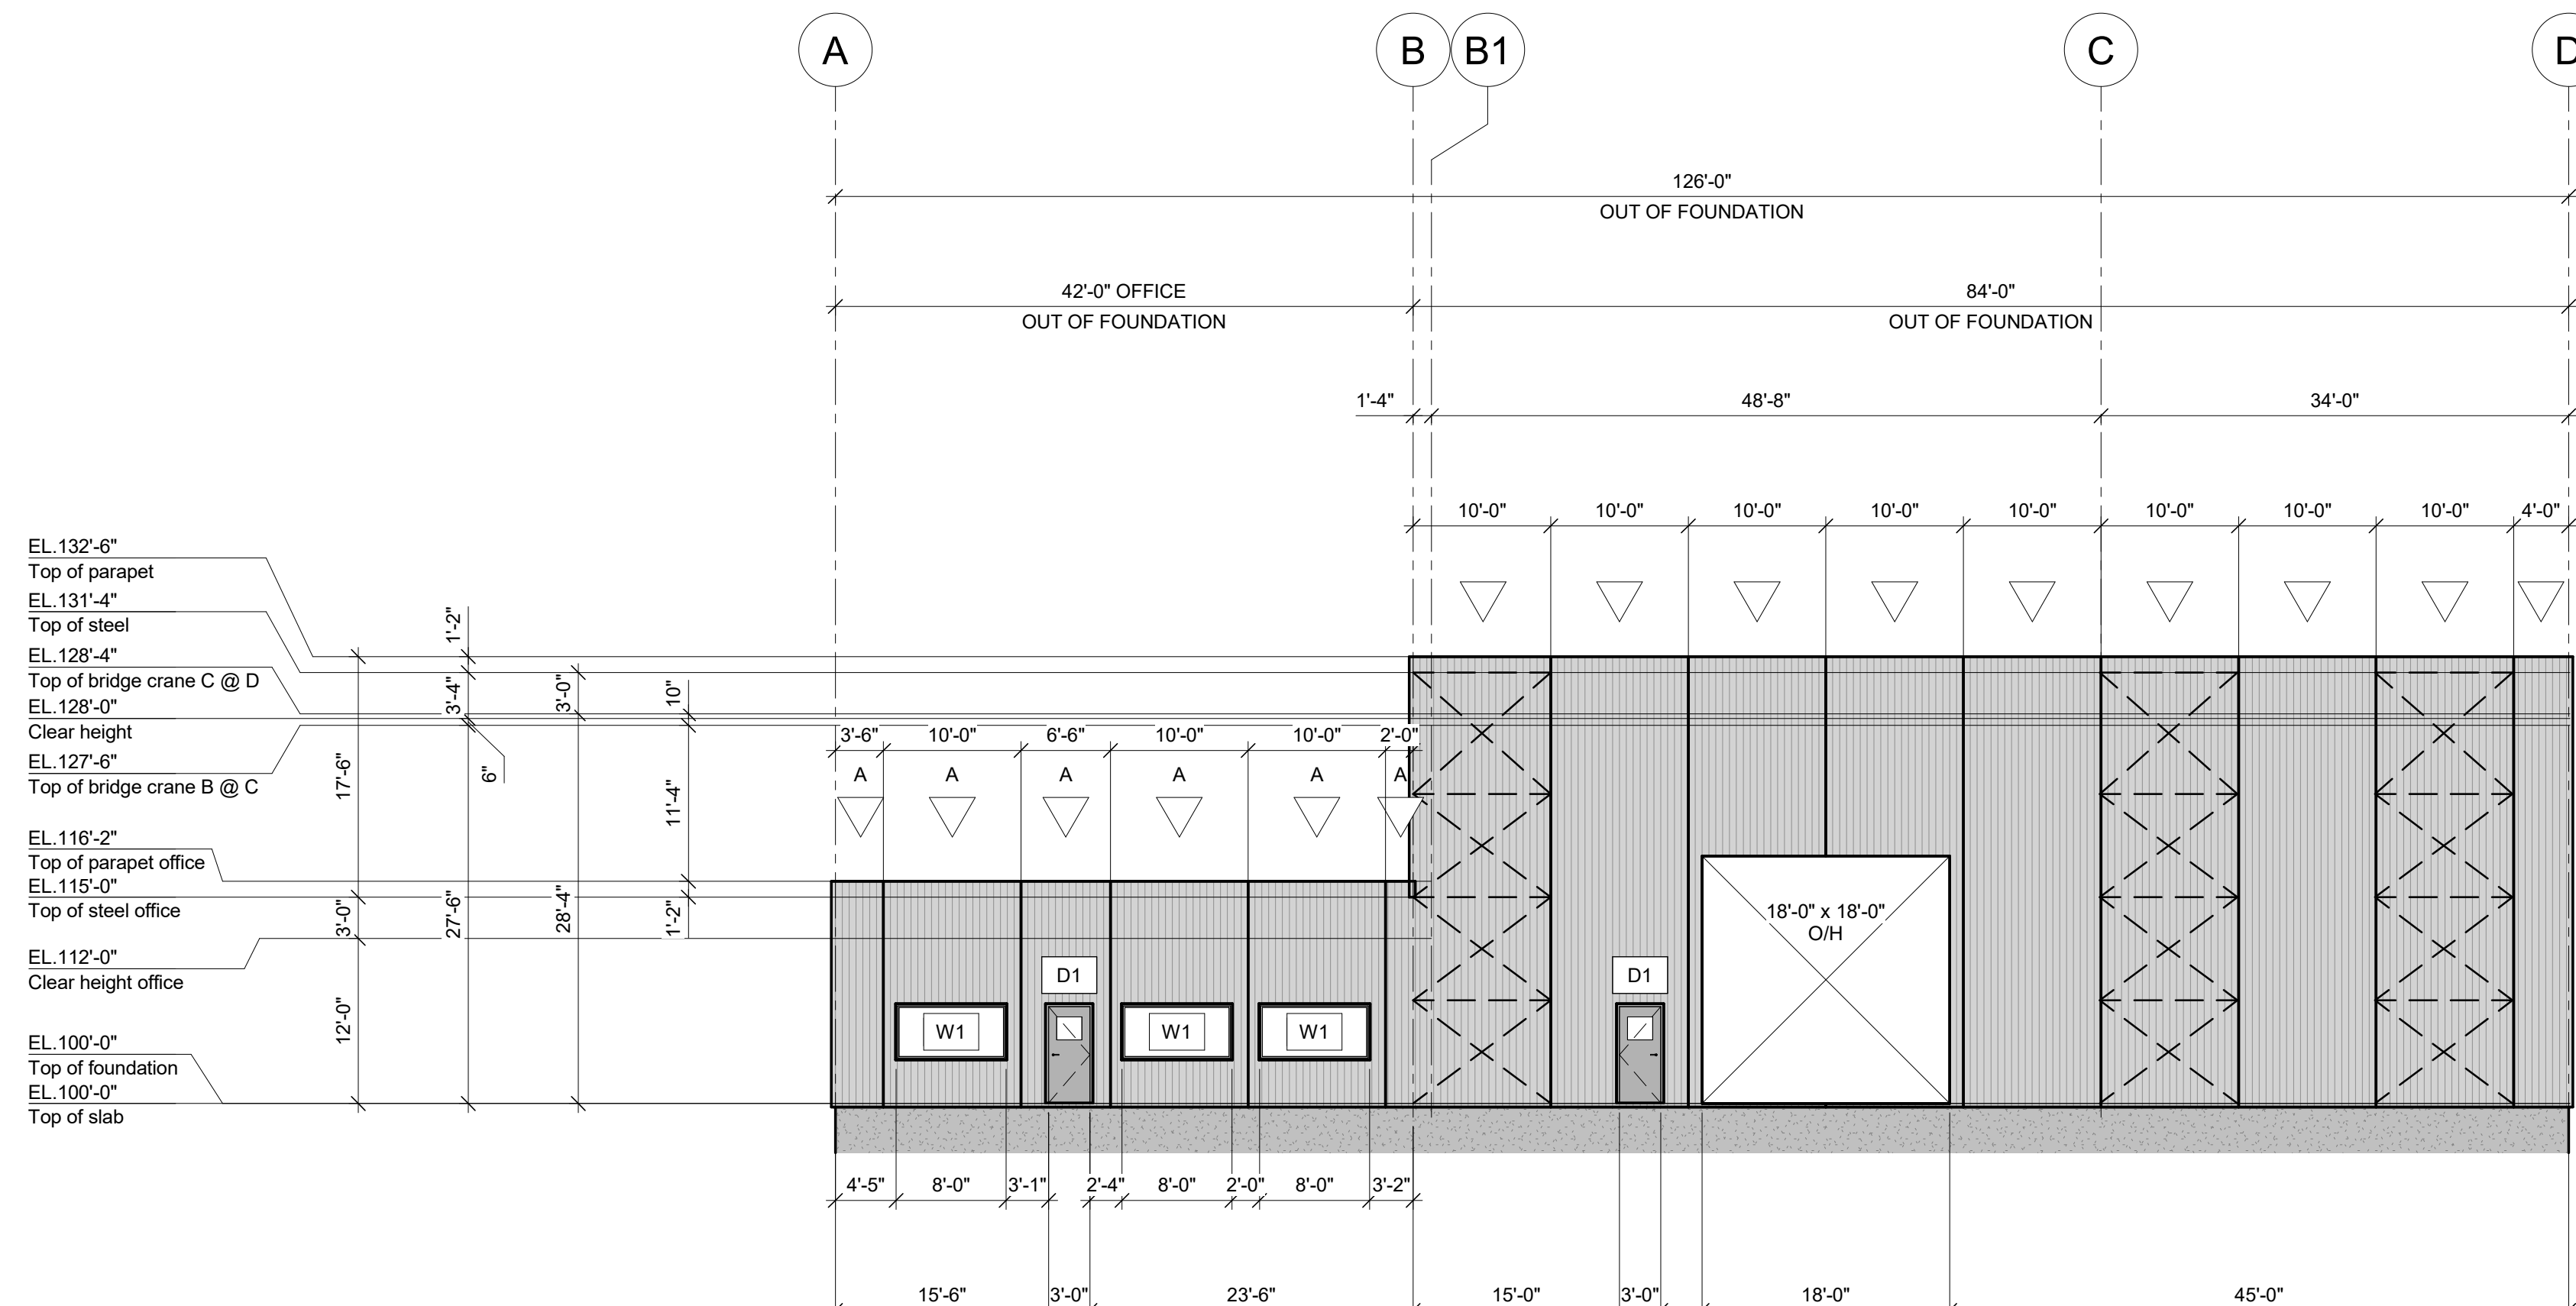


ELEVATION LINE 1 (SOUTH)

3/32" = 1'-0"

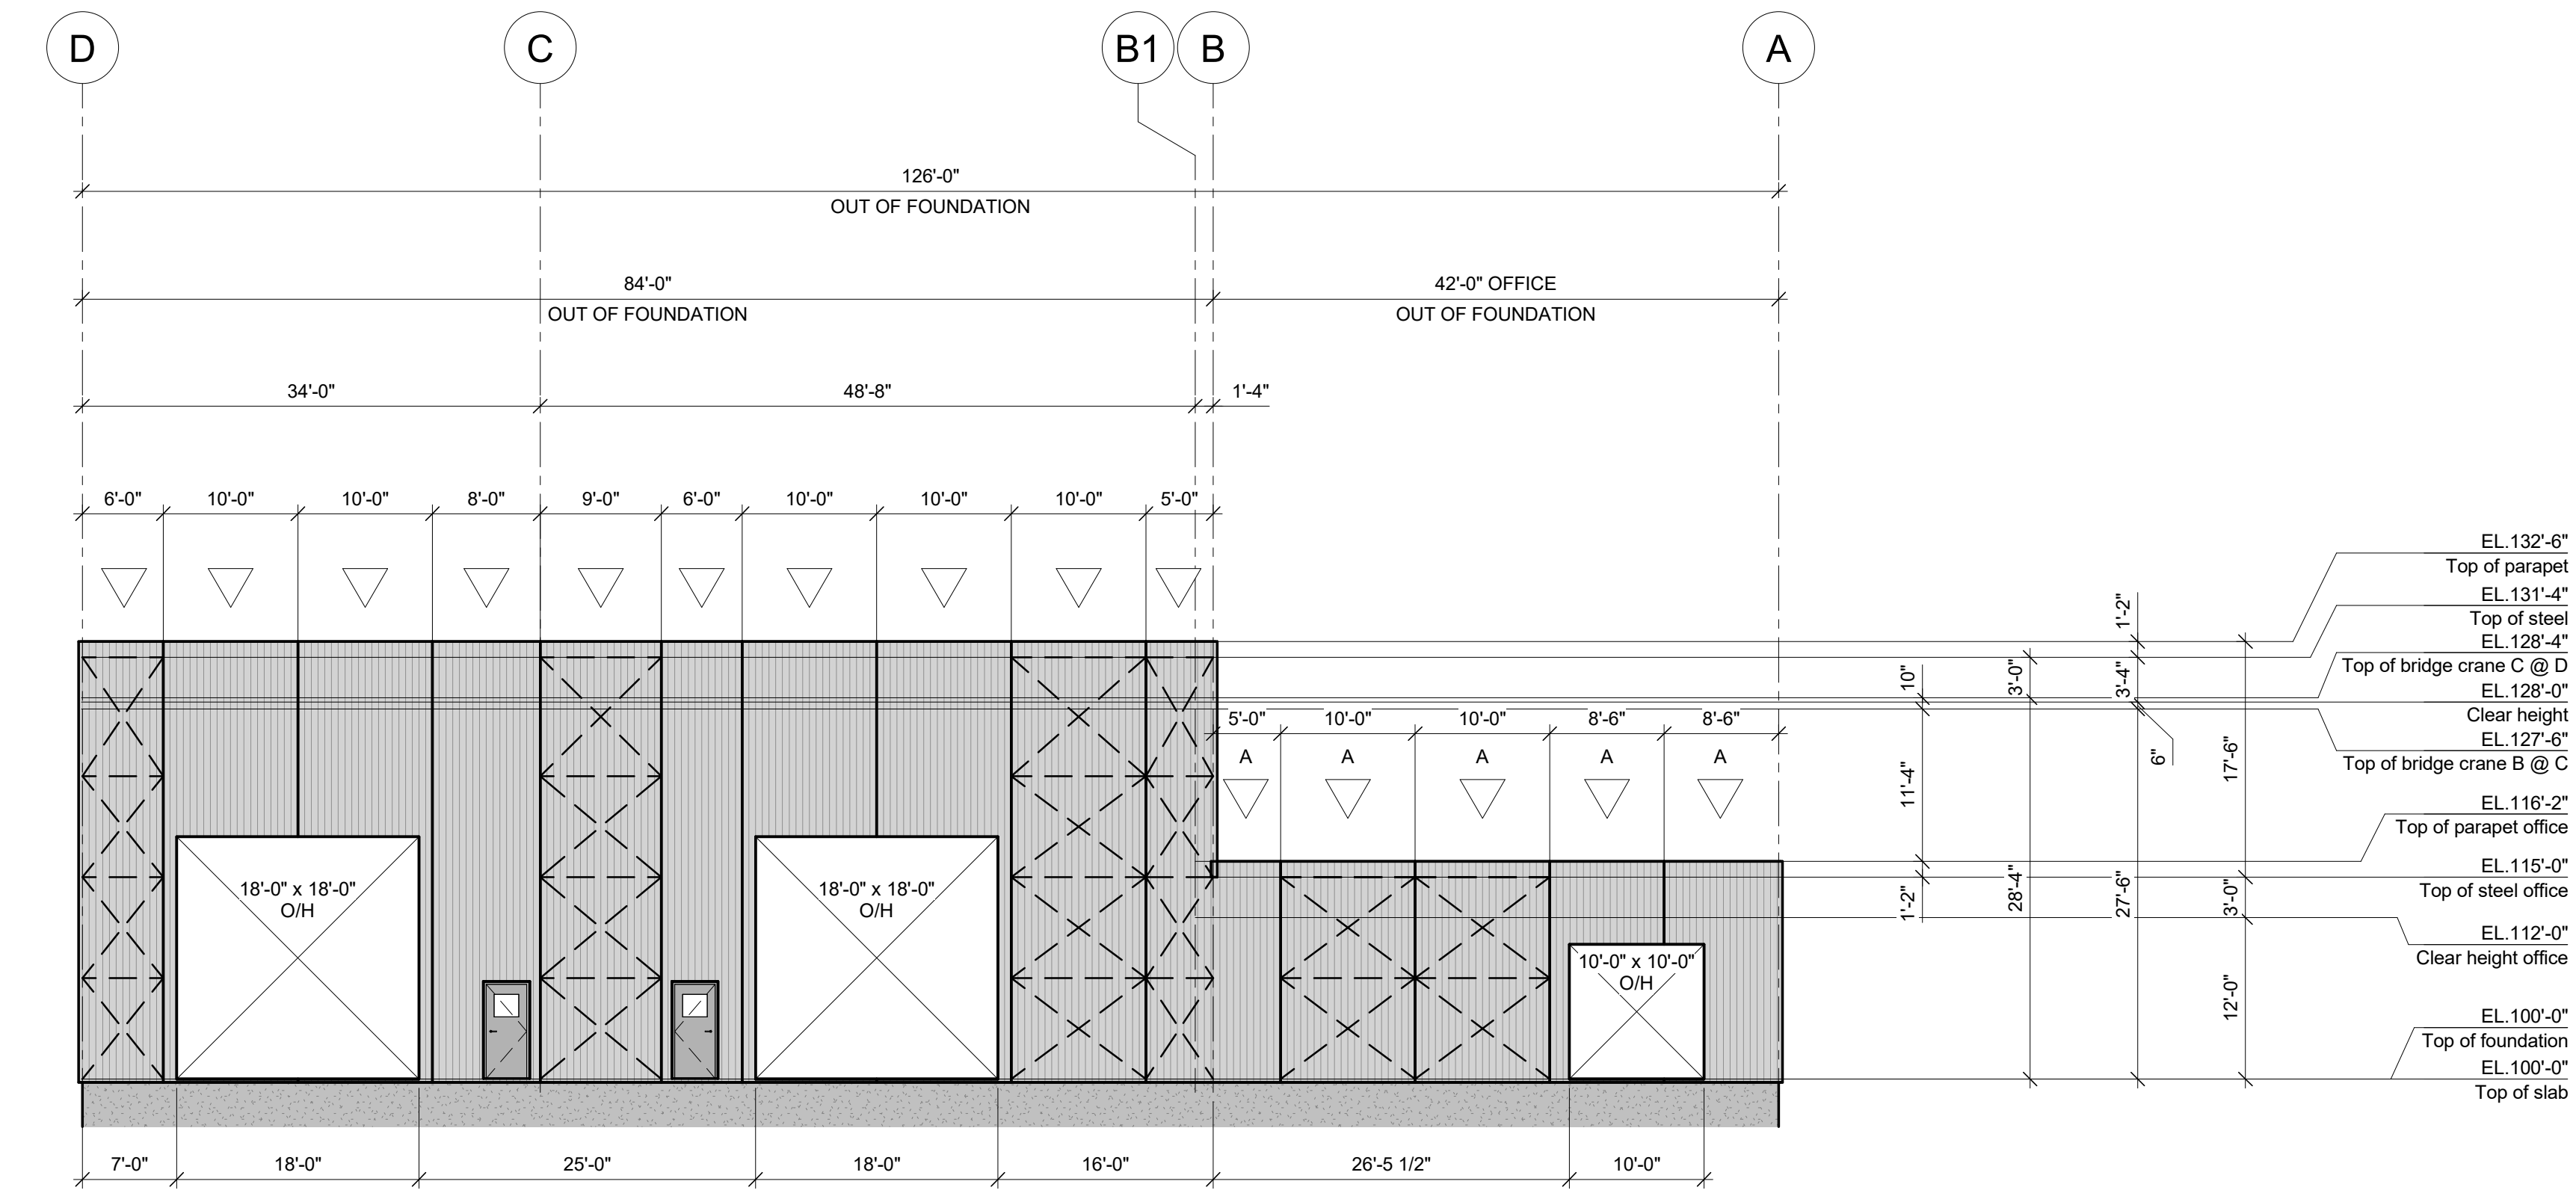

ELEVATION LINE 9 (NORTH)

3/32" = 1'-0"

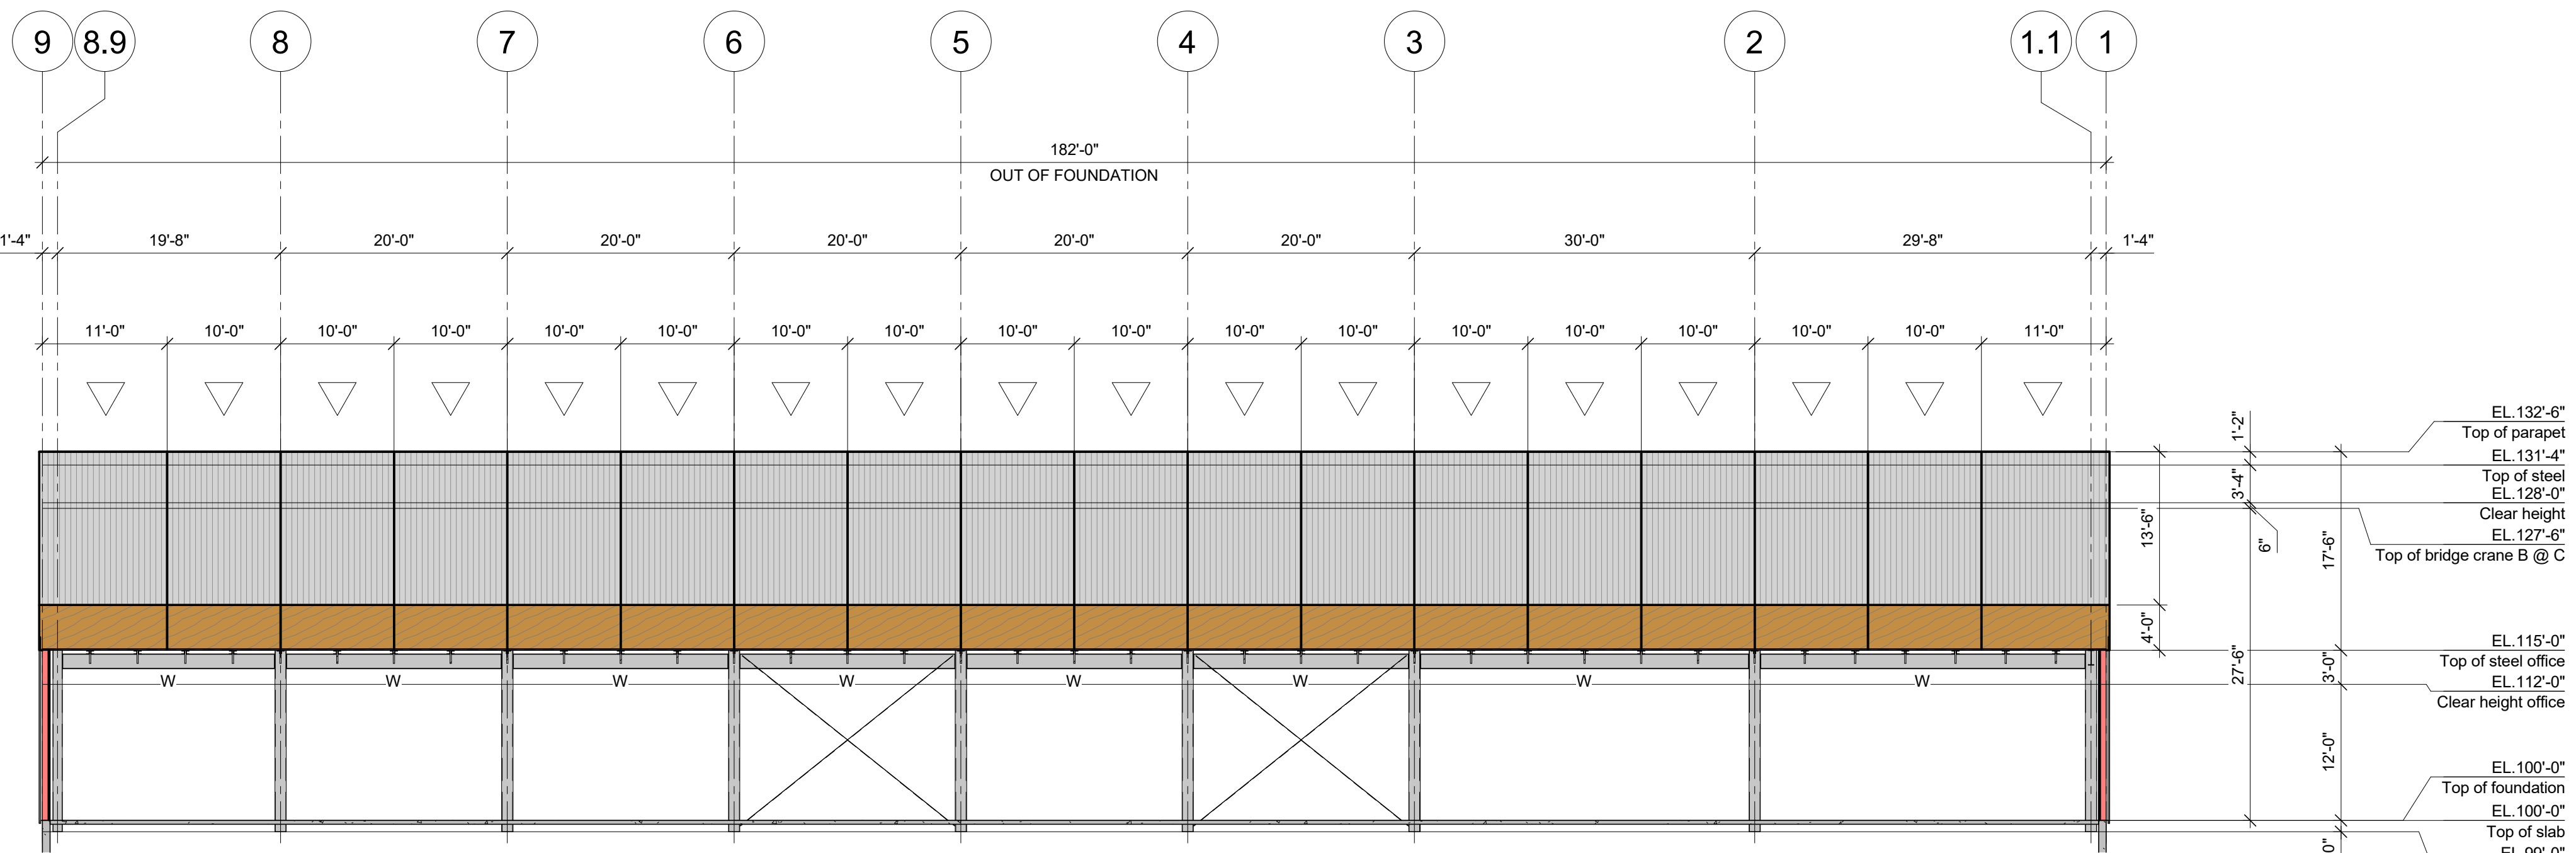

ELEVATION LINE B (WEST)

3/32" = 1'-0"

CONTRACTOR/RECTOR NOTE:
IT IS PROHIBITED TO MODIFY, COPY, REPRODUCE OR OTHERWISE
DISTRIBUTE THIS DRAWING OR ANY REPRESENTATION OF THIS
DRAWING OR ANY MEDIA, INCLUDING ELECTRONIC, WITHOUT THE
PRIOR WRITTEN APPROVAL OF CANAM GROUP INC.

PRELIMINARY

NOT TO BE USED FOR CONSTRUCTION

REVISION	DATE	DESCRIPTION	ISSUE	VER
----------	------	-------------	-------	-----

PROJECT MANAGER				
-				
-				
-				

DRAWING				
---------	--	--	--	--

DRAWN	DESIGNED	PROJECT ENGINEER	SCALE
J.P.			Comme indiqu�

CHECKED	CONSULTING ENGINEERS/ARCHITECTS	DATE (yyyy/mm/dd)
		2028/01/09

CUSTOMER: BMG Engineering



11505, 1re Avenue, bureau 500, Saint-Georges Beauce
Quebec, Canada, G5V 7G3
Phone : (418) 228-8031
Toll free : (877) 498-6049
www.canam.com

PROFESSIONAL SEAL

PROJECT

BMG Shop
Chelmsford, Ontario

DRAWING TITLE

PRELIMINARY SKETCH - ELEVATIONS,
WALL SECTION AND SCHEDULES

CONTRACT NUMBER	DRAWING NUMBER	DIVISION	REVISION
-----------------	----------------	----------	----------

P2028-001
EsMx501

Initials