
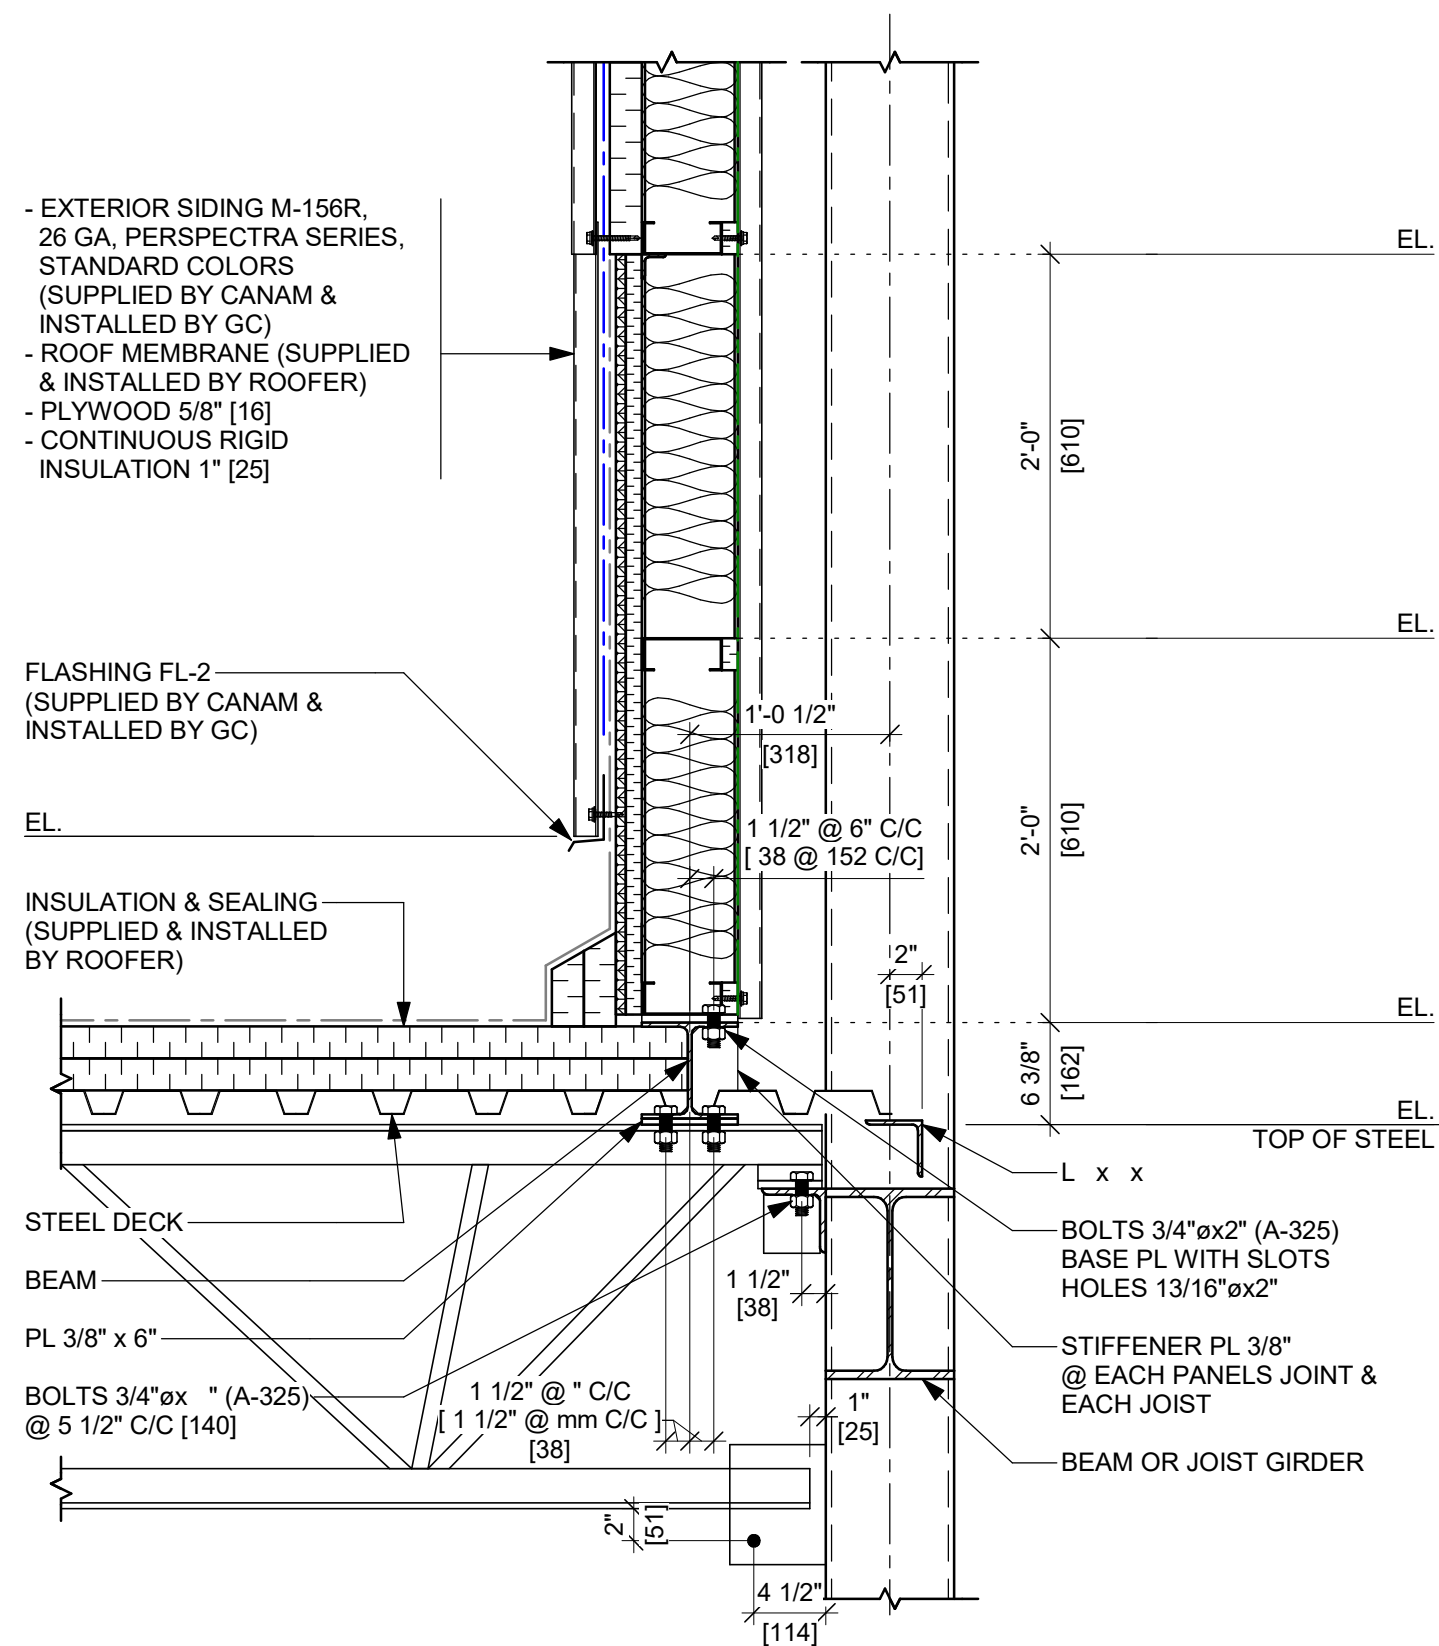
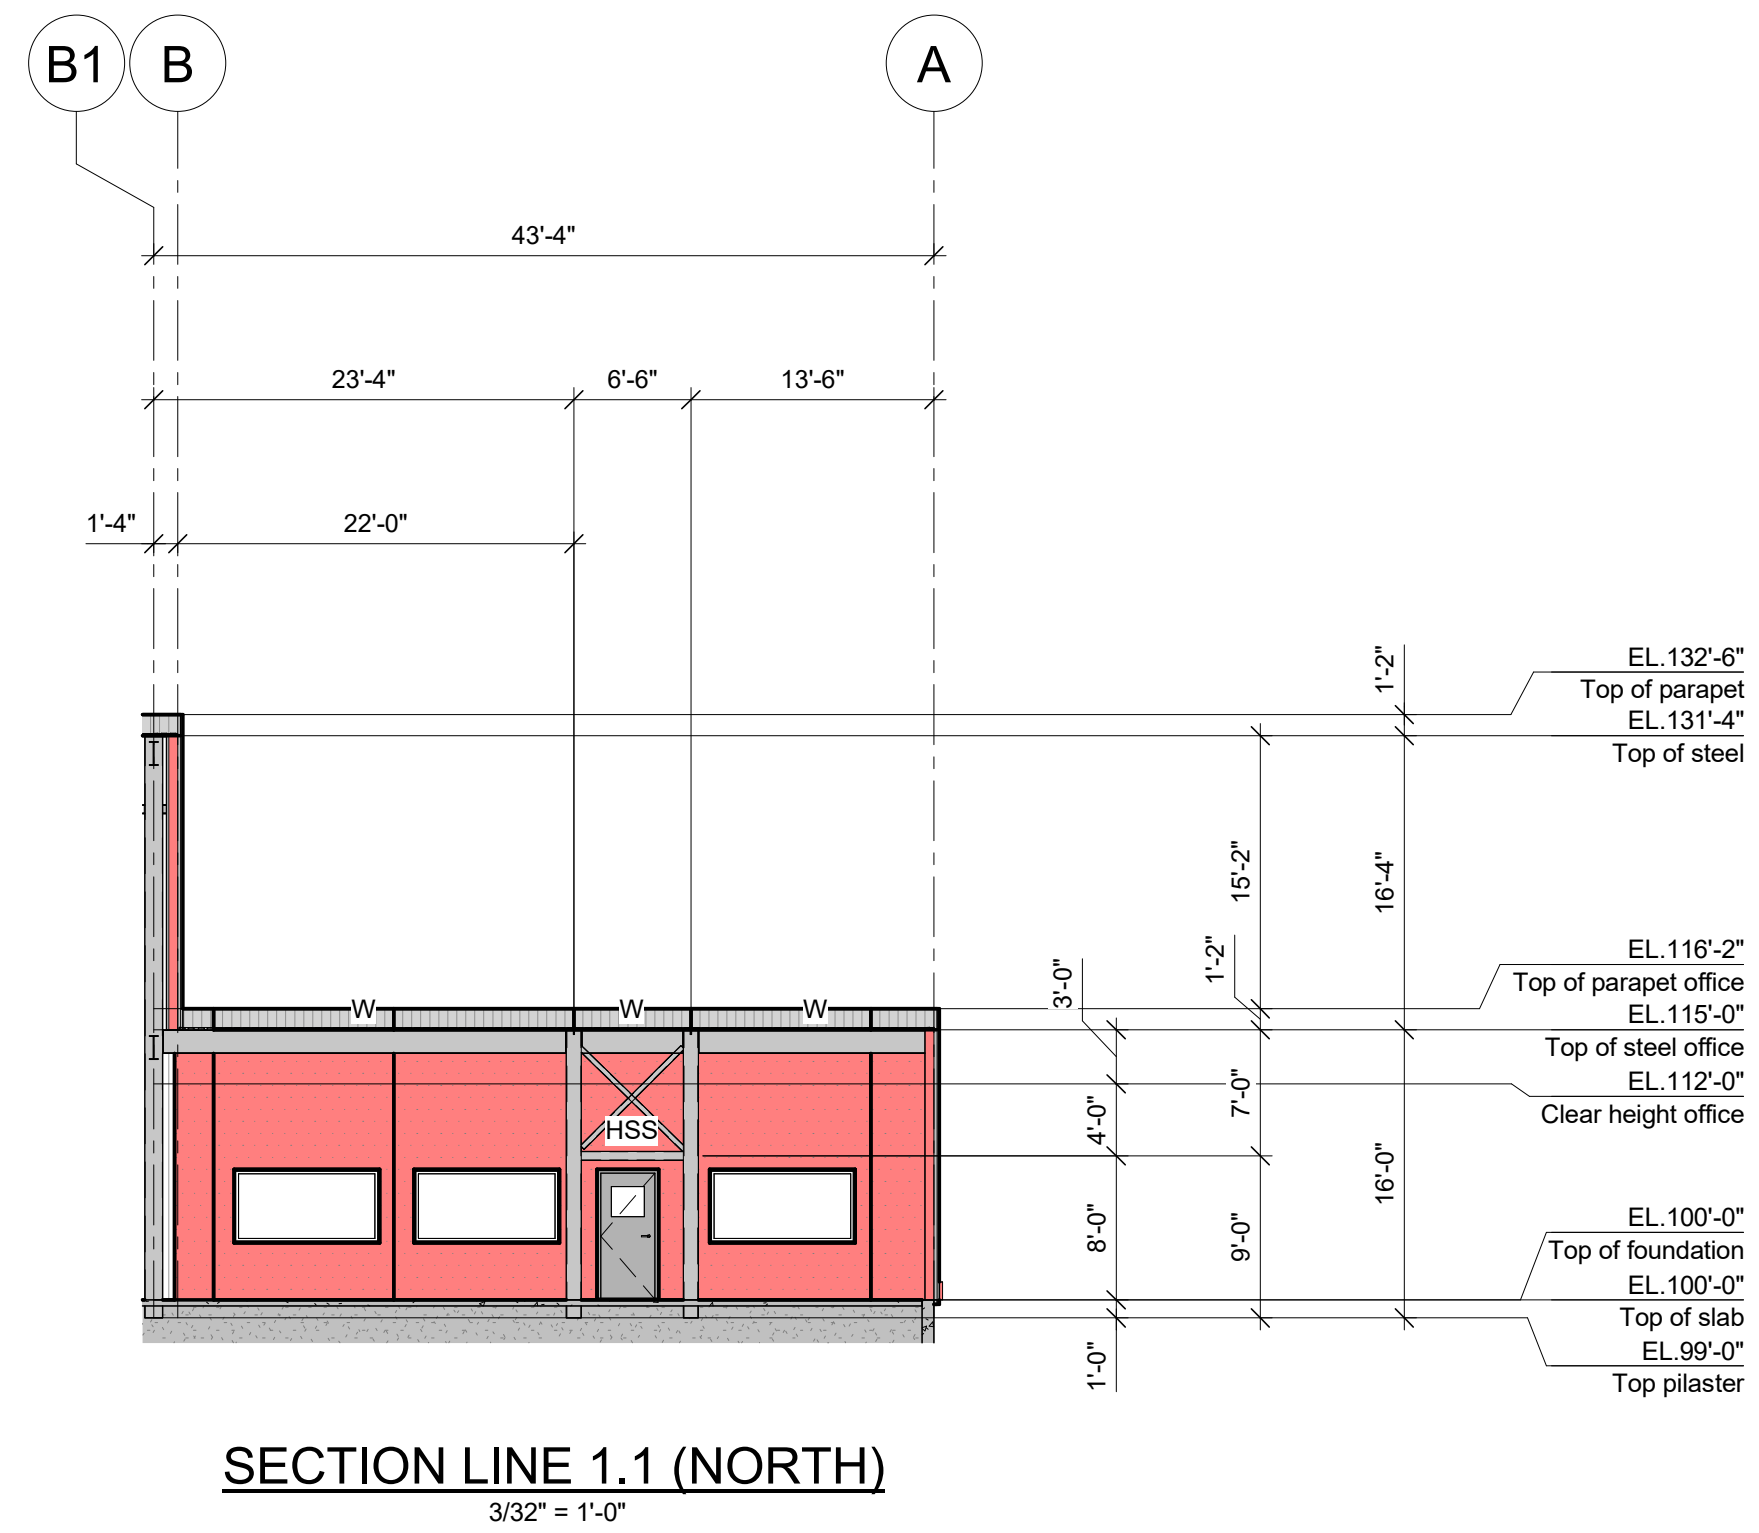


CONTRACTOR/ERECTOR NOTE:
IT IS PROHIBITED TO MODIFY, COPY, REPRODUCE OR OTHERWISE
DISTRIBUTE THIS DRAWING OR ANY REPRESENTATION OF THIS
DRAWING, OR ANY MEDIA, INCLUDING ELECTRONIC, WITHOUT THE
PRIOR WRITTEN APPROVAL OF CANAM GROUP INC.

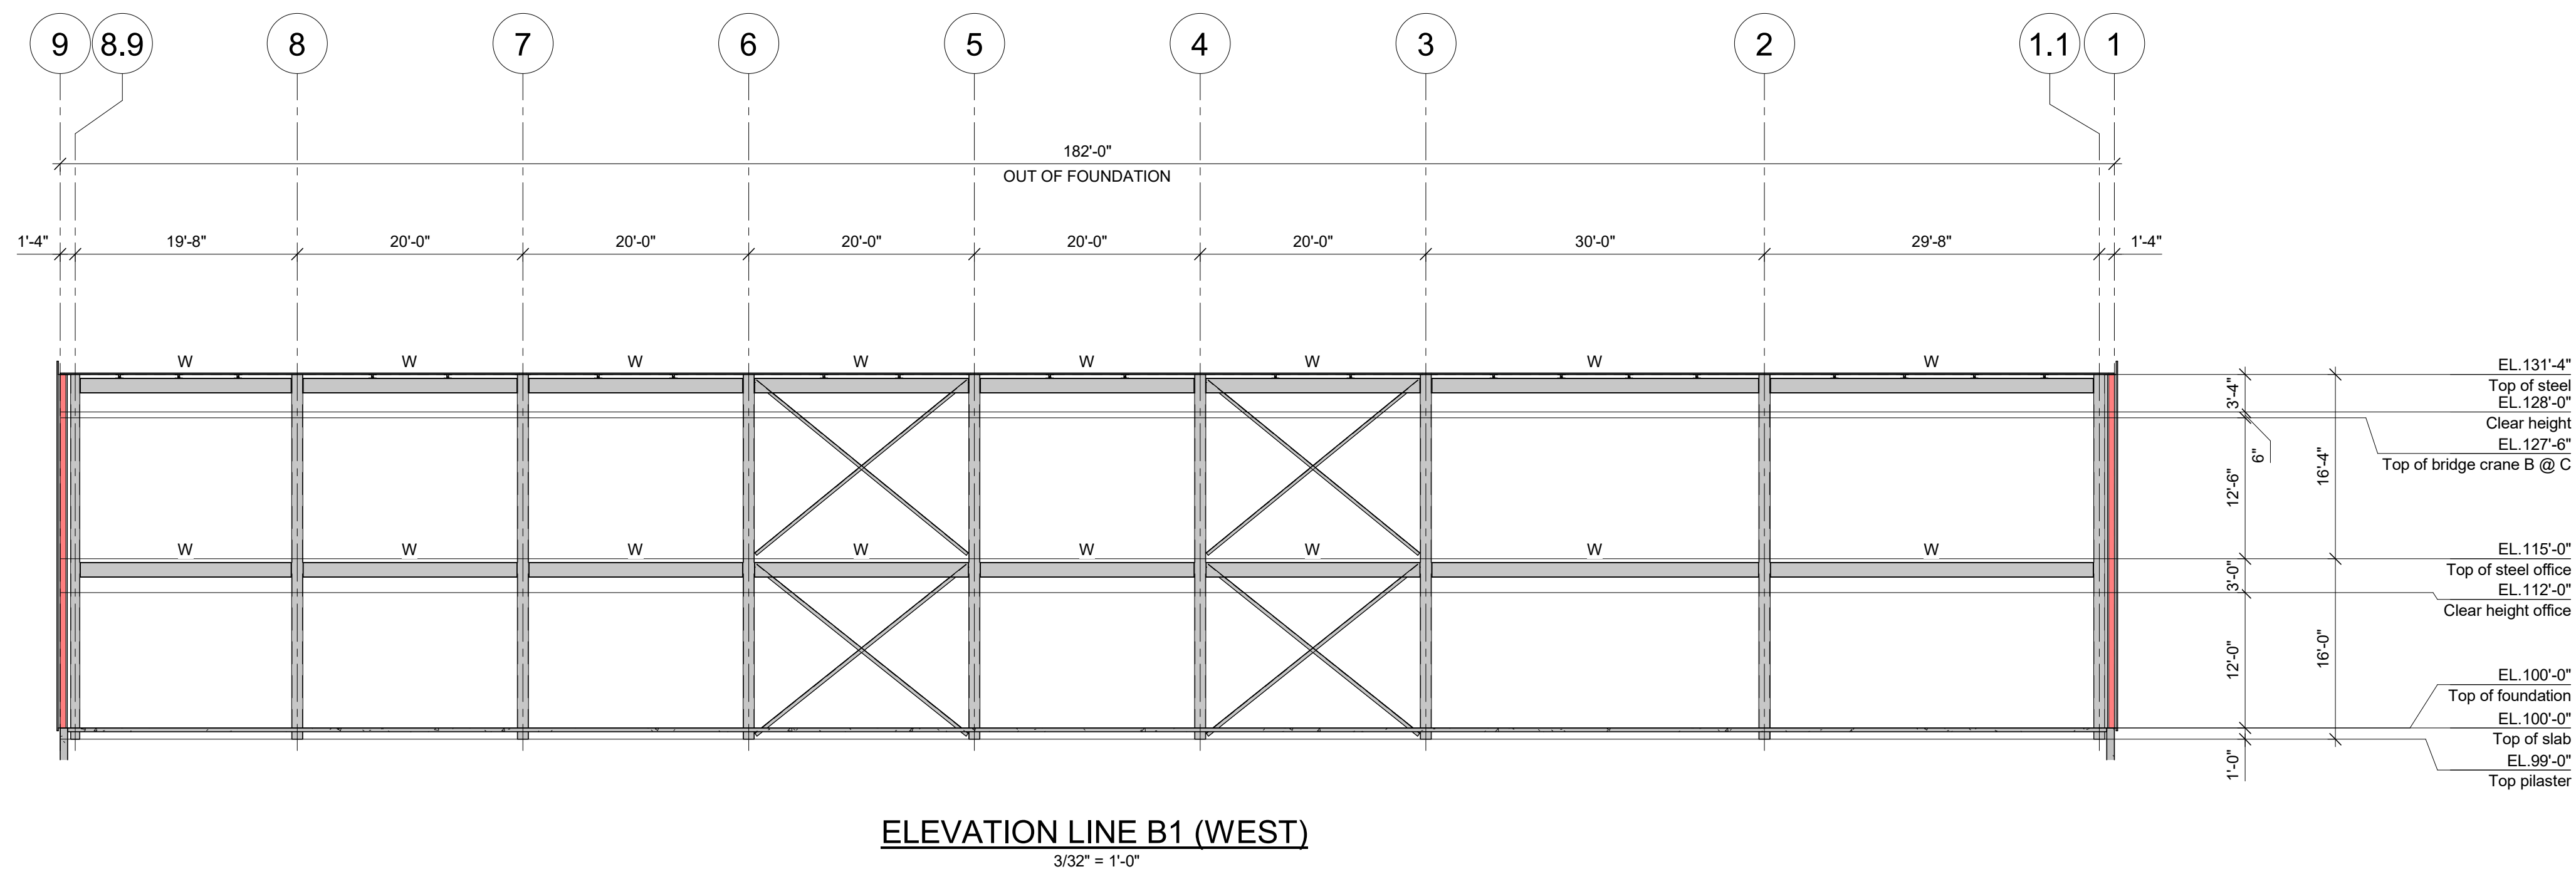

PRELIMINARY

NOT TO BE USED FOR CONSTRUCTION

REVISION	DATE	DESCRIPTION	DESS	VER
PROJECT MANAGER				
		-		
		-		
		-		
		-		
		-		

DRAFTING:			
DRAWN INITIALE	DESIGNED	PROJECT ENGINEER	SCALE: Comme indiqué
CHECKED	CONSULTING ENGINEERS / ARCHITECTS		DATE (yyyy/mm/dd) : 2026/01/09

CUSTOMER: BMG Engineering



11505, 1re Avenue, bureau 500, Saint-Georges Beauce
Quebec, Canada, G5Y 7X3
Phone : (418) 228-8031
Toll free : (877) 499-6049
www.canam.com

PROFESSIONAL SEA

PROJECT

BMG Shop
Chelmsford, Ontario

DRAWING TITLE

PRELIMINARY SKETCH - ELEVATION,
SECTION AND DETAIL

CONTRACT NUMBER P2026-001	DRAWING NUMBER EsMx502	DIVISION	REVISION 
------------------------------	---------------------------	----------	---