

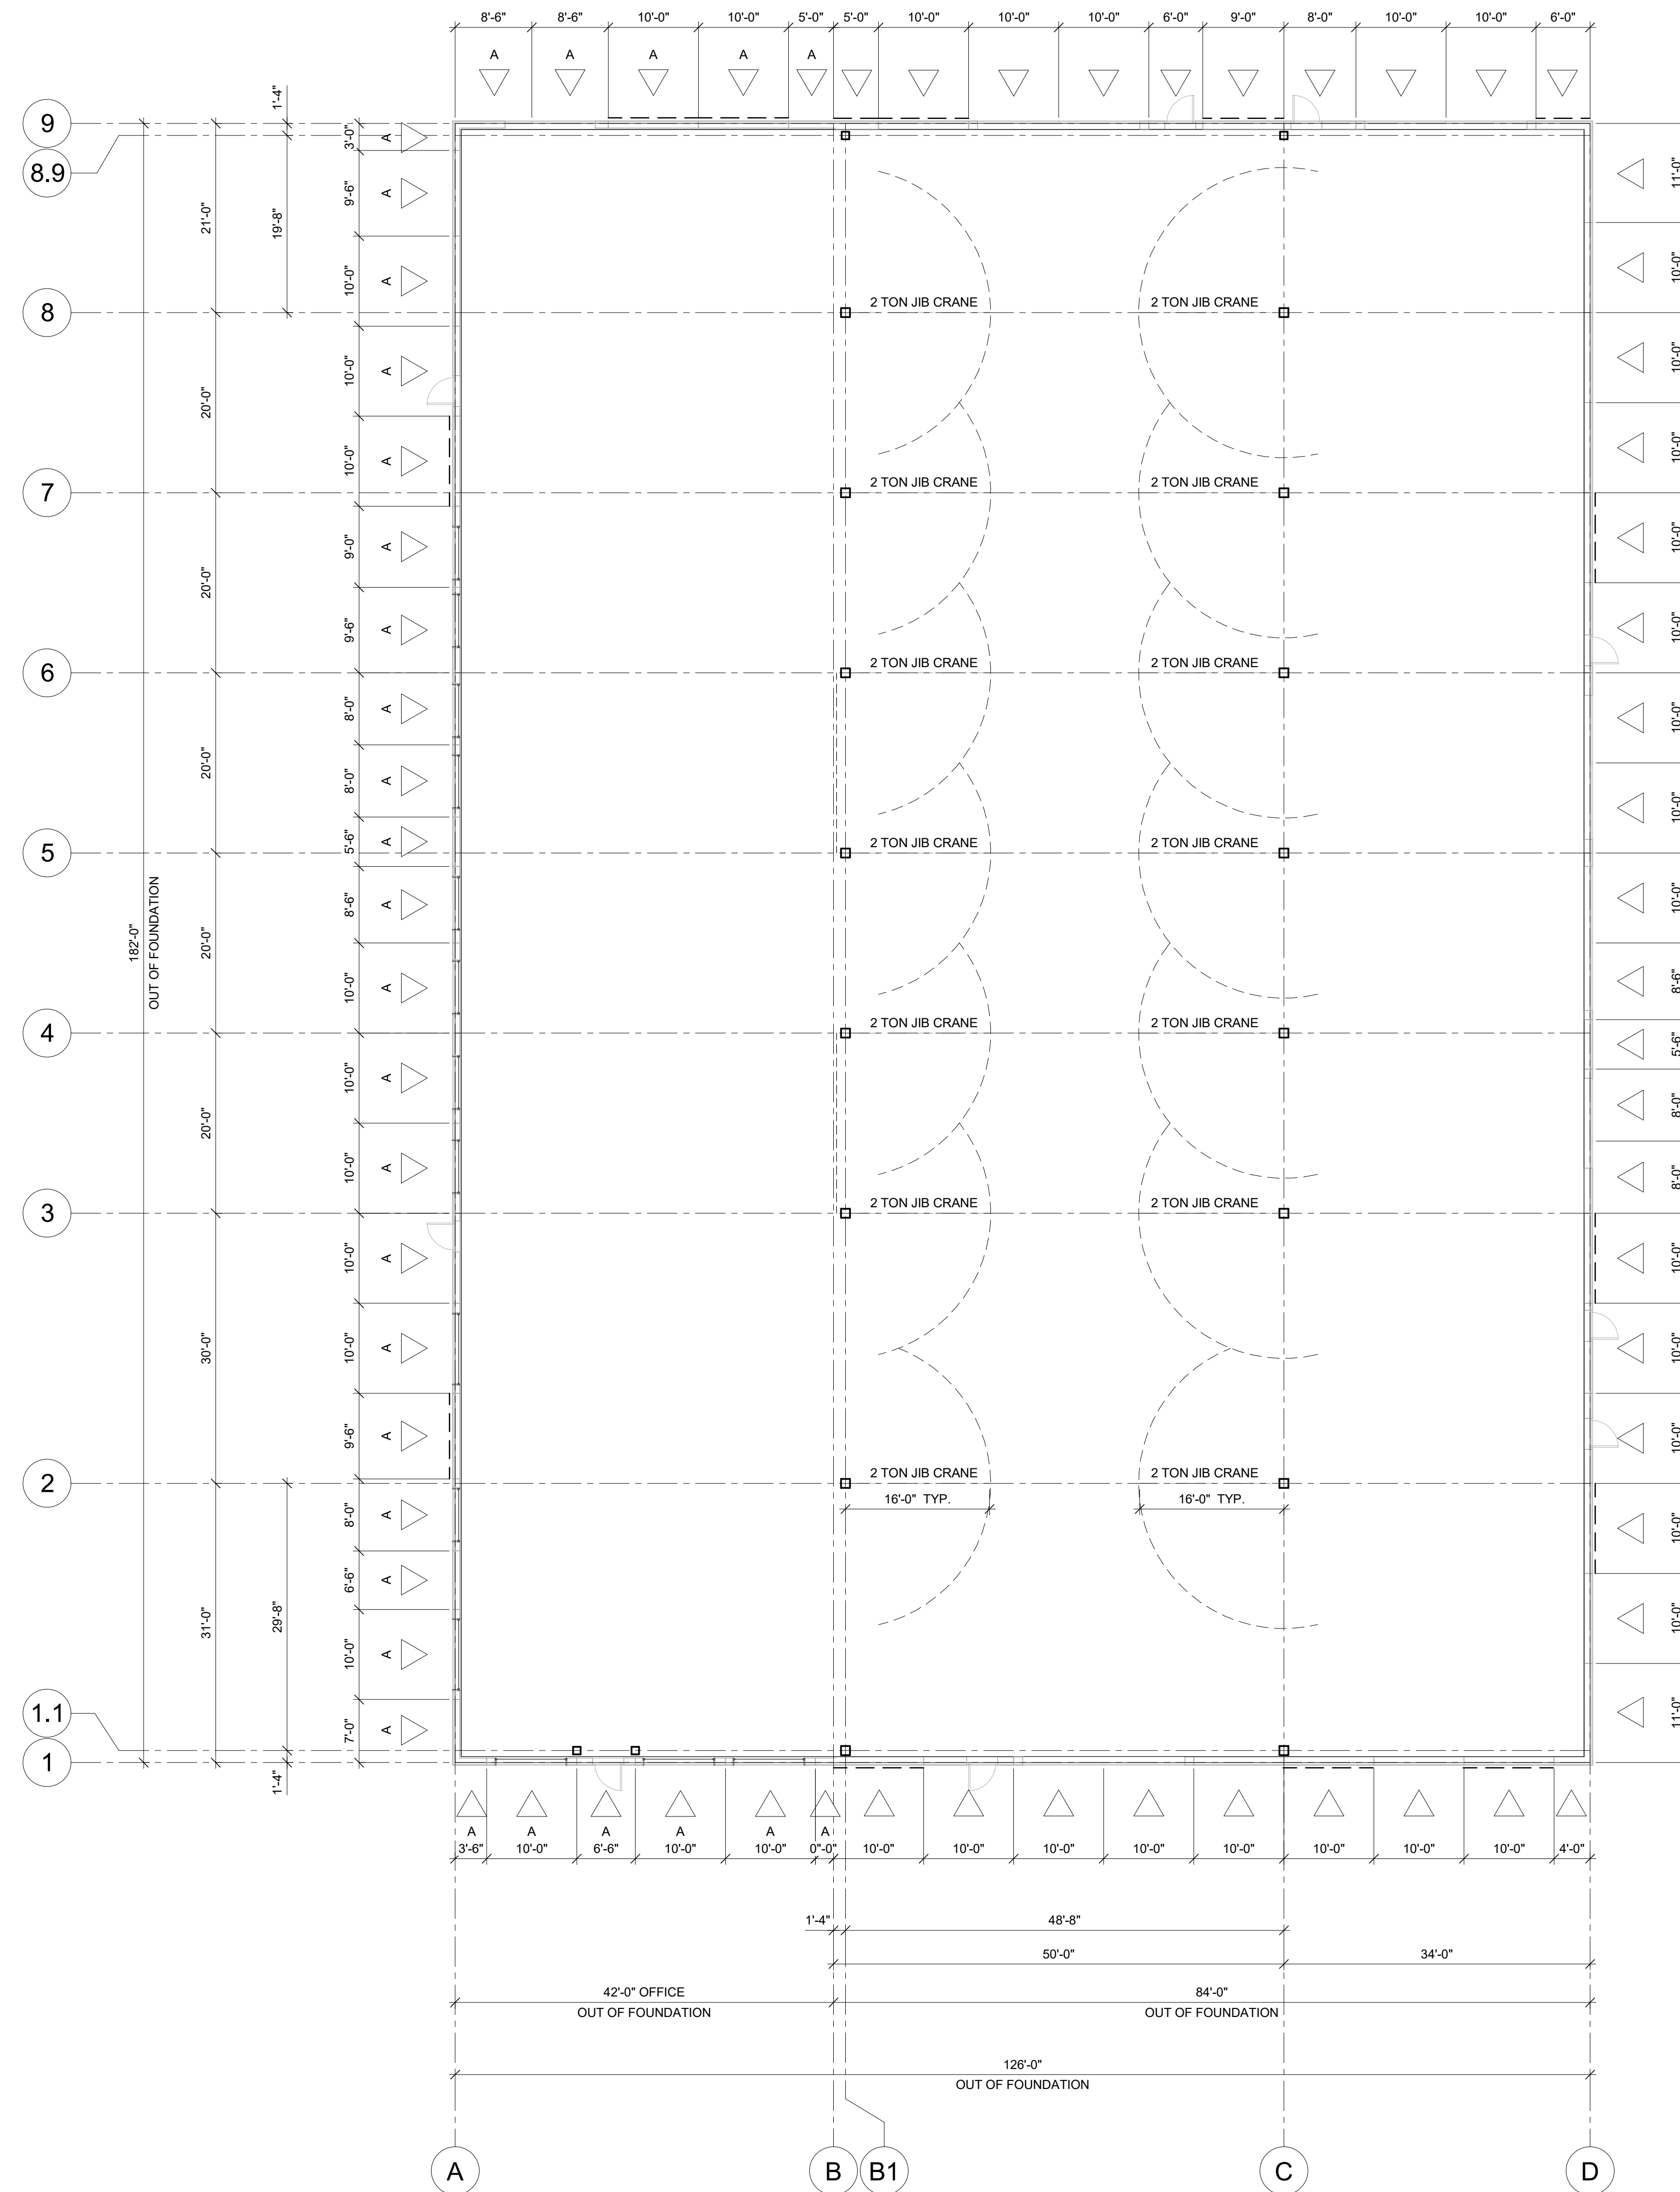
NOTE : ALL SERVICE LOADS ARE EXPRESSED IN Kips, TYP. U.N.

NOTE: ALL SERVICE LOADS ARE EXPRESSED IN KILO NEWTONS (KN)														End of table	
VERTICAL LOADS						BRACINGS								JIB CRANES LOADS	
COL		D	S	C	W	E		C		W		C			
ans						H(N/S)	H(E/W)	V.	H(N/S)	H(E/W)	V.	H(N/S)	H(E/W)	M2 (Kg/T)	
B.1	1.1	25.0	85.0	56.0	10.0										
B.1	2	45.0	130.0	74.0	17.0										
B.1	3	37.0	105.0	70.0	15.0	±50		±82	±9		±14	±12	±16	±4 ±28	
B.1	4,5 & 6	30.0	85.0	67.0	12.0	±50		±82	±9		±14	±12	±16	±4 ±28	
B.1	7&8	30.0	85.0	67.0	12.0									±4 ±28	
B.1	8,9	24.0	40.0	44.0	7.0										
C	1.1	20.0	35.0	84.0	8.0									±4 ±28	
C	2	35.0	70.0	120.0	15.0									±4 ±28	
C	3	30.0	60.0	105.0	12.0									±4 ±28	
C	4 to 8	25.0	40.0	67.0	10.0									±4 ±28	
C	8,9	15.0	25.0	67.0	7.0										
1.1	(2 col. Added each side of the office door)	2.0	6.0		1.0	±20		±88				±8	±36		

NOTE : ALL SERVICE LOADS ARE EXPRESSED IN Kips, TYP. U.N

[illegible]

NOTE : ALL SERVICE LOADS ARE EXPRESSED IN Kips, TYP. U.N

[illegible]

ANCHOR PLAN
3/32" = 1'-0"

NOTE:

All columns on line B & C will be designed to support a 2 ton jib crane, with a span of 16'-0", with the bracket attached to the columns at 6'-0"