
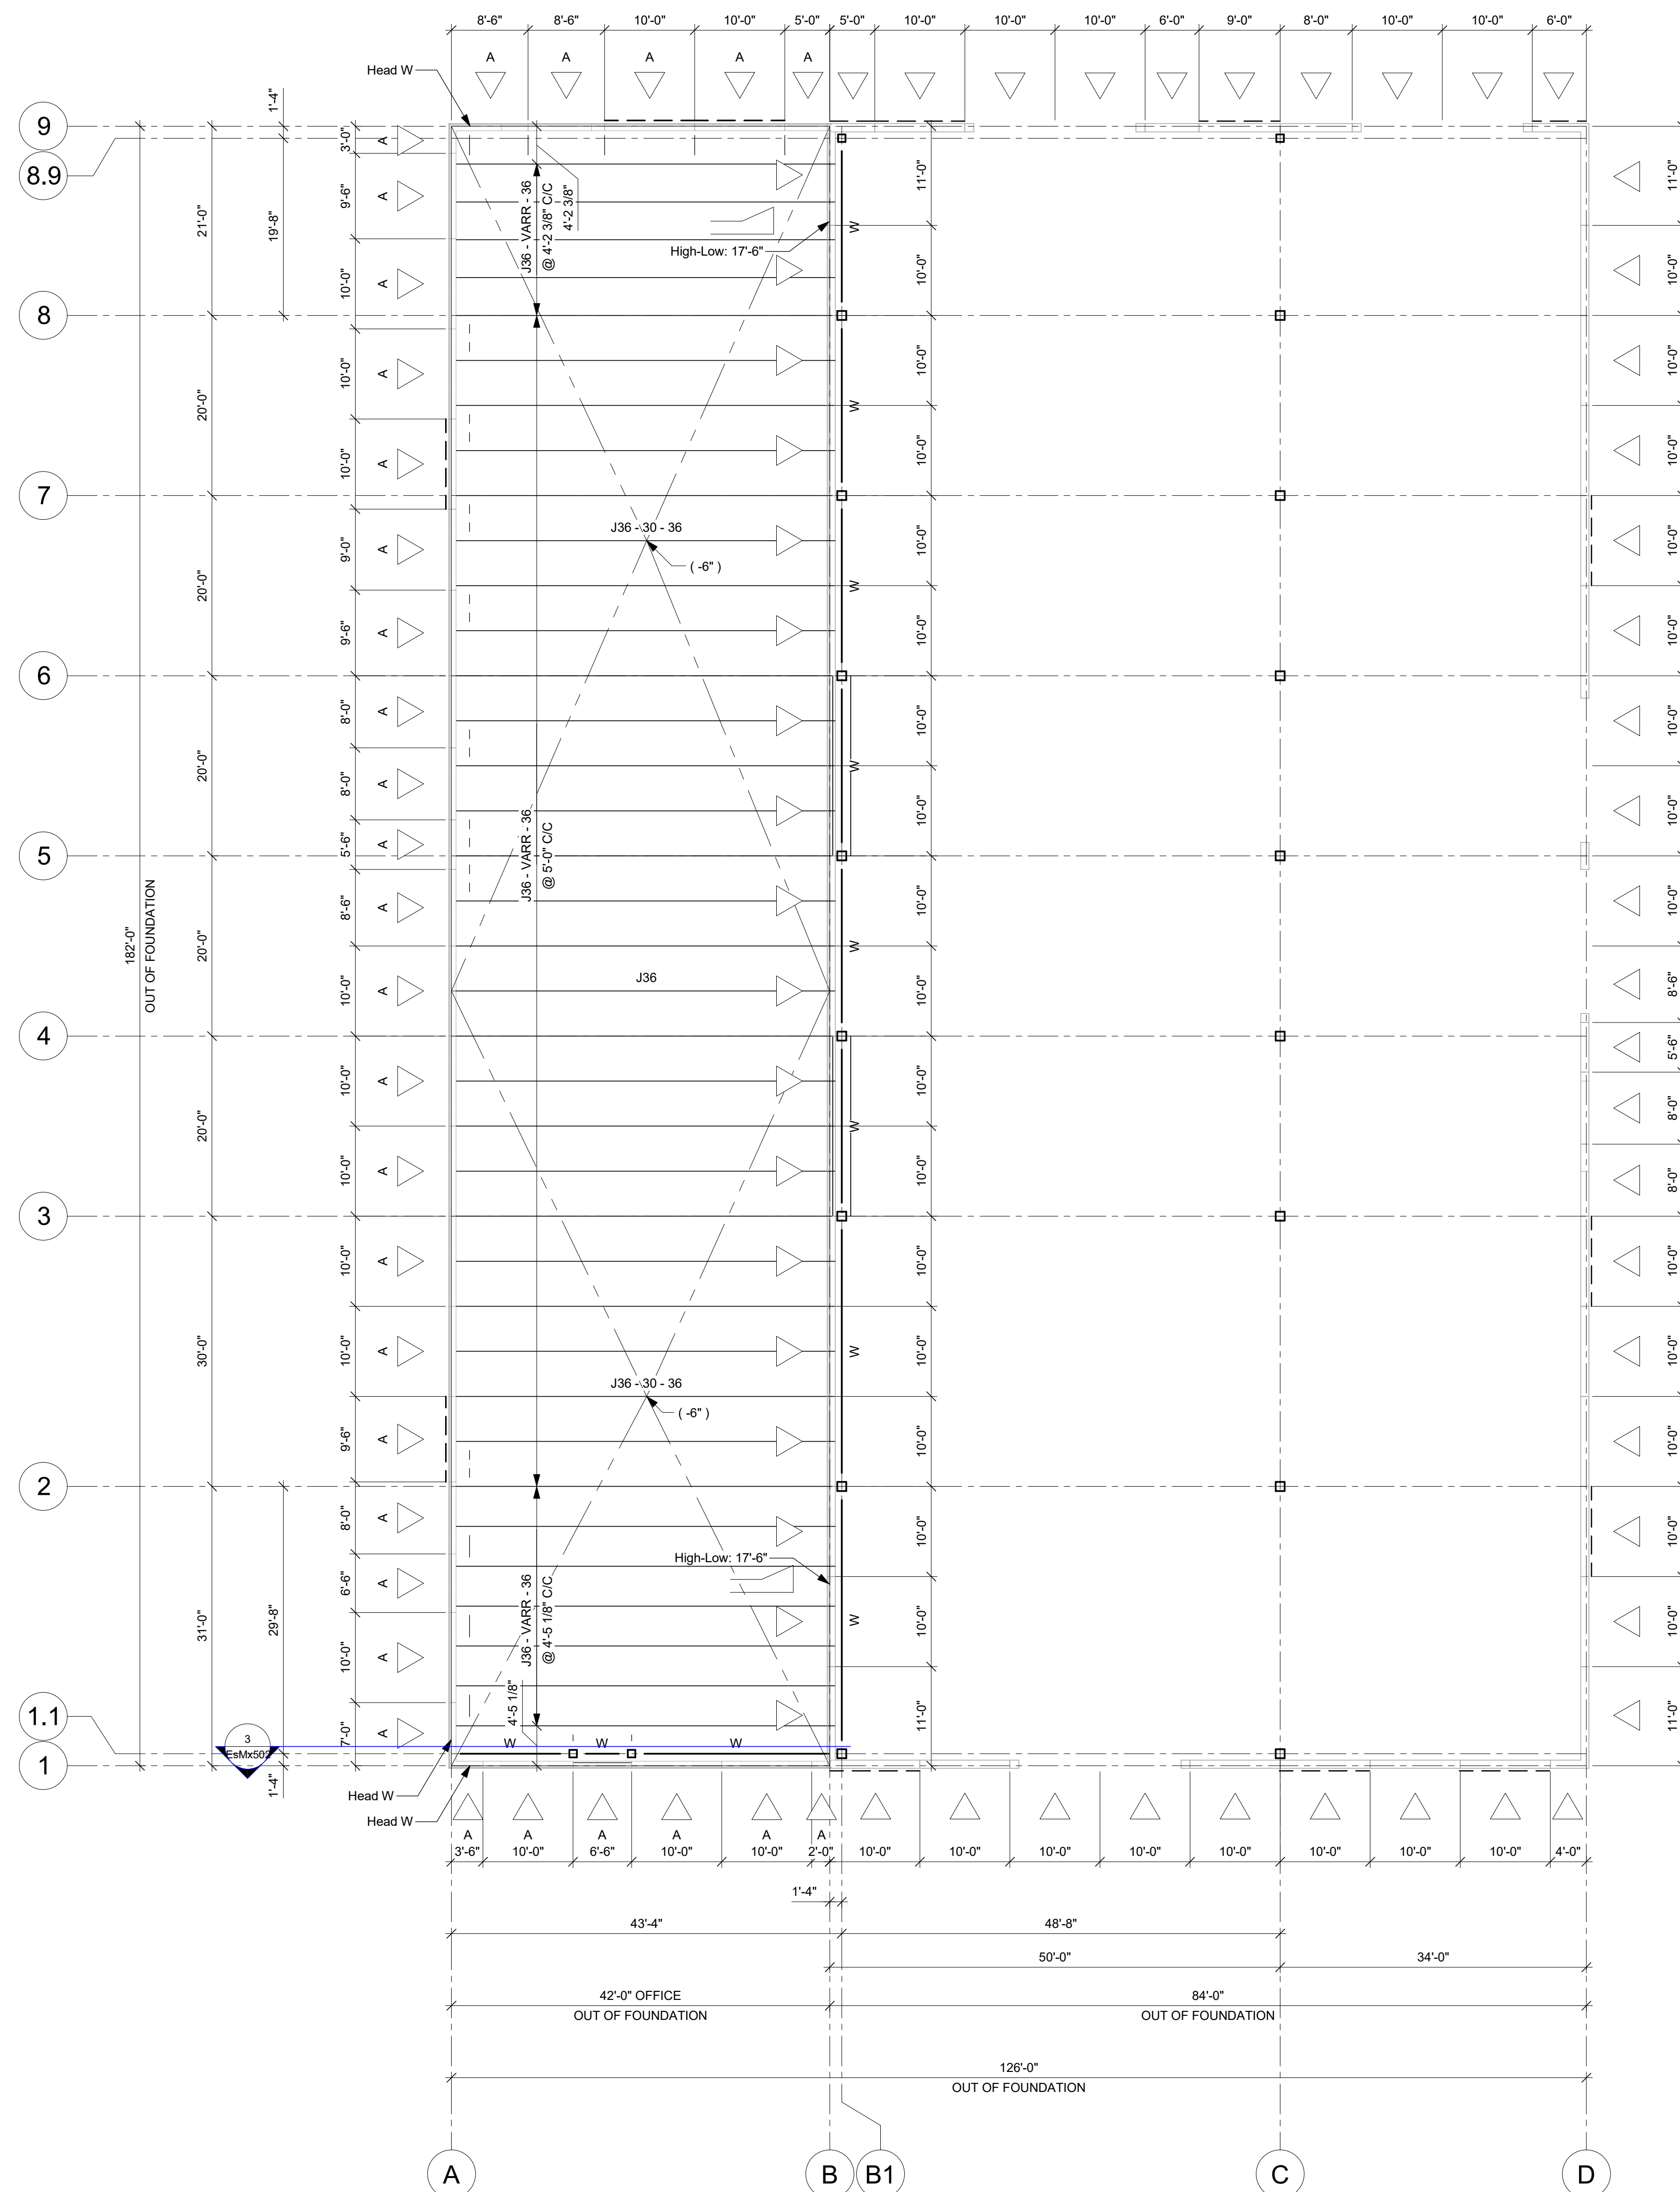
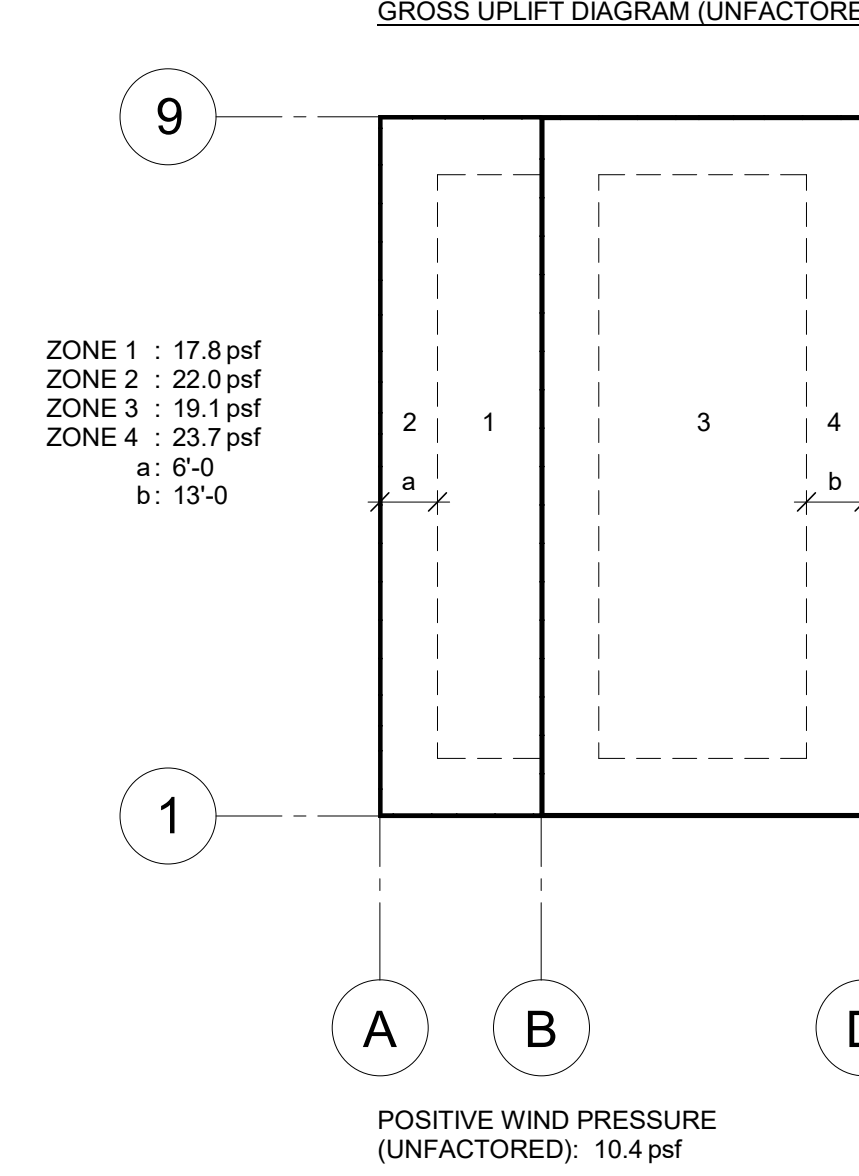
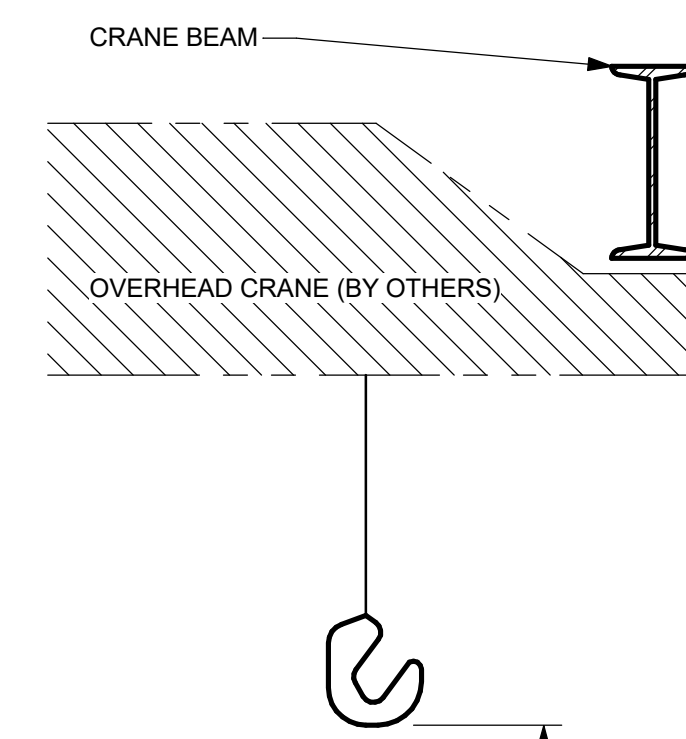
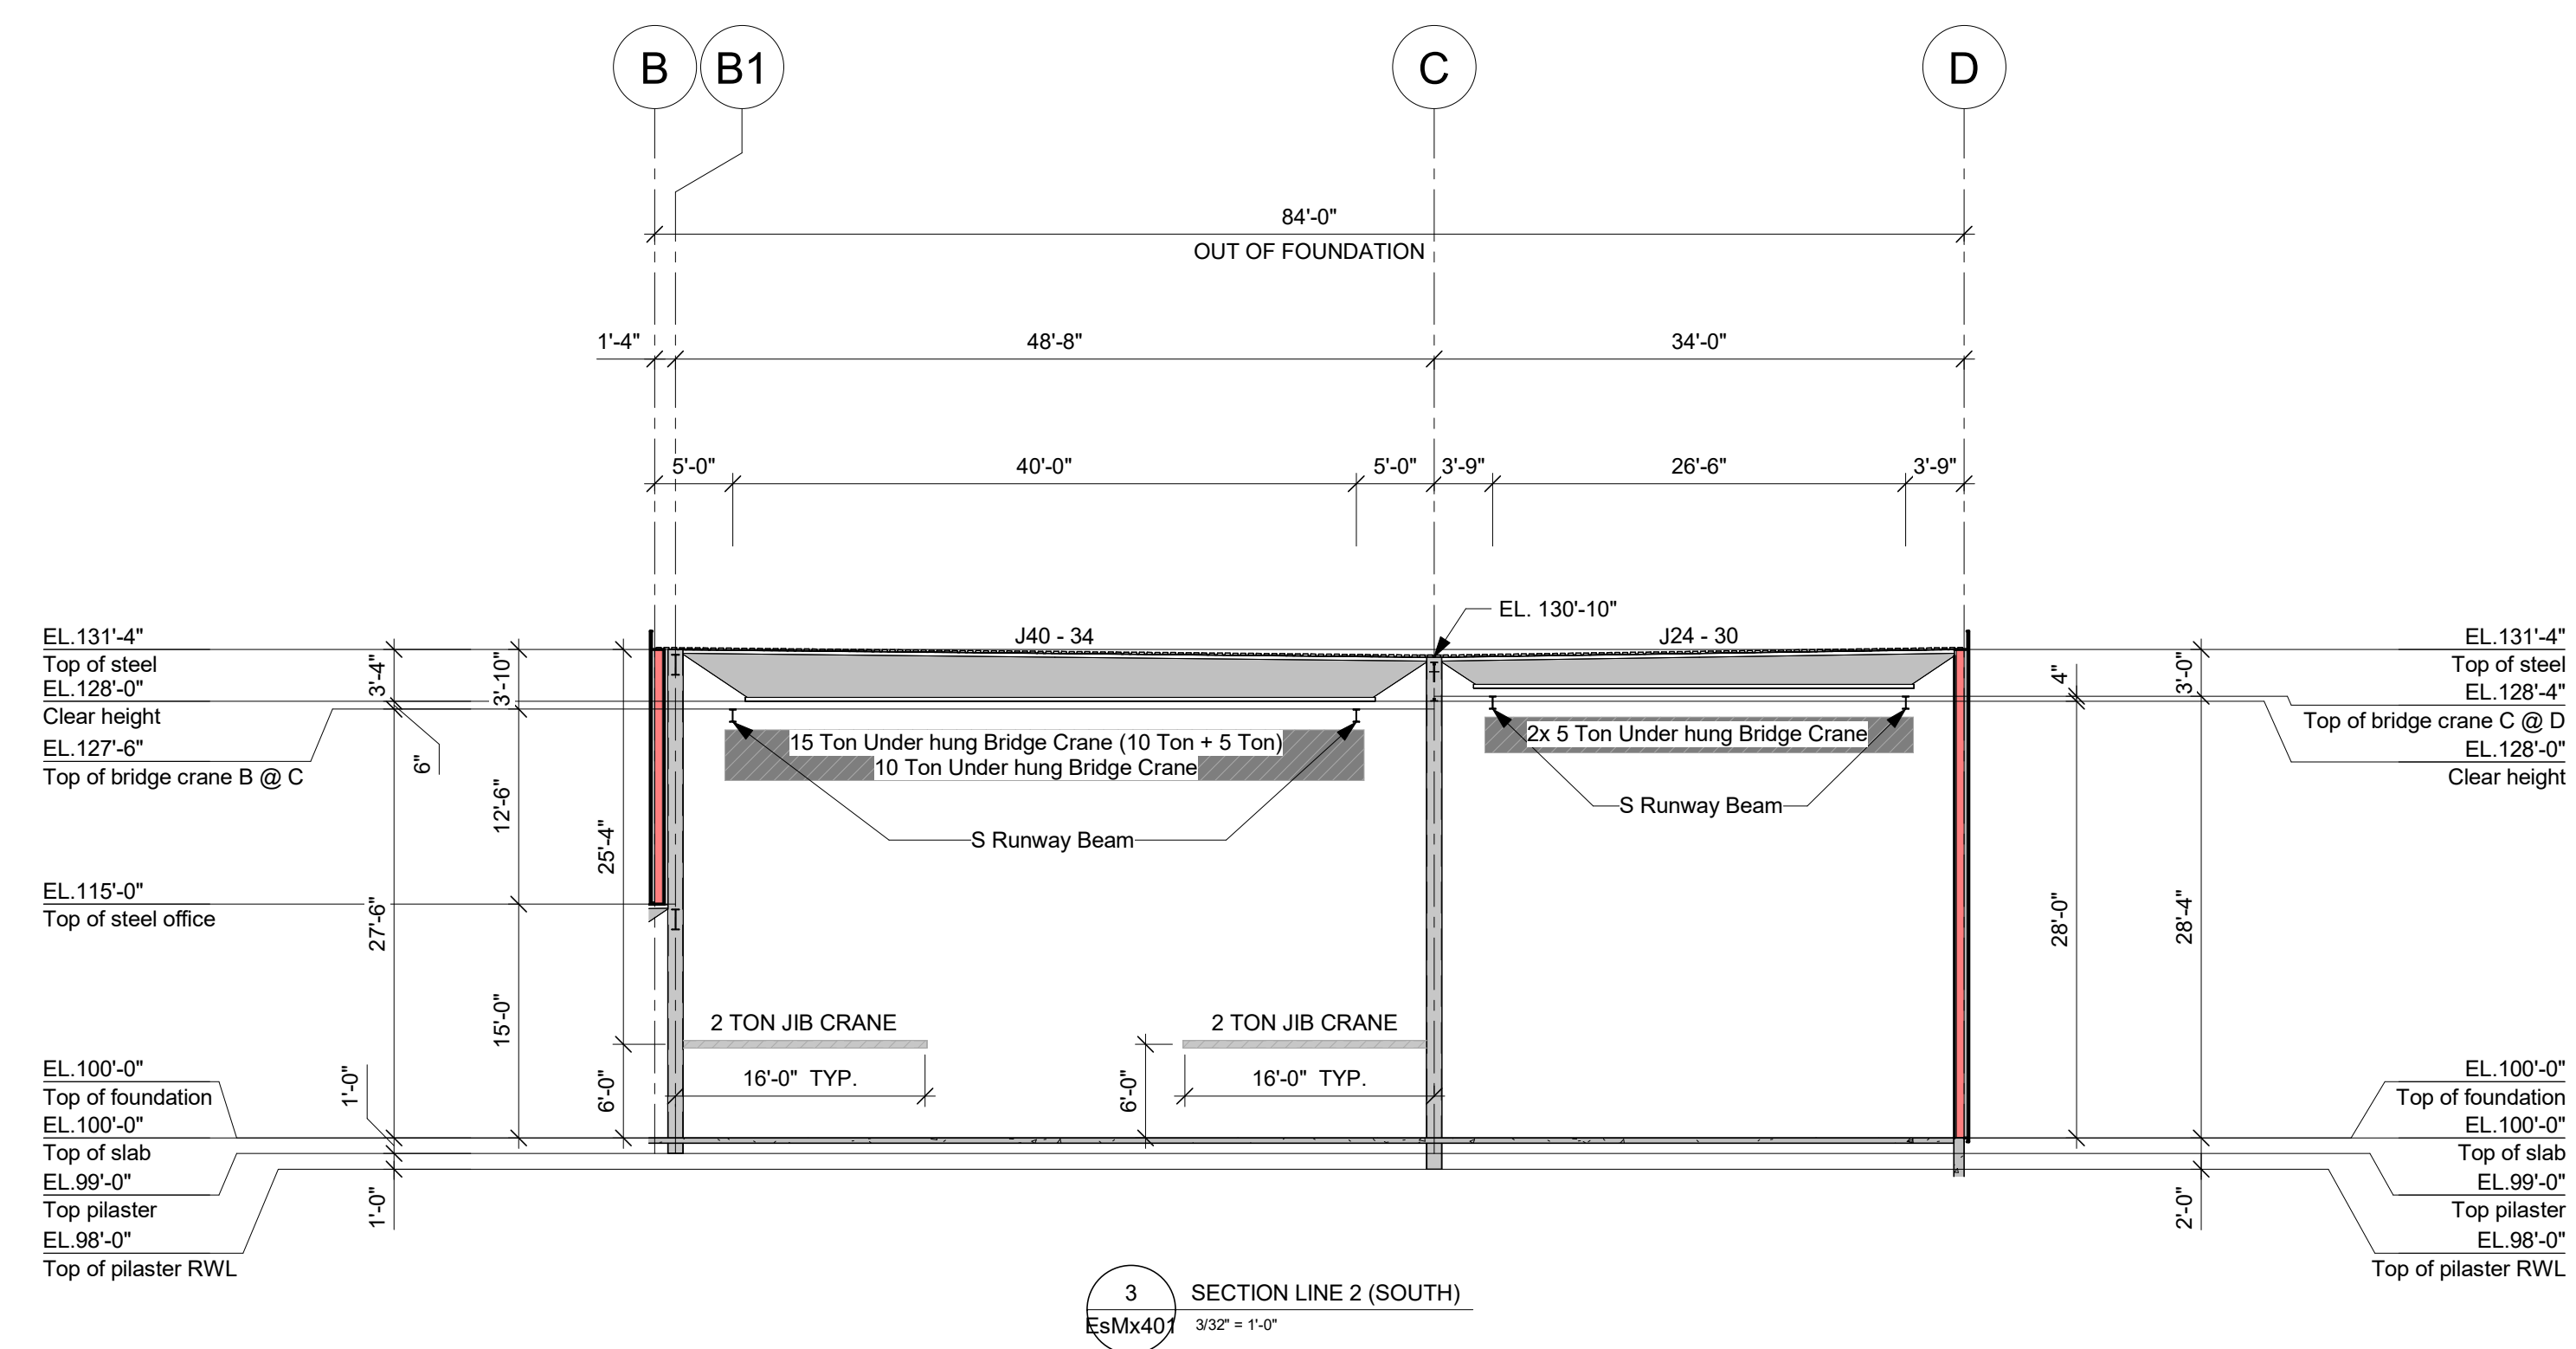


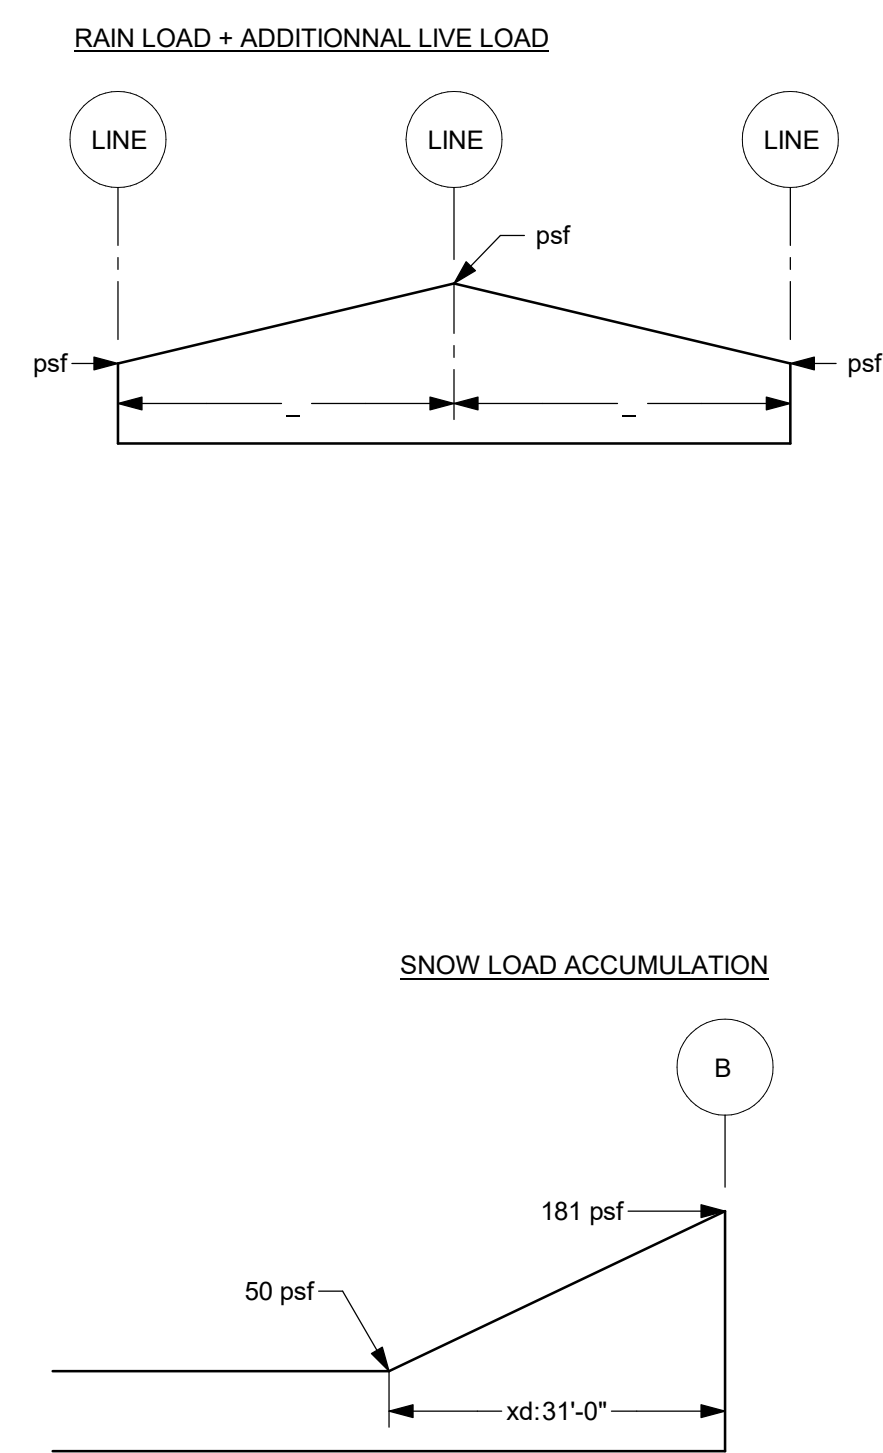


OFFICE ROOF PLAN
3/32" = 1'-0"

CRANE BEAM LOADS				
CAPACITY	CRANE WEIGHT	HOIST	MAX. WHEEL LOAD	WHEELS SPACING
5 Ton	2798 lb	900 lb	8.40 kip	6'-6 3/4"
5 Ton	2798 lb	900 lb	8.40 kip	6'-6 3/4"
10 Ton	9361 lb	1400 lb	17.70 kip	7'-6 1/2"
15 Ton (10 + 5)	9813 lb	2250 lb	18.30 kip	8'-2 3/8"

NOTE:

- The 10 ton and 5 ton hooks if the 15 ton cannot be used at the same time.
- No distance limitation between cranes.

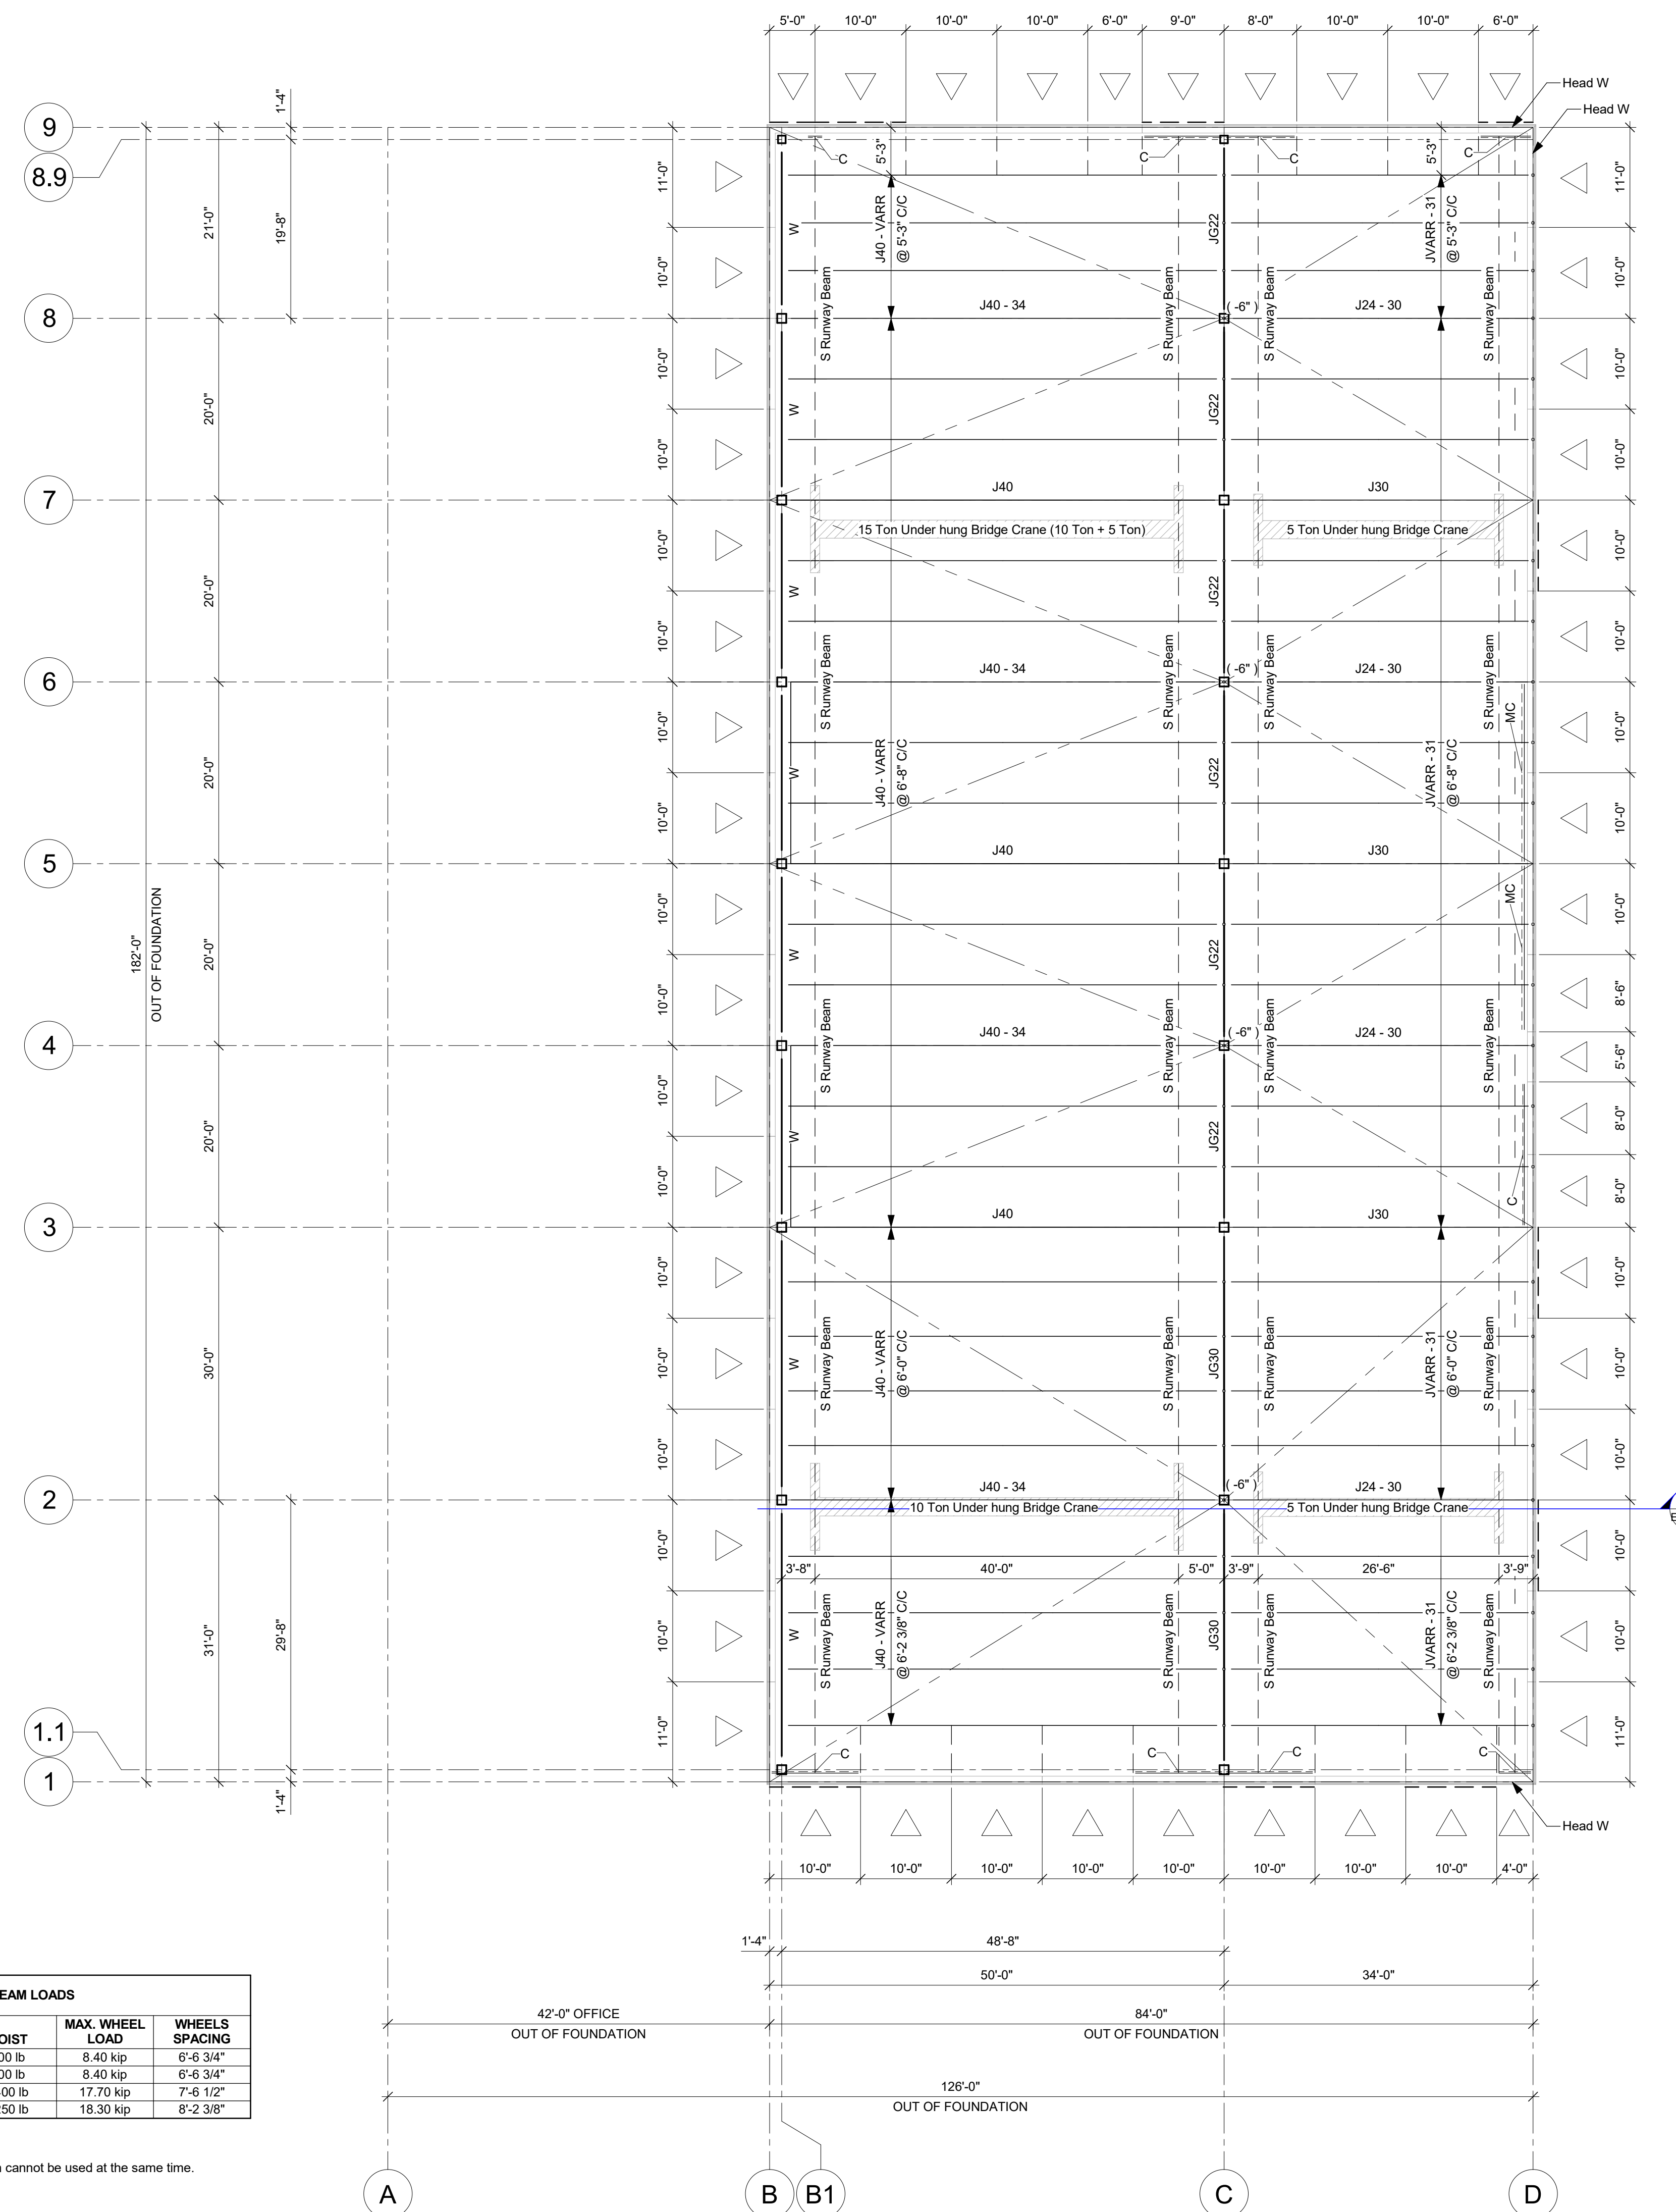

ROOF PLAN
3/32" = 1'-0"