


Quincaillerie standard du fournisseur:
- Chamères : Stanley FBB179 4.5" x 4"
- Barre panique : Vot Dupin 22 x 688 avec poignée extérieure 230L
- Cylindre permanent : Schlage 2001C 626
- Ferme-porte : LCN 1261 689
- Coupe-froid de tête et des montants : Unique 1650
- Coupe-froid du bas : Unique DS4
- Seuil : Voir la remarque dans la "Cédule de porte"


CÉDULE DES OUVERTURES			
Total	Type	Tag	Commentaires
1	2'-0" x 2'-0"	OUV	
Total général: 1			

CÉDULE DES PORTES													
Identifiant	Qté	Porte 18 ja.		Vitrage		Cadre d'acier 16 ja., avec bris thermique	(3) Pentures @ tige fixe	Poignée seulement	Barre panique sans poignée ext. 2350	Barre panique avec poignée ext. 230L	Quincaillerie		Remarques
		Installation	Isolation (R12)	Dimensions	Sens ouv.	Largeur	Hauteur				Verrou en surface (Porte inactive)	Seuil machiné	
P7	1			3'-0" x 7'-0"									


CÉDULE DES P.M. ET DES OU			
Total	Type	Tag	Commentaires
1	16'-0" x 14'-0"	PM	
1	18'-0" x 8'-0"	PM	
Total général: 2			

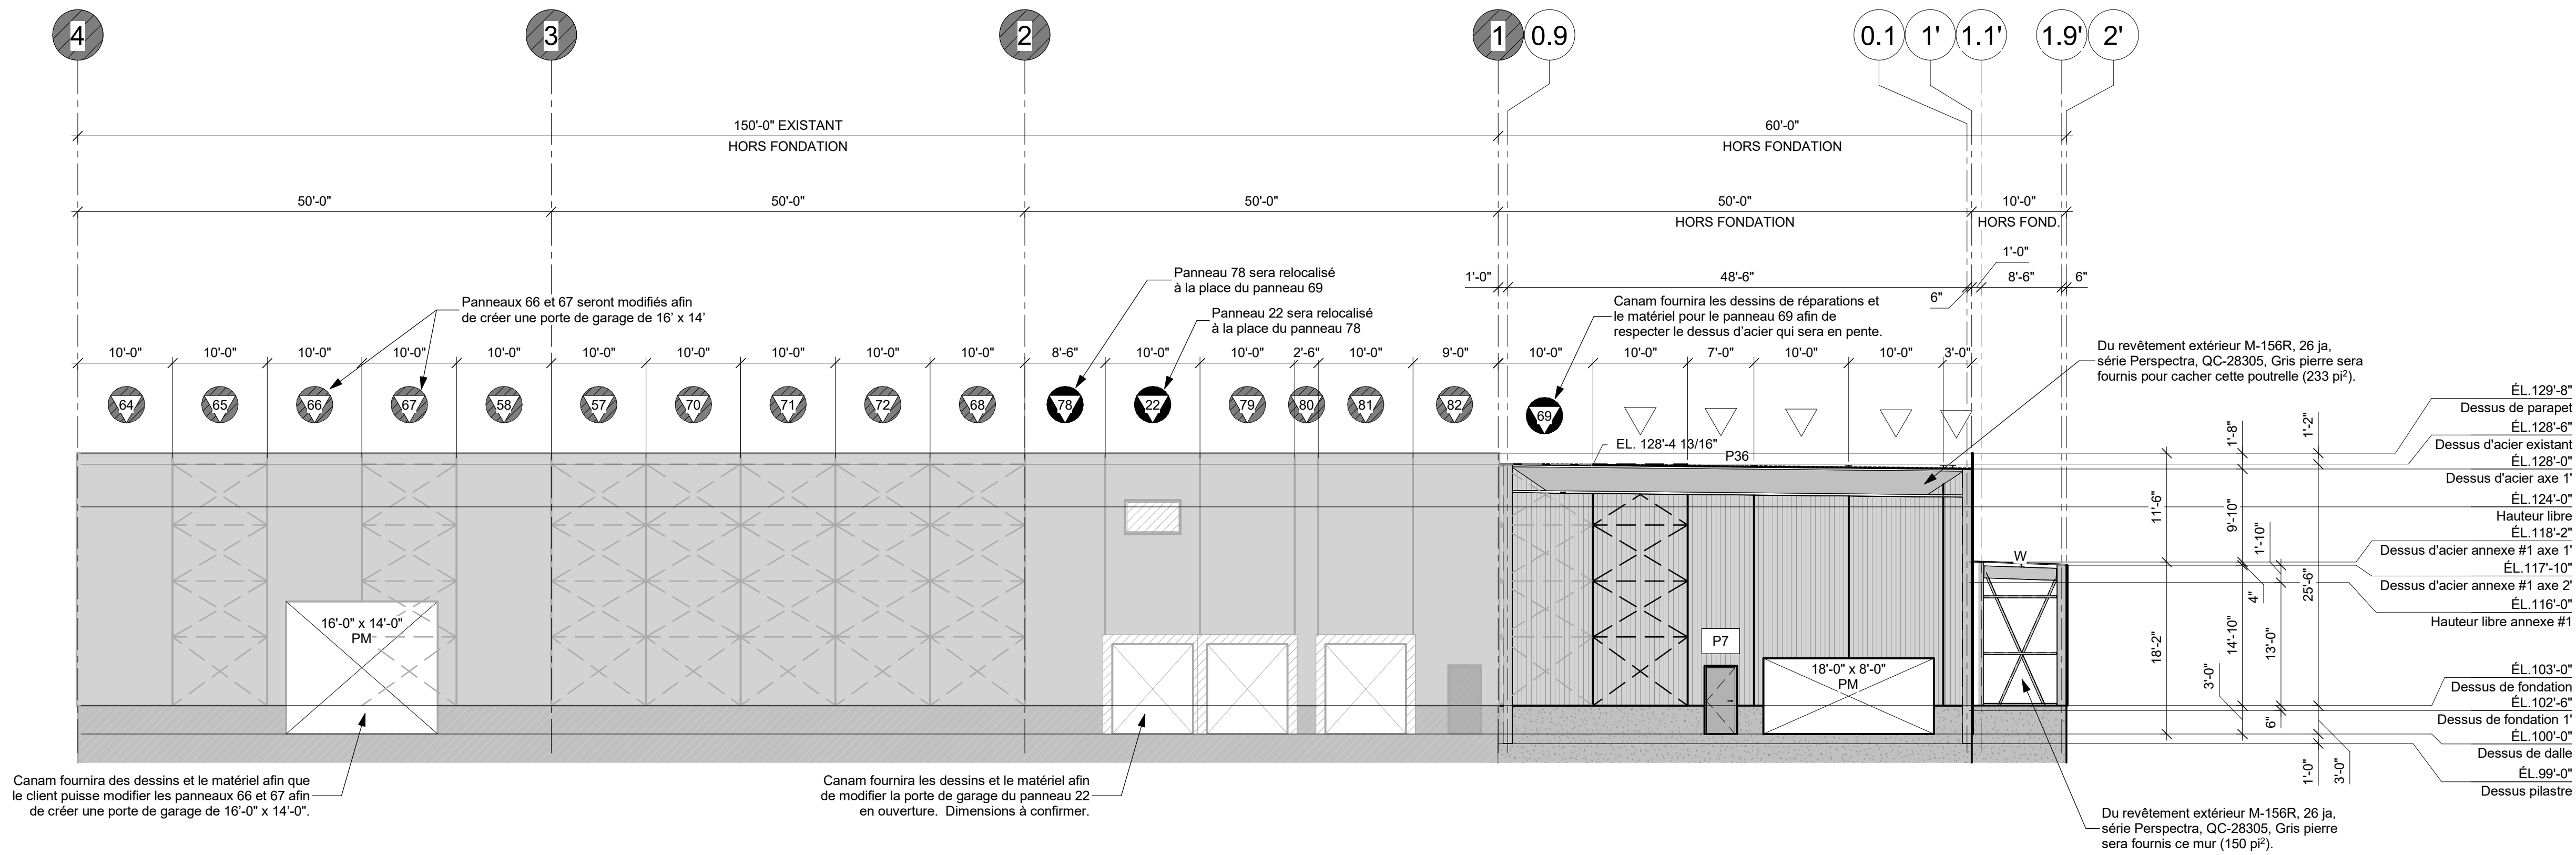

ÉLÉVATION AXE F, C & B7 (EST)
3/32" = 1'-0"

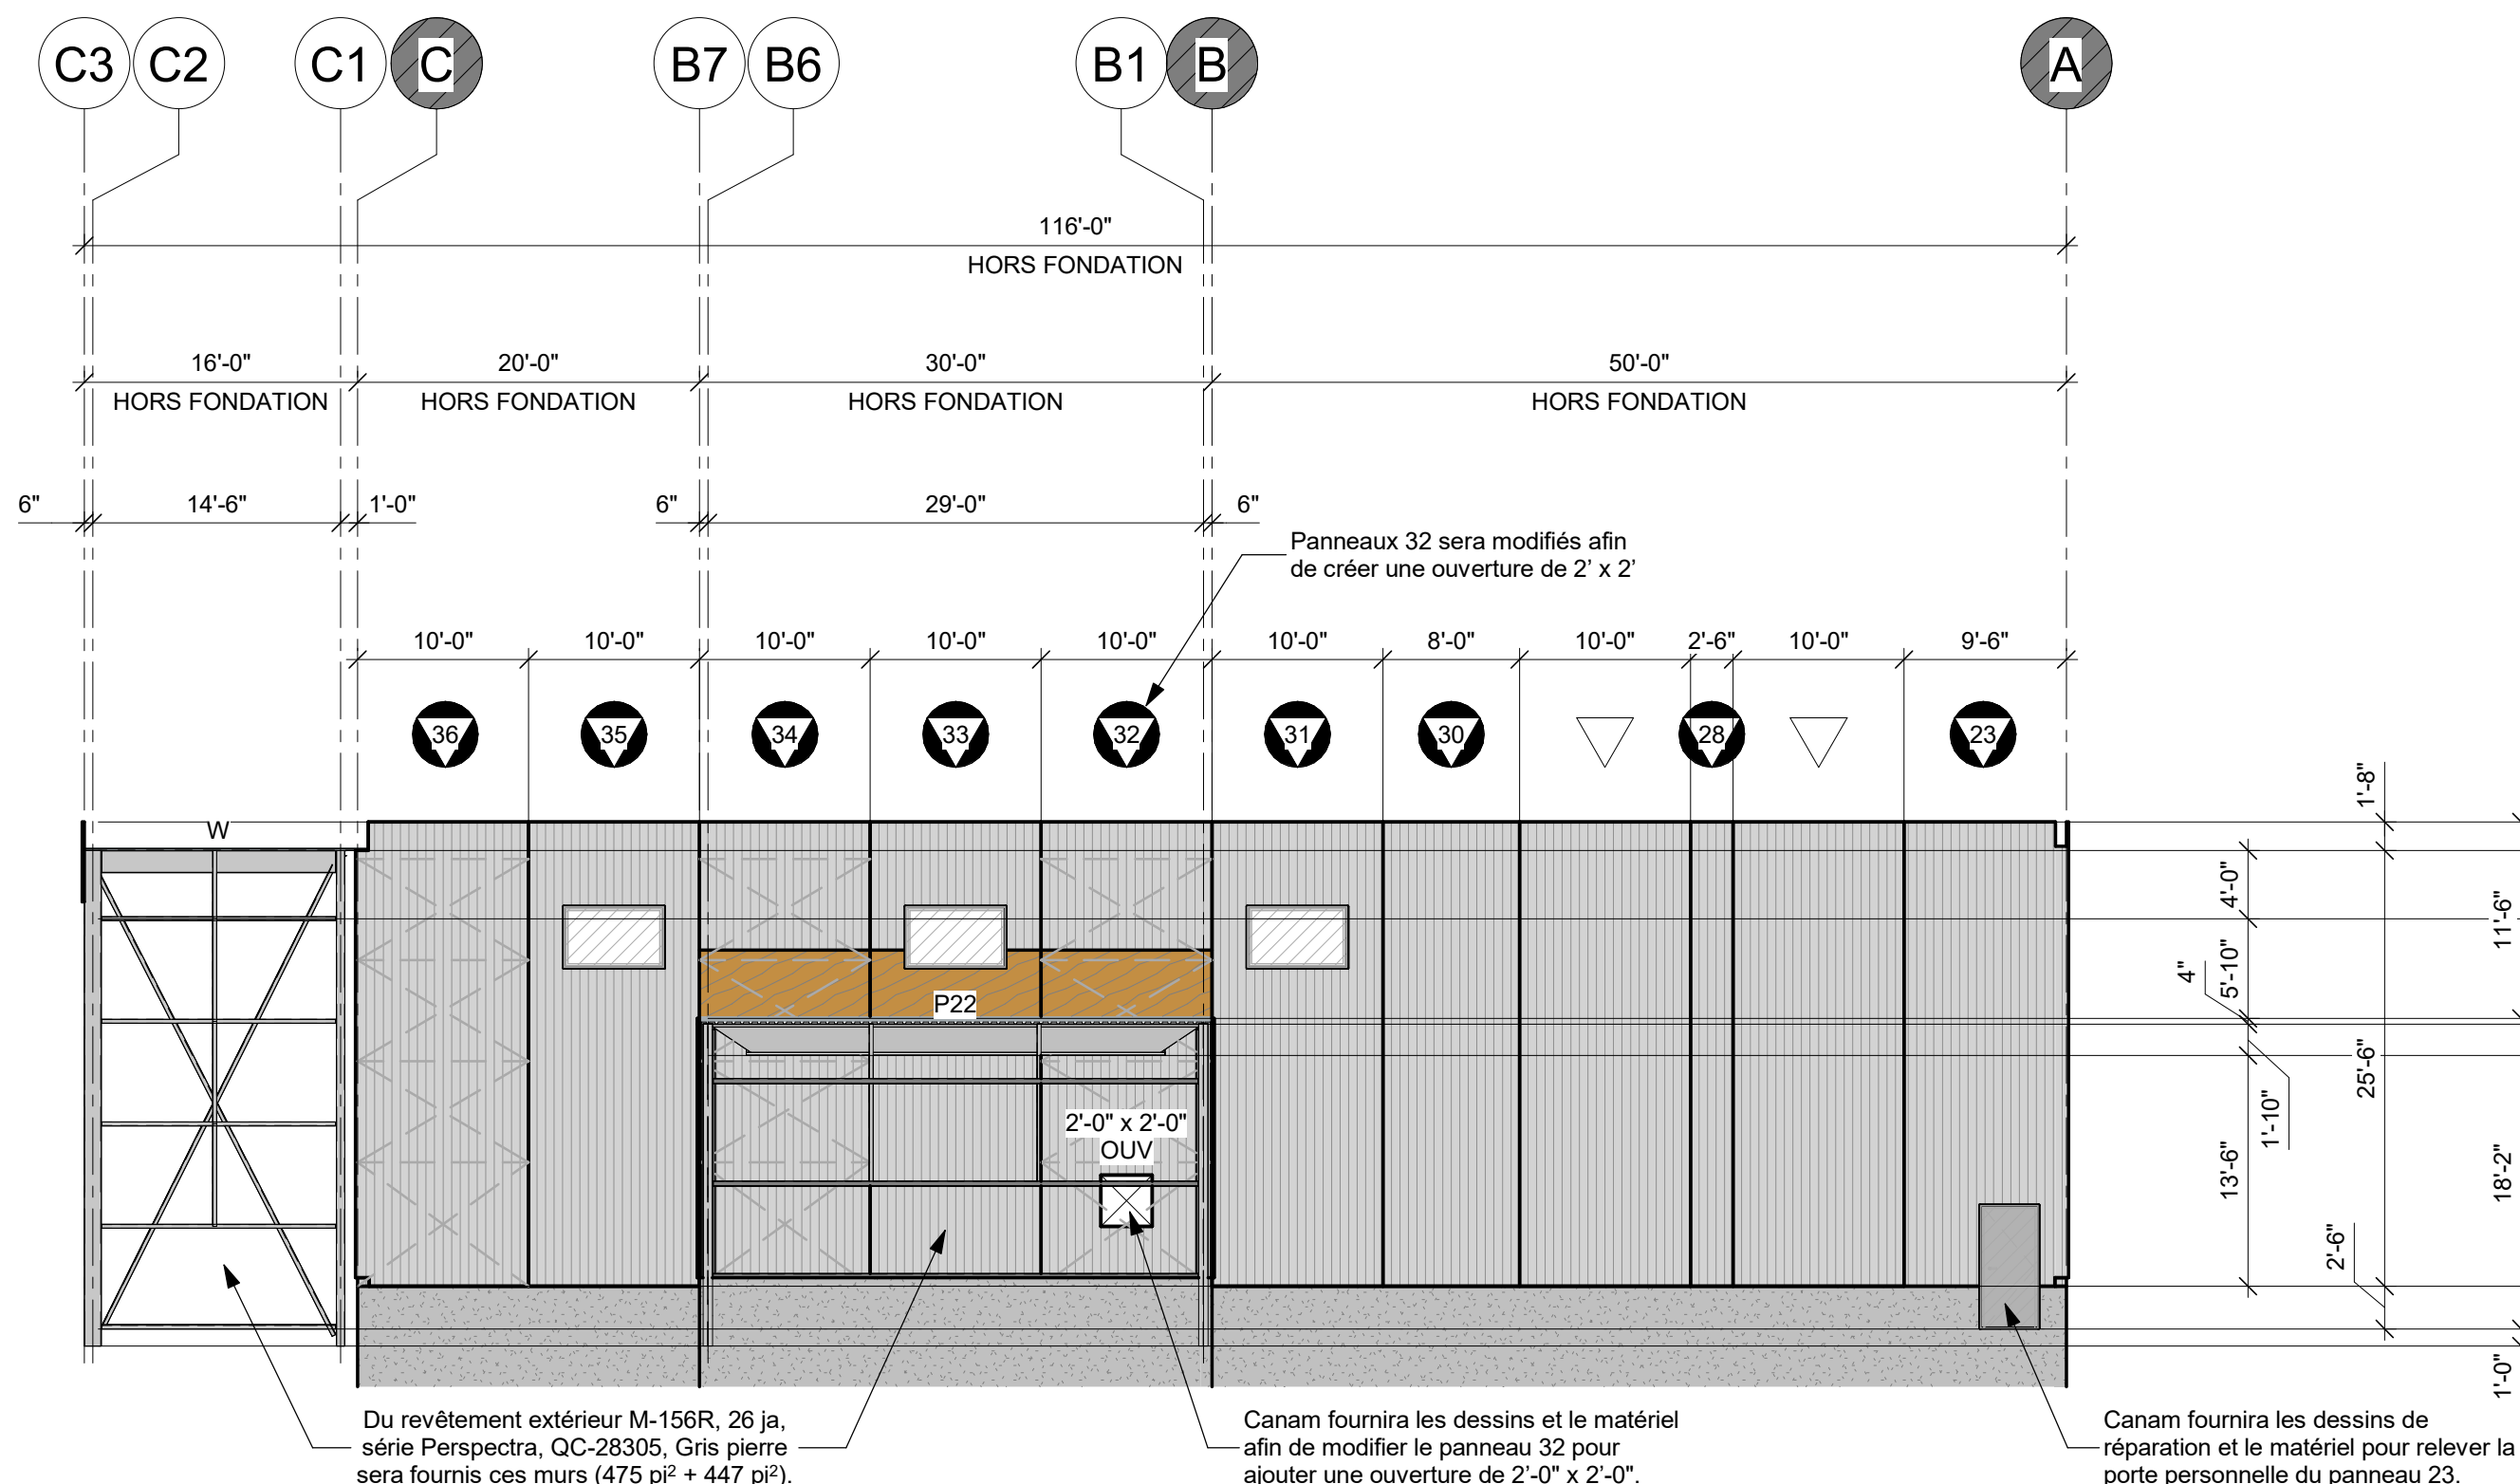

ÉLÉVATION AXE 2' & 1' (NORD)
3/32" = 1'-0"

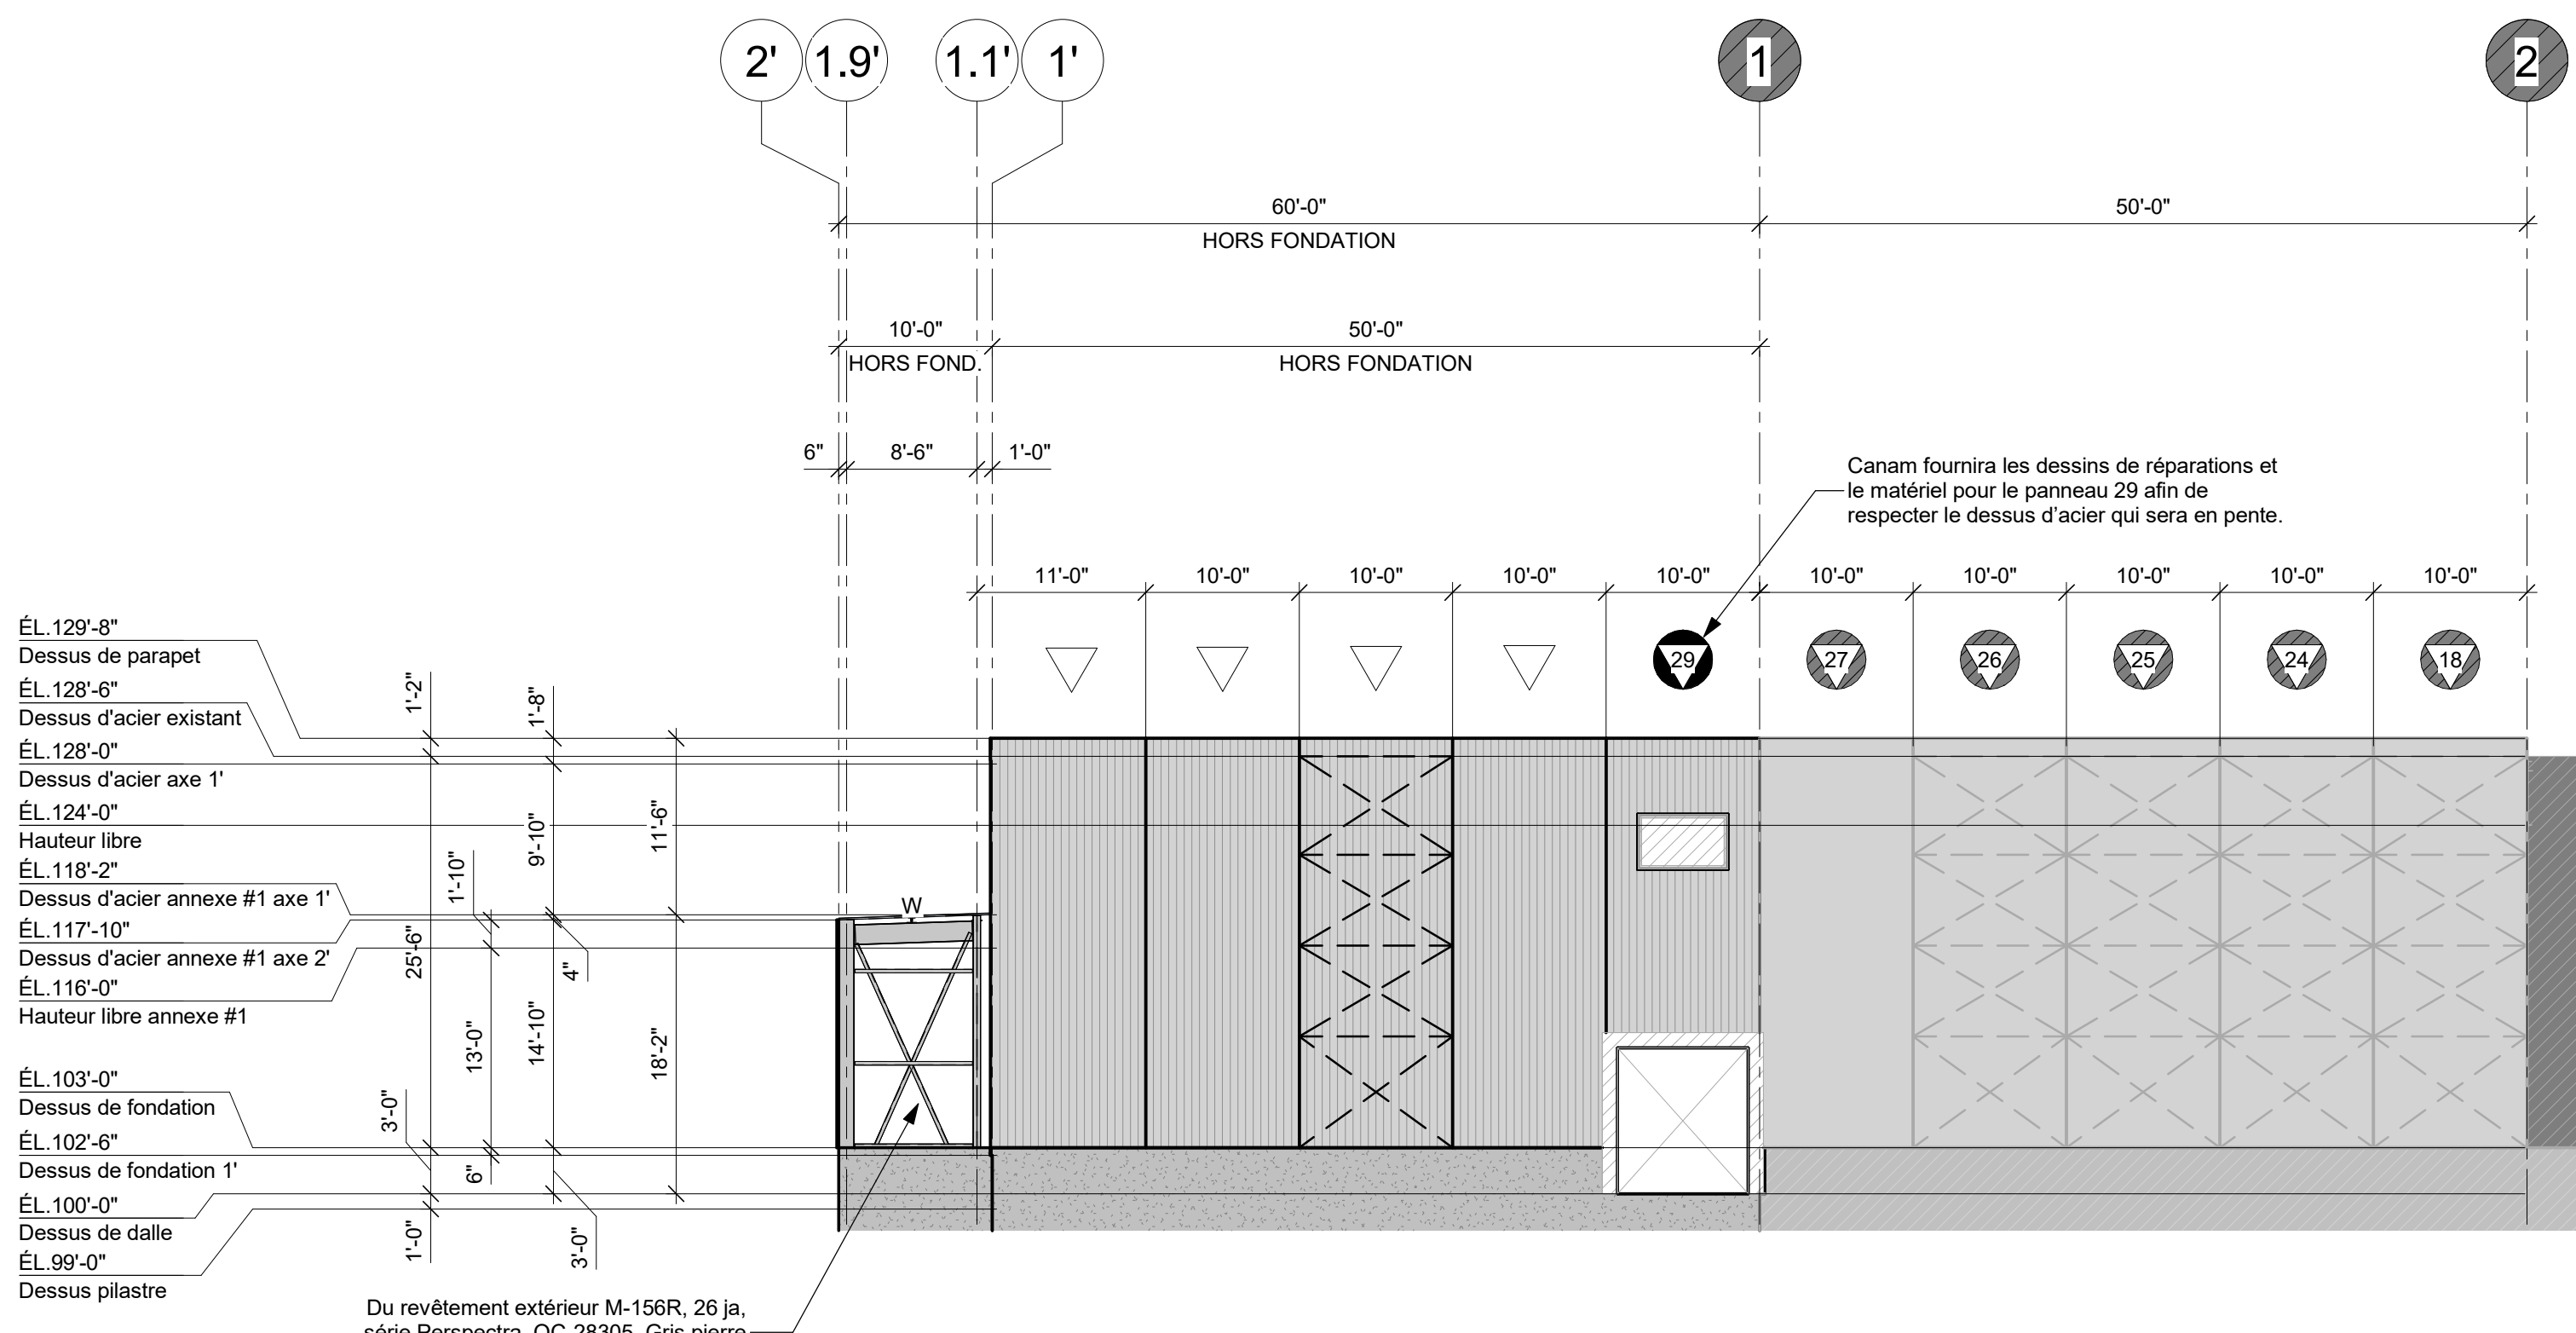

ÉLÉVATION AXE B & A (OUEST)
3/32" = 1'-0"

