
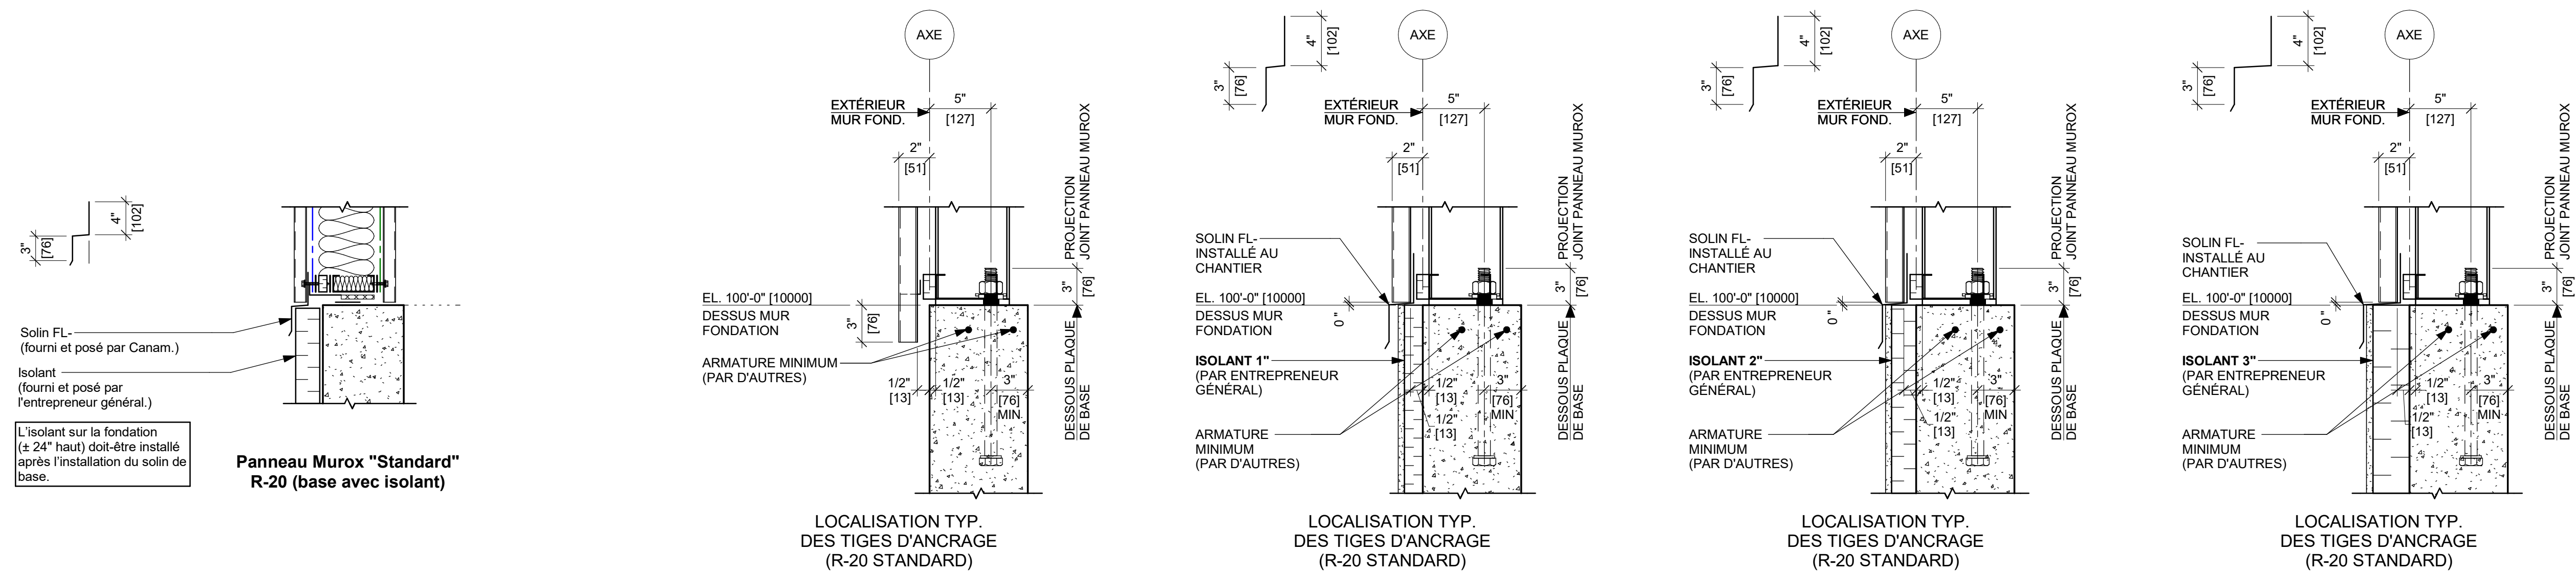
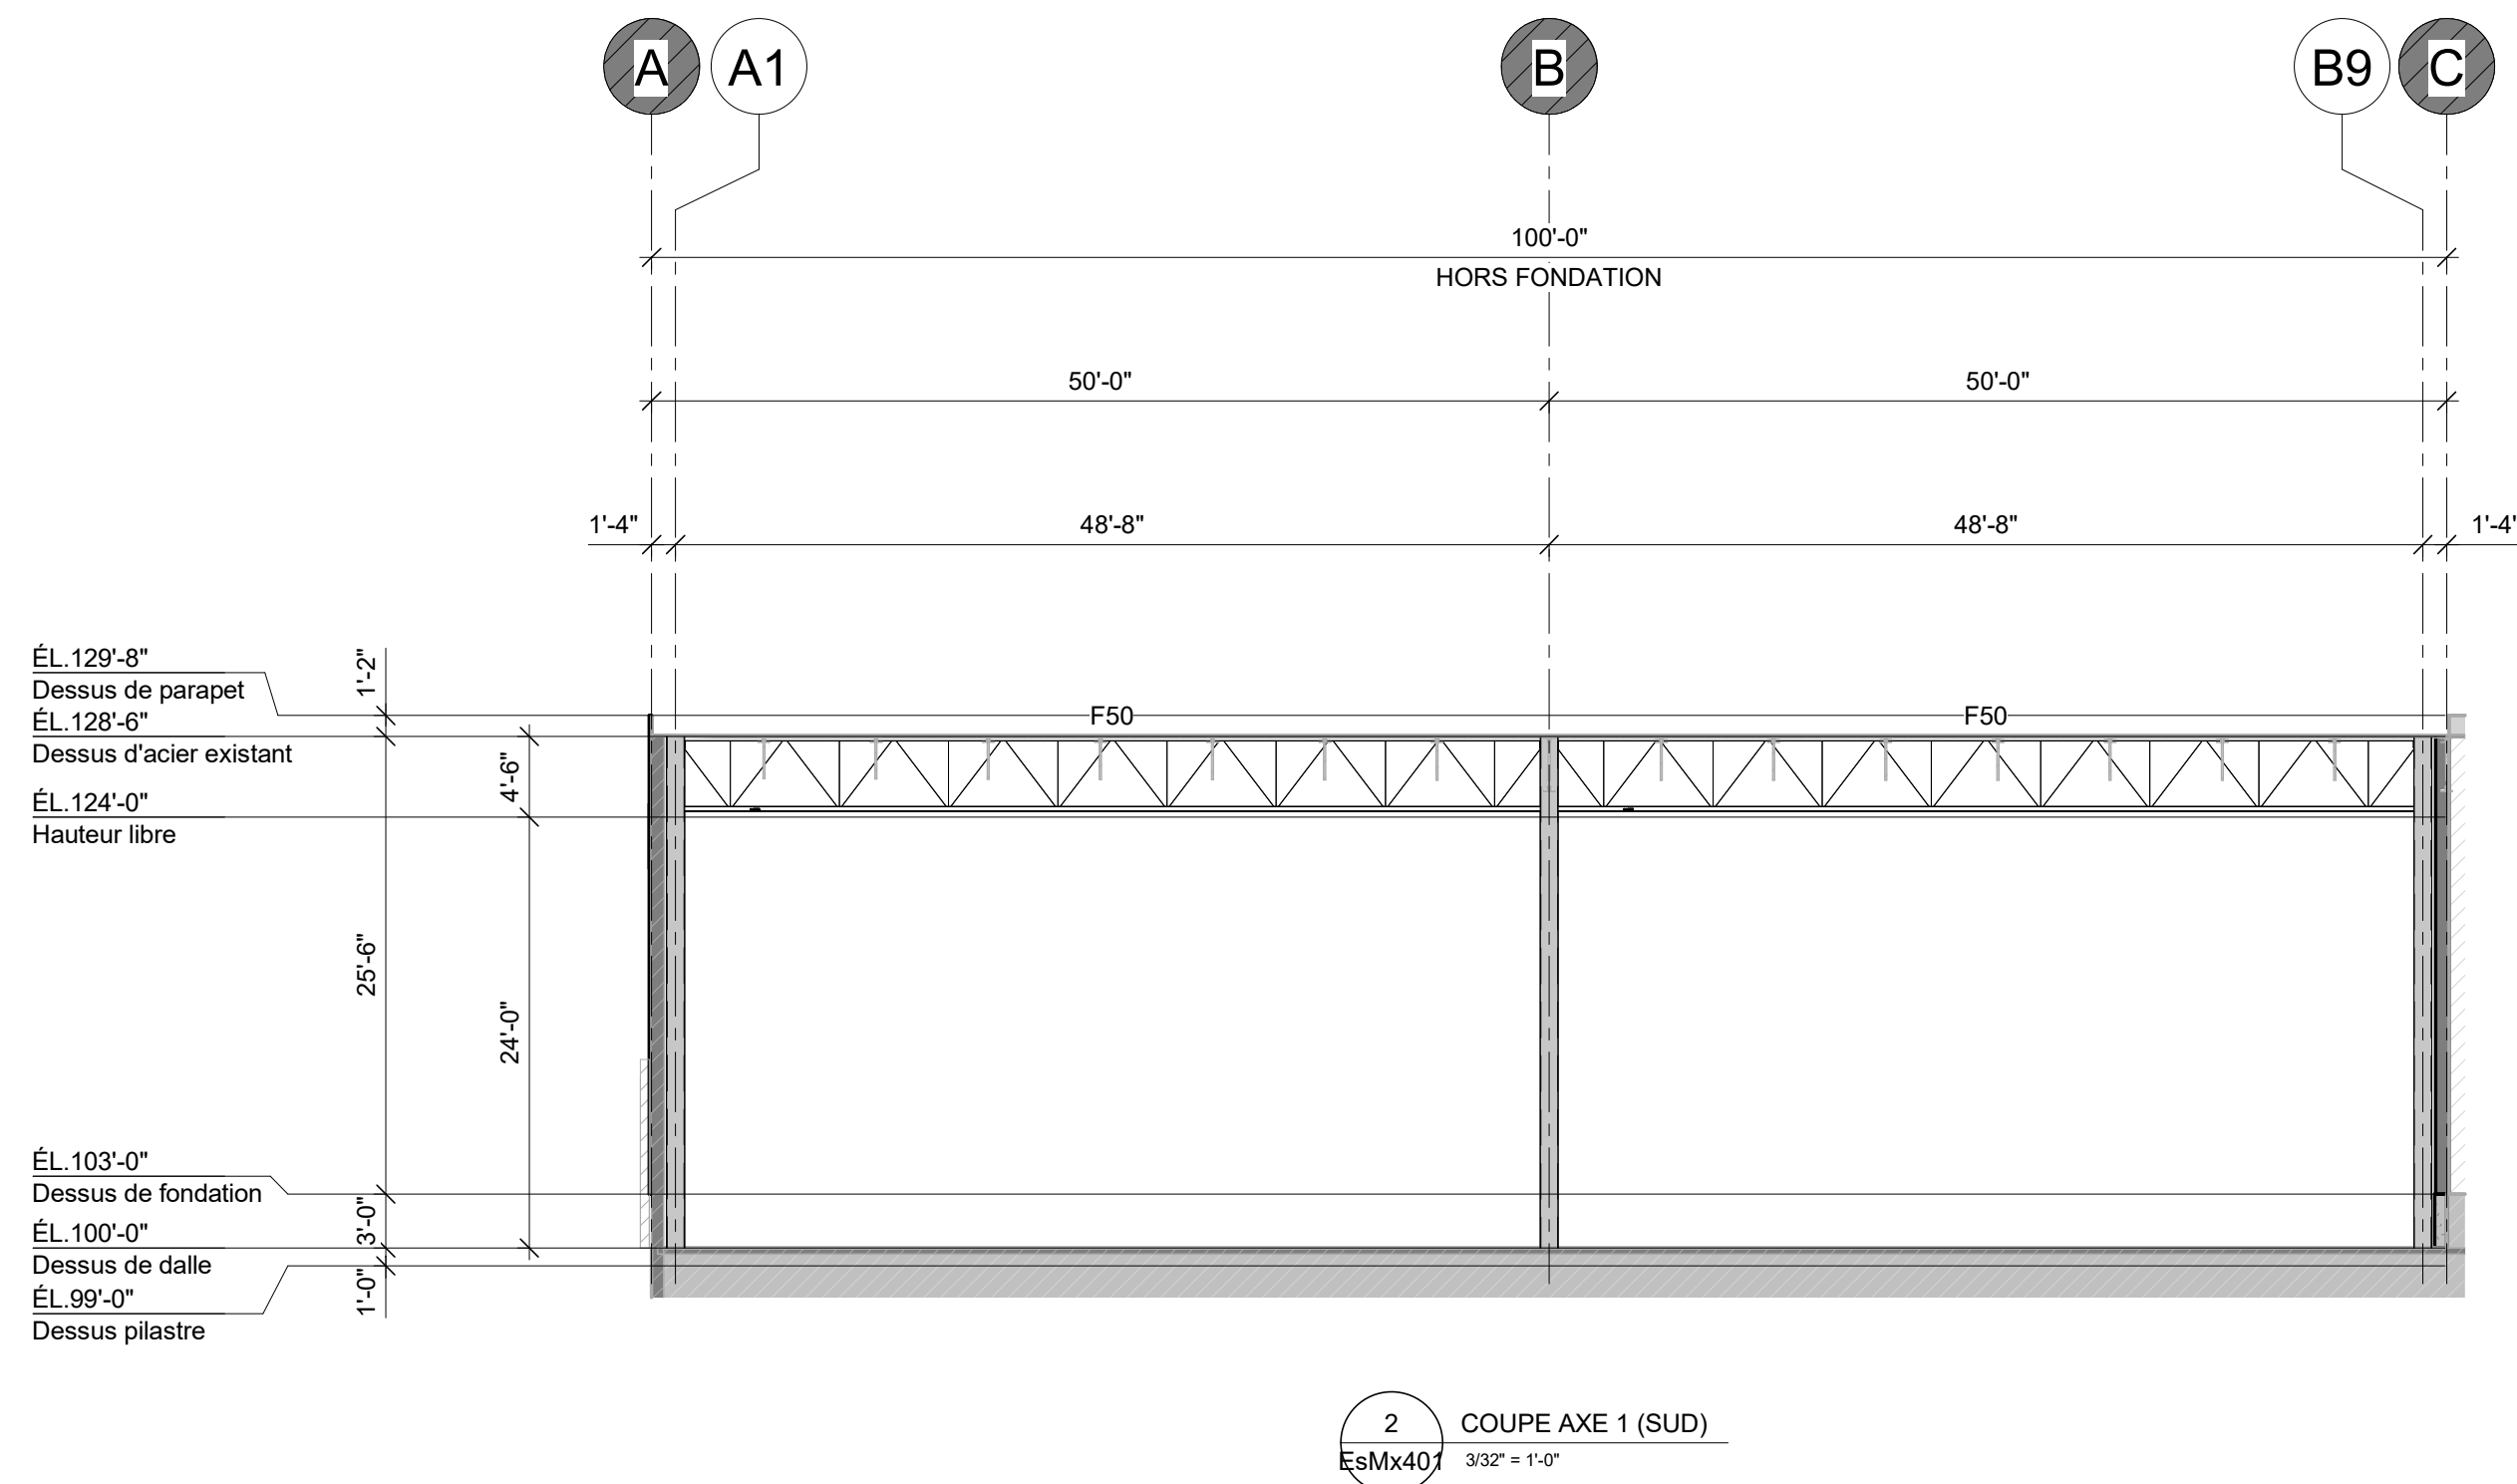


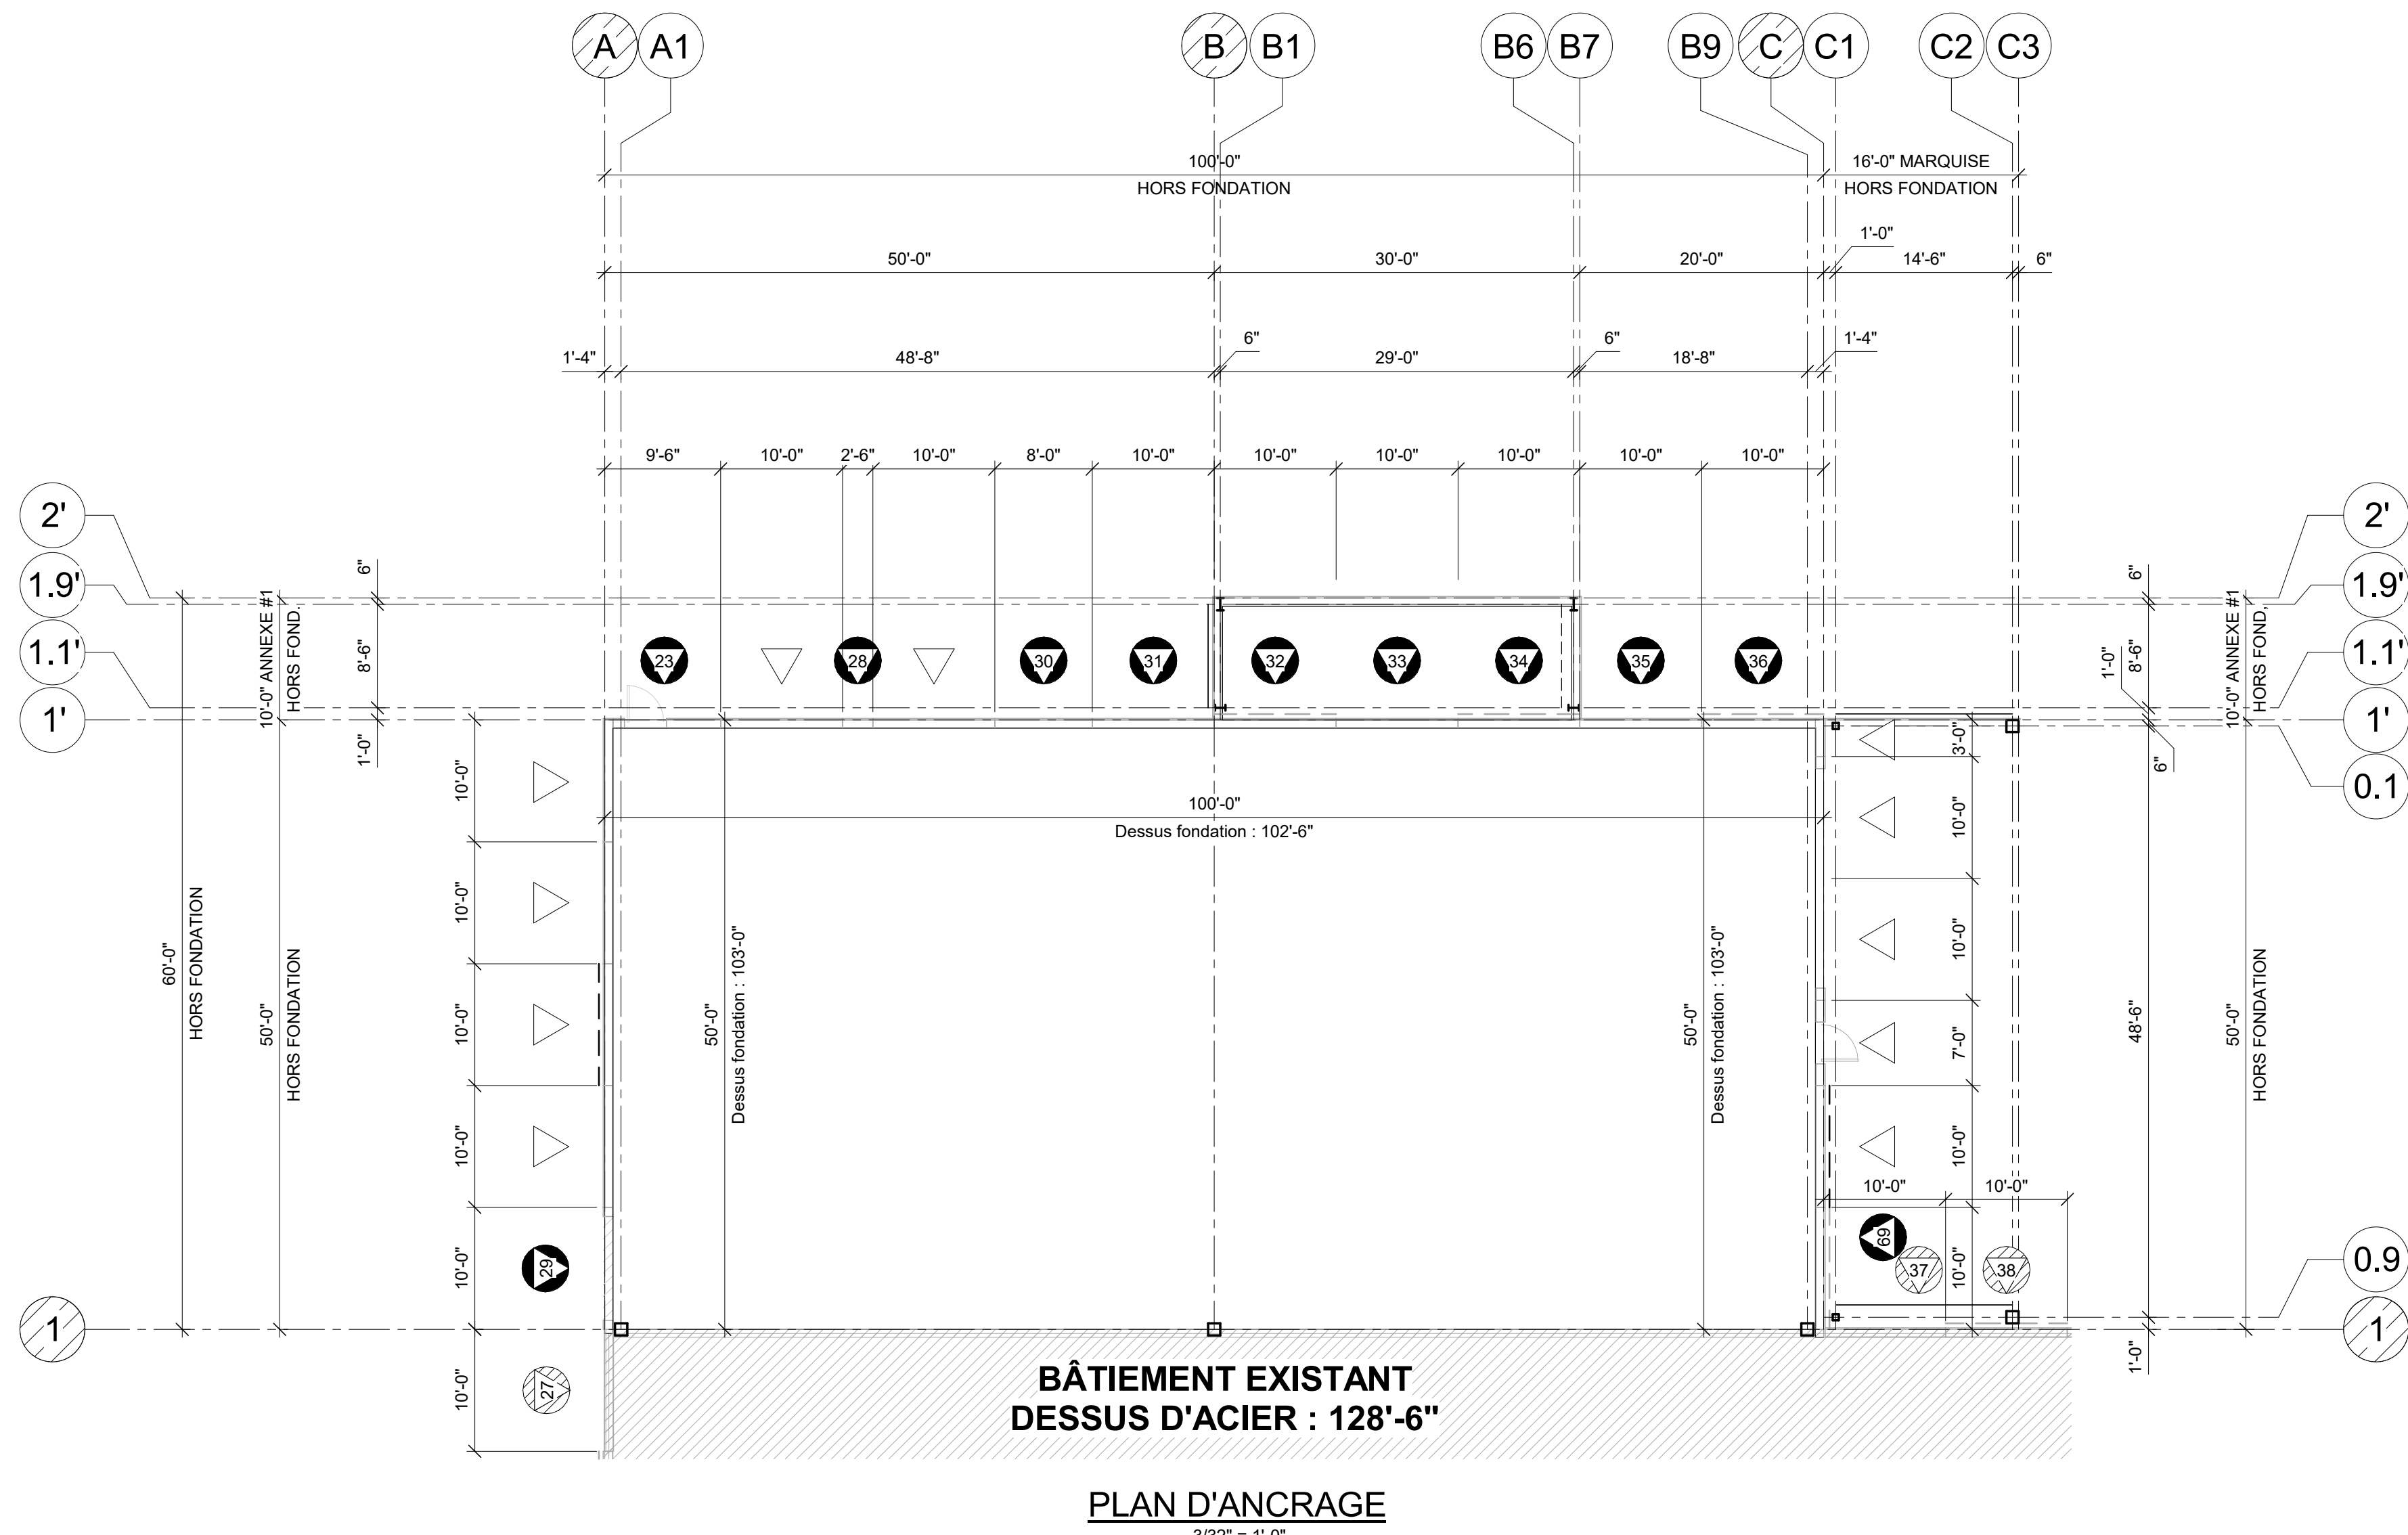

NOTE POUR LE CONTRACTEUR/ÉRECTEUR:

IL EST STRICTEMENT DÉFENDU DE MODIFIER, COPIER, REPRODUIRE OU DE DISTRIBUER CES DESSINS OU QUELQUES REPRÉSENTATIONS DE CES DESSINS, PAR TOUTES SOURCES DE MÉDIA INCLUANT ÉLECTRONIQUEMENT, SANS L'APPROBATION ÉCRITE DE GROUPE CANAM INC.

PRÉLIMINAIRE

NE DOIT PAS SERVIR À LA
CONSTRUCTION

REVISION	DATE	DESCRIPTION	DESS	VER
----------	------	-------------	------	-----

GERANT DE PROJET	-
-	-
-	-
-	-

DESSIN

DESSINÉ PAR	CONÇU PAR	INGÉNIEUR DU PROJET	ÉCHELLE
INITIALE			Comme indiqué

VÉRIFIÉ PAR	INGÉNIEURS CONSEILS / ARCHITECTES	DATE (mm/aaaa)
		28/01/2026

CLIENT: Construction Jean Pouliot Inc



11505, 1re Avenue, bureau 500, Saint-Georges Beauceville
Québec, Canada G5Y 7X3
Téléphone : (418) 228-8031
Sans frais : (877) 499-8049
www.canam.com

SCAUX PROFESSIONNELS

PROJET

Agrandissement Matra Beauceville
Beauceville, Québec

TITRE
CROQUIS PRÉLIMINAIRE - PLAN
D'ANCRAGE ET DETAILS

NUMÉRO CONTRAT	NUMÉRO DESSIN	DIVISION	REVISION
P2026-006	EsMx101		