


WINDOW SCHEDULE					
Identity	Qty.	Installation	Description	Sizes (Ext. of frame) (width & height)	Frame color
W1	18		Fixed aluminium window with thermal break and sealed glass + Low-E argon clear	8'-6" x 5'-0"	Aluminum Frame (no color)
Remarks					

OPENING SCHEDULE			
Total	Type	Tag	Remarks

DOOR SCHEDULE																	
Identity	Qty.	Installation	Door 18 ga.			Glass		Steel frame 16 ga with thermal break	(3) Hinges non-rising removable pin	Door lock & latch set	Panic bar without outside trim 22EO	Panic bar with outside trim 230L	Hardware				
			Insulation (R12)	Dimensions	Swing side	Width	Height						Surface bolt Inactive door	Threshold	Astragal for inactive door	Door closer	Door chain stop
D1	5			36" x 84"		1'-10"	2'-6"										
D2	3			12x12"													
D3	3			10x12"													
D4	1			20x12"													
D5	1			72" x 84"		1'-10"	2'-6"										
D6	1			12x10"													
Remarks																	

O/H & OPENING SCHEDULE			
Total	Type	Tag	Remarks
7	8'-6" x 9'-6"	OPN	
1	12'-0" x 9'-6"	OPN	
Total general: 8			

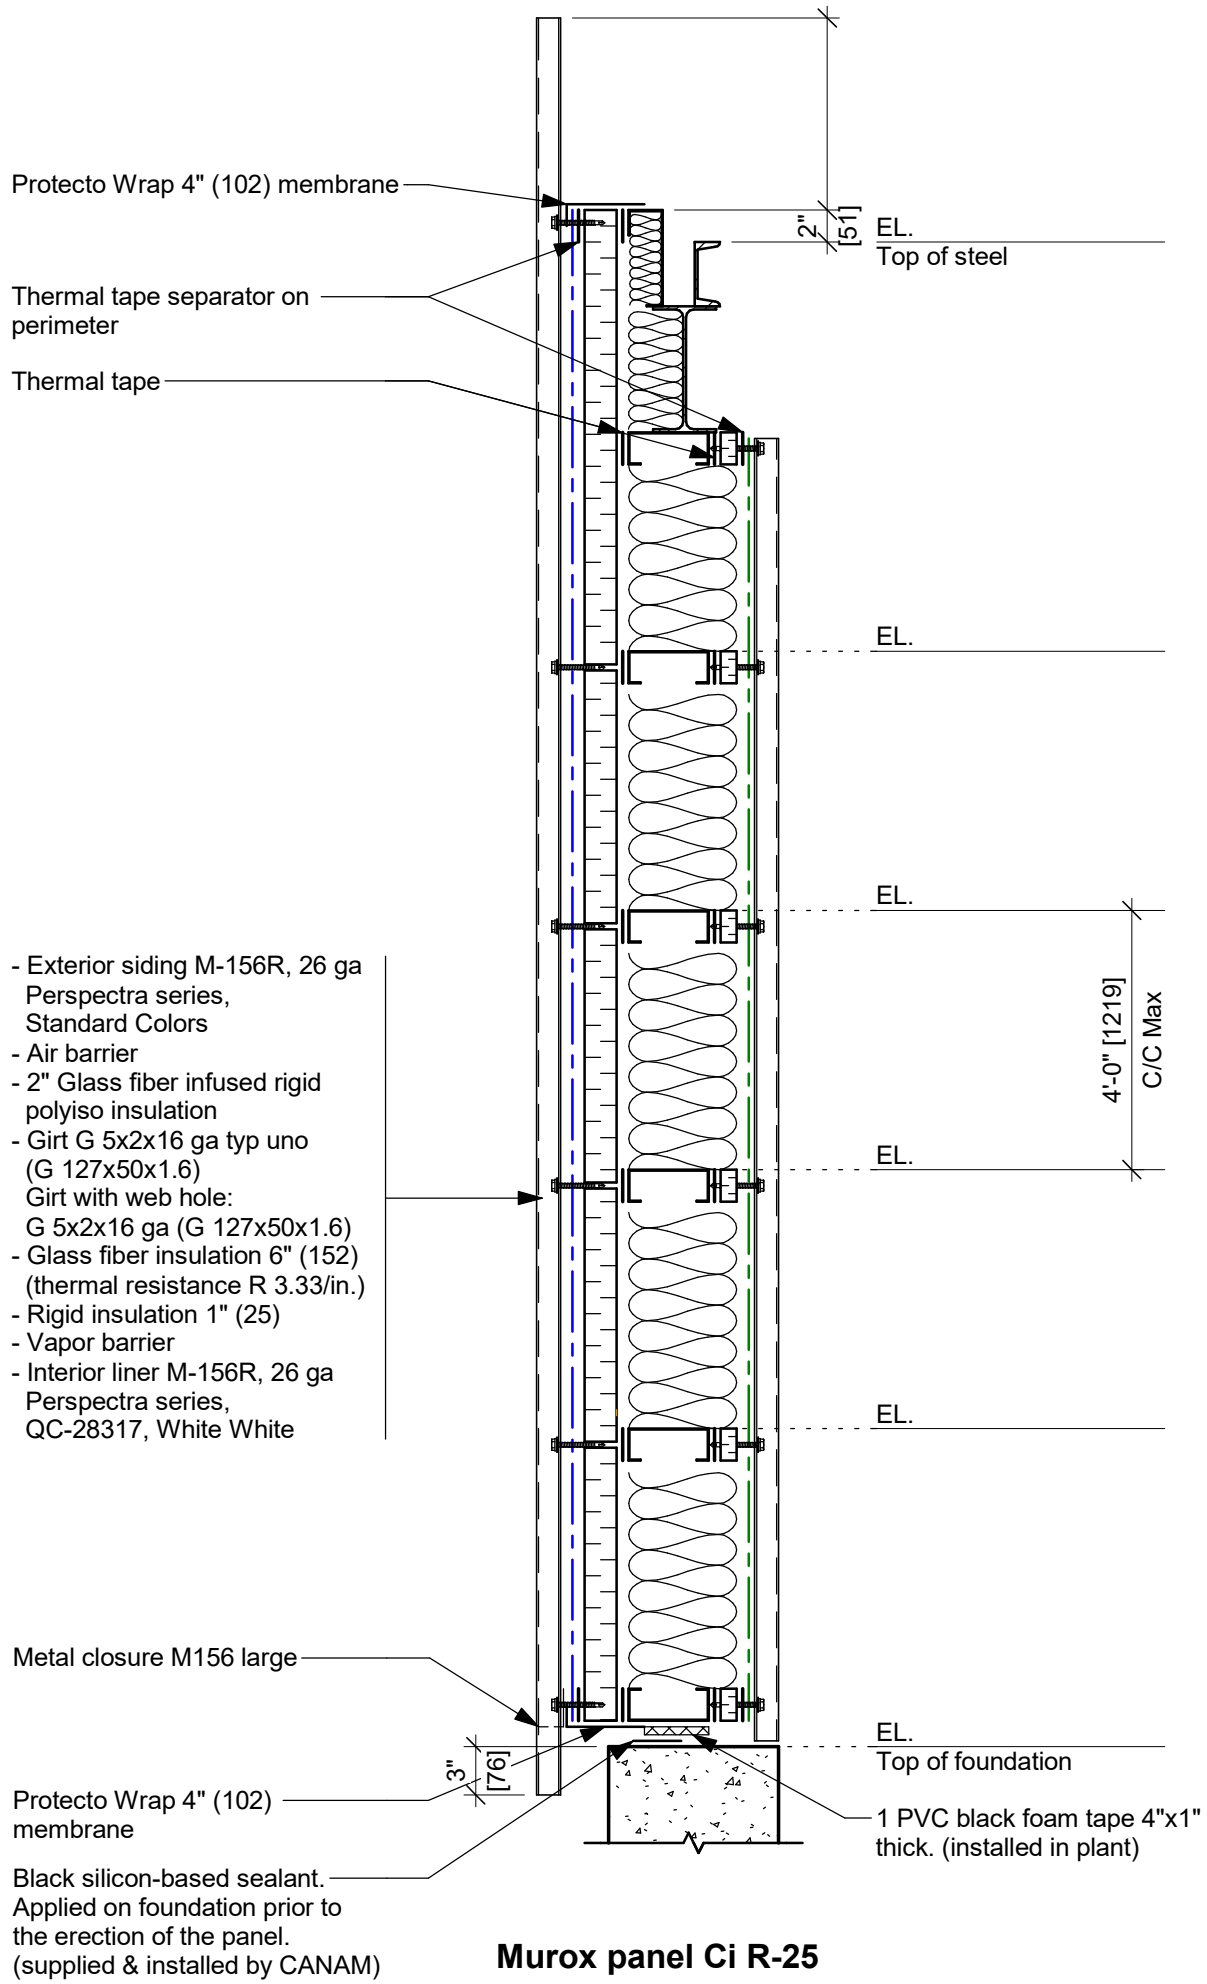

Supplier's standard hardware:

- Hinges : Stanley F8B179 4.5" x 4"
- Exit device : Von Duprin 22 x 689 with outside trim 230L
- Permanent cylinder : Schlage 20001C 626
- Door closure : LCN 1261 689
- Head and jamb seal : Unique 1650
- Bottom seal : Unique DS4
- Threshold : See the remarks in "Door schedule"