




MEZZANINE
CLEAR HEIGHT UNDER MEZZ. : 10'-0"
TOP OF STEEL MEZZ. : 11'-8"
CLEAR HEIGHT ABOVE MEZZ. : 10'-0"

MEZZANINE
D.L. : 70 psf
L.L. : 100 psf
Δ L/360

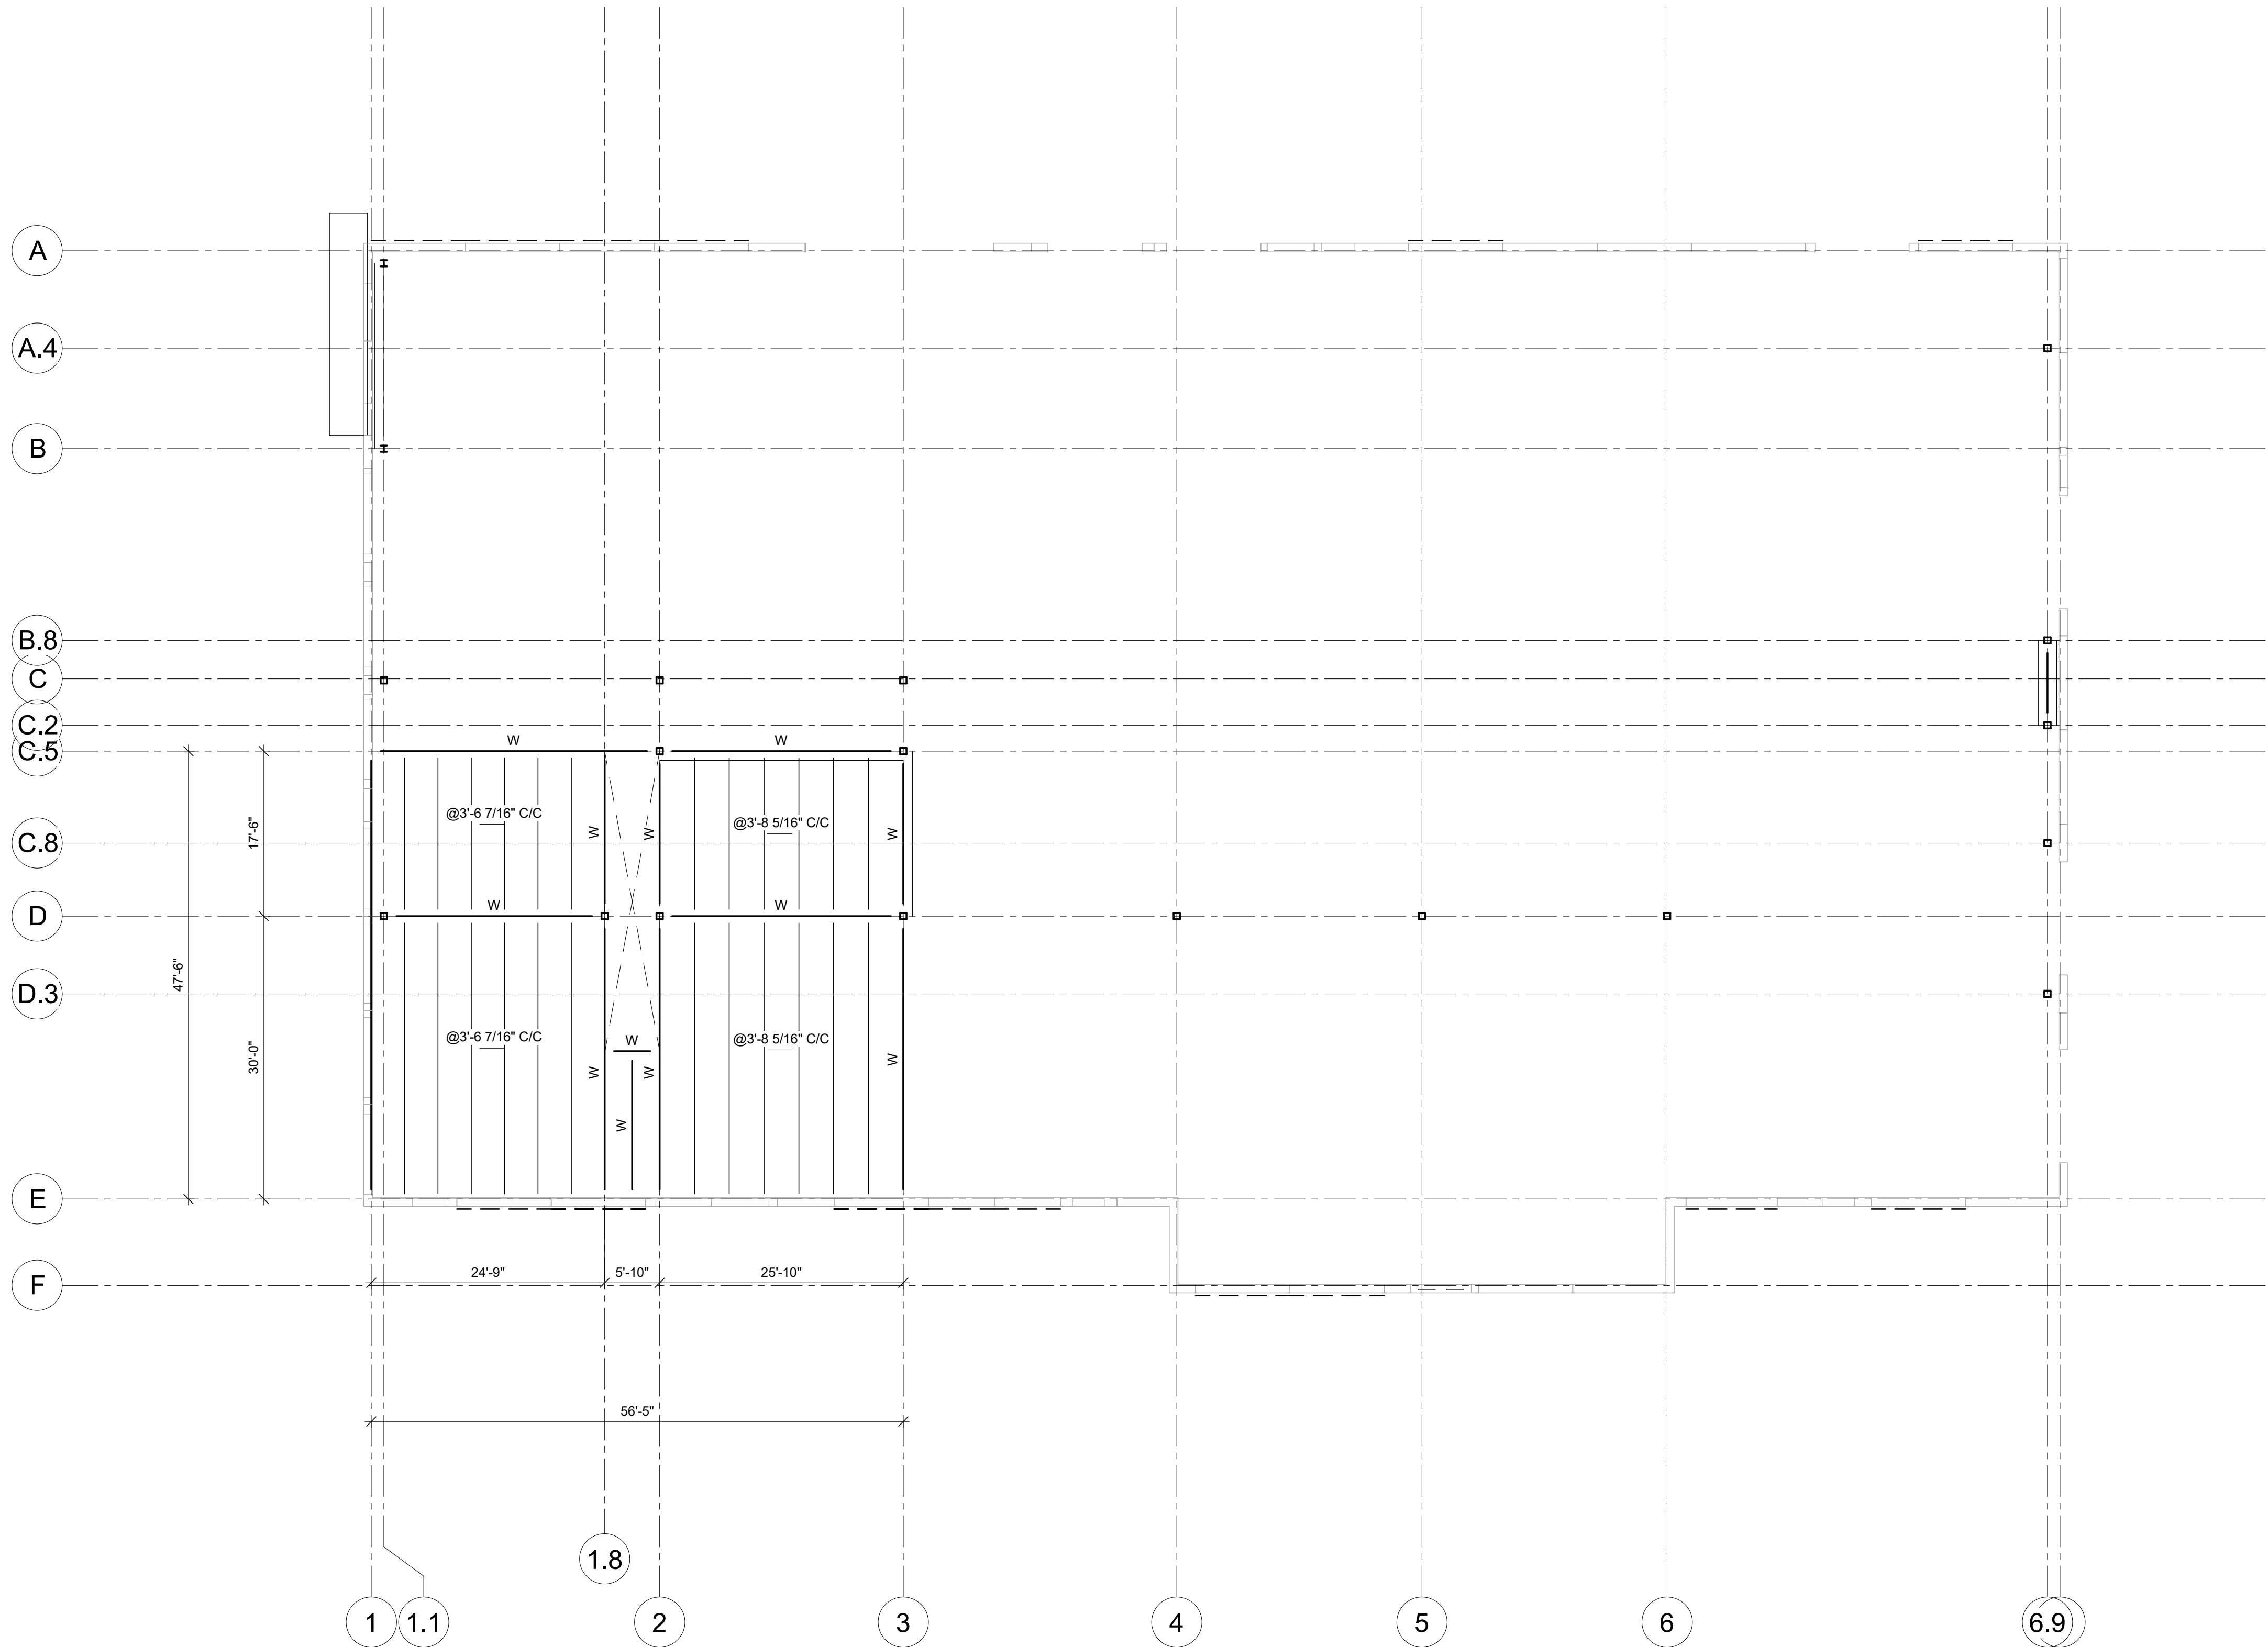

MEZZANINE PLAN
3/32" = 1'-0"

PRELIMINARY

NOT TO BE USED FOR CONSTRUCTION

REVISION	DATE	DESCRIPTION	DESIGNED	VER.
PROJECT MANAGER				
-				
-				
-				
-				
DRAFTING				
-				
DRAWN	INITIALE	DESIGNED	PROJECT ENGINEER	SCALE:
			PROJECT ENG.	3/32" = 1'-0"
CHECKED		CONSULTING ENGINEERS - ARCHITECTS	ENGINEER	DATE (YYYYMMDD)
			ARCHITECT	YYYYMMDD

CUSTOMER:

**CANAM**
11505, 1re Avenue, bureau 500, Saint-Georges Beauce
Châteauguay, Québec, G5Y 7X5
Phone : (418) 228-8031
Toll free : (877) 499-6049
www.canam.com

PROFESSIONAL SEAL

PROJECT

DRAWING TITLE
PRELIMINARY SKETCH - MEZZANINE PLAN

CONTRACT NUMBER	DRAWING NUMBER	DIVISION	REVISION
PJ NO.	EsMx201		

Initials